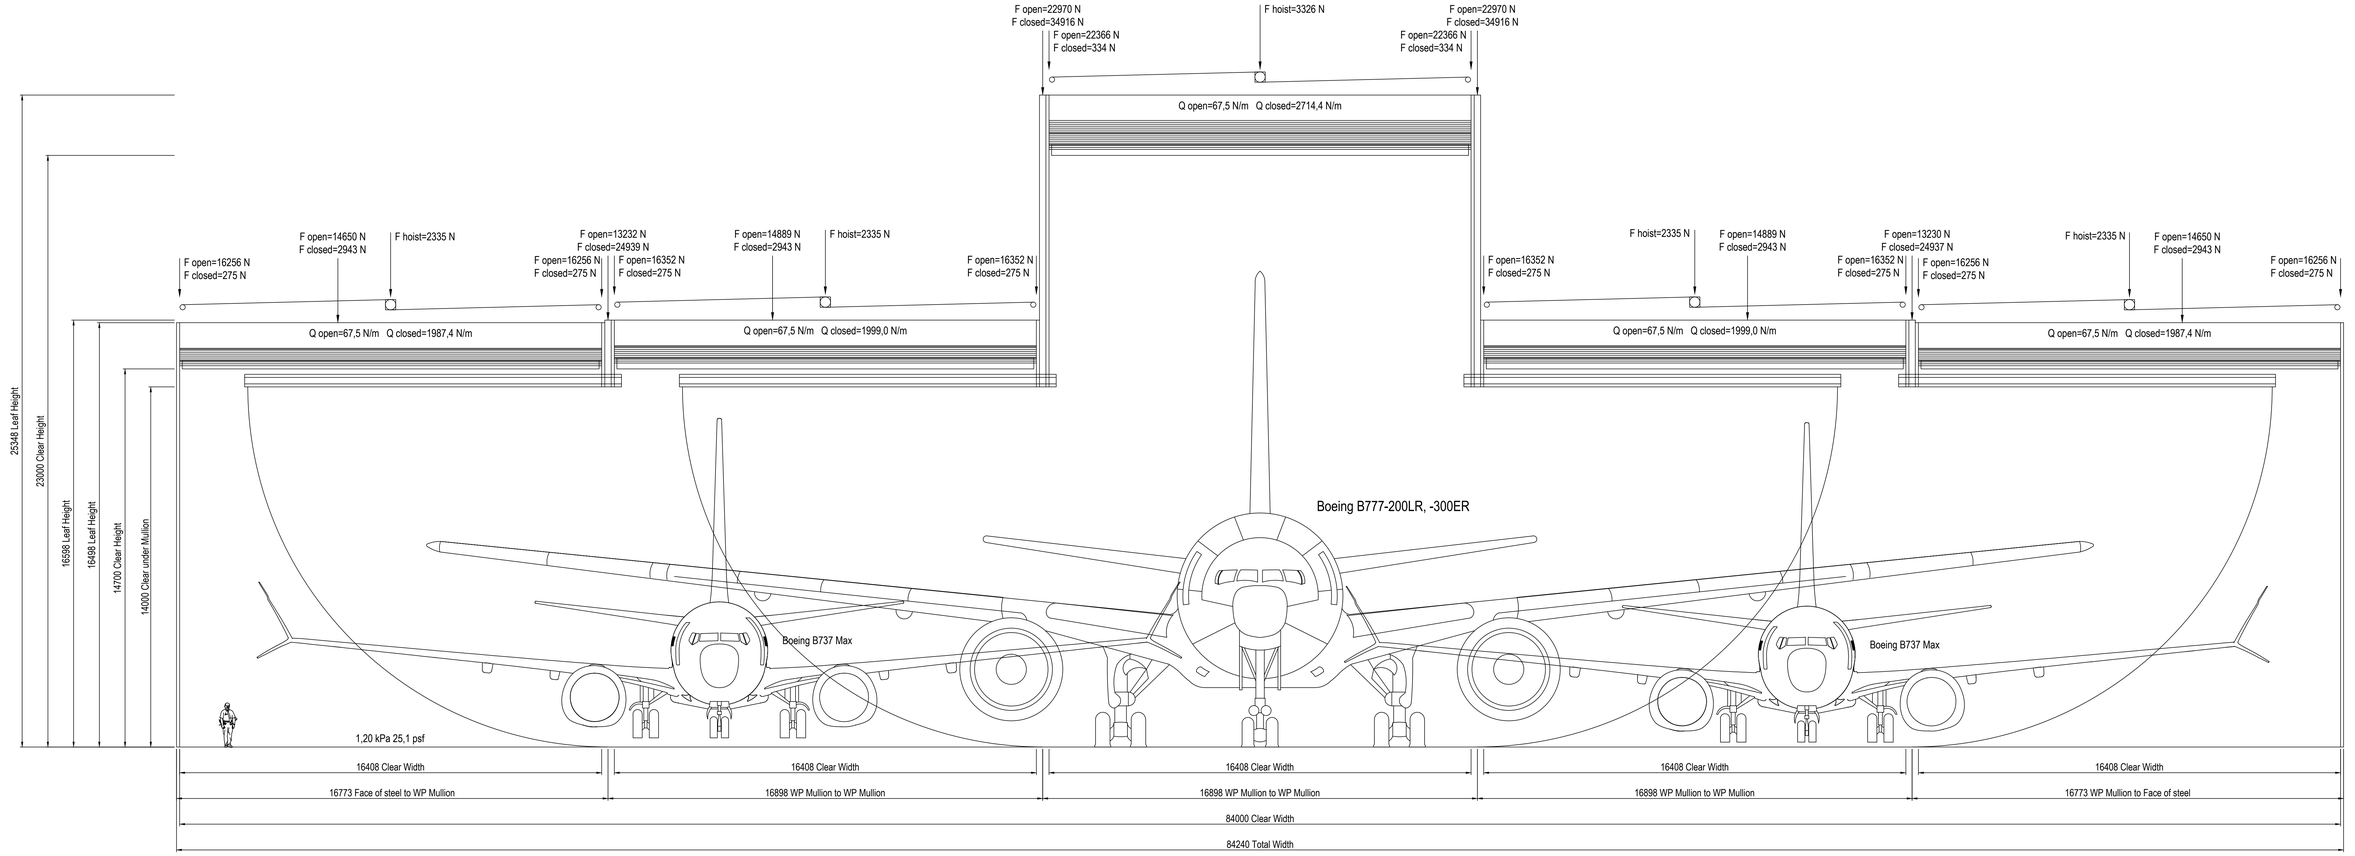


Contact Information

Ashish Nair
Sales Manager - Middle East
MEGADOOR/
ASSA ABLOY Entrance Systems
P.O. Box 80983
Dubai, United Arab Emirates
Visiting address: Dubai Investment Park 1
Phone: +971 (0)4 88 52888
Mobile: +971 (0)50 632 04 95
E-mail: ashish.achuthan@assaabloy.com
www.assaabloyentrance.ae

Quotation only. Do not use for design.
Nominal static vertical loads are indicated.
A dynamic surload factor of 1.25 should be added to door leaf loads in open position.
Includes items provided by ASSA ABLOY Entrance Systems only.
Total weight: 32543 kg
Total static weight: 32154 kg
Total motor power: 32,3 kW
Total rated current: 64,9 A
Total peak current: 81,1 A
Power supply: 400V/50Hz/3ph
(max. allowed voltage drop at start: 5%)
Control system: 24V
Mains power to control panel supplied by others than ASSA ABLOY Entrance Systems.

ASSA ABLOY

SALES REP. Ashish Nair	DATE ISSUED 24-3-2021
SALES No. 221-129	DATE DRAWN 24-3-2021
SCALE N.T.S.	
DRAWING No. 221-129	REVISION

GMR Aero Technic Hangar 1

Mumbai
India

Load diagram