


PRODUCED BY AN AUTODESK EDUCATIONAL PRODUCT

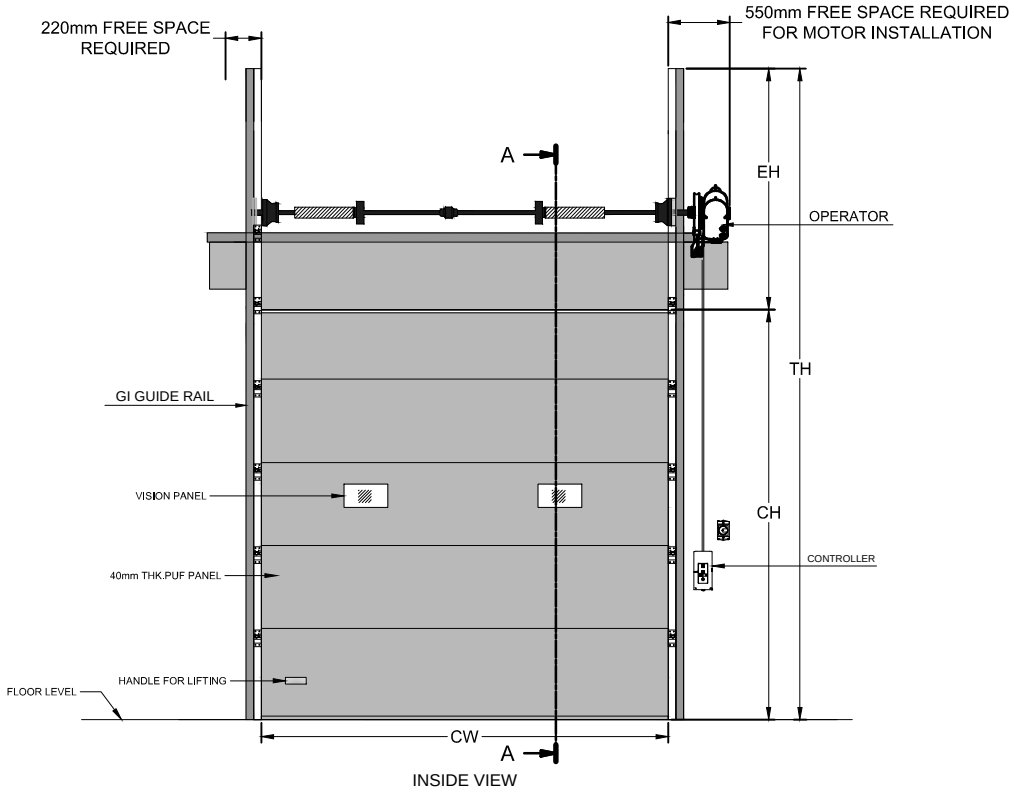

INSIDE VIEW

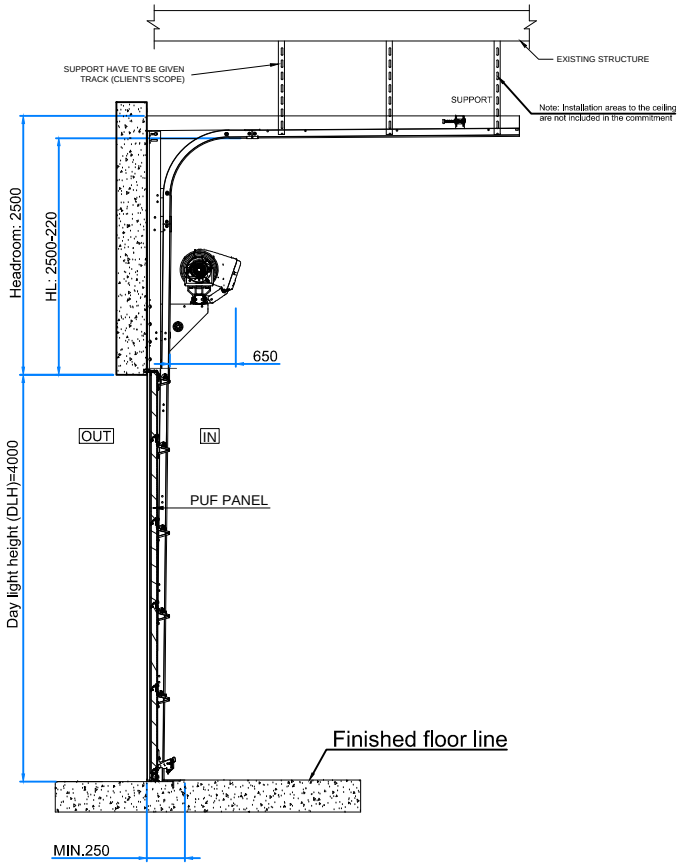

SECTION A-A

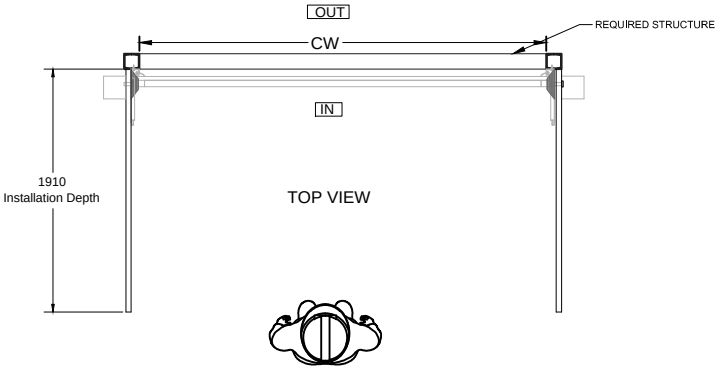

TOP VIEW

SR NO	CLEAR WIDTH	CLEAR HEIGHT	QTY	TH	EH
01	4000mm	4000mm	2	6500	2500

R02	AKASH		1).TOTAL HEIGHT UPDATED.
R01	SURAJ		1).HEIGHT CHANGED. 2).GUIDE DETAIL ADDED.
REV NO	DRAWN	SIGN	DESCRIPTION

TOLERANCE: ±10mm

This drawing & design is the property of NIHVA TECHNOLOGIES. Not to be sold or copied to any other concern.

TITLE
SECTIONAL DOOR (HL)

NIHVA TECHNOLOGIES PVT. LTD. PUNE
NIHVA TECHNOLOGIES PVT. LTD.
Tel : 020 66304033
Website:- www.nihva.com
Email:- info@nihva.com

	NAME	SIGN	DATE
DRAWN	SURAJ		16/07/17
CHECK	VIKRANT		16/07/17
APPROVAL	R.D		16/07/17

CLIENT -PROJECTSPOOL ENGG. SERVICE PVT. LTD.
PROJECT -
SITE - PUNE.
If any queries contact : design@nihva.com
DWG. NO. : NIHVA/18-19/0087/R02
REV: 02
ALL DIMENSION ARE IN mm
SCALE: NTS
WT:
SHEET: 01 OF 01

PRODUCED BY AN AUTODESK EDUCATIONAL PRODUCT