

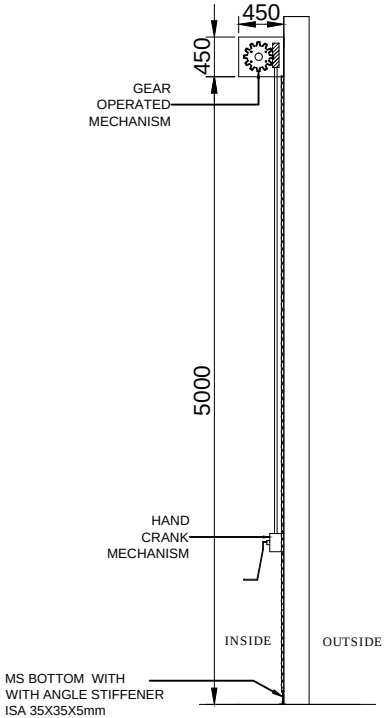



SIDE VIEW

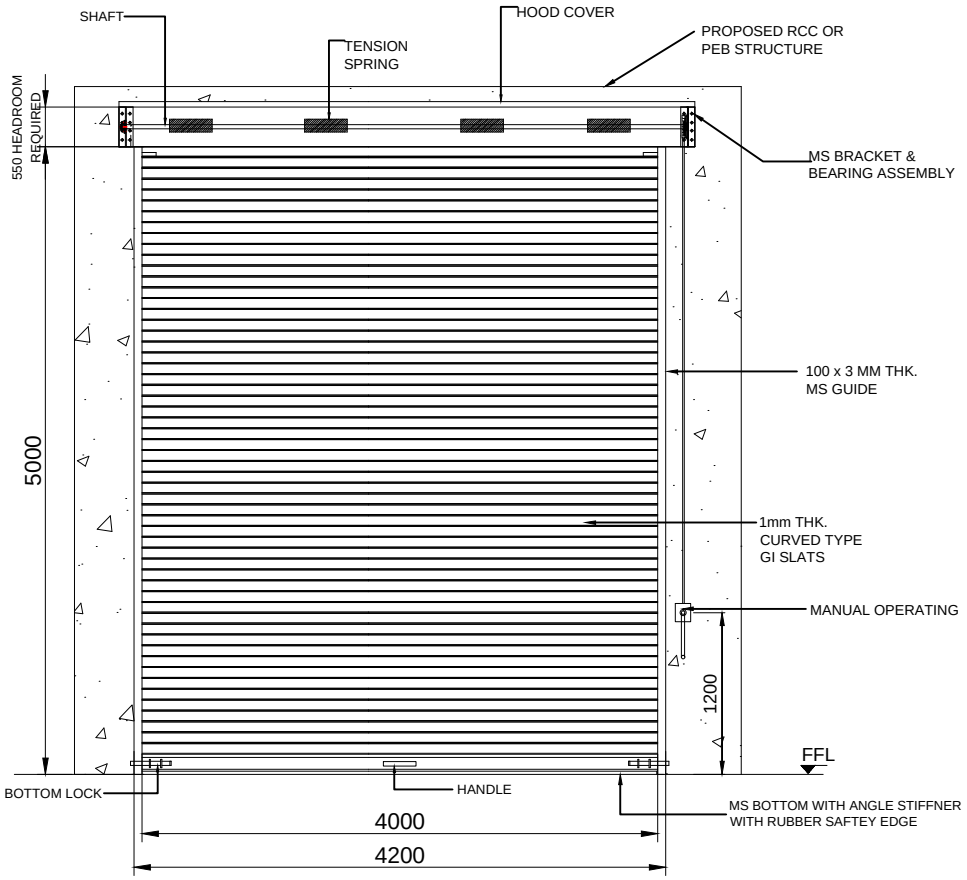


INSIDE ELEVATION

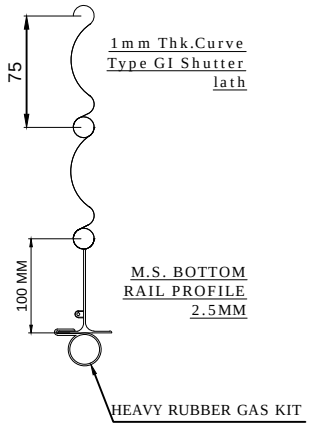

M.S. BOTTOM RAIL PROFILE 2.5MM

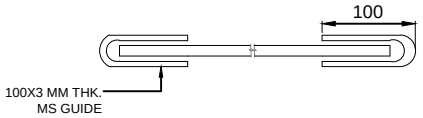

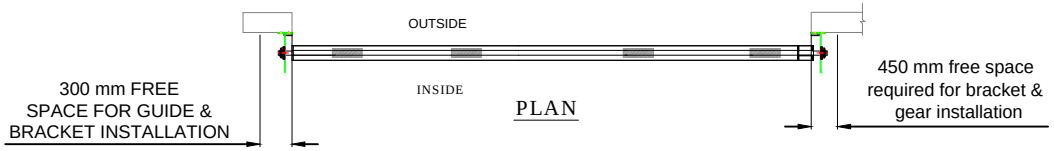

PLAN

TOLERANCE - ±10mm

S.N.	LOCATION	SIZE	QUANTITY
1	B7E	4000(W)X5000(H)	01

NOTE-
1. ALL CIVIL WORK WILL BE CLIENT'S SCOPE.
2.STRUCTURE REQUIRED FOR SHUTTER IS IN CLIENT'S SCOPE.
3.FINAL FINISH OF SHUTTER WILL BE IN POWDER COATING OF APPROVED COLOR i.e. RAL 7001.

This drawing & design is the property of NIHVA TECHNOLOGIES. Not to be sold or copied to any other concern.

TITLE	GEAR OPERATED ROLLING SHUTTER 4mX5m With Right side gearbox			NIHVA TECHNOLOGIES PVT. LTD. PUNE
	NAME	SIGN	DATE	Tel : 020 66304033
DRAWN	SURAJ		21.08.2018	Email:- info@nihva.com
CHECK	PRADEEP		21.08.2018	Website:- www.nihva.com
APPRD.	R.D		21.08.2018	

NIHVA TECHNOLOGIES PVT. LTD.

CLIENT - INDOSPACE			
PROJECT - BUILDING B7E			
SITE LOCATION - CHAKAN 1			
If any queries contact : design@nihva.com	DWG. NO. : NIHVA/18-19/0101		REV- 0
ALL DIMENSION ARE IN mm	SCALE: NTS	WT:	SHEET: 01 OF 01