


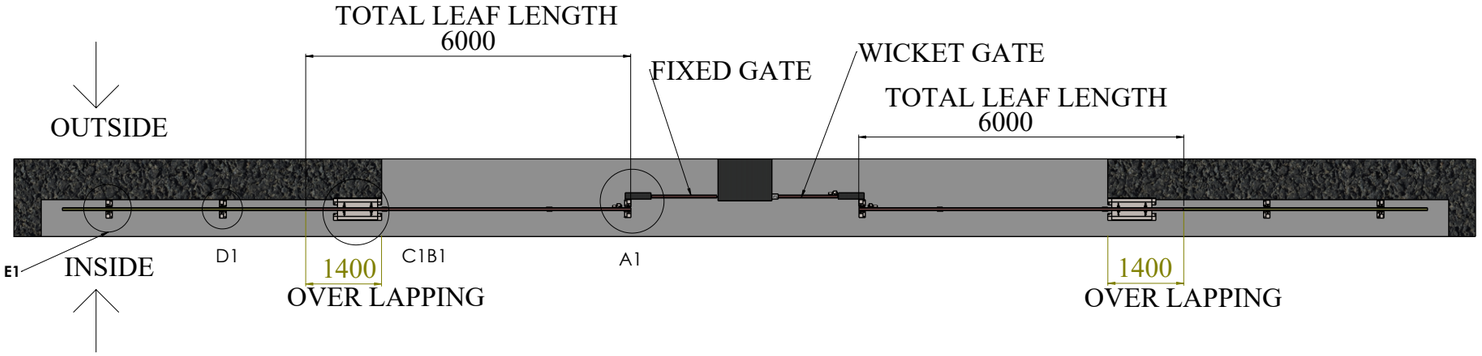


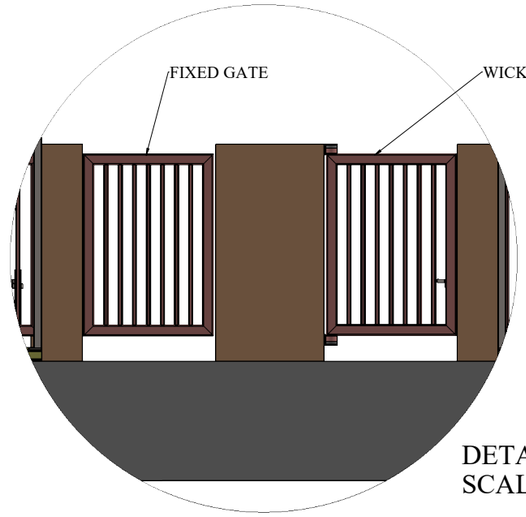


DETAIL E1
SCALE 1 : 20

FIXED GATE AND SWING
GATE VIEW

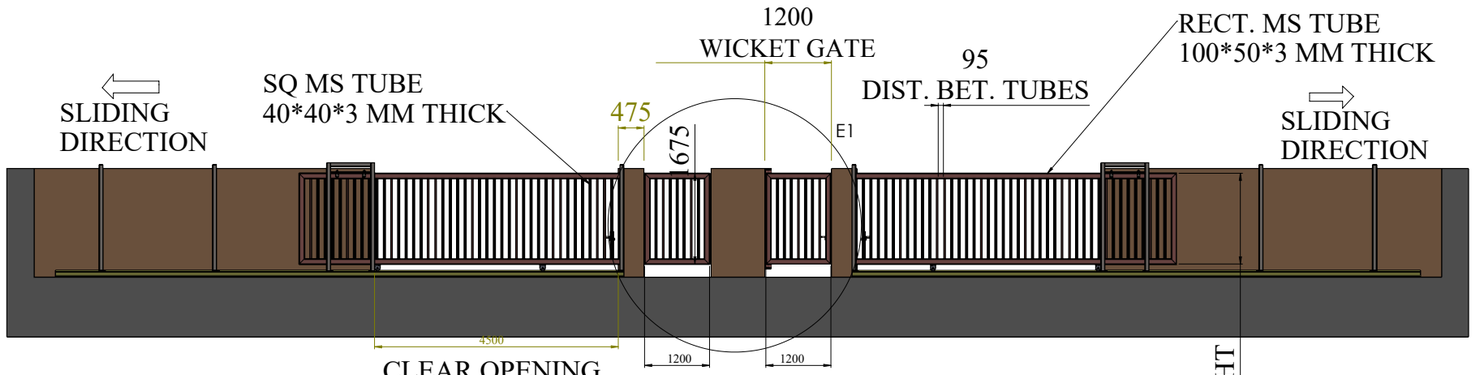


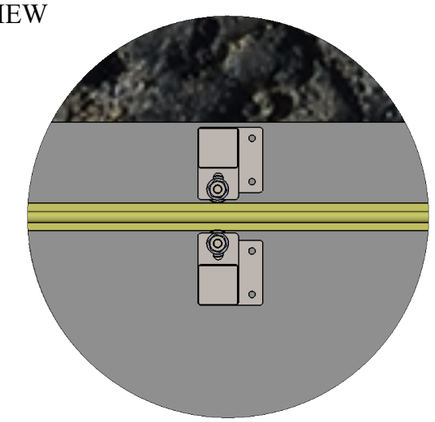

DETAIL D1
SCALE 1 : 4

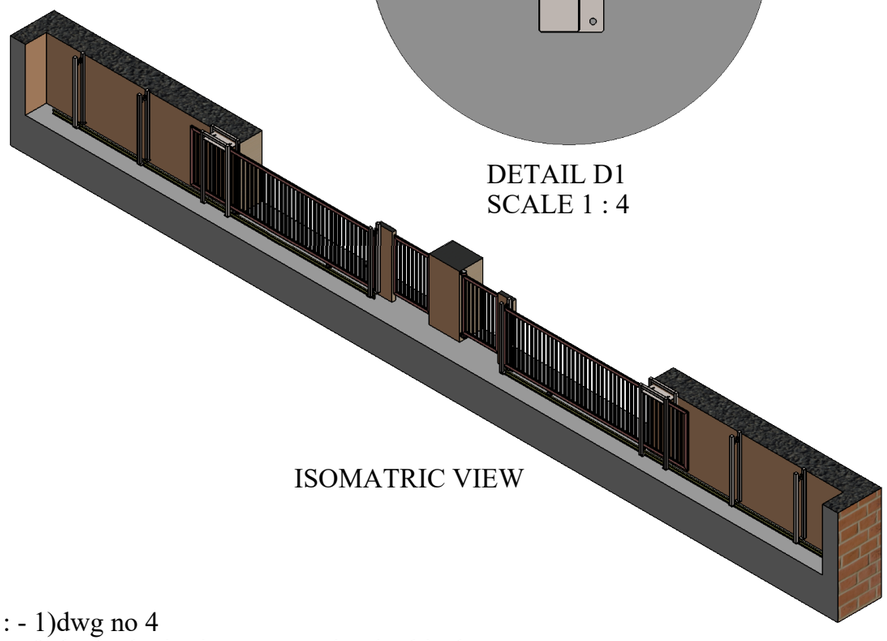


ISOMATRIC VIEW

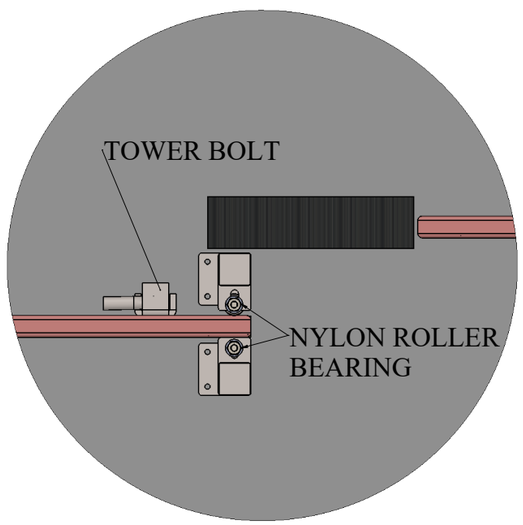

POST 1 AND NYLON ROLLER
BEARING ASSEM.

DETAIL A1
SCALE 1 : 5

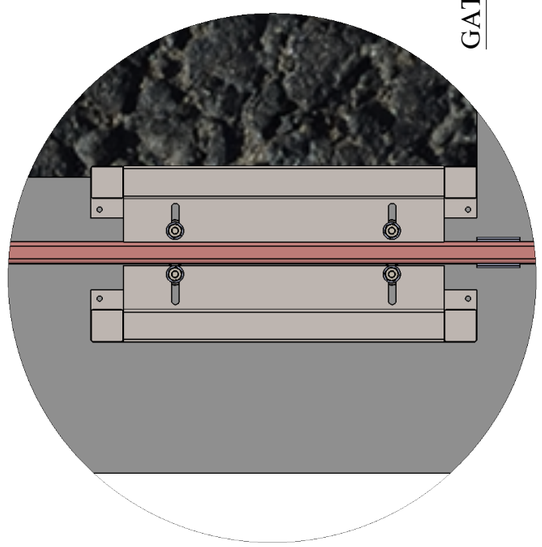

POST 2 AND NYLON ROLLER
BEARING ASSEM.

DETAIL C1B1
SCALE 1 : 5

Note : - 1)dwg no 4
2) barbed wire is not menstion in this dwg.
3)Total column -10(A1,B1,C1,D1,E1 SAME AS RIGHT SIDE ADD 5 POST)
4) 03 column posts when the gates is in the closed position.(A1,B1,C1)
5) 04 column posts when the gates is in the fully open position.(B1,C1,D1,E1)

TITLE - GATE AUTOMATION				NIHVA TECHNOLOGIES PVT.LTD.PUNE Website - www.nihva.com	
DWG NO - NTPL-290-PM-004				PRODUCT - SLIDING_GATE	
	NAME	SIGNATURE	DATE	PROJECT NO - NTPL-290-PM	REVISION - 00
DRAWN	V.W.		29-07-2025	SITE LOCATION - AMRAVATI	WEIGHT -
CHKD	B.S.		29-07-2025	MATRIAL -	QTY - 1
APP'D	V.T.		29-07-2025		
If any queries contact - design@nihva.com				PROJECTION METHOD:	SCALE :
ALL DIMENSION ARE IN mm			A0		SHEET 1 OF 1