
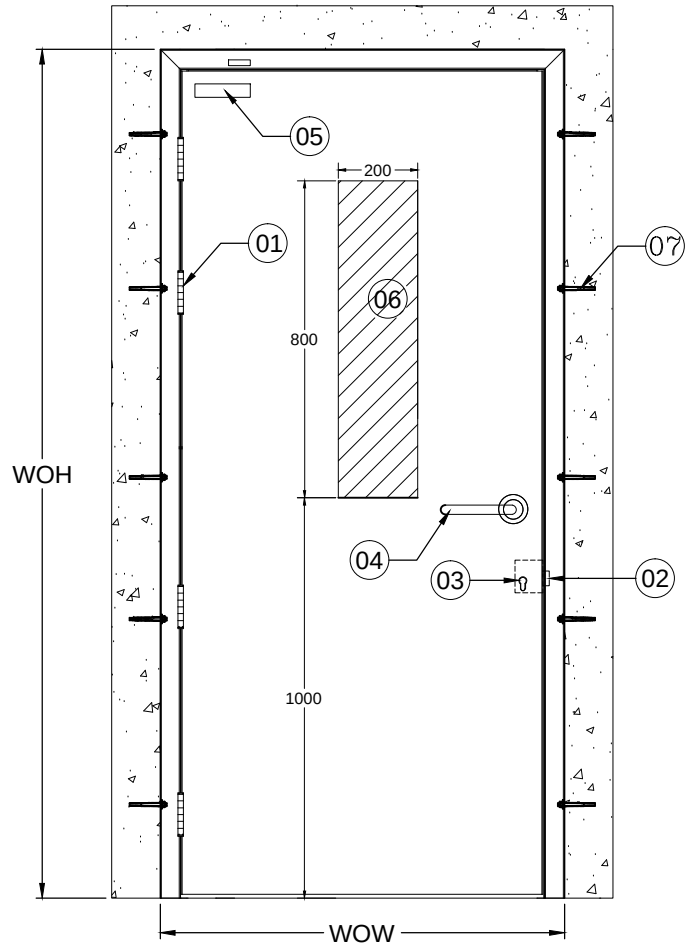


OUTSIDE ELEVATION

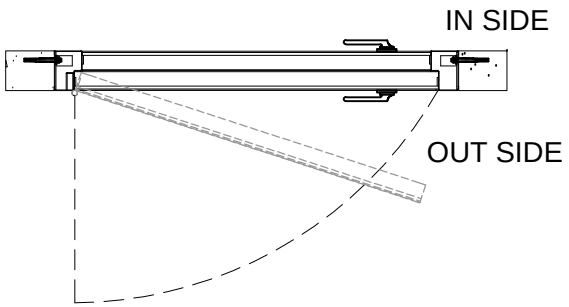

Abbrevation's:
WOW-Wall Opening Width
WOH-Wall Opening Height

Hardware List :-

SR.NO	DESCRIPTION	QTY.
01	HINGES	04 Nos.
02	DEAD LOCK	01 No.
03	CYLINDER WITH BOTH SIDE KEY	01 No.
04	BOTH SIDE LEVER HANDLE	01 No.
05	DOOR CLOSER	01 No.
06	VISION PANEL 200X800	01 No.
07	ANCHOR FASTENERS	10 Nos.

DOOR OPENING TYPE: TYPE 3 - LEFT HAND REVERSE

(for opening type refer door handling sheet)

Door Sizes :-

SR.NO	WOW	WOH	QTY.
01	1000	2100	02 NOS.

COLOR : RAL 7035 LIGHT GRAY

NOTE:-
*All Dimensions are in mm.
*Tolerance:-All Linear Dimensions ±3mm,Others ±0.5mm.
*The Drawing Is For Location of Hardware only. Drawing Does Not Represent The Hardware For More Clarity, Please Go Through Hardware Broucher.

TOLERANCE : All Linear Dimensions ±3 mm,Others ±1mm

NIHVA TECHNOLOGIES PVT. LTD.
NIHVA TECHNOLOGIES PVT. LTD. PUNE
Email:- info@nihva.com
Website:- www.nihva.com

TITLE:

STEEL DOOR(SINGLE LEAF)

CLIENT'S APPROVAL :

CLIENT -

PROJECT -

SITE LOCATION -

DWG. NO. : NIHVA/16-17/

SCALE: NTS	WT:	SHEET:1 OF 1

DRAWN BY: ANIL KHOT DATE: 29-07-2016

CHECK : ANIL DATE: 29-07-2016

If any queries contact : projects@nihva.com

NOTE: ALL DIMENSION ARE IN mm

THIS DRAWING & DESIGNING IS THE PROPERTY OF NIHVA TECHNOLOGIES. NOT BE SOLD OR COPY TO ANY OTHER CONCERN.