
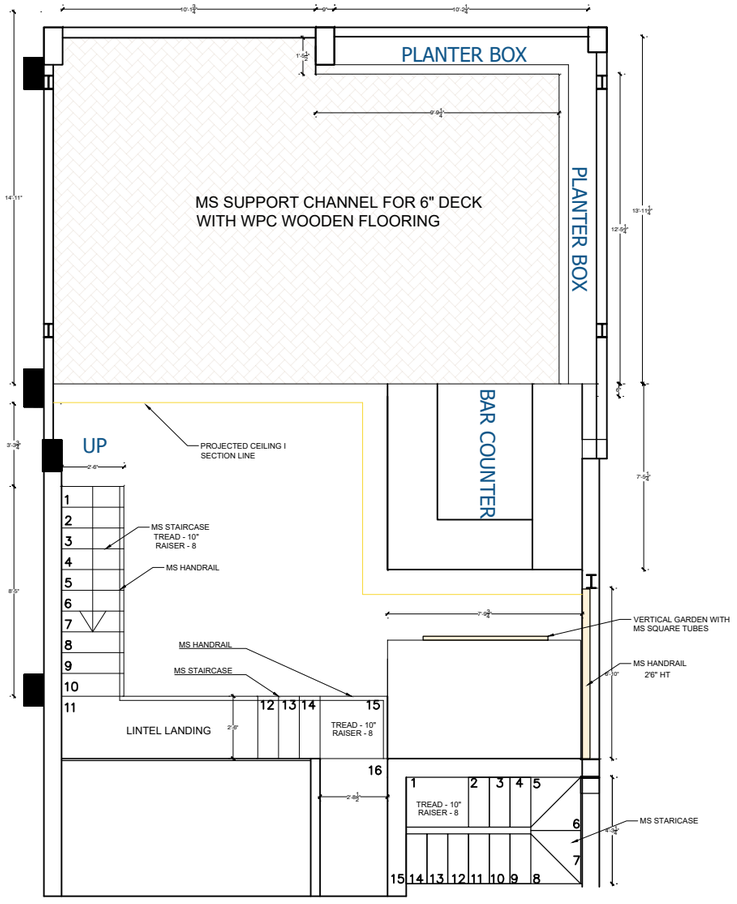


FLOOR PLAN

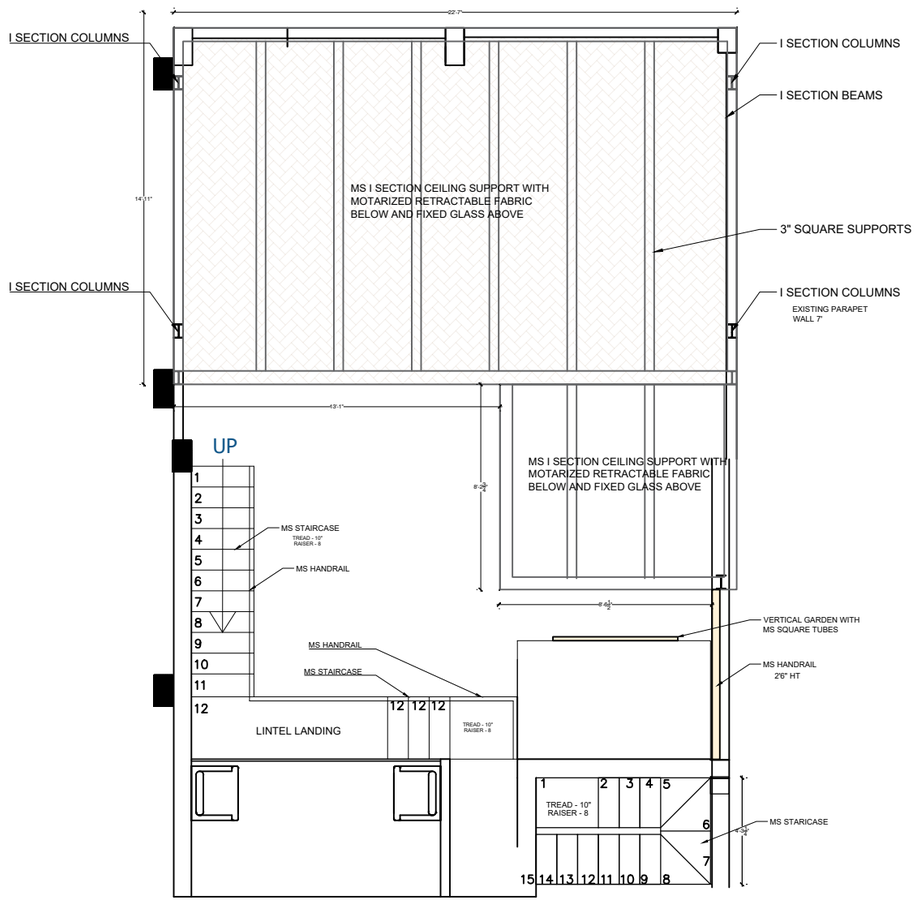

CEILING PLAN

GENERAL NOTES:

1. ALL DIMENSIONS ARE IN FEET AND INCHES.
2. ALL OPENING DIMENSIONS TO BE CHECKED AND VERIFIED AT SITE BEFORE FABRICATION OF CASEMENTS.
3. ALL LEVELS ARE IN FEET AND INCHES AND ARE FINISHED LEVELS OTHER THAN WHAT IS MENTIONED FOR OPEN TERRACES.
4. DO NOT SCALE DRAWINGS. ONLY WRITTEN DIMENSIONS SHALL BE FOLLOWED, ANY DISCREPANCIES NOTED SHALL BE BROUGHT TO THE NOTICE OF THE ARCHITECT PRIOR TO EXECUTION.
5. FOR DETAILS SUCH AS DOORS, WINDOWS, GRILLS, GATES, SKYLIGHT, TOILETS, STAIRCASES, HANDRAILS,RAILING, ETC. REFER RESPECTIVE ARCHITECTURAL DRAWINGS.
6. THESE DRAWINGS SHALL BE CORRELATED AND READ IN CONJUNCTION WITH RESPECTIVE CONSULTANT'S APPROVED DRAWINGS FOR STRUCTURAL MEMBERS, SERVICES SUCH AS PLUMBING,SANITARY,ELECTRICAL, AIR–CONDITIONING,VENTILATION, RAINWATER DRAINAGE & WATERPROOFING AND LANDSCAPING. ANY DISCREPANCIES NOTED SHALL BE BROUGHT TO THE NOTICE OF THE ARCHITECT PRIOR TO EXECUTION.
7. OPENING SIZES MENTIONED IN THE SCHEDULE ARE CLEAR OPENING SIZES AFTER PLASTERING.

NOTES

SCOPE OF WORK

1) DECK FLOORING CHANNEL WORK WITH WPC FLOORING FINISH
2) MS I SECTION SEMI COVERED I SECTION COLUMNS I SECTION BEAMS WITH MS SQUARE TUBE FOR SUPPORT WITH RETRACTABLE FABRIC BELOW AND FIXED GLASS ABOVE
3) MS I SECTION COVERED BAR COUNTER CEILING WITH MS SQUARE TUBE SUPPORTS AND WPC COVERED CEILING TOP AND BELOW.
4) BAR COUNTER WITH MS CABINETS WITH GRANITE COUNTER TOP WITH MS SQUARE TUBES WALL DISPLAY UNIT .
5) STAIRCASE FROM INFOMAL LIVING TO TERRACE LVL TO BE MADE WITH MS STAIRCASE WITH 10" THREAD AND 8" RAISER
6) STAIRCASE FROM TERRACE LVL TO 2ND TERRACE LVL TO BE MADE WITH MS STAIRCASE WITH 10" THREAD AND 8" RAISER

KARISHMA ARCHITEKTON

REYAN MARVEL - RESIDENCE INTERIOR


OPEN TERRACE - MS WORKS DETAILS

MUON ARCHITECTURE STUDIO

76, RAJAMMAL STREET,UDHAYA NAGAR ,
PORUR,CHENNAI - 600116
CONTACT - +91 9791141724
+91 8248673276
EMAIL : surendharan.ar@gmail.com

GOOD FOR CONSTRUCTION

REV	DRAWN BY	CHKD BY	DATE	SHEET
R0	SP	SP	08-03-2024	A3
DWG_NO	1116_2024_RM_INT_01			

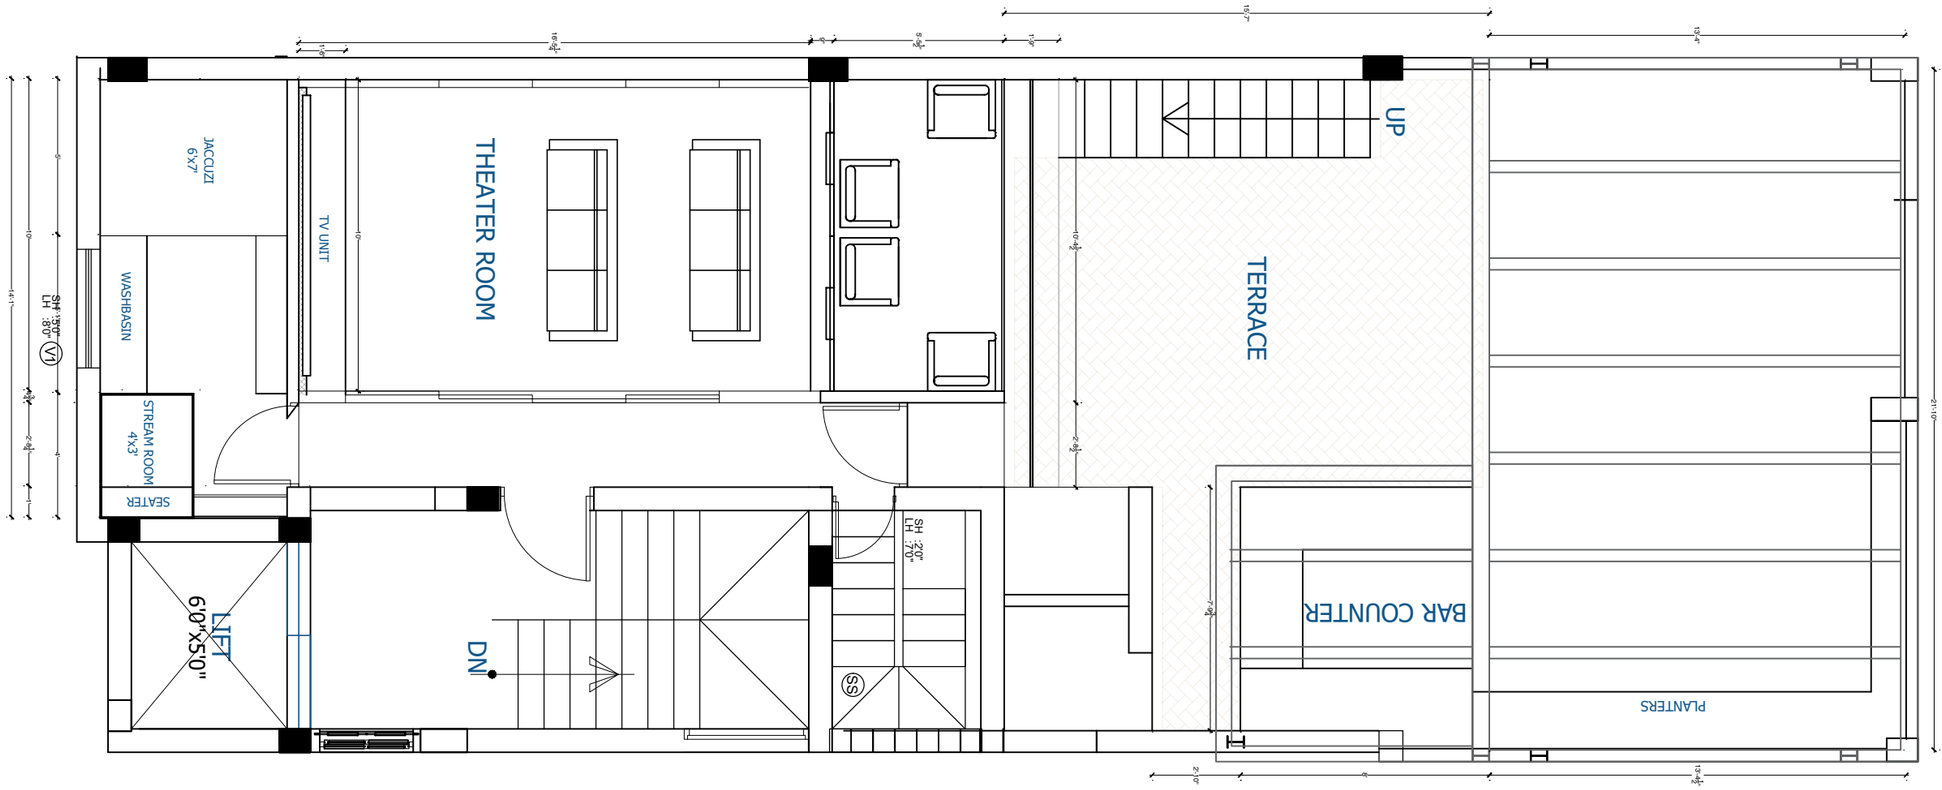

GENERAL NOTES:

1. ALL DIMENSIONS ARE IN FEET AND INCHES.
2. ALL OPENING DIMENSIONS TO BE CHECKED AND VERIFIED AT SITE BEFORE FABRICATION OF CASEMENTS.
3. ALL LEVELS ARE IN FEET AND INCHES AND ARE FINISHED LEVELS OTHER THAN WHAT IS MENTIONED FOR OPEN TERRACES.
4. DO NOT SCALE DRAWINGS. ONLY WRITTEN DIMENSIONS SHALL BE FOLLOWED, ANY DISCREPANCIES NOTED SHALL BE BROUGHT TO THE NOTICE OF THE ARCHITECT PRIOR TO EXECUTION.
5. FOR DETAILS SUCH AS DOORS, WINDOWS, GRILLS, GATES, SKYLIGHT, TOILETS, STAIRCASES, HANDRAILS,RAILING, ETC. REFER RESPECTIVE ARCHITECTURAL DRAWINGS.
6. THESE DRAWINGS SHALL BE CORRELATED AND READ IN CONJUNCTION WITH RESPECTIVE CONSULTANT'S APPROVED DRAWINGS FOR STRUCTURAL MEMBERS, SERVICES SUCH AS PLUMBING,SANITARY,ELECTRICAL, AIR–CONDITIONING,VENTILATION, RAINWATER DRAINAGE & WATERPROOFING AND LANDSCAPING. ANY DISCREPANCIES NOTED SHALL BE BROUGHT TO THE NOTICE OF THE ARCHITECT PRIOR TO EXECUTION.
7. OPENING SIZES MENTIONED IN THE SCHEDULE ARE CLEAR OPENING SIZES AFTER PLASTERING.

NOTES

KARISHMA ARCHITEKTON

REYAN MARVEL - RESIDENCE INTERIOR


FURNITURE LAYOUT - TERRACE FLOOR


MUON ARCHITECTURE STUDIO

76, RAJAMMAL STREET,UDHAYA NAGAR ,
PORUR,CHENNAI - 600116
CONTACT - +91 9791141724
+91 8248673276
EMAIL : surendharan.ar@gmail.com

GOOD FOR CONSTRUCTION

REV	DRAWN BY	CHKD BY	DATE	SHEET
R0	SP	SP	08-03-2024	A3
DWG_NO	1116_2024_RM_INT_01			

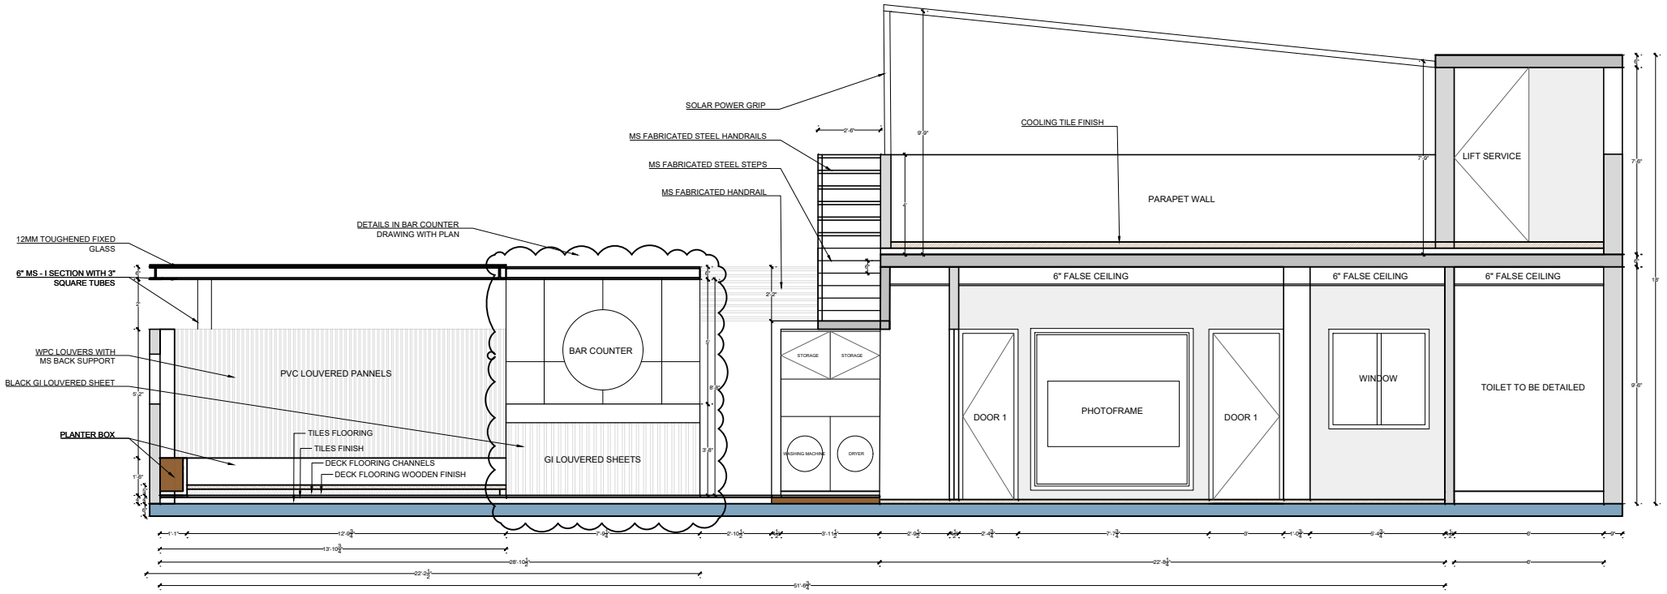

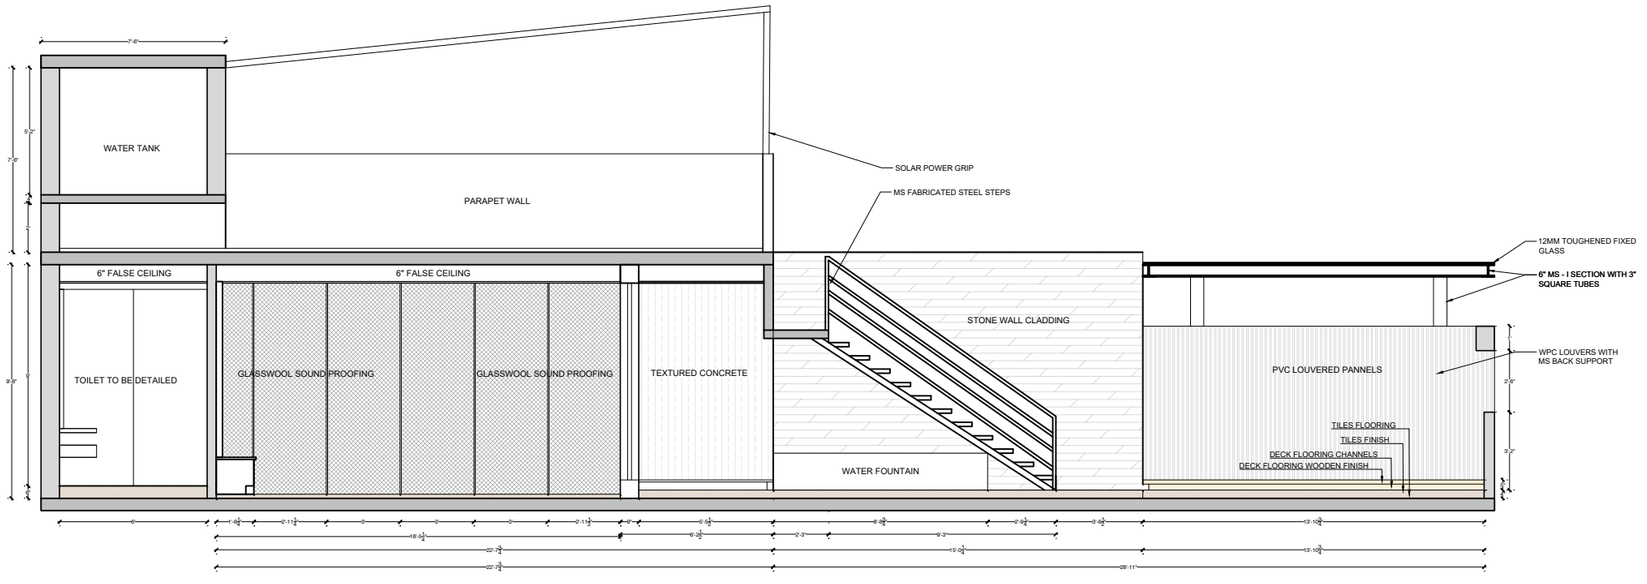

GENERAL NOTES:

1. ALL DIMENSIONS ARE IN FEET AND INCHES.
2. ALL OPENING DIMENSIONS TO BE CHECKED AND VERIFIED AT SITE BEFORE FABRICATION OF CASEMENTS.
3. ALL LEVELS ARE IN FEET AND INCHES AND ARE FINISHED LEVELS OTHER THAN WHAT IS MENTIONED FOR OPEN TERRACES.
4. DO NOT SCALE DRAWINGS. ONLY WRITTEN DIMENSIONS SHALL BE FOLLOWED, ANY DISCREPANCIES NOTED SHALL BE BROUGHT TO THE NOTICE OF THE ARCHITECT PRIOR TO EXECUTION.
5. FOR DETAILS SUCH AS DOORS, WINDOWS, GRILLS, GATES, SKYLIGHT, TOILETS, STAIRCASES, HANDRAILS,RAILING, ETC. REFER RESPECTIVE ARCHITECTURAL DRAWINGS.
6. THESE DRAWINGS SHALL BE CORRELATED AND READ IN CONJUNCTION WITH RESPECTIVE CONSULTANT'S APPROVED DRAWINGS FOR STRUCTURAL MEMBERS, SERVICES SUCH AS PLUMBING,SANITARY,ELECTRICAL, AIR–CONDITIONING,VENTILATION, RAINWATER DRAINAGE & WATERPROOFING AND LANDSCAPING. ANY DISCREPANCIES NOTED SHALL BE BROUGHT TO THE NOTICE OF THE ARCHITECT PRIOR TO EXECUTION.
7. OPENING SIZES MENTIONED IN THE SCHEDULE ARE CLEAR OPENING SIZES AFTER PLASTERING.

NOTES

KARISHMA ARCHITEKTON

REYAN MARVEL - RESIDENCE INTERIOR


TERRACE SECTION 1


MUON ARCHITECTURE STUDIO

76, RAJAMMAL STREET,UDHAYA NAGAR ,
PORUR,CHENNAI - 600116
CONTACT - +91 9791141724
+91 8248673276
EMAIL : surendharan.ar@gmail.com

GOOD FOR CONSTRUCTION

REV	DRAWN BY	CHKD BY	DATE	SHEET
R0	SP	SP	08-03-2024	A3
DWG_NO	1116_2024_RM_INT_01			

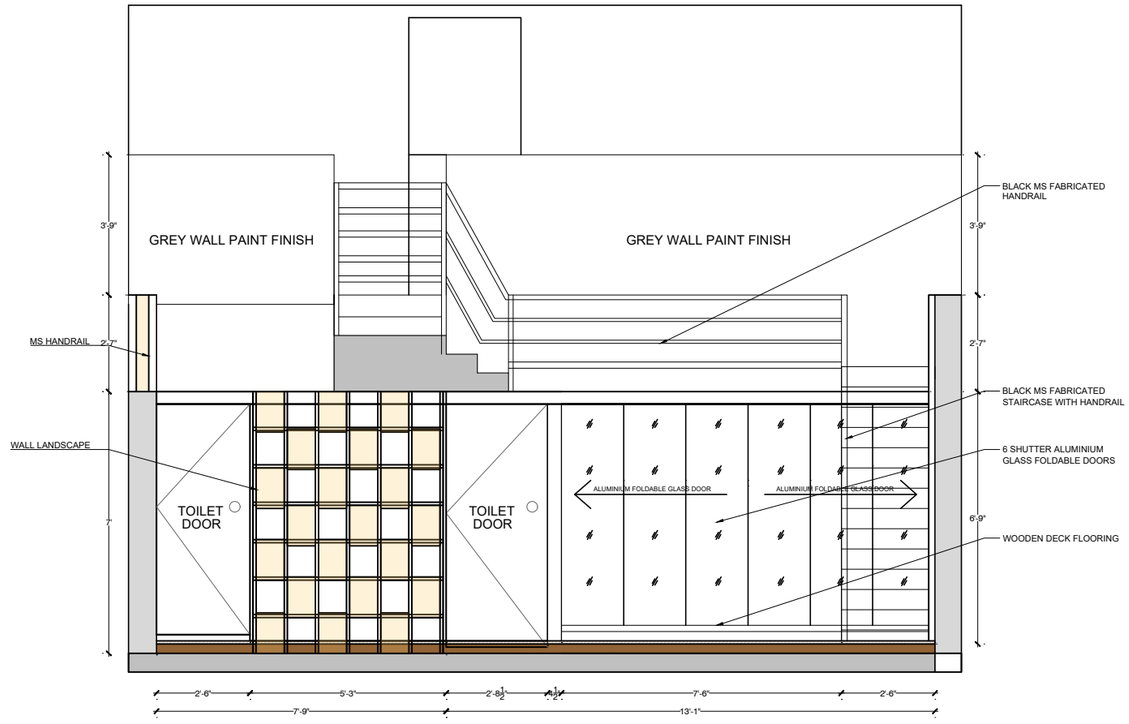

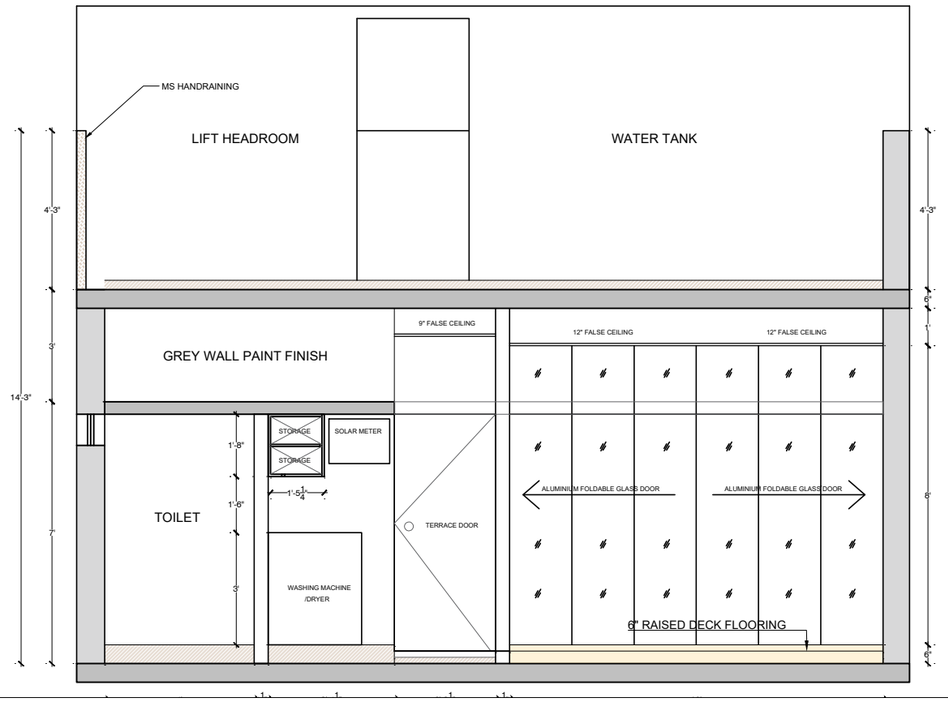

GENERAL NOTES:

1. ALL DIMENSIONS ARE IN FEET AND INCHES.
2. ALL OPENING DIMENSIONS TO BE CHECKED AND VERIFIED AT SITE BEFORE FABRICATION OF CASEMENTS.
3. ALL LEVELS ARE IN FEET AND INCHES AND ARE FINISHED LEVELS OTHER THAN WHAT IS MENTIONED FOR OPEN TERRACES.
4. DO NOT SCALE DRAWINGS. ONLY WRITTEN DIMENSIONS SHALL BE FOLLOWED, ANY DISCREPANCIES NOTED SHALL BE BROUGHT TO THE NOTICE OF THE ARCHITECT PRIOR TO EXECUTION.
5. FOR DETAILS SUCH AS DOORS, WINDOWS, GRILLS, GATES, SKYLIGHT, TOILETS, STAIRCASES, HANDRAILS,RAILING, ETC. REFER RESPECTIVE ARCHITECTURAL DRAWINGS.
6. THESE DRAWINGS SHALL BE CORRELATED AND READ IN CONJUNCTION WITH RESPECTIVE CONSULTANT'S APPROVED DRAWINGS FOR STRUCTURAL MEMBERS, SERVICES SUCH AS PLUMBING,SANITARY,ELECTRICAL, AIR–CONDITIONING,VENTILATION, RAINWATER DRAINAGE & WATERPROOFING AND LANDSCAPING. ANY DISCREPANCIES NOTED SHALL BE BROUGHT TO THE NOTICE OF THE ARCHITECT PRIOR TO EXECUTION.
7. OPENING SIZES MENTIONED IN THE SCHEDULE ARE CLEAR OPENING SIZES AFTER PLASTERING.

NOTES

KARISHMA ARCHITEKTON

REYAN MARVEL - RESIDENCE INTERIOR

TERRACE SECTION 2


MUON ARCHITECTURE STUDIO

76, RAJAMMAL STREET,UDHAYA NAGAR ,
PORUR,CHENNAI - 600116
CONTACT - +91 9791141724
+91 8248673276
EMAIL : surendharan.ar@gmail.com


GOOD FOR CONSTRUCTION

REV	DRAWN BY	CHKD BY	DATE	SHEET
R0	SP	SP	08-03-2024	A3
DWG_NO	1116_2024_RM_INT_01			


1)BAR COUNTER PLAN

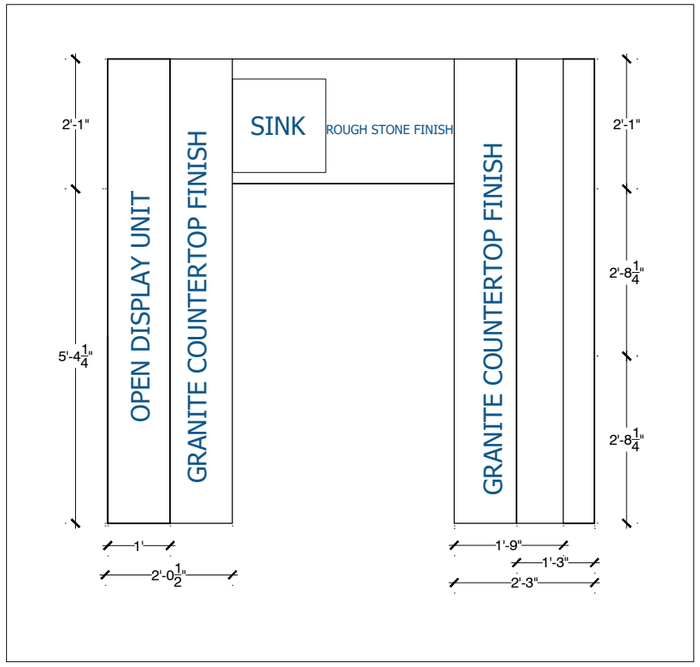


2) BAR COUNTER LOWER CABINET PLAN

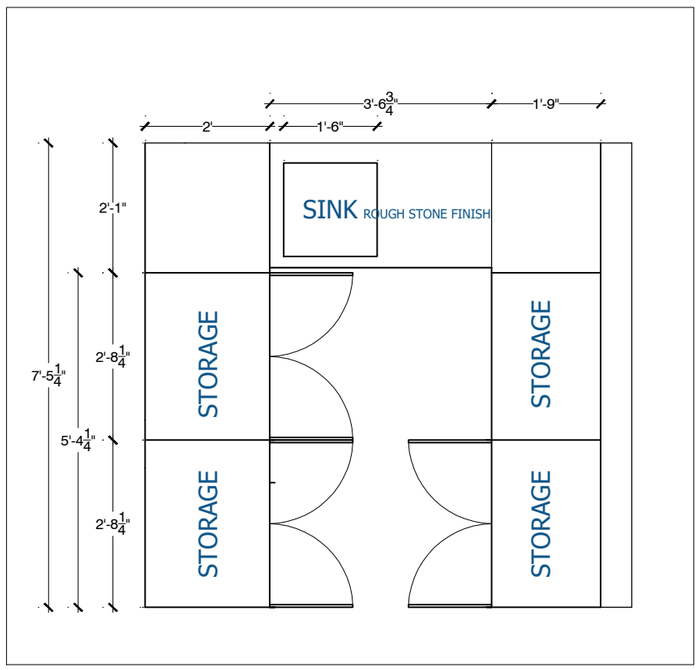

3) BAR COUNTER SECTION

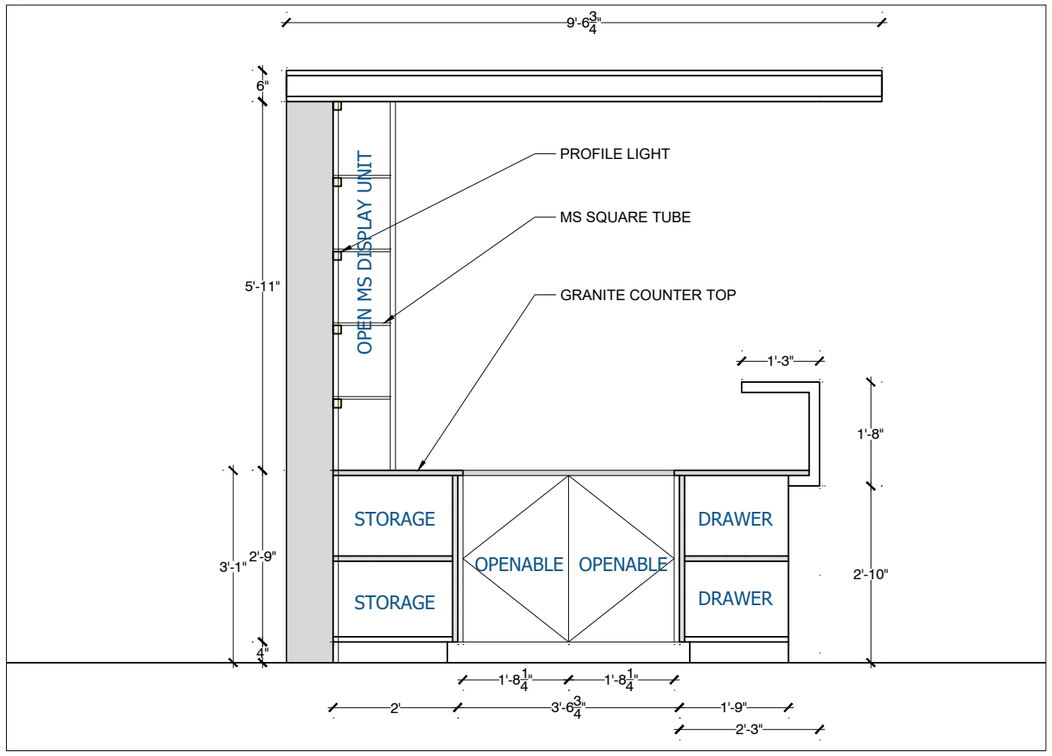

3) BAR COUNTER ELEVATION

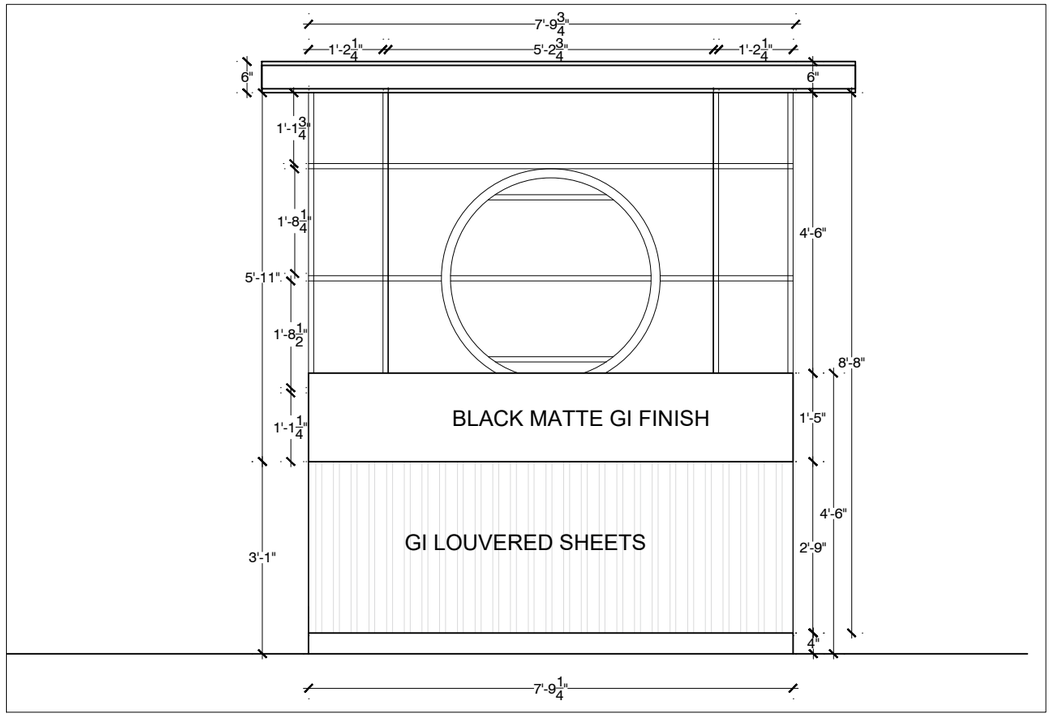

GENERAL NOTES:

1. ALL DIMENSIONS ARE IN FEET AND INCHES.
2. ALL OPENING DIMENSIONS TO BE CHECKED AND VERIFIED AT SITE BEFORE FABRICATION OF CASEMENTS.
3. ALL LEVELS ARE IN FEET AND INCHES AND ARE FINISHED LEVELS OTHER THAN WHAT IS MENTIONED FOR OPEN TERRACES.
4. DO NOT SCALE DRAWINGS. ONLY WRITTEN DIMENSIONS SHALL BE FOLLOWED, ANY DISCREPANCIES NOTED SHALL BE BROUGHT TO THE NOTICE OF THE ARCHITECT PRIOR TO EXECUTION.
5. FOR DETAILS SUCH AS DOORS, WINDOWS, GRILLS, GATES, SKYLIGHT, TOILETS, STAIRCASES, HANDRAILS,RAILING, ETC. REFER RESPECTIVE ARCHITECTURAL DRAWINGS.
6. THESE DRAWINGS SHALL BE CORRELATED AND READ IN CONJUNCTION WITH RESPECTIVE CONSULTANT'S APPROVED DRAWINGS FOR STRUCTURAL MEMBERS, SERVICES SUCH AS PLUMBING,SANITARY,ELECTRICAL, AIR–CONDITIONING,VENTILATION, RAINWATER DRAINAGE & WATERPROOFING AND LANDSCAPING. ANY DISCREPANCIES NOTED SHALL BE BROUGHT TO THE NOTICE OF THE ARCHITECT PRIOR TO EXECUTION.
7. OPENING SIZES MENTIONED IN THE SCHEDULE ARE CLEAR OPENING SIZES AFTER PLASTERING.

NOTES

KARISHMA ARCHITEKTON

REYAN MARVEL - RESIDENCE INTERIOR

BAR COUNTER DETAILS


MUON ARCHITECTURE STUDIO


76, RAJAMMAL STREET,UDHAYA NAGAR ,
PORUR,CHENNAI - 600116
CONTACT - +91 9791141724
+91 8248673276
EMAIL : surendharan.ar@gmail.com

GOOD FOR CONSTRUCTION

REV	DRAWN BY	CHKD BY	DATE	SHEET
R0	SP	SP	08-03-2024	A3
DWG_NO	1116_2024_RM_INT_01			


3) BAR COUNTER WITH TERRACE SECTION

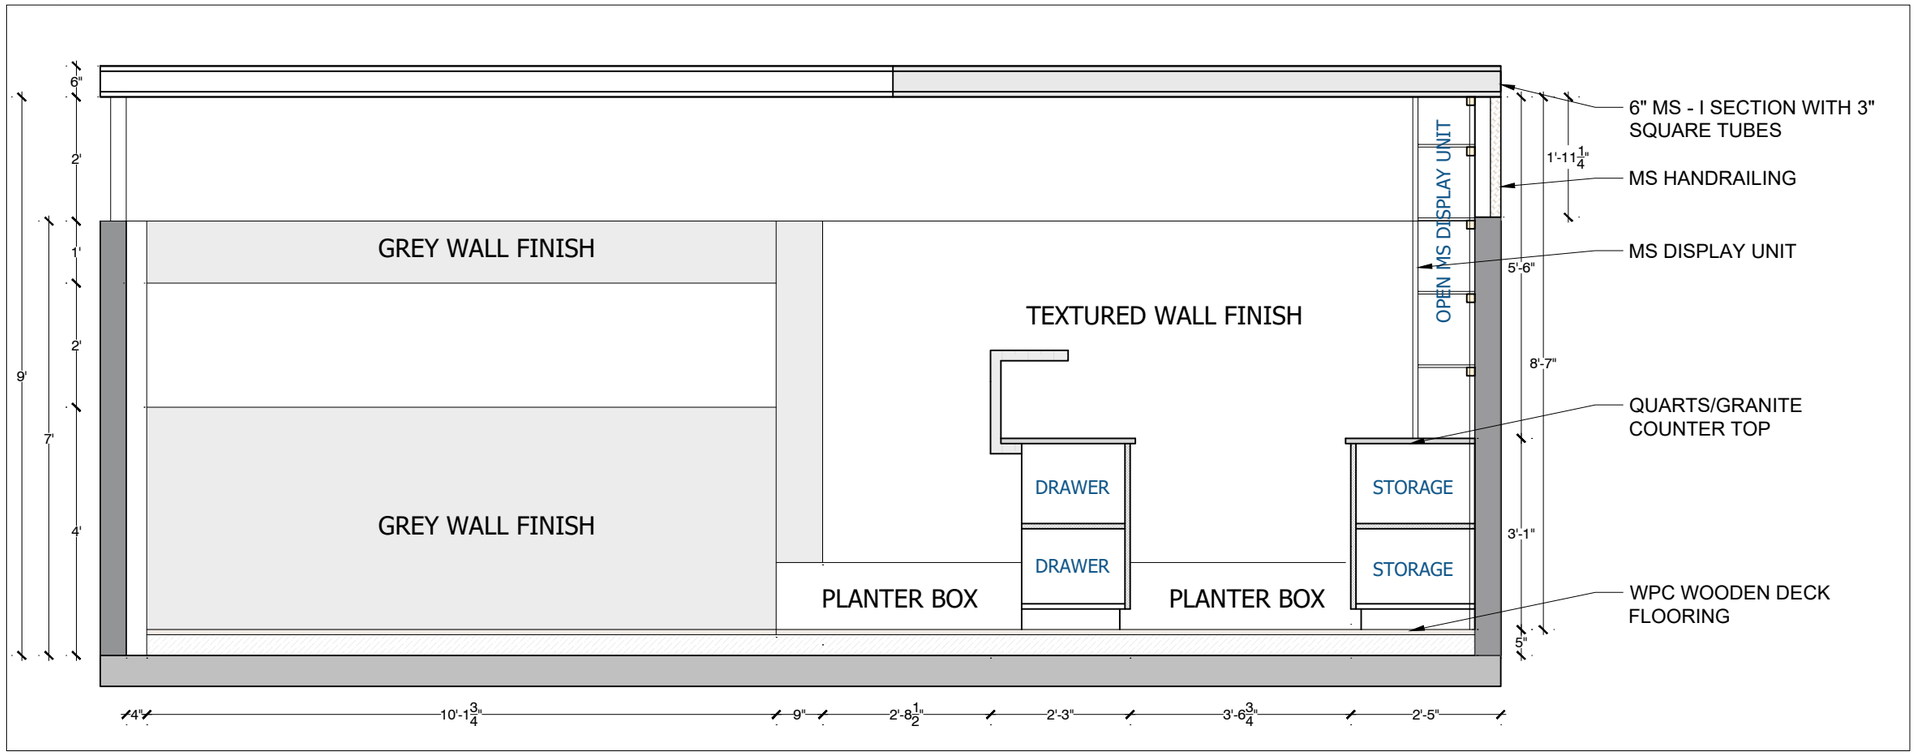

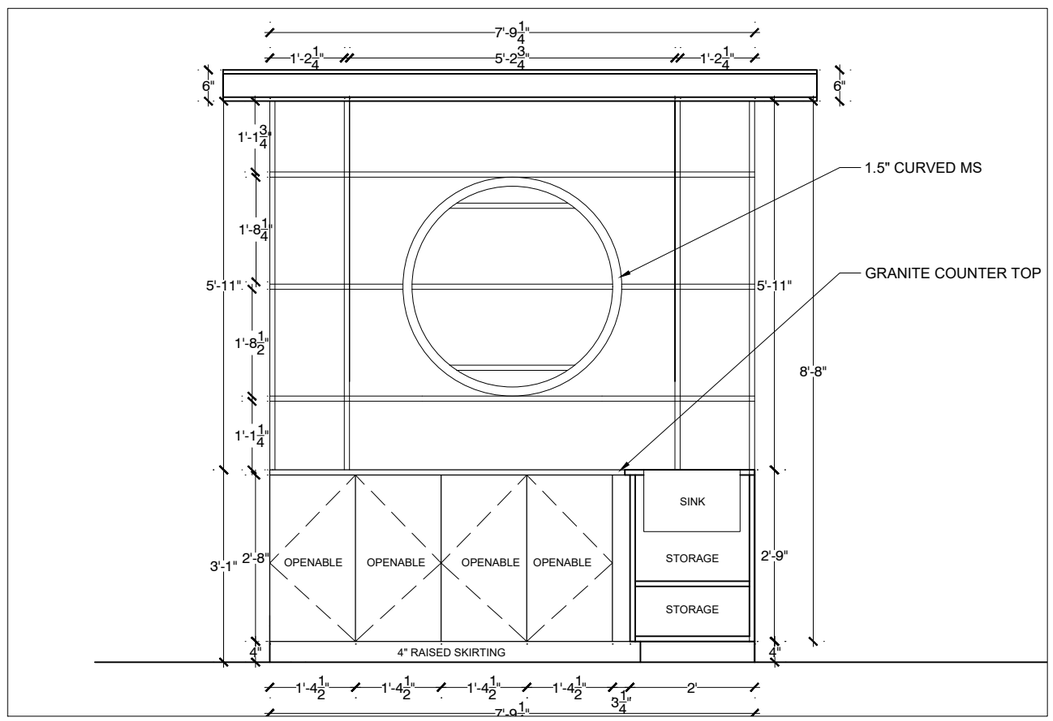

6) BAR COUNTER SECTIONAL ELEVATION 1

7) BAR COUNTER ELEVATION

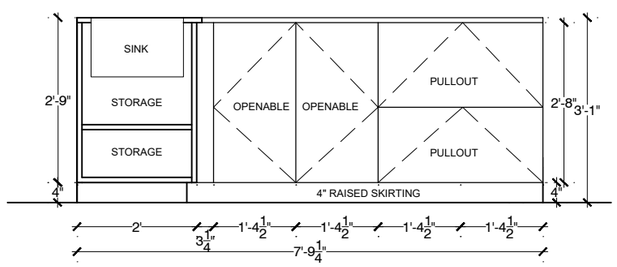

GENERAL NOTES:

1. ALL DIMENSIONS ARE IN FEET AND INCHES.
2. ALL OPENING DIMENSIONS TO BE CHECKED AND VERIFIED AT SITE BEFORE FABRICATION OF CASEMENTS.
3. ALL LEVELS ARE IN FEET AND INCHES AND ARE FINISHED LEVELS OTHER THAN WHAT IS MENTIONED FOR OPEN TERRACES.
4. DO NOT SCALE DRAWINGS. ONLY WRITTEN DIMENSIONS SHALL BE FOLLOWED, ANY DISCREPANCIES NOTED SHALL BE BROUGHT TO THE NOTICE OF THE ARCHITECT PRIOR TO EXECUTION.
5. FOR DETAILS SUCH AS DOORS, WINDOWS, GRILLS, GATES, SKYLIGHT, TOILETS, STAIRCASES, HANDRAILS,RAILING, ETC. REFER RESPECTIVE ARCHITECTURAL DRAWINGS.
6. THESE DRAWINGS SHALL BE CORRELATED AND READ IN CONJUNCTION WITH RESPECTIVE CONSULTANT'S APPROVED DRAWINGS FOR STRUCTURAL MEMBERS, SERVICES SUCH AS PLUMBING,SANITARY,ELECTRICAL, AIR–CONDITIONING,VENTILATION, RAINWATER DRAINAGE & WATERPROOFING AND LANDSCAPING. ANY DISCREPANCIES NOTED SHALL BE BROUGHT TO THE NOTICE OF THE ARCHITECT PRIOR TO EXECUTION.
7. OPENING SIZES MENTIONED IN THE SCHEDULE ARE CLEAR OPENING SIZES AFTER PLASTERING.

NOTES

KARISHMA ARCHITEKTON

REYAN MARVEL - RESIDENCE INTERIOR


BAR COUNTER DETAILS

MUON ARCHITECTURE STUDIO


76, RAJAMMAL STREET,UDHAYA NAGAR ,
PORUR,CHENNAI - 600116
CONTACT - +91 9791141724
+91 8248673276
EMAIL : surendharan.ar@gmail.com

GOOD FOR CONSTRUCTION


REV	DRAWN BY	CHKD BY	DATE	SHEET
R0	SP	SP	08-03-2024	A3
DWG_NO	1116_2024_RM_INT_01			

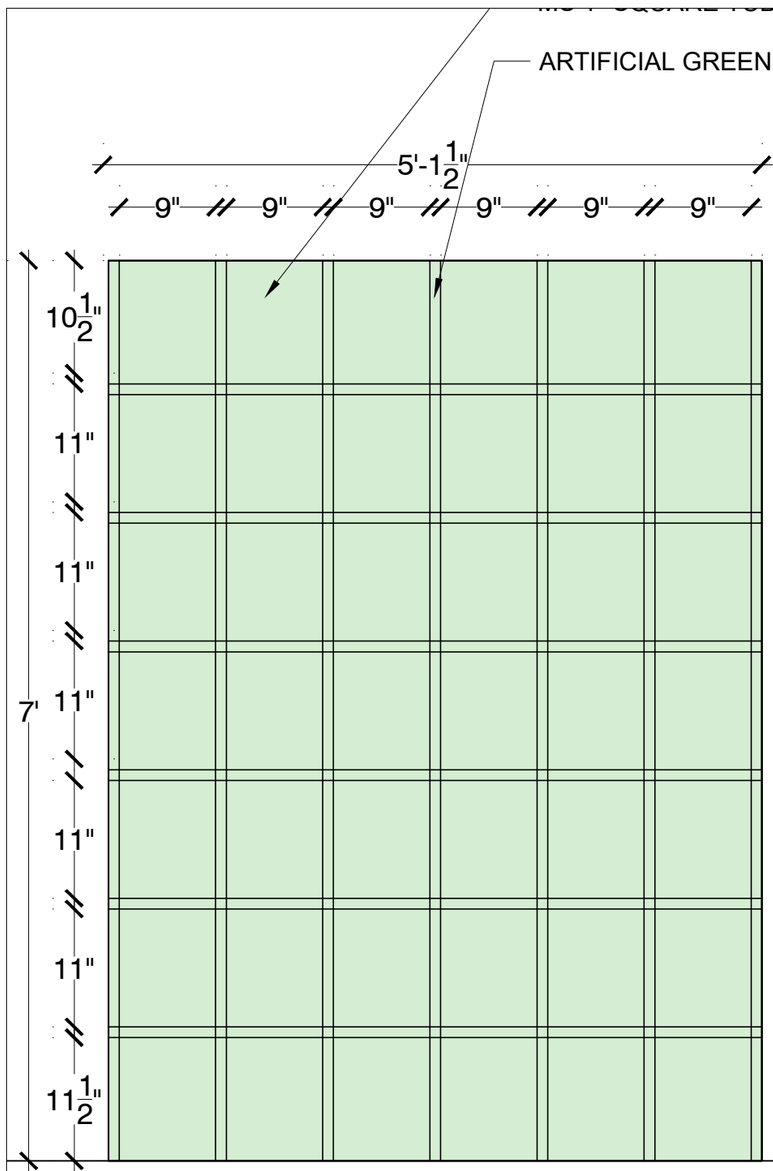

MS FRAMEWORK

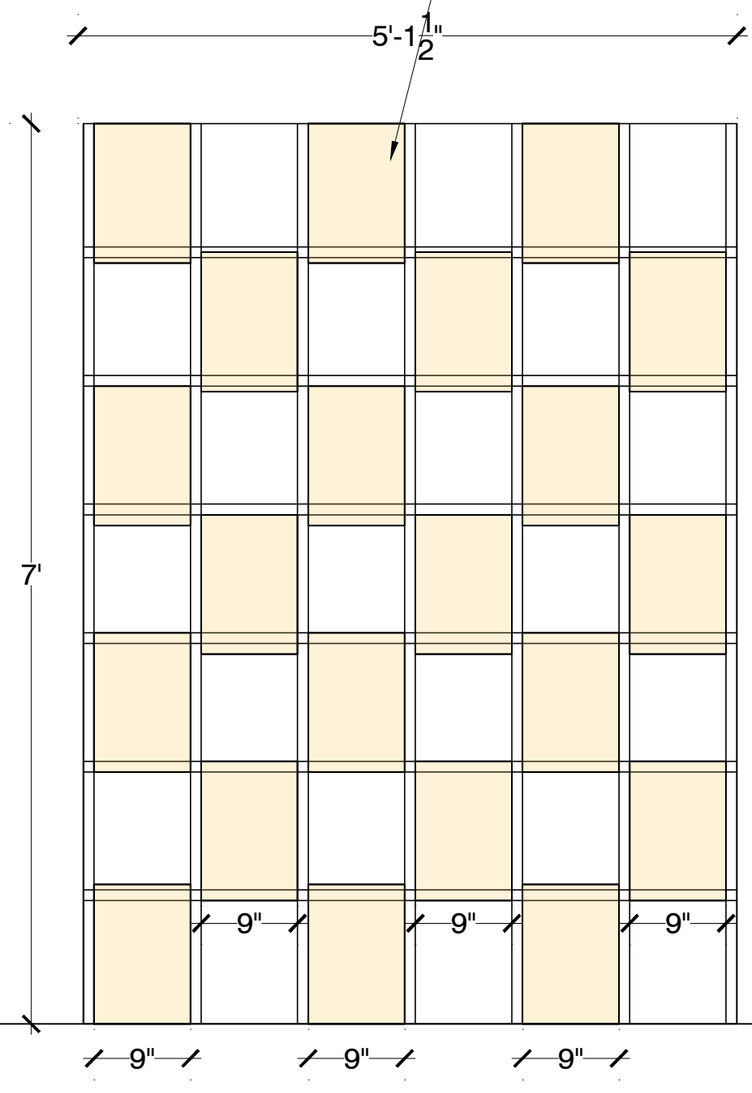

PLANTER BOX DETAILS

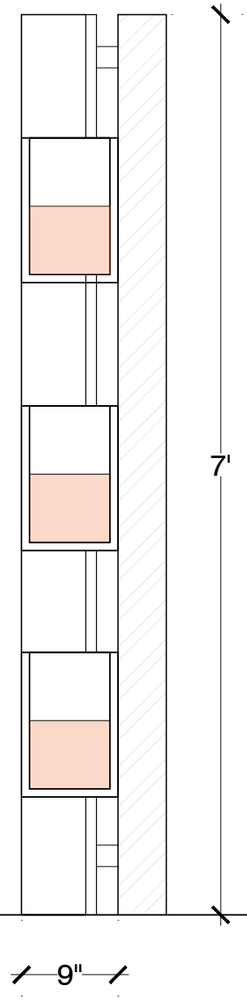

SECTION

GENERAL NOTES:

1. ALL DIMENSIONS ARE IN FEET AND INCHES.
2. ALL OPENING DIMENSIONS TO BE CHECKED AND VERIFIED AT SITE BEFORE FABRICATION OF CASEMENTS.
3. ALL LEVELS ARE IN FEET AND INCHES AND ARE FINISHED LEVELS OTHER THAN WHAT IS MENTIONED FOR OPEN TERRACES.
4. DO NOT SCALE DRAWINGS. ONLY WRITTEN DIMENSIONS SHALL BE FOLLOWED, ANY DISCREPANCIES NOTED SHALL BE BROUGHT TO THE NOTICE OF THE ARCHITECT PRIOR TO EXECUTION.
5. FOR DETAILS SUCH AS DOORS, WINDOWS, GRILLS, GATES, SKYLIGHT, TOILETS, STAIRCASES, HANDRAILS,RAILING, ETC. REFER RESPECTIVE ARCHITECTURAL DRAWINGS.
6. THESE DRAWINGS SHALL BE CORRELATED AND READ IN CONJUNCTION WITH RESPECTIVE CONSULTANT'S APPROVED DRAWINGS FOR STRUCTURAL MEMBERS, SERVICES SUCH AS PLUMBING,SANITARY,ELECTRICAL, AIR–CONDITIONING,VENTILATION, RAINWATER DRAINAGE & WATERPROOFING AND LANDSCAPING. ANY DISCREPANCIES NOTED SHALL BE BROUGHT TO THE NOTICE OF THE ARCHITECT PRIOR TO EXECUTION.
7. OPENING SIZES MENTIONED IN THE SCHEDULE ARE CLEAR OPENING SIZES AFTER PLASTERING.

NOTES

KARISHMA ARCHITEKTON

REYAN MARVEL - RESIDENCE INTERIOR

LANDSCAPE WALL DETAILS

MUON ARCHITECTURE

76, RAJAMMAL STREET,UDHAYA NAGAR ,
PORUR,CHENNAI - 600116
CONTACT - +91 9791141724
+91 8248673276
EMAIL : surendharan.ar@gmail.com

GOOD FOR CONSTRUCTION

REV	DRAWN BY	CHKD BY	DATE	SHEET
R0	SP	SP	08-03-2024	A3
DWG_NO	1116_2024_RM_INT_01			