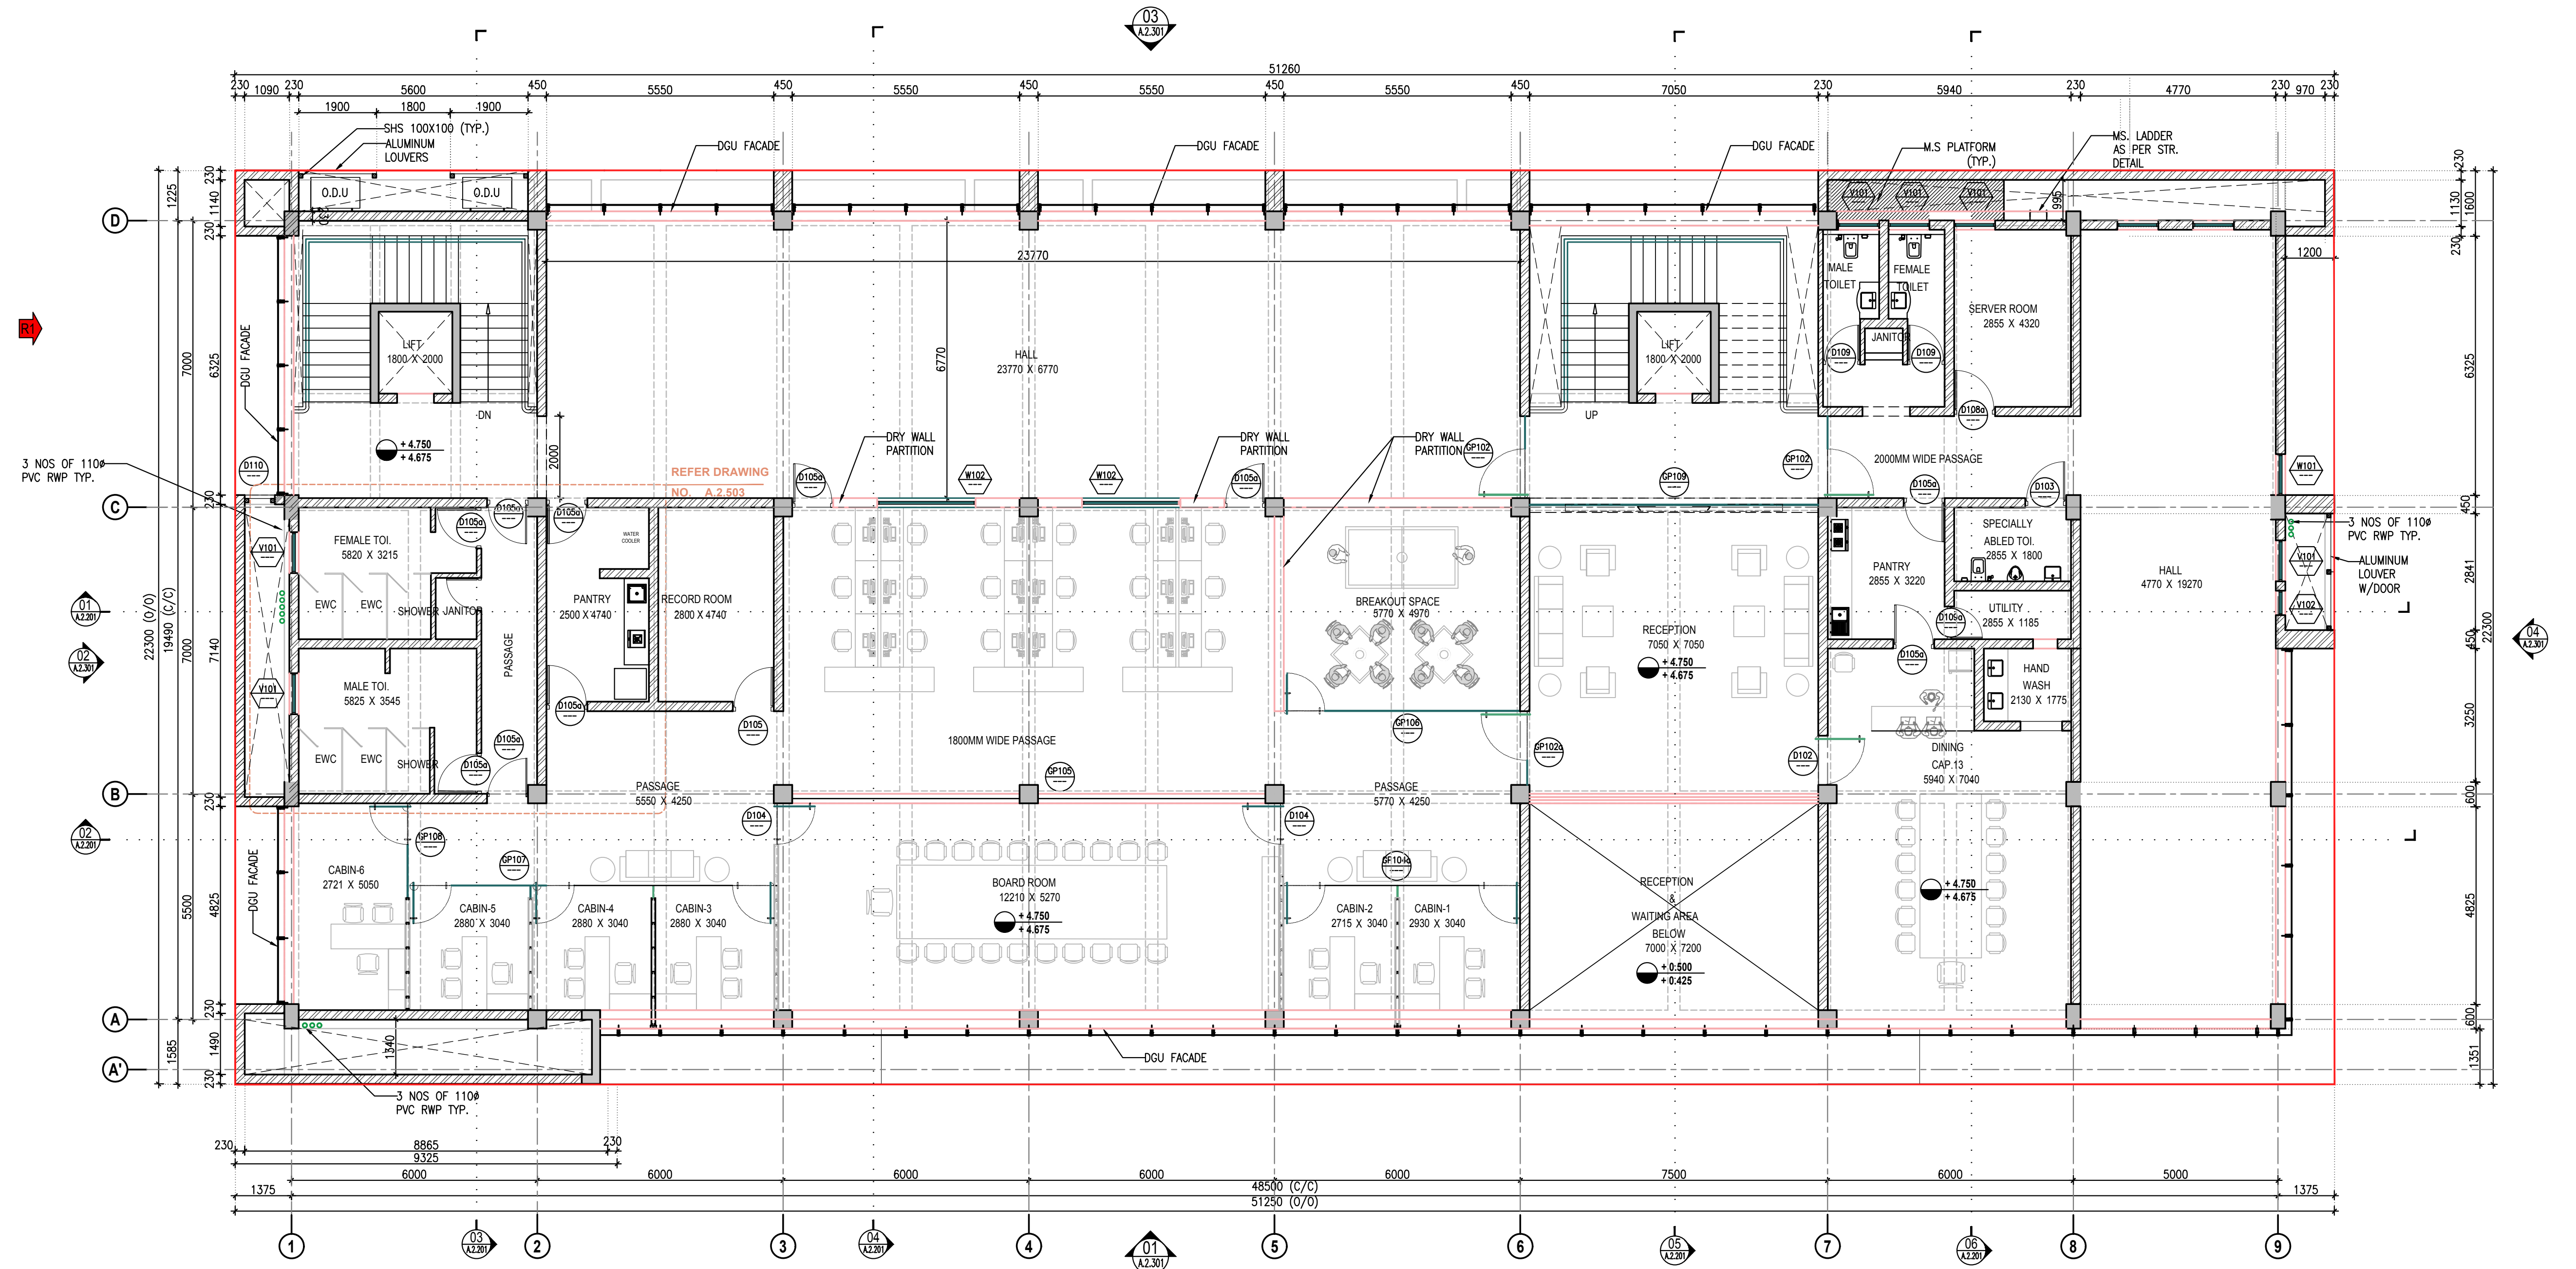

02 **FIRST FLOOR PLAN**
SCALE 1:100

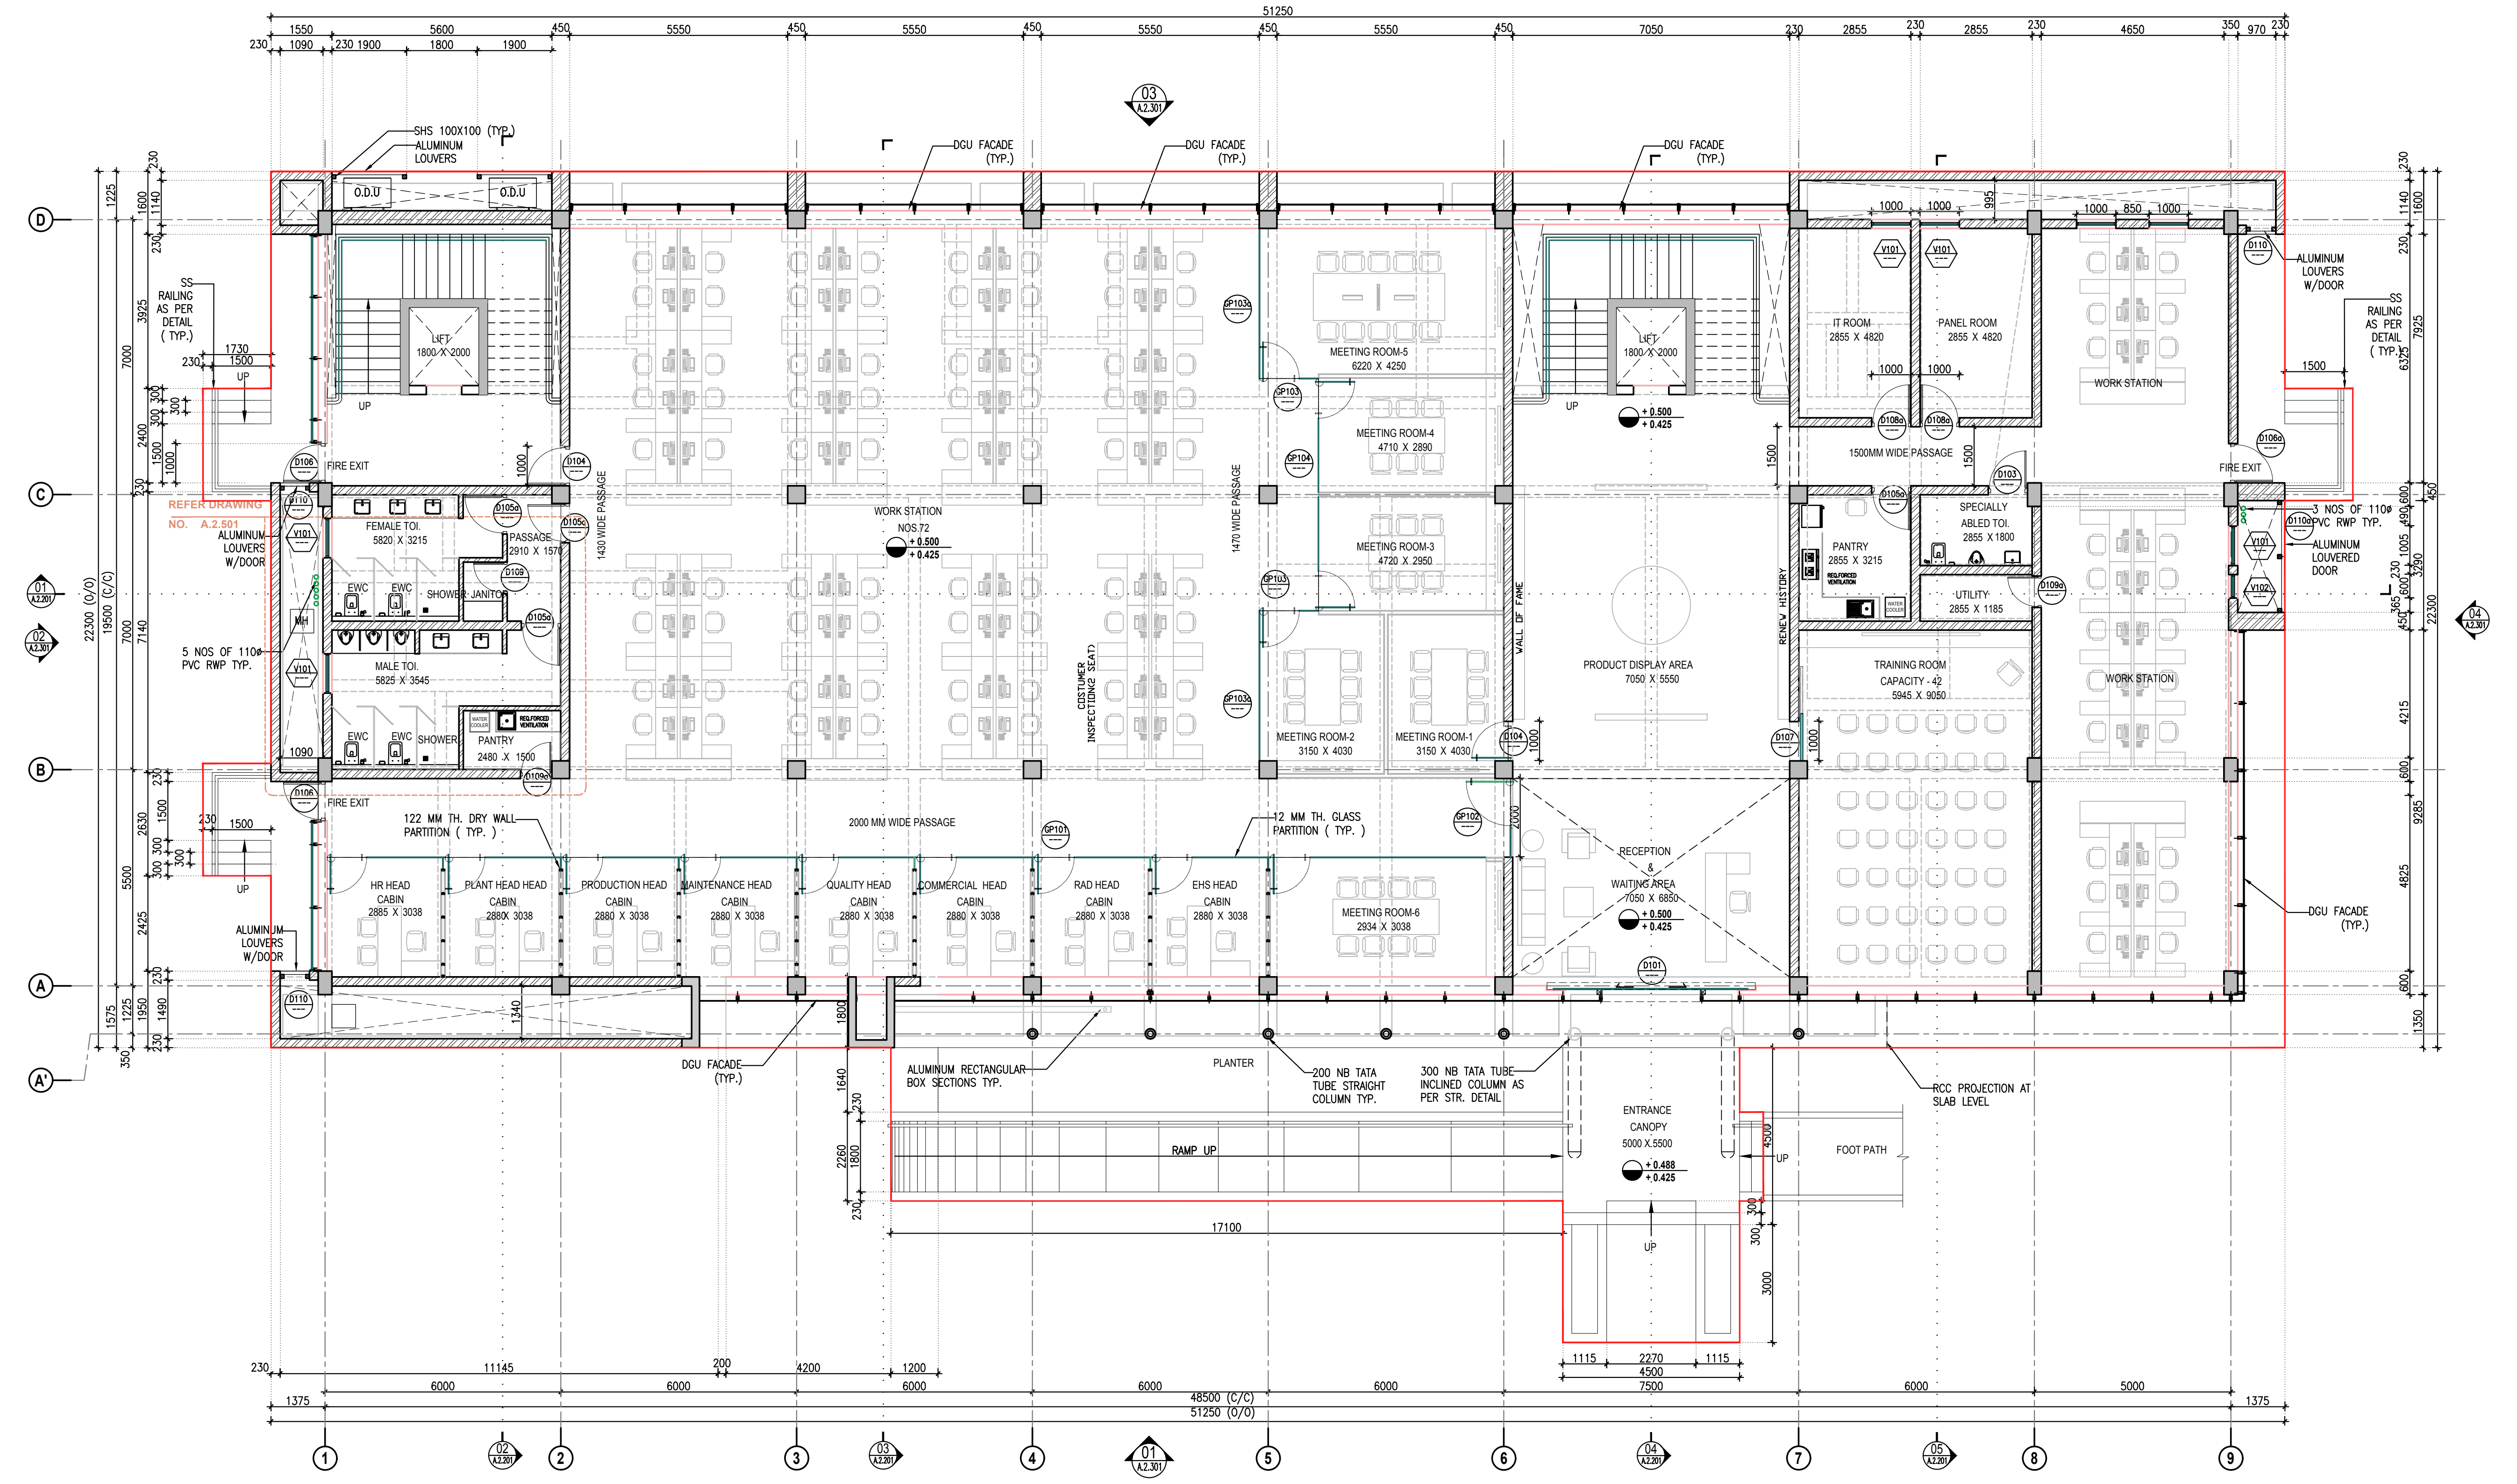
SHS 100X100 (TYP.)
ALUMINUM LOUVERS
DGU FACADE (TYP.)
SS RAILING AS PER DETAIL (TYP.)
FIRE EXIT
LIFT 1800 X 2000
REFER DRAWING NO. A.2.501
FEMALE TOI. 5820 X 3215
MALE TOI. 5825 X 3545
PASSAGE 2910 X 1570
PANTRY 2480 X 1500
5 NOS OF 110ø PVC RWP TYP.
1430 WIDE PASSAGE
WORK STATION NOS.72
COSTUMER INSPECTION(2 SEAT)
1470 WIDE PASSAGE
MEETING ROOM-5 6220 X 4250
MEETING ROOM-4 4710 X 2890
MEETING ROOM-3 4720 X 2950
MEETING ROOM-2 3150 X 4030
MEETING ROOM-1 3150 X 4030
2000 MM WIDE PASSAGE
122 MM TH. DRY WALL PARTITION (TYP.)
12 MM TH. GLASS PARTITION (TYP.)
HR HEAD CABIN 2885 X 3038
PLANT HEAD HEAD CABIN 2880 X 3038
PRODUCTION HEAD CABIN 2880 X 3038
MAINTENANCE HEAD CABIN 2880 X 3038
QUALITY HEAD CABIN 2880 X 3038
COMMERCIAL HEAD CABIN 2880 X 3038
RAD HEAD CABIN 2880 X 3038
EHS HEAD CABIN 2880 X 3038
MEETING ROOM-6 2934 X 3038
WALL OF FAME
PRODUCT DISPLAY AREA 7050 X 5550
RENEW HISTORY
RECEPTION & WAITING AREA 7050 X 6850
IT ROOM 2855 X 4820
PANEL ROOM 2855 X 4820
1500MM WIDE PASSAGE
PANTRY 2855 X 3215
SPECIALLY ABLED TOI. 2855 X 1800
UTILITY 2855 X 1185
TRAINING ROOM CAPACITY - 42 5945 X 9050
WORK STATION
ALUMINUM LOUVERED DOOR
3 NOS OF 110ø PVC RWP TYP.
ALUMINUM RECTANGULAR BOX SECTIONS TYP.
PLANTER
200 NB TATA TUBE STRAIGHT COLUMN TYP.
300 NB TATA TUBE INCLINED COLUMN AS PER STR. DETAIL
RCC PROJECTION AT SLAB LEVEL
RAMP UP
ENTRANCE CANOPY 5000 X 5500
FOOT PATH
UP
17100
48500 (C/C)
51250 (O/O)

01 **GROUND FLOOR PLAN**
SCALE 1:100

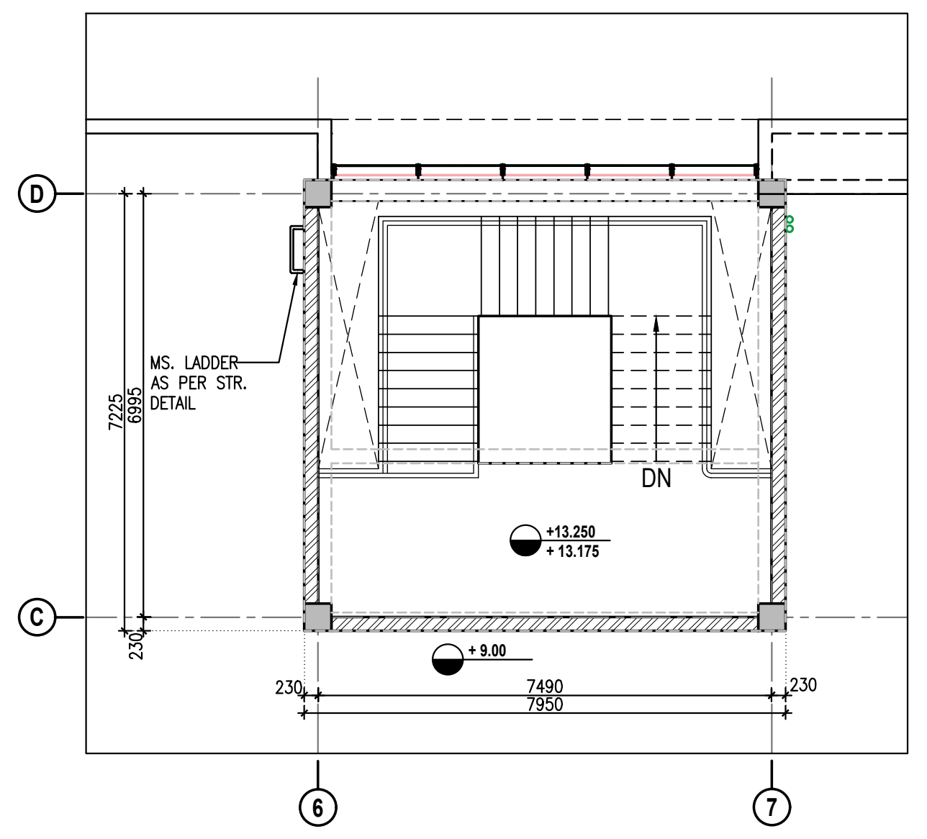

04 **STAIR CABIN PLAN**
SCALE 1:100

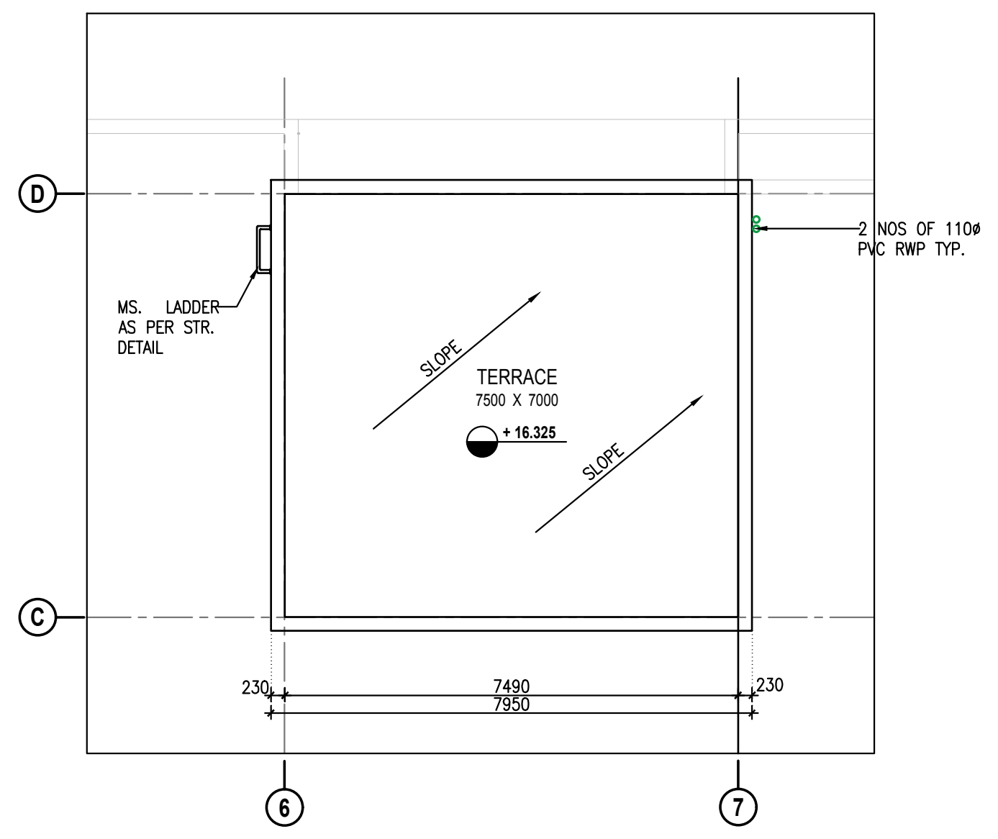

05 **STAIR CABIN TERRACE**
SCALE 1:100

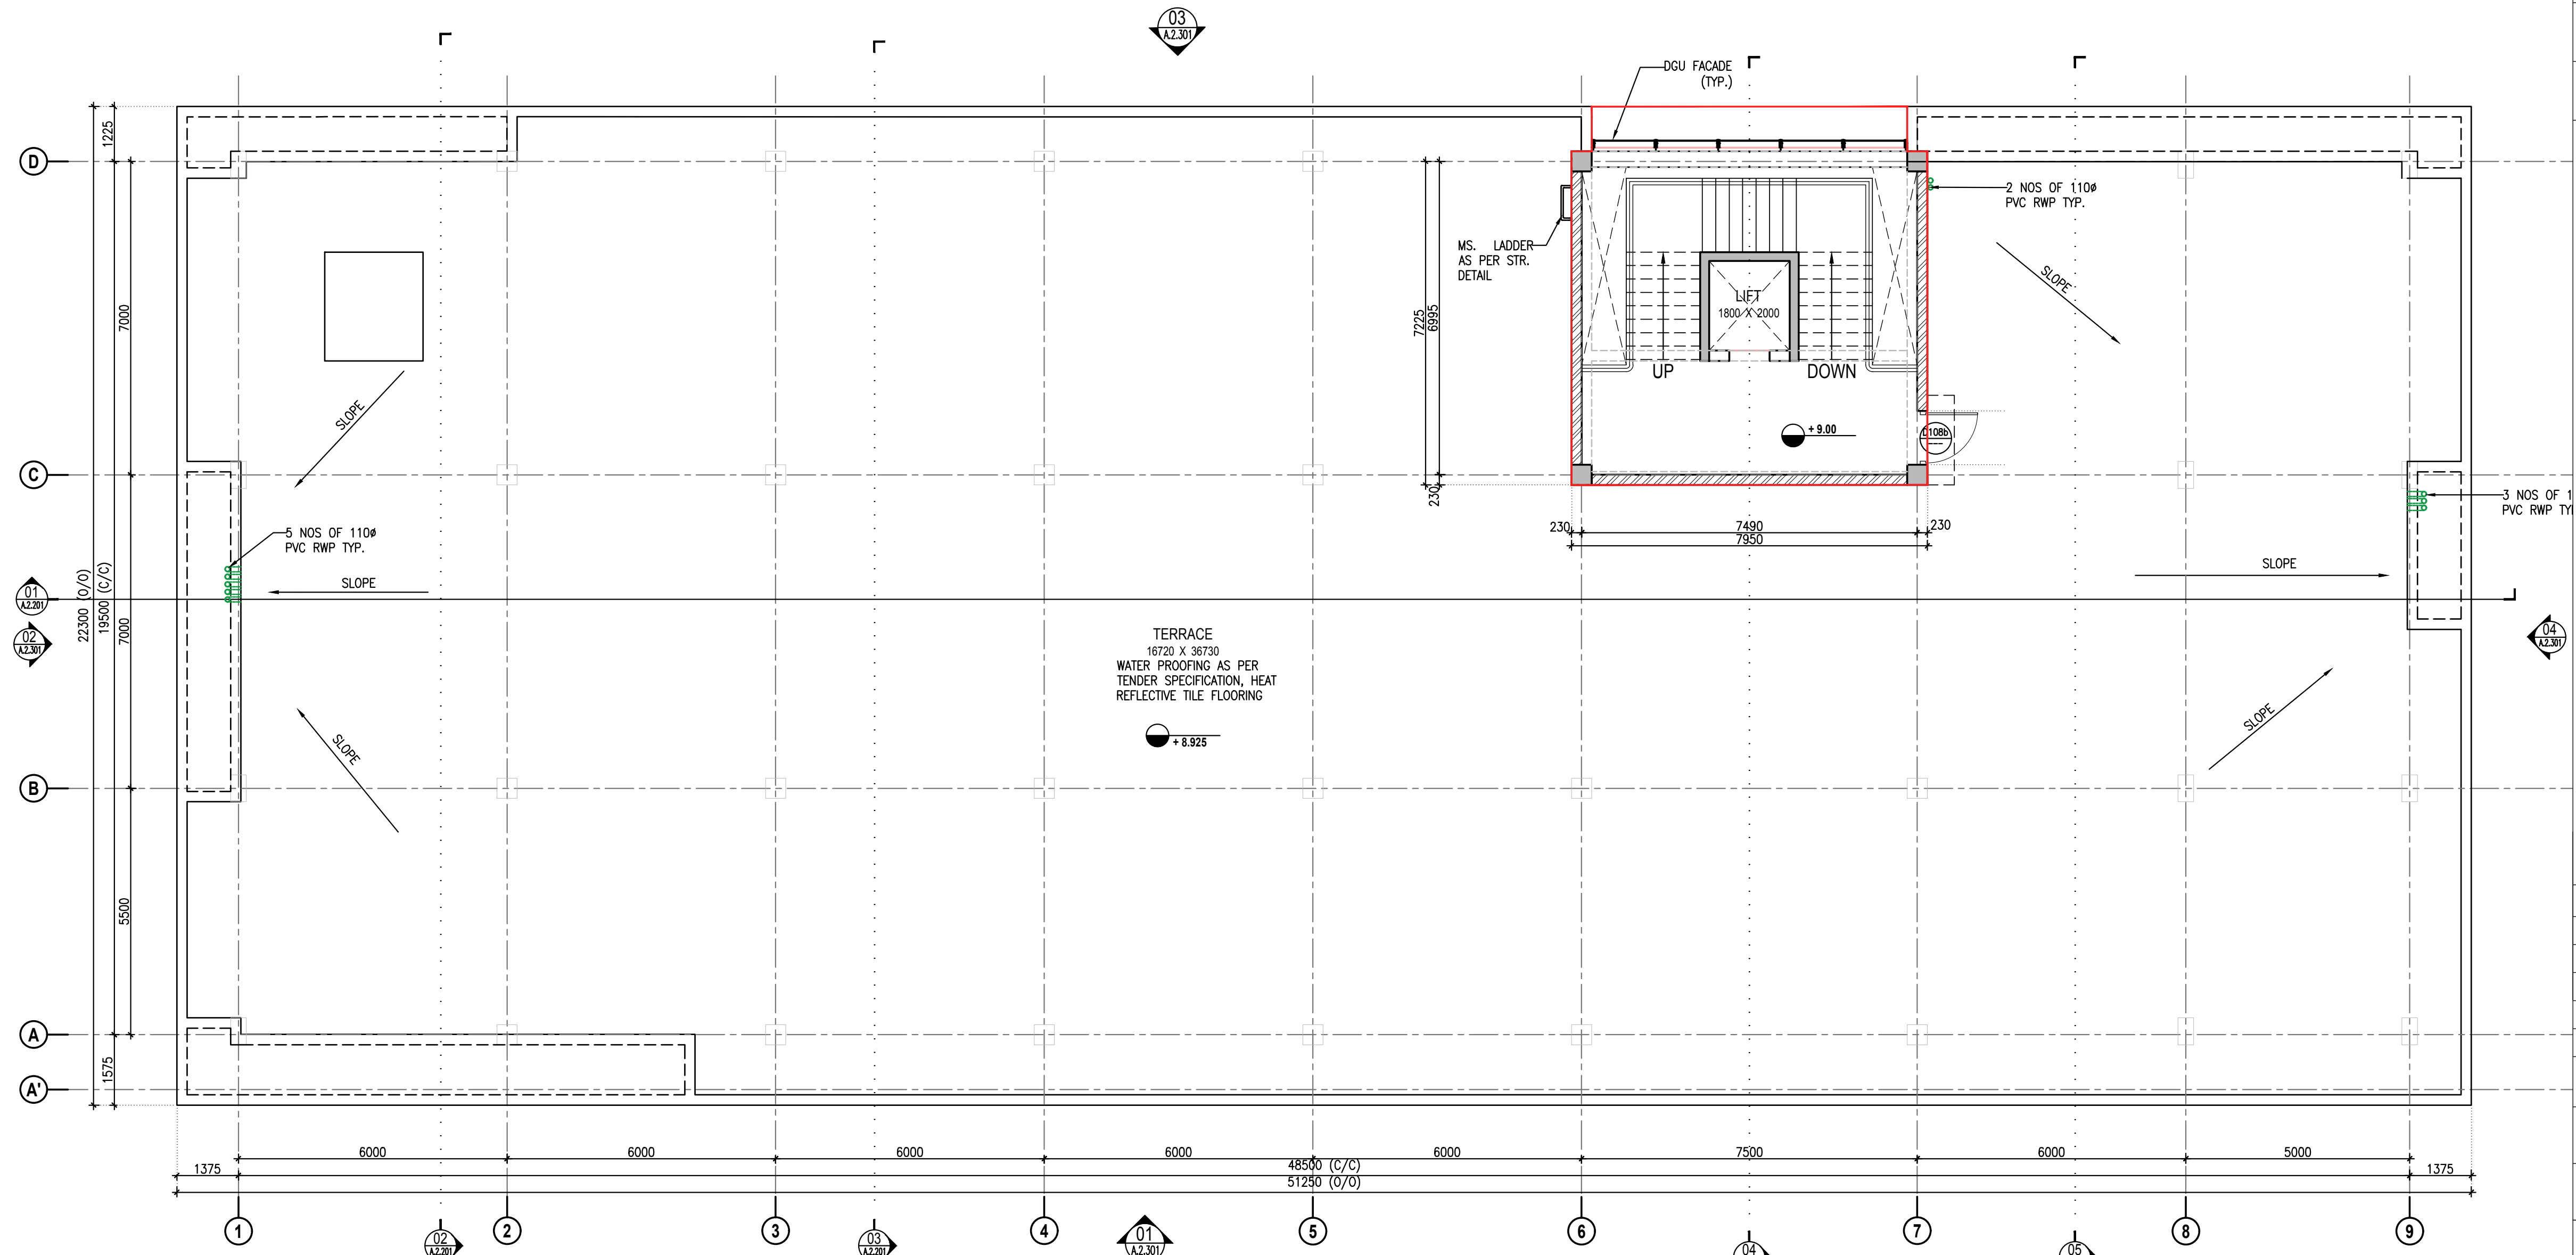
DGU FACADE (TYP.)
MS. LADDER AS PER STR. DETAIL
LIFT 1800 X 2000
UP
DOWN
+ 9.00
2 NOS OF 110ø PVC RWP TYP.
5 NOS OF 110ø PVC RWP TYP.
3 NOS OF 110ø PVC RWP TYP.
SLOPE
TERRACE 16720 X 36730 WATER PROOFING AS PER TENDER SPECIFICATION, HEAT REFLECTIVE TILE FLOORING
+ 8.925
48500 (C/C)
51250 (O/O)

03 **SECOND FLOOR PLAN**
SCALE 1:100

**SCHEDULE OF OPENINGS:**

| MKD. | SIZE | SILL HT. | LINTEL HT. | TOTAL NO. | REMARKS |
|---|---|---|---|---|---|
| D101 | 2500X2400 | ---- | 2400 | 1 | SLIDING GLASS DOOR WITH AUTOMATION |
| D102 | 1200X2100 | ---- | 2100 | 1 | GLASS DOOR WITH PATCH FITTING |
| D103 | 1200X2100 | ---- | 2100 | 2 | FLUSH DOOR WITH FROSTED VISION PANEL |
| D104 | 1000X2100 | ---- | 2100 | 4 | GLASS DOOR WITH PATCH FITTING |
| D105 | 1000X2100 | ---- | 2100 | 1 | FLUSH DOOR |
| D105a | 1000X2100 | ---- | 2100 | 14 | FLUSH DOOR WITH VISION PANEL |
| D106 | 1000X2100 | ---- | 2100 | 2 | FIRE EXIT GLAZED DOOR WITH PANIC BAR |
| D106a | 1000X2100 | ---- | 2100 | 1 | FIRE EXIT DOOR WITH PANIC BAR |
| D107 | 1000X2100 | ---- | 2100 | 1 | SLIDING WOODEN DOOR |
| D108 | 1000X2100 | ---- | 2100 | 1 | HMPS DOOR WITH VISION PANEL |
| D108a | 1000X2500 | ---- | 2500 | 3 | HMPS DOOR WITH VISION PANEL |
| D108b | 1000X2250 | ---- | 2250 | 1 | HMPS DOOR WITH VISION PANEL |
| D109 | 800X2100 | ---- | 2100 | 3 | FLUSH DOOR |
| D109a | 800X2100 | ---- | 2100 | 3 | FLUSH DOOR WITH VISION PANEL |
| D110 | 750X2100 | ---- | 2100 | 3 | ALUMINUM LOUVERS DOOR |
| D110a | 1000X2100 | ---- | 2100 | 1 | ALUMINUM LOUVERS DOOR |
| GP101 | 29965X3000 | ---- | ---- | 1 | ALUMINUM FRAME WITH GLASS PARTITION |
| GP102 | 2000X3000 | ---- | ---- | 3 | ALUMINUM FRAME WITH GLASS PARTITION |
| GP102a | 1800X3000 | ---- | ---- | 1 | ALUMINUM FRAME WITH GLASS PARTITION |
| GP103 | 1500X3000 | ---- | ---- | 2 | ALUMINUM FRAME WITH GLASS PARTITION |
| GP103a | 3825X3000 | ---- | ---- | 2 | ALUMINUM FRAME WITH GLASS PARTITION |
| GP104 | 5850X3000 | ---- | ---- | 1 | ALUMINUM FRAME WITH GLASS PARTITION |
| GP104a | 5775X3000 | ---- | ---- | 1 | ALUMINUM FRAME WITH GLASS PARTITION |
| GP105 | 11550X3000 | ---- | ---- | 1 | ALUMINUM FRAME WITH GLASS PARTITION |
| GP106 | 5780X3000 | ---- | ---- | 1 | ALUMINUM FRAME WITH GLASS PARTITION |
| GP107 | 8880X3000 | ---- | ---- | 1 | ALUMINUM FRAME WITH GLASS PARTITION |
| GP108 | 2300X3000 | ---- | ---- | 1 | ALUMINUM FRAME WITH GLASS PARTITION |
| GP109 | 7050X3000 | ---- | ---- | 1 | ALUMINUM FRAME WITH GLASS PARTITION+SLIDING DOOR |
| W101 | 1000X1800 | 4250 | 6350 | 1 | WINDOW |
| W102 | 2400X1200 | 5150 | 6350 | 2 | WINDOW |
| V101 | 1000X600 | 1500/5750 | 2100/6350 | 11 | VENTILATION |
| V102 | 600X600 | 1500/5750 | 2100/6350 | 2 | VENTILATION |

THIS DRAWING & DESIGN IS THE SOLE PROPERTY OF VMS & SHALL NOT BE COPIED,
TRACED OR REPRODUCED BY ANY MEANS WITHOUT PRIOR WRITTEN CONSENT OF THE FIRM.

**GENERAL NOTES :**

1. ALL THE DIMENSIONS ARE UNFINISHED DIMENSIONS.
2. ALL DIMENSIONS ARE IN MM AND LEVELS ARE IN MT, UNLESS OTHERWISE MENTIONED.
3. ALL THE DIMENSIONS SHALL BE READ & NOT TO BE MEASURED.
4. IN CASE OF ANY DISCREPANCY, BRING IT TO THE NOTICE OF THE ARCHITECT IMMEDIATELY.
5. DETAIL DRAWING PRECEDES THE GENERAL DRAWING

**STANDARD DRAWING SYMBOLS:**

+ FINISHED LEVEL
+ UNFINISHED LEVEL

01 --- SECTION SYMBOL
UPPER HALF INDICATES DIAGRAM NO. (NUMERICAL VALUE) IN DRAWING SHEET & LOWER HALF INDICATES DRAWING NO.

04 --- ELEVATION SYMBOL
UPPER HALF INDICATES DIAGRAM NO. IN DRAWING SHEET & LOWER HALF INDICATES DRAWING NO.

W100 A000 WINDOW SYMBOL
UPPER HALF INDICATES WINDOW NO. & LOWER HALF INDICATES DRAWING NO.

D100 A000 DOOR SYMBOL
UPPER HALF INDICATES DOOR NO. & LOWER HALF INDICATES DRAWING NO.

**GRAPHIC LEGEND :**

| | |
|---|---|
| ▨ | 230THK. FLY ASH BRICK WALL |
| ▩ | 115THK. FLY ASH BRICK WALL 2.1MT. HT. |
| ■ | RCC COLUMN CUT IN PLAN. |

**NOTE : FOR CIVIL CONTRACTORS**

FOR TENDER

| NO. | DATE | DESCRIPTION | DRAWN BY | CHECKED BY |
|---|---|---|---|---|
| | | | | |
| | | | | |
| | | | | |

**REVISION HISTORY**

KEY PLAN
SCALE : N.T.S.

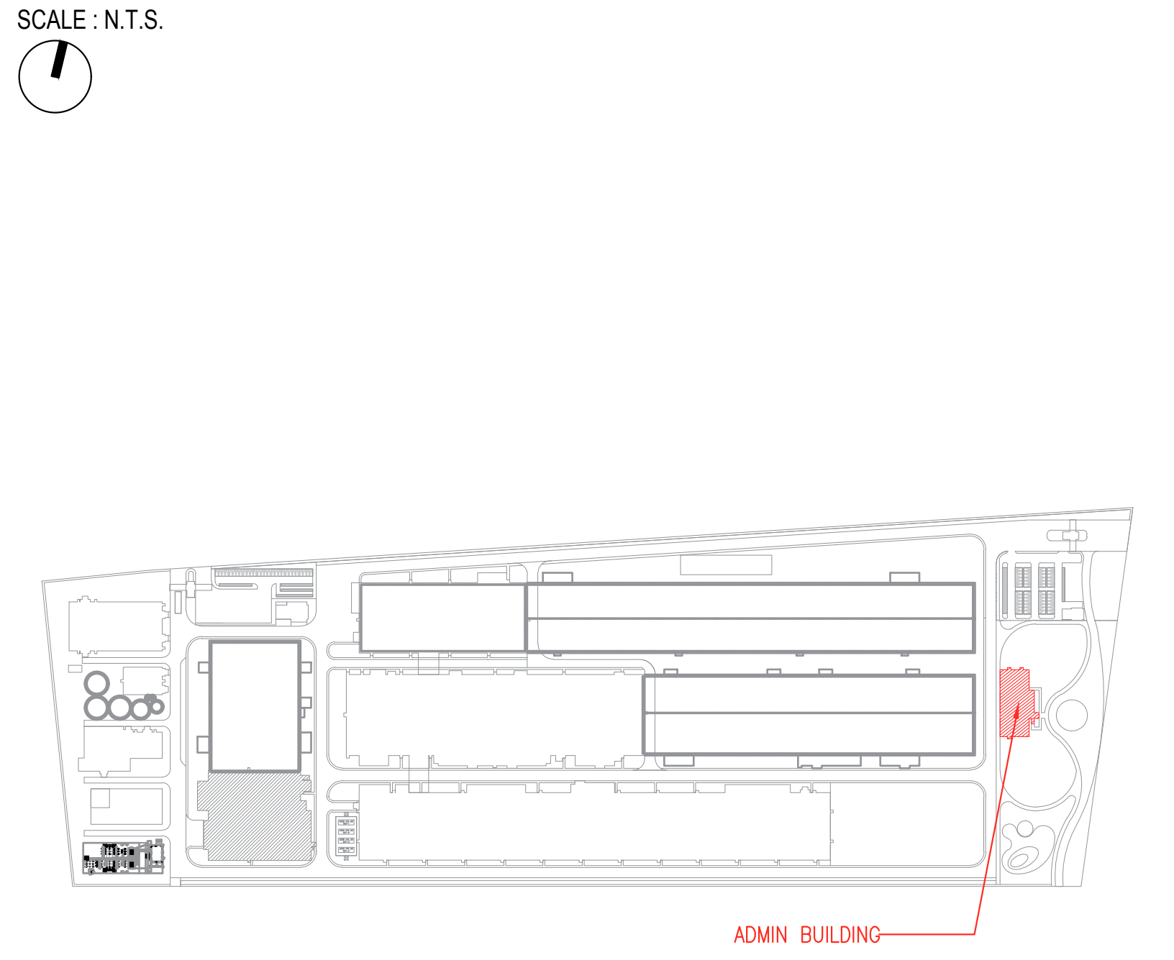

**REFERENCE DRAWINGS :**

01. ARCHITECTURAL : A.5.101, A.5.201, A.5.301
02. STRUCTURAL :
03. HVAC : -
04. ELECTRICAL : -
05. UTILITIES : -

# FLOOR PLANS

# ADMIN BUILDING

# AGRAWAL METAL WORKS(P) LTD.

| PROJECT NO. | SCALE : | DRAWN : | NAMRATA |
|---|---|---|---|
| 3824 | AS NOTED | CHECKED: | DARSH |
| | DATE : | APPROVED: | DARSH |
| | 03-12-2024 | COORDINATION CHECKED: | DARSH |

ENGINEERING + ARCHITECTURE
**VMS ENGINEERING & DESIGN SERVICES (P) LTD.**
CHITRAKOOT FLATS, B/H TIMES OF INDIA, OFF ASHRAM ROAD,
AHMEDABAD-380 009. PHONE: +91 (079) 2658-8829, 4023-6236
WWW.VMSCONSULTANTS.COM

| SHEET SIZE | DRAWING NO. | TENDER | REVISION: |
|---|---|---|---|
| 600x 1200 | T.A.5.101 | T | R0 |