


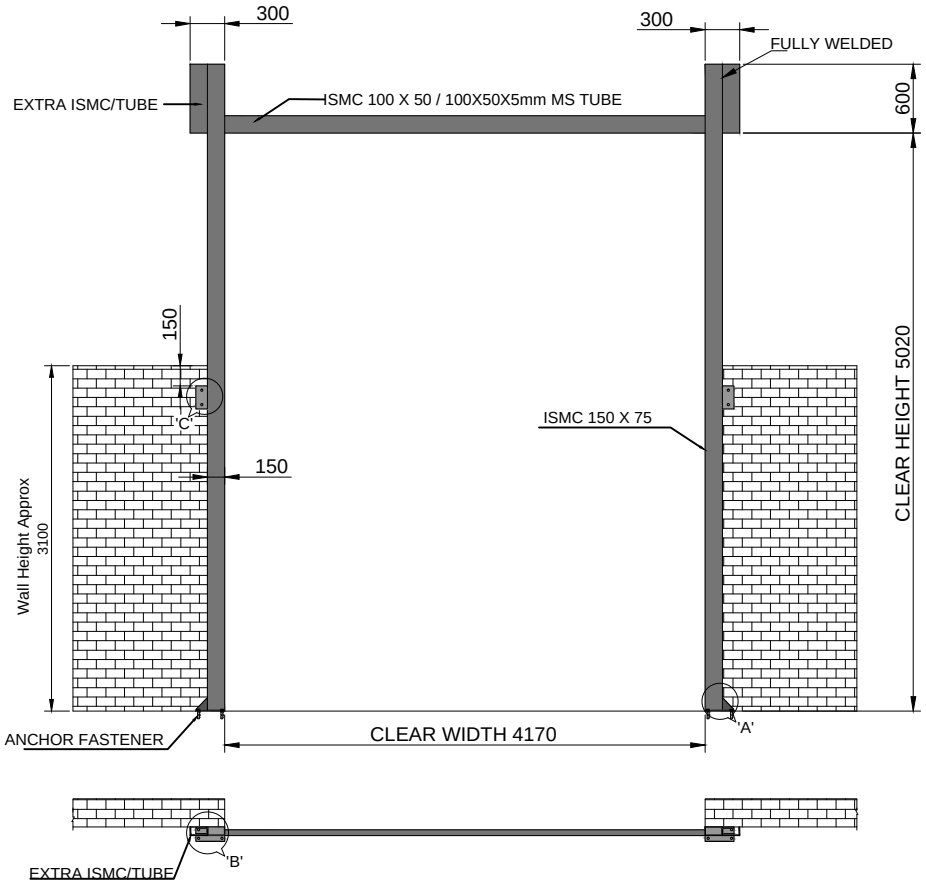


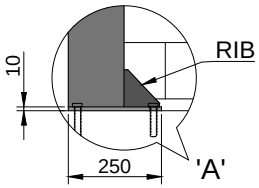

DETAIL VIEW 'A'.

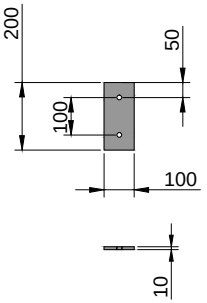

DETAIL VIEW 'C'.

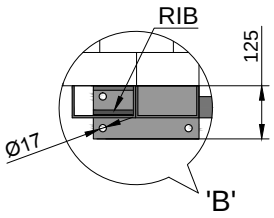

DETAIL VIEW 'B'.

1. ISMC 150 X 75 X 12.45 MTR = 204.18 KGS
2. ISMC 100 X 50 X 4.17 MTR = 38.36 KGS

TOTAL WEIGHT = 242.54 KGS

CLEAR WIDTH	CLEAR HEIGHT	QUANTITY
4170	5020	02

TOLERANCE - ±10mm & 15 kgs

NOTE :
1. MATERIAL FOR ALL STRUCTURE = M.S

SURAJ		R01	28/07/2018.	1.Structure Detail Added.
DRAWN NAME	SIGN	REVISION	DATE	REVISION DETAILS

This drawing & design is the property of NIHVA TECHNOLOGIES. Not to be sold or copied to any other concern.

TITLE
STRUCTURE FOR GEAR OPERATED ROLLING SHUTTER

NIHVA
NIHVA TECHNOLOGIES PVT. LTD.

NIHVA TECHNOLOGIES PVT. LTD. PUNE
Tel : 020 66304033
Email:- info@nihva.com
Website:- www.nihva.com

	NAME	SIGN	DATE
DRAWN	PRADEEP		12-07-2018
CHECK	PRADEEP		12-07-2018
APPRD.	R.D		12-07-2018

CLIENT - SYNERGY
PROJECT-EMBASSY INDUSTRIAL PARKS PVT. LTD.
SITE LOCATION - CHAKAN
If any queries contact : design@nihva.com
DWG. NO. : NIHVA/17-18/0082/R01 | REV- 01
ALL DIMENSION ARE IN mm | SCALE: NTS | WT: | SHEET: 01 OF 01