


Revision		Date	By
A	CW was 9000, CH was 5400	2021-09-27	KMÖ
B	Side fastening was with side jamb	2021-11-11	KMÖ

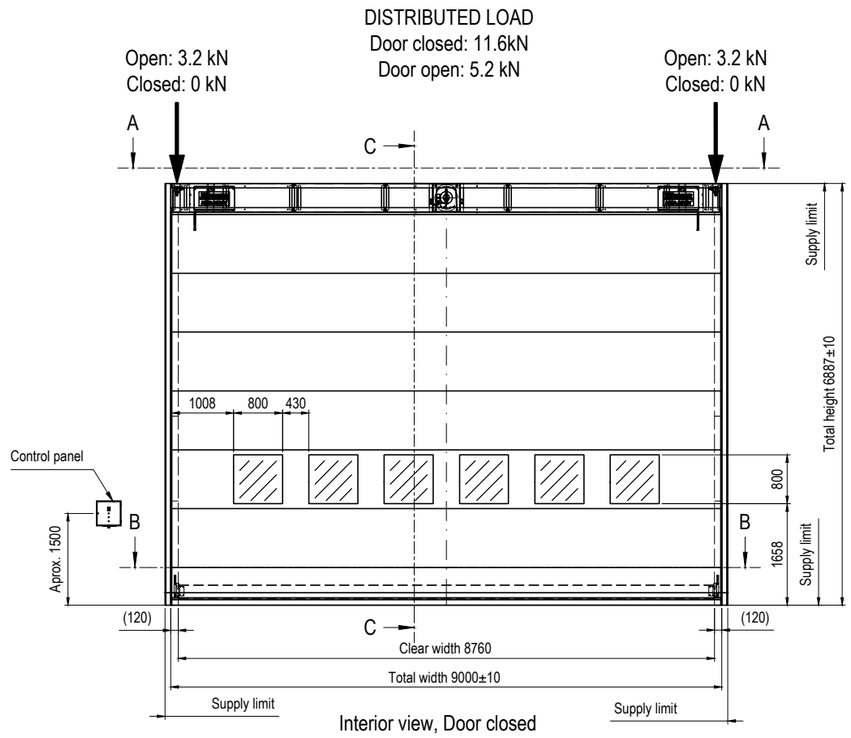


Interior view, Door closed

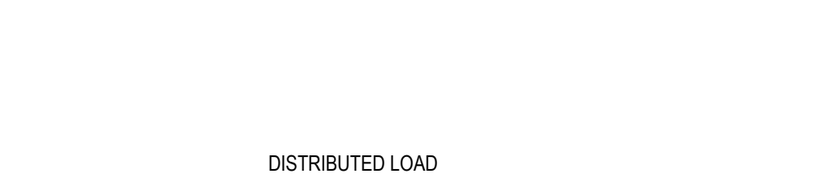


SECTION A-A
Scale 1:50

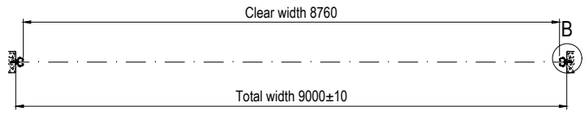


SECTION B-B
Door leaf is not shown for clarification
Scale 1:50

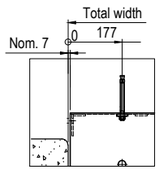


DETAIL C, SCALE (1:10)

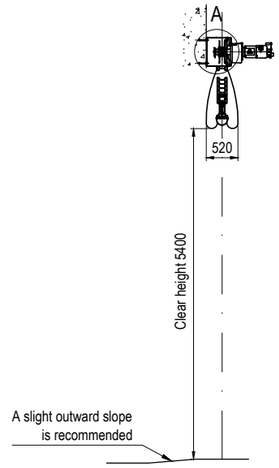


SECTION C-C
Open door
Scale 1:50

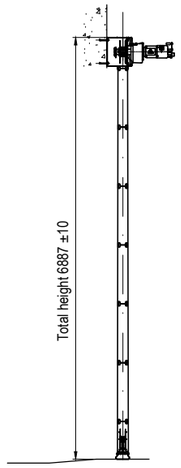


SECTION C-C
Closed door
Scale 1:50

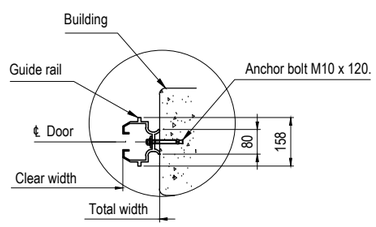


DETAIL B, SCALE (1:10)

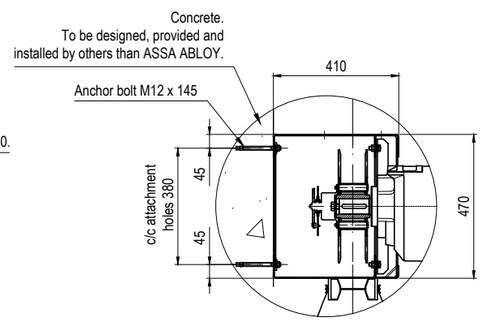

DETAIL A, SCALE (1:10)

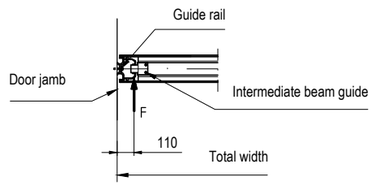

Force by differential pressure
transferred to guide rail at
each intermediate position.
F=4.7 kN

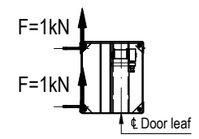

Load on header box attachment
(each screw), due to wind load
and door weight

NOT INCLUDED IN DOOR SUPPLY:

1. Design and supply of all door supporting structural components.
2. Design and supply of all closure between door and adjacent steel.
3. Door jambs adjustable for overall door width and true to plumb.
4. Paint job after completed door installation.
5. Any frameworks being provided by ASSA ABLOY will be clearly indicated as "by ASSA ABLOY".

REQUIREMENTS ON BUILDING:

6. Door head support must be straight within 1/600 of span in the in/out direction and free from protrusions of any kind.
7. For a single door leaf, door head support should be horizontal and straight within 1/600 of span at distributed full door load.
8. Door side jambs must be smooth, straight and parallel, out of plumb must not exceed 2mm/m (total deviation at full length 5 mm) in any direction.
9. Any footings at bottom of jamb columns must not interfere with installation of guide rails at floor level.
10. At time of installation, finished floor, free from obstructions, out to a distance of 2 m on each side of door centreline must be available.
11. Header box must be accessible from both sides during installation.

DOOR PROPERTIES:

12. The door is designed to withstand a differential pressure of 1.15kPa.
15. Guide rails, top- and intermediate beams in extruded aluminium with natural finish.
16. Color of header box: BLACK (NCS 9000-N. RAL 9005)
15. Color of door fabric: Color of door fabric: GREY (NCS 3500, RAL 7004)
16. Metal trim: motor side

ELECTRICAL:

17. One main control panel provided of PLC type.
18. Audible and visual alarm
19. Back-up power switch
20. Safety edge
21. Approx. size of main control panel: WxHxD (500mm x 600mmx250 mm),
22. Power: 2.7kW
23. Nom. current: 6.4A
24. (max. allowed voltage drop at start: 5%)

BELT HOIST UNITS:
SK 873.1-100L/4 Z dual brake

Building: ARFF4

DESIGNED: KMÖ	SIZE: A1	SCALE: 1:50	Delhi Fire Station
CODE: 22238-22239	If not otherwise stated:		India
ITEM NO:	Tolerances: ISO 2768-m EN ISO 13920-B		Megadoor 8760 x 5400
DATE: 2021-07-22	Cutting class: ISO 9013-442		Sales interface
ASSA ABLOY	Weld class: ISO 5817-C	DRAWING NO: 74147	REVISION: B
	Surface finish: Smooth raw surface		PLOT DATE

This document is the property of ASSA ABLOY Entrance Systems AB and shall not be reproduced or otherwise disclosed to a third party or used for any other unauthorized purpose.