

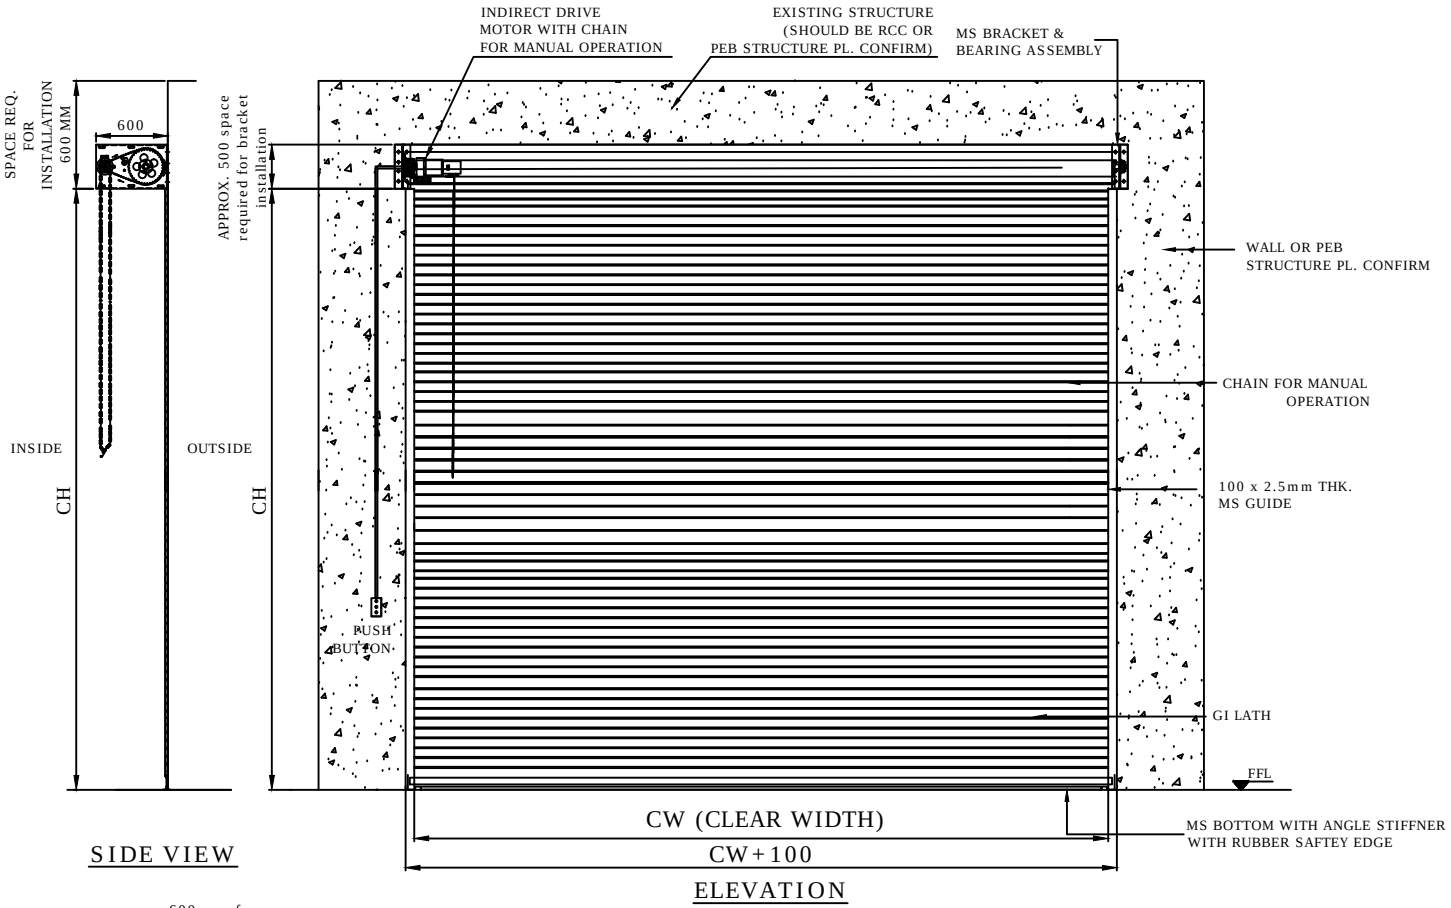



SIDE VIEW

ELEVATION

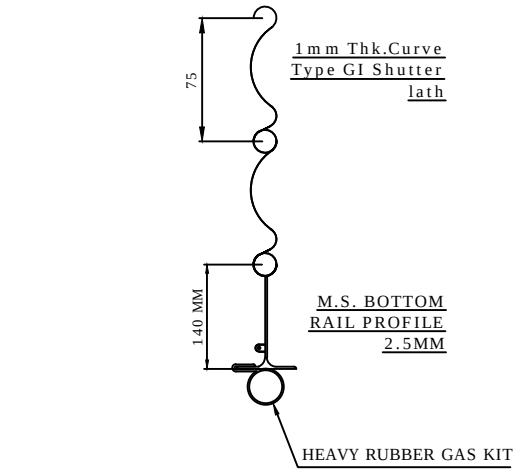

M.S. BOTTOM RAIL PROFILE 2.5MM

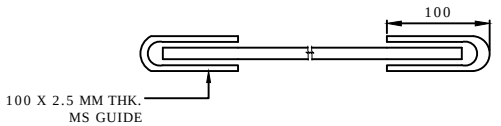

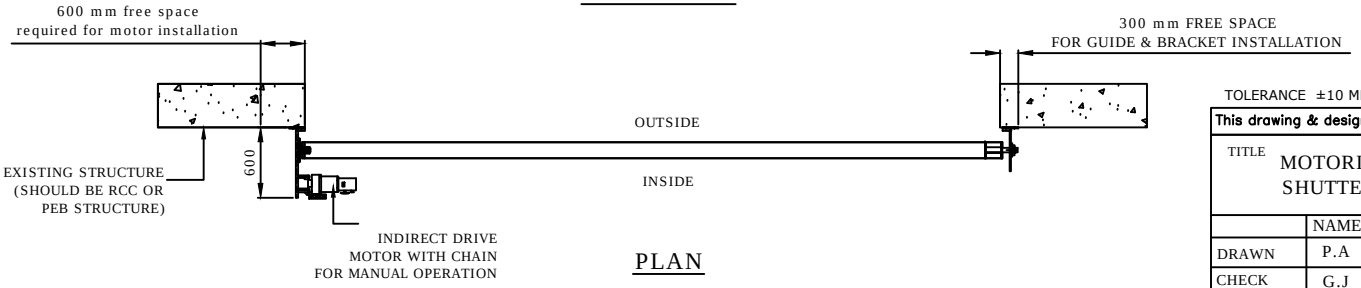

PLAN

CLEAR WIDTH (CW)	CLEAR HEIGHT (CH)	QUANTITY
4000	3150	1 NO

REV NO	DATE	DRAWN	REMARK
R01	19.12.19	P.A	1. CLEAR HEIGHT CHANGE

TOLERANCE ±10 MM

This drawing & designing is the property of NIHVA TECHNOLOGIES. Not to be sold or copied to any other concern.

TITLE: MOTORIZED ROLLING SHUTTER

	NAME		DATE
DRAWN	P.A		22.11.19
CHECK	G.J		22.11.19
REV.			
APPROVAL			

If any queries contact : projects@nihva.com

ALL DIMENSION ARE IN mm

NIHVA TECHNOLOGIES PVT. LTD.
NIHVA TECHNOLOGIES PVT. LTD. PUNE
Tel : 020 66304033
Email:- info@nihva.com
Website:- www.nihva.com

CLIENT - BSA

PROJECT -

SITE LOCATION - CHAKAN

DWG. NO. : NIHVA/19-20/0159/R01 | REV : R01

SCALE: NTS | WT: | SHEET: 01 OF 01