
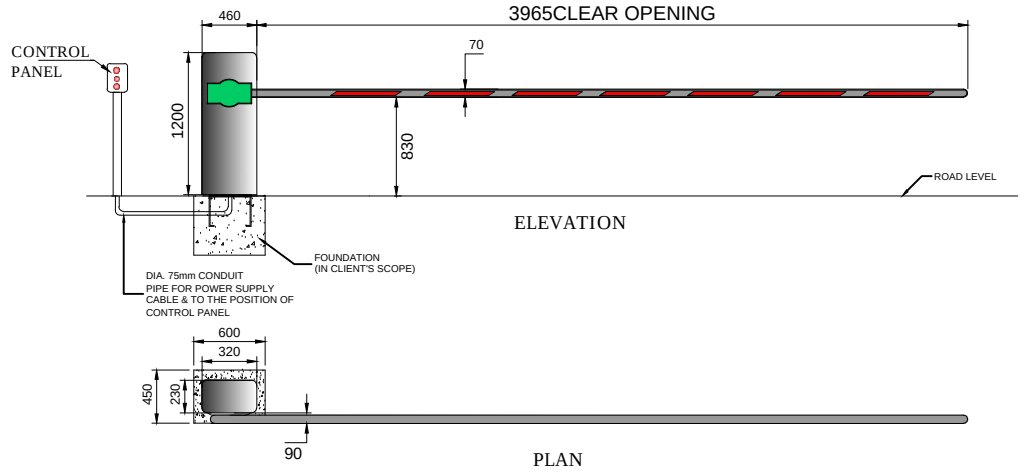


LOCATION - SEZ -4
FOUNDATION PLATE SIZE- 320X230
REFER FOUNDATION PLATE ASSEMBLY 2 PDF

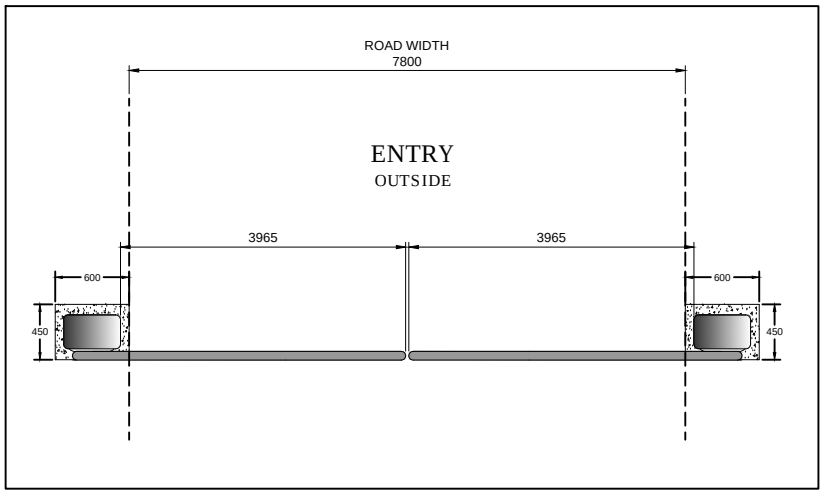

REV NO	DATE	DRAWN	REMARK
R04	25.12.20	S.M.S.	PLATE DIMENSION CHANGED
R03	03.07.20	P.A	1. ROAD WIDTH CHANGE.
R02	09.06.20	P.A	1. QTY CHANGE
R01	09.06.20	P.A	1. DIMENSION CHANGE

TOLERANCE - ±10mm

This drawing & design is the property of NIHVA TECHNOLOGIES. Not to be sold or copied to any other concern.

TITLE
BOOM BARRIER

NIHVA
NIHVA TECHNOLOGIES PVT. LTD.

NIHVA TECHNOLOGIES
PVT. LTD. PUNE
Tel : 020 66304033
Email:- info@nihva.com
Website:- www.nihva.com

	NAME	SIGN	DATE
DRAWN	P.A		14.04.2020
CHECK	G.J		14.04.2020
APPROVAL			

CLIENT - SERUM BIO-PHARMA PARK
PROJECT -
SITE LOCATION - HADPSAR, PUNE
DWG. NO. : NIHVA/20-21/0003/R04 REV-R04
If any queries contact : projects@nihva.com
SCALE: NTS WT: SHEET: 01 OF 01
ALL DIMENSION ARE IN mm