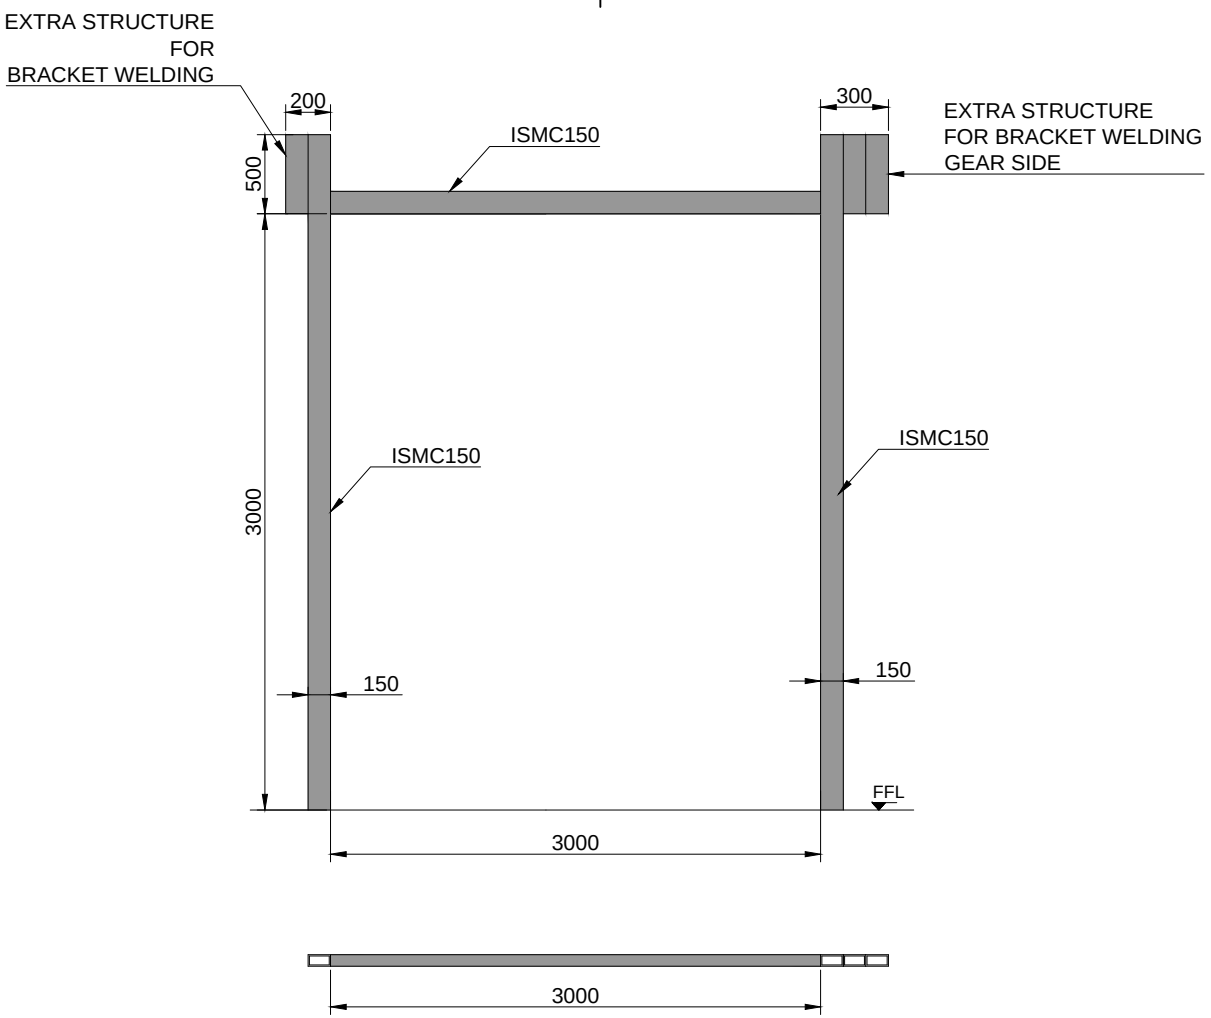



| S.N. | LOCATION | SIZE | QUANTITY |
|---|---|---|---|
| 1 | PUMP ROOM | 3000(W)X3000(H) | 1 |

NOTE-
1. ALL CIVIL WORK WILL BE CLIENT'S SCOPE.
2.STRUCTURE REQUIRED FOR SHUTTER IS IN CLIENT'S SCOPE.

TOLERANCE - ±10mm

This drawing & design is the property of NIHVA TECHNOLOGIES. Not to be sold or copied to any other concern.

TITLE: STRUCTURE FOR GEAR OPERATED ROLLING SHUTTER 3mX3m

NIHVA TECHNOLOGIES PVT. LTD.
NIHVA TECHNOLOGIES PVT. LTD. PUNE
Tel : 020 66304033
Website:- www.nihva.com
Email:- info@nihva.com

| | NAME | SIGN | DATE |
|---|---|---|---|
| DRAWN | SURAJ | | 05-10-2018 |
| CHECK | PRADEEP | | 05-10-2018 |
| APPRD. | R.D | | 05-10-2018 |

CLIENT -SCON PROJECTS PVT LTD.
PROJECT -ENZENE BIOSCIENCES LTD.
SITE LOCATION -CHAKAN
If any queries contact : design@nihva.com
DWG. NO. : NIHVA/18-19/0138
REV- 0
ALL DIMENSION ARE IN mm
SCALE: NTS
WT:
SHEET: 01 OF 01