

Abbrevation's:
WOW-Wall Opening Width
WOH-Wall Opening Height
UC-Under Cut
FFL-Finished Floor Level

ASSESORIES DETALES

(A) HINGES: SS Ball bearing butt hinges size 100x75x3mm

(B) LOCK : Mortise latch with double cylinder with Escutcheon.


(C) DOOR CLOSER : F8500

(D) VISION PANEL : 5 mm THK. VISION GLASS OF SIZE 200(W) X 300(H)mm

(E) LEVER HANDLE (BOTH SIDE)

Shutter thickness : 47 mm
Frame Sheet thick : 1.20mm
Shutter sheet thick : 0.80mm
Fixing : On Solid Brick plastered wall with Anchors


NOTE:- *All Dimensions are in mm.
*Tolerance:-All Linear Dimensions ±3mm,Others ±0.5mm.
*The Drawing Is For Location of Hardware only. Drawing Does Not Represent The Hardware For More Clarity, Please Go Through Hardware Broucher.

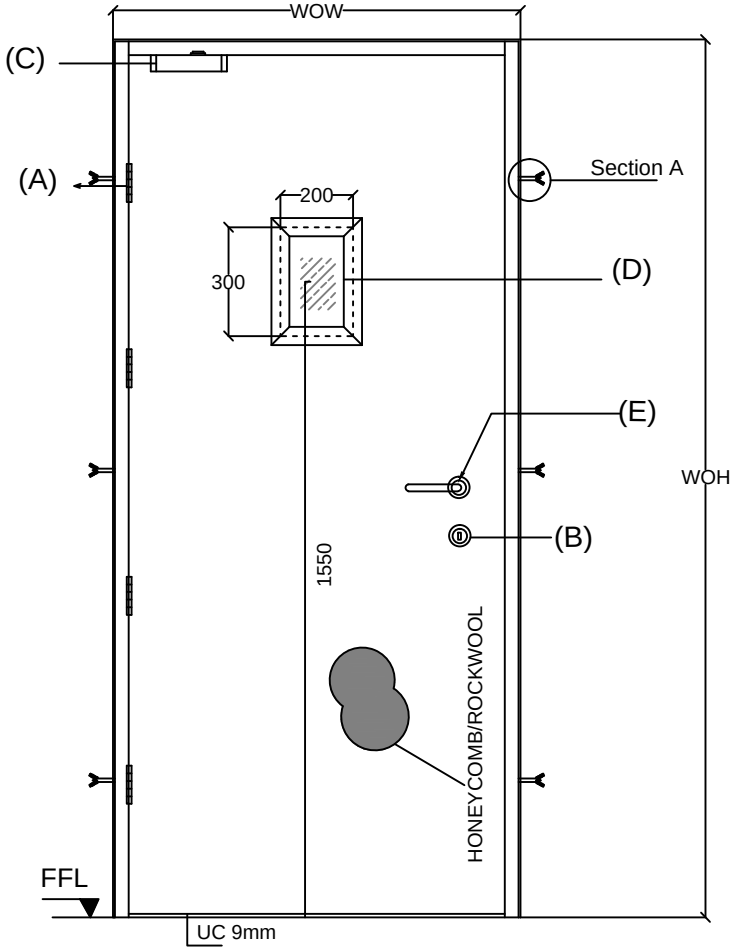

OUTSIDE ELEVATION



TOP VIEW

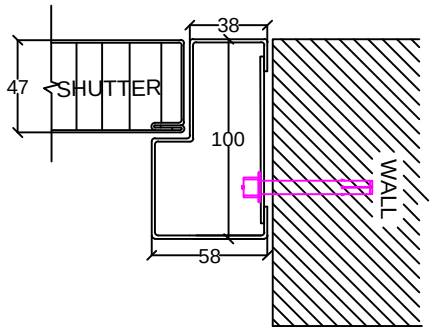

Detail view of Section A

FIRE RATED STEEL DOOR					
SR. NO.	WOW	WOH	TYPE 3	QUANTITY	LOCATION
1	1030	2080	1	1	PUMP ROOM

COLOR- RAL 9006(White Aluminum)

This drawing & design is the property of NIHVA TECHNOLOGIES. Not be sold or copy to any other concern.

FIRE RATED STEEL DOOR (SINGLE LEAF)

CLIENT APPROVAL

ALL DIMENSION ARE IN mm

	NAME	DATE	SIGN.
DRAWN BY	OMKAR	25/04/17	
CHECK BY	SAGAR P.	25/04/17	
REV.			
APPROVED BY			
MFG			

NIHVA TECHNOLOGIES PVT. LTD.
NIHVA TECHNOLOGIES PVT. LTD. PUNE
Tel : 020 66304033
Email:- info@nihva.com
Website:-www.nihva.com

CLIENT -
PROJECT -
SITE -
DWG. NO. - NIHVA/17-18/VDR/0018
SCALE: NTS | WT: | SHEET: 01 OF 01
If any queries contact : projects@nihva.com