


PLANS

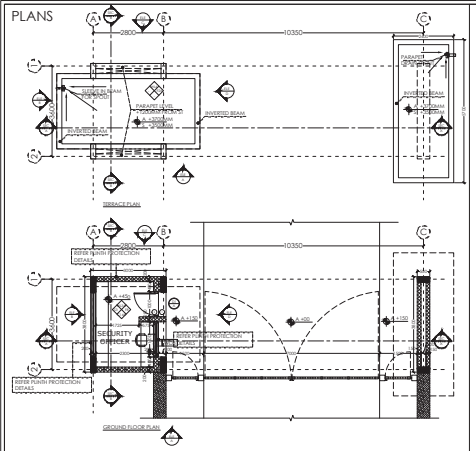


RCP & ARE

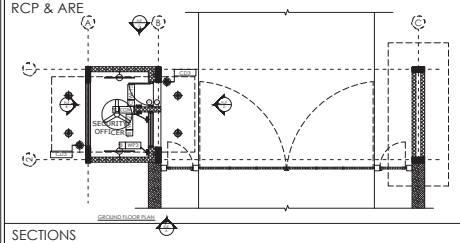


MS GRILL GATE DETAIL

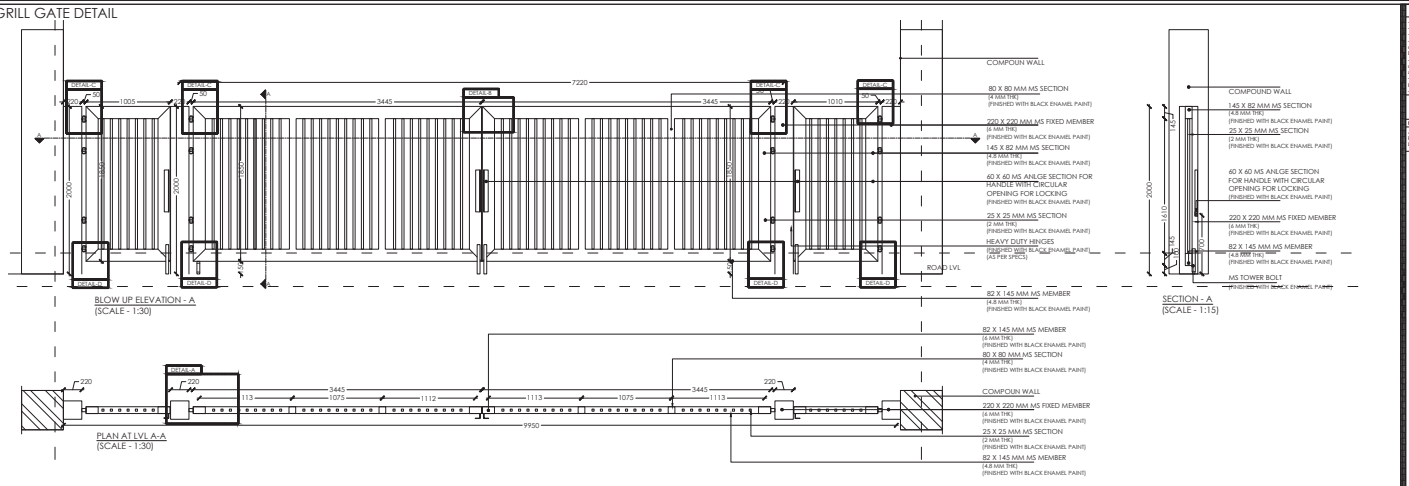


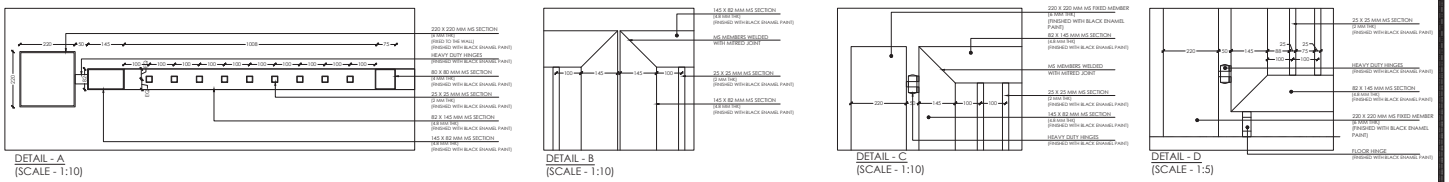


SECTIONS

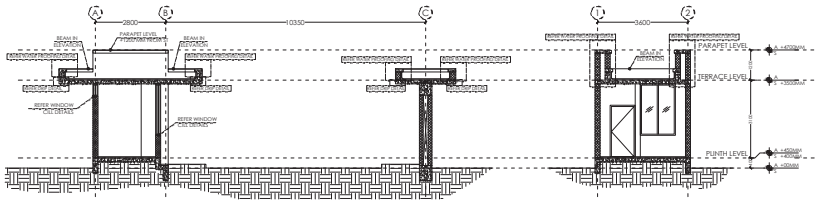


ELEVATIONS

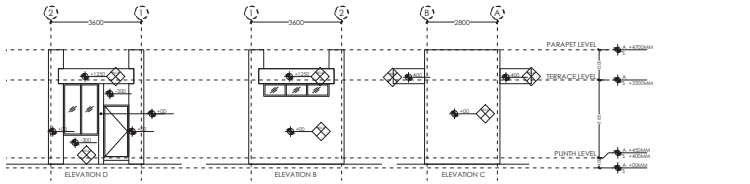

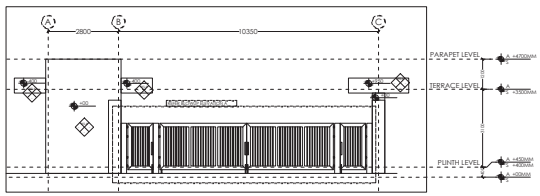

STRUCTURAL DETAIL OF GUARD HOUSE AND GATE

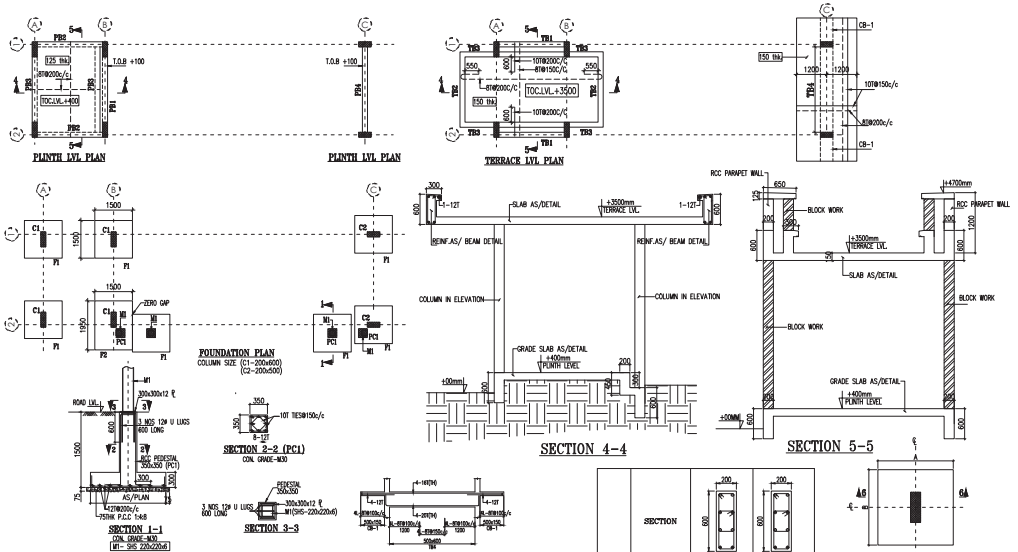

SCHEDULE OF BEAM REINFORCEMENT

BEAM MKD	BEAM SIZE	BEAM REINFORCEMENT				
		BOTTOM REINF.		TOP REINF.		STIRRUPS
		ALLTH. (BH1)	EXTRA (BH2)	ALLTH. (BT1)	EXTRA (BT2)	
PB1	(200X800)	2-20T	- -	2-16T	- -	S1/S2
PB2	(200X800)	2-20T	- -	2-16T	- -	S1/S2
PB3	(200X450)	2-20T	- -	2-16T	- -	S1/S2
PB4	(200X600)	2-16T	- -	2-16T	- -	S1/S2
TB1	(200X600)	2-16T	- -	2-16T	- -	S1/S2
TB2	(200X600)	2-16T	- -	2-16T	- -	S1/S2
TB3	(200X600)	2-16T	- -	2-16T	- -	S1/S2
TB4	(500X600)	4-20T	- -	4-16T	- -	S7/S8

SCHEDULE OF STIRRUPS

S1	2L-8T@100C/C	S7	4L-8T@100C/C
S2	2L-8T@200C/C	S8	4L-8T@150C/C

SCHEDULE OF FOOTINGS

FOOTING MKD	FOOTING SIZE	DEPTH OF FOOTING	REINFORCEMENT	TOP REIN.
	AxB	D	(AxB)	(AxB)
F-1	1500x1500	300	12T@200c/c	-
F-2	1500x1950	300	12T@200c/c	-

FOUNDATION TO TERMINATION LVL	SECTION		
	TIES/SET	a+b [G1]	a+b [G1]
	REINF.	8-16T	8-16T
	MIX.	M-30	M-30
	COLUMN SIZE	200x600	200x500
LEVELS	MARKED	C1	C2

NOTES

- Dimensions are not to be scaled.
- All Dimensions are in Millimeters unless stated otherwise.
- All Levels are in Millimeters and relate to ..... Datum level.
- Contractor should verify all dimensions, details,specifications & site conditions & shall report any error, omission and/or anomoly to the Campus Designer before commencement of work.
- For construction purposes, the dimensions shall not be measured directly of the drawings. The drawings shall not be used for construction until they are issued for construction.
-These drawings are to be read in co-ordination with HVAC, Electrical, Plumbing drawings & all relevant sections of specifications.
-All shop drawings should be provided to the Campus Designer for approval.

NOTE:
ALL PLANS IN THE DRAWING ARE GENERAL PLANS FOR DETAIL PURPOSES ONLY. PLEASE REFER THE ARCHITECTURAL PLANS AND LAYOUTS FOR INDIVIDUAL BUILDINGS.

ISSUES

DATE	REVISION	DESCRIPTION

* SHUTTERING DRAWING TO BE PROVIDED TO THE CAMPUS DESIGNER FOR APPROVAL.
* CONTRACTOR TO PROVIDE SHOP DRAWINGS FOR THE APPROVAL FROM THE CAMPUS DESIGNER

CLIENTS:
INDIAN INSTITUTE OF MANAGEMENT VISAKHAPATNAM
Indian Institute of Management Visakhapatnam, Prof. G.V. Subbaraman Drive, I.I.P. Transit Campus, Andhra Bank School of Business Building, Andhra Univ. Campus, Visakhapatnam - 530003, A.P.

ARCHITECTS:
ARCOP ASSOCIATES PVT. LTD.
A-15, Panchsheel Enclave, S.K. 1,
New Delhi-110048
Phone : 011 - 26433550

Architect's Signature | Client's Signature

Job Title
IIM VISAKHAPATNAM

Drawing Title
TYPICAL GATE 02 DETAILS

Document Release Type
TENDER (GFC)

Scale	Drawing No.
VARIES	TYP-AR-919
14 JAN 2020	
Drawn by: SS	Revision No.: R0
Checked by: VB	

AUTHORITY: