
Higher level cross member required with min 200mm face where the opening width is over 3000mm or where the operator is mounted centrally.

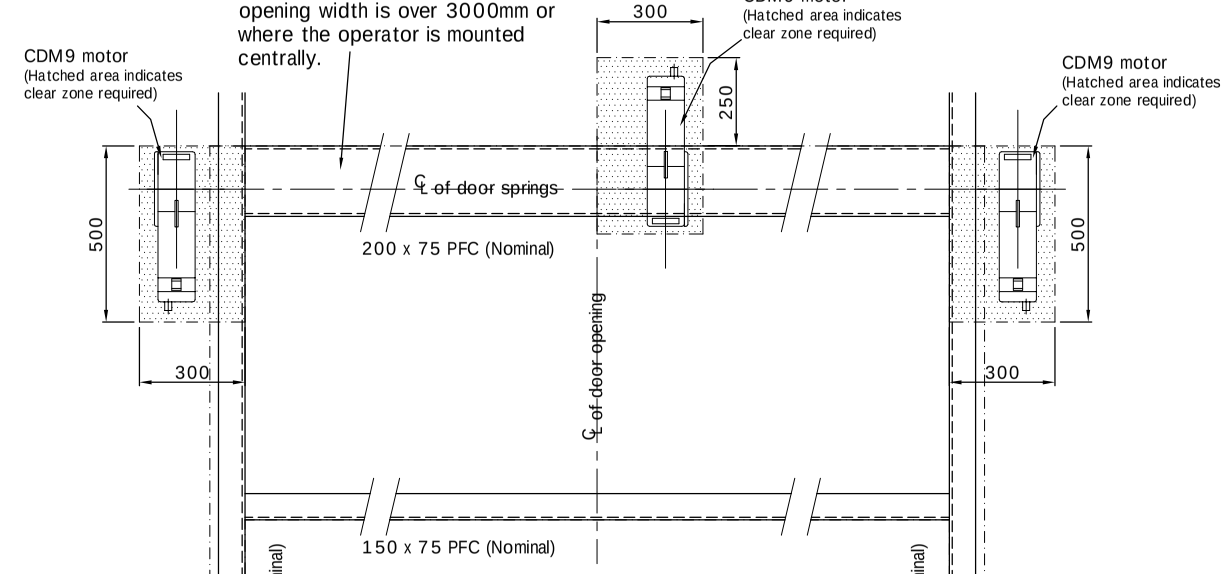

INTERNAL VIEW OF DOOR OPENING

(Door tracks omitted for clarity)


All steelwork to be by others in conjunction with the structural engineers design, calculations and specification

Note: All steel must have the internal fixing faces set flush in the same plane and be clear from projections, such as bolt heads.


Vertical posts to have a minimum 75mm free fixing face

All base plates must be kept clear of the internal face of the posts.

All secondary steelwork including mounting plates and suitable mounting surfaces for control equipment must be provided by others in line with our installation requirements

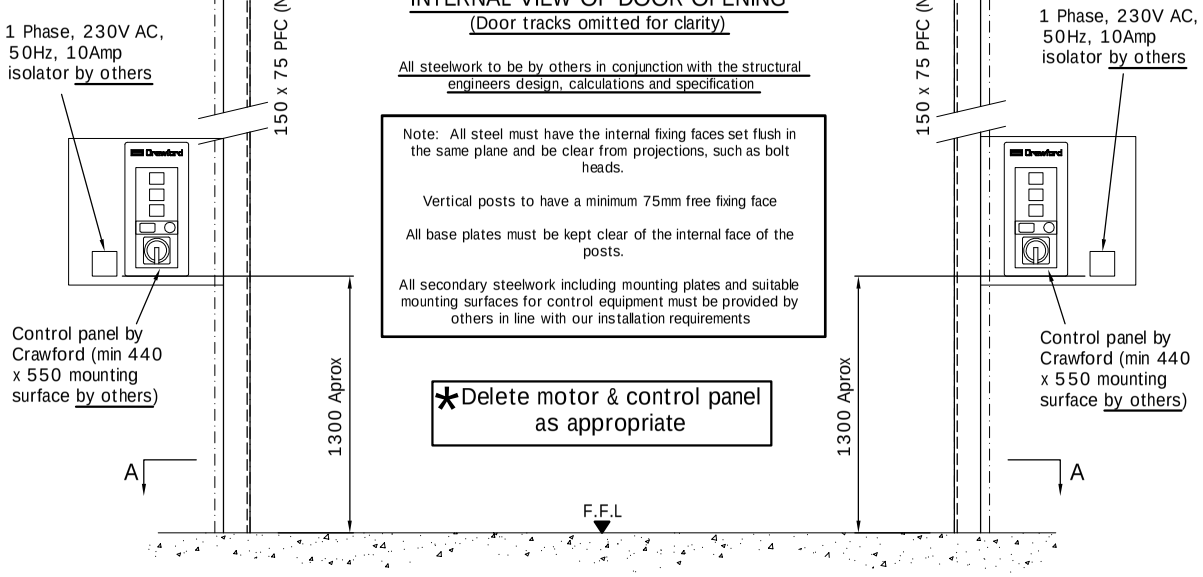

*Delete motor & control panel as appropriate

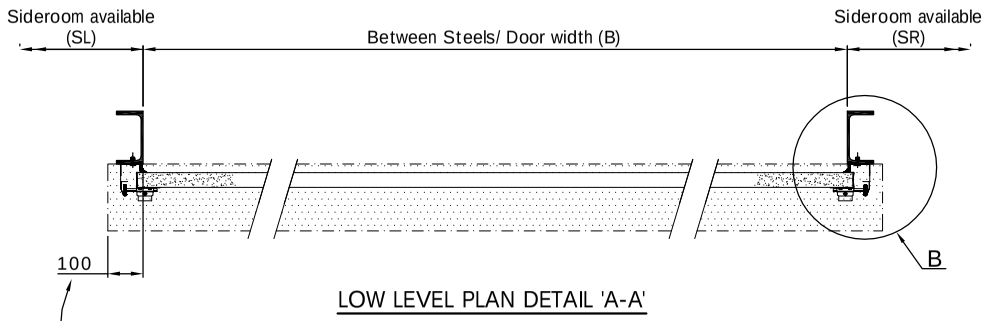

LOW LEVEL PLAN DETAIL 'A-A'

Note:- Minimum clearance required to each side except where a lock interlock is required, then 150mm will apply at control panel side, also differs at operator location see elevation.


© COPYRIGHT AAES

TOLERANCES +/- 3mm (DO NOT SCALE - if in doubt ask)

* ……..° Pitched Horizontal Tracks

(Available in incriments of 5° upto max 35°)

Std. track hangers 2000mm long max by Crawford at max 2000mm centres. Suitable structure to fix to required by others.

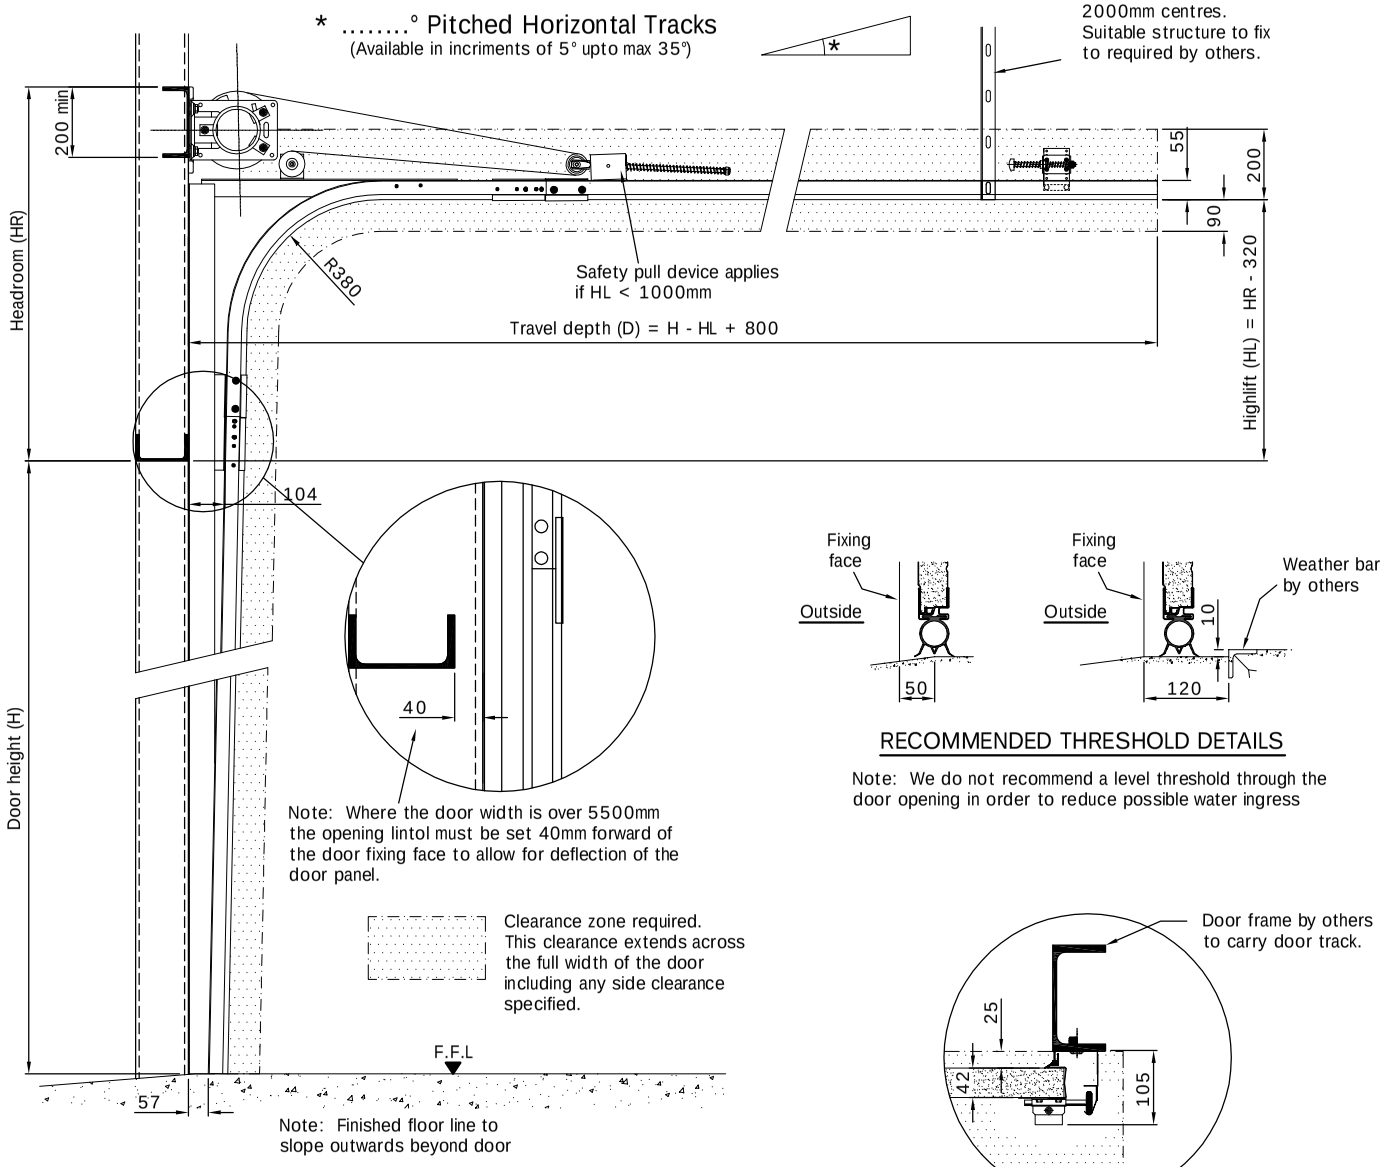

Note: Where the door width is over 5500mm the opening lintol must be set 40mm forward of the door fixing face to allow for deflection of the door panel.


Clearance zone required. This clearance extends across the full width of the door including any side clearance specified.

Note: Finished floor line to slope outwards beyond door

SECTION DETAIL

RECOMMENDED THRESHOLD DETAILS

Note: We do not recommend a level threshold through the door opening in order to reduce possible water ingress

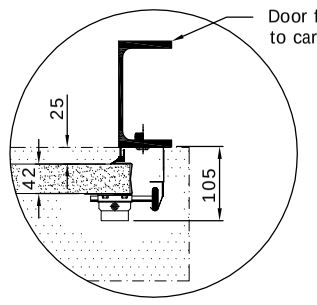

ENLARGED DETAIL 'B'

Pos.	Qty.	B	H	HR	HL	D	SL	SR

SPECIFICATION

DOOR TYPE: OH1042 P ☑ F ☐

OPERATION: CDM9 Motor

CONTROL PANEL:

- 920 Panel (205x150x75, Impulse up, deadman down) ☐
- 930 Panel (205x150x75, Impulse up & down, safety edge) ☐
- 950 Panel (360x150x120, Impulse up & down, safety edge) ☐

OPTIONS (930 / 950 panel only)

- Automatic closing (930 / 950 panel) ☐
- Reversing a closing door (930 / 950 panel) ☐
- Pull Rope (930 / 950 panel) ☐
- Photocells (930 / 950 panel) ☐
- Remote control (930 / 950 panel) ☐
- Magnetic Loop (950 panel) ☐
- Radar (950 panel) ☐
- Traffic lights (950 panel) ☐
- Warning lights (950 panel) ☐
- Reduced opening (950 panel) ☐
- Airlock (950 panel) ☐

FINISHES:

- Internal (Standard Ral 9002 - off white) ☐
- Other (specify Ral / BS colour) _____ ☐
- External (Standard polyester options) ☐
- Ral 3002 - Red ☐ Ral 1021 - Yellow ☐
- Ral 5010 - Blue ☐ Ral 7016 - Grey ☐
- Ral 9010 - White ☐ Ral 9006 - Silver ☐
- Ral 9002 - Off white ☐ Ral 9007 - Grey ☐
- Ral 6005 - Green ☐
- Other (specify Ral / BS colour) _____ ☐

WINDOWS:

Panel (P) Option:	Frame (F) Option:
DARP ☐	Solid Bottom Panel ☐
DAOP ☐	Double Glazed ☐
Single glazed ☐	Single glazed ☐
Sections _____	Glass _____

PASSDOOR: (Viewed from inside)

Left hand hung ☐ Right hand hung ☐

On left ☐ In Center ☐ On right ☐

LOCKING:

Lockbolt ☐ Cylinder Lock ☐

NOTES:

ASSA ABLOY

ASSA ABLOY Entrance Systems Ltd
Industrial Door and Docking Solutions

7Churchill Way .35A Business Park .Chapeltown .Sheffield .UK .S35 2PY
Tel: +44 (0)114 257 4330 Fax: +44 (0)114 257 4399

TITLE: Setting out details for electric operated sectional overhead door with high lift hardware fitting to steelwork.

ID 052 - 542-242 HL - Electric _Steel B

CLIENT:

SITE:

DRAWING STATUS

- PRELIMINARY ✓
- FOR APPROVAL
- CONSTRUCTION
- AS BUILT

REV.	BY	DATE	COMMENT

DRAWN BY:

CHECKED BY:

DATE:

DRAWING No.

REV.

PDF created with pdfFactory trial version www.pdffactory.com