


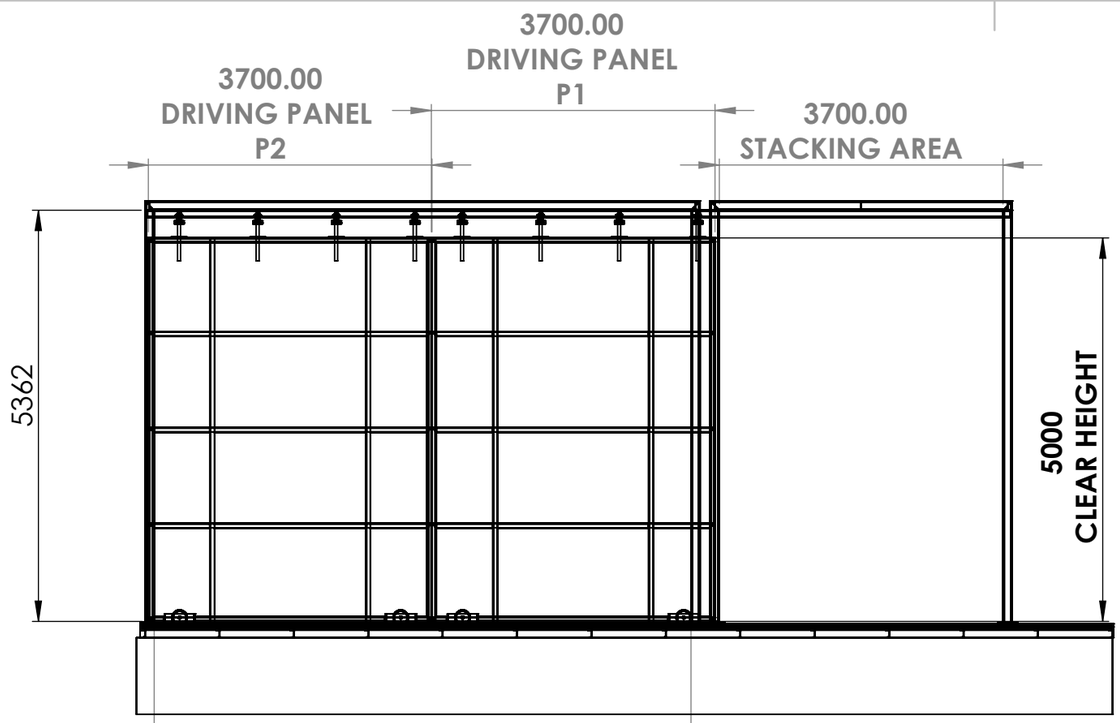


CLOSE POSITION

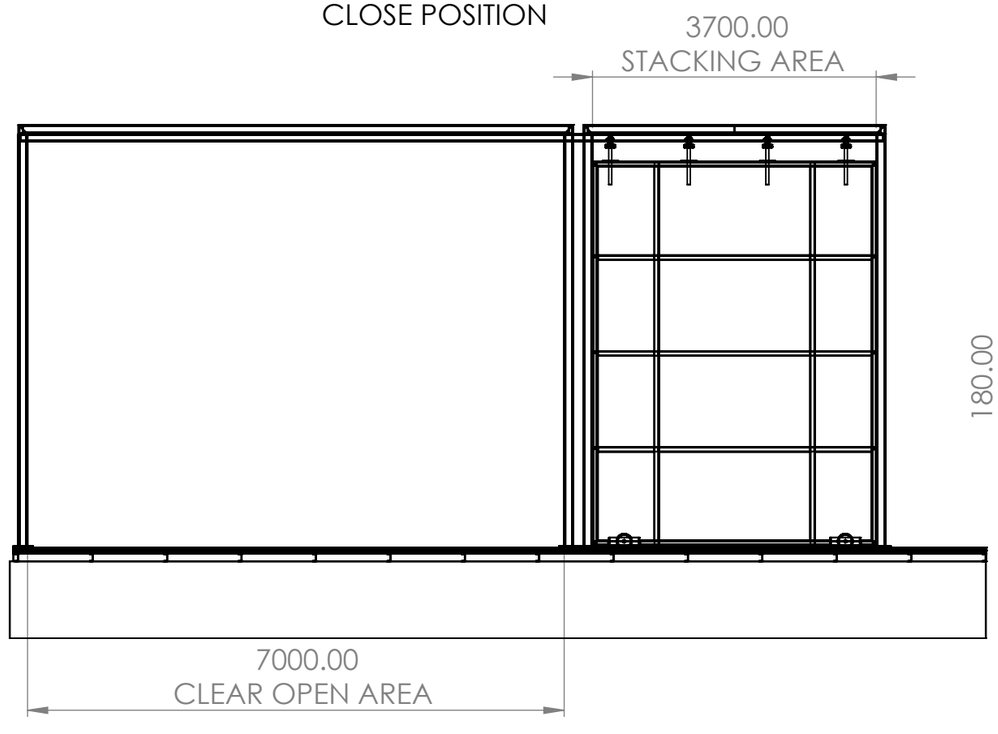


OPEN POSITION

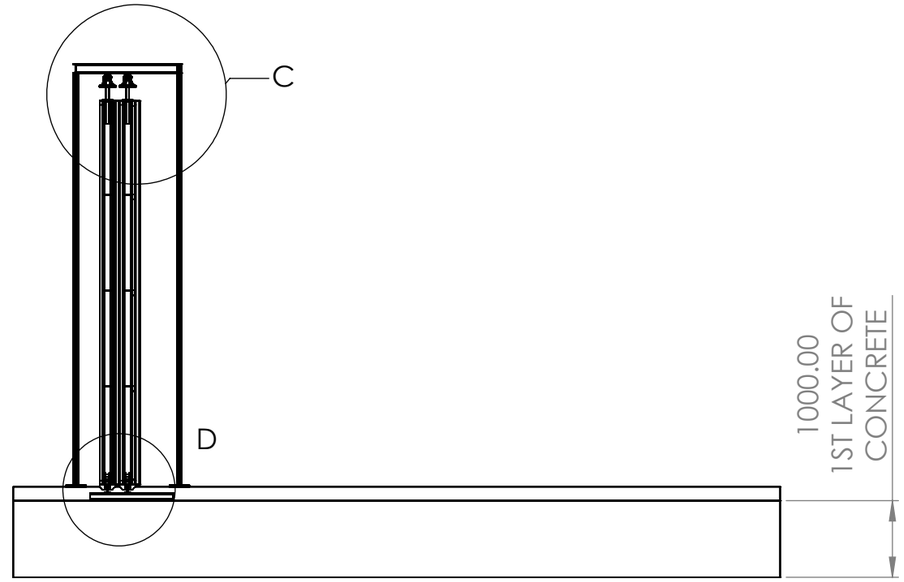

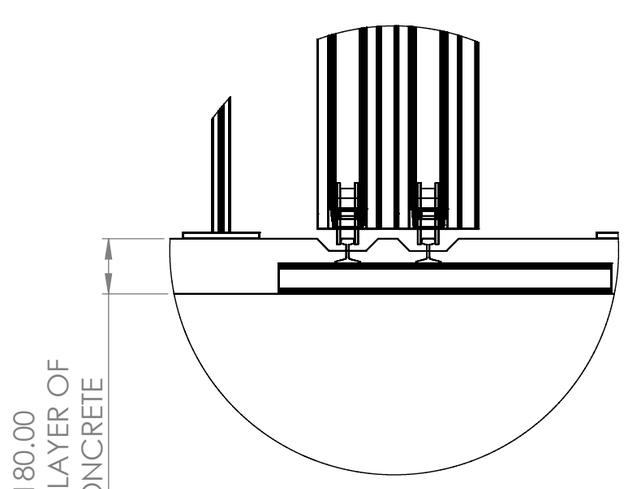

DETAIL D
SCALE 1 : 20

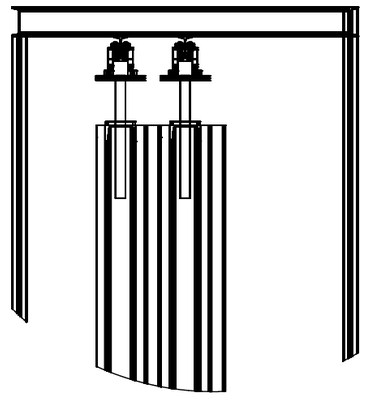

DETAIL C
SCALE 1 : 25

TITLE : HANGING SLIDING DOOR 7000 WIDTH X 5000 HEIGHT MM			NIHVA Technologies Pvt. Ltd. NIHVA TECHNOLOGIES PVT LTD
	NAME	SIGN	DATE
DRAWN	BHARATI SABALE		10-01-2025
CHK'D	SURAJ WARALE		10-01-2025
APPV'D	VIJAY T.		10-01-2025
CLIENT NAME : ISRO			
PRODUCT NAME : HANGING SLIDING DOOR			
SITE LOCATION : ALUVA, KERALA			
DWG NO. GA			A3
			REVISION : 0
	DIMENSIONS ARE IN MILLIMETERS		SCALE: / SHEET 1 OF 1