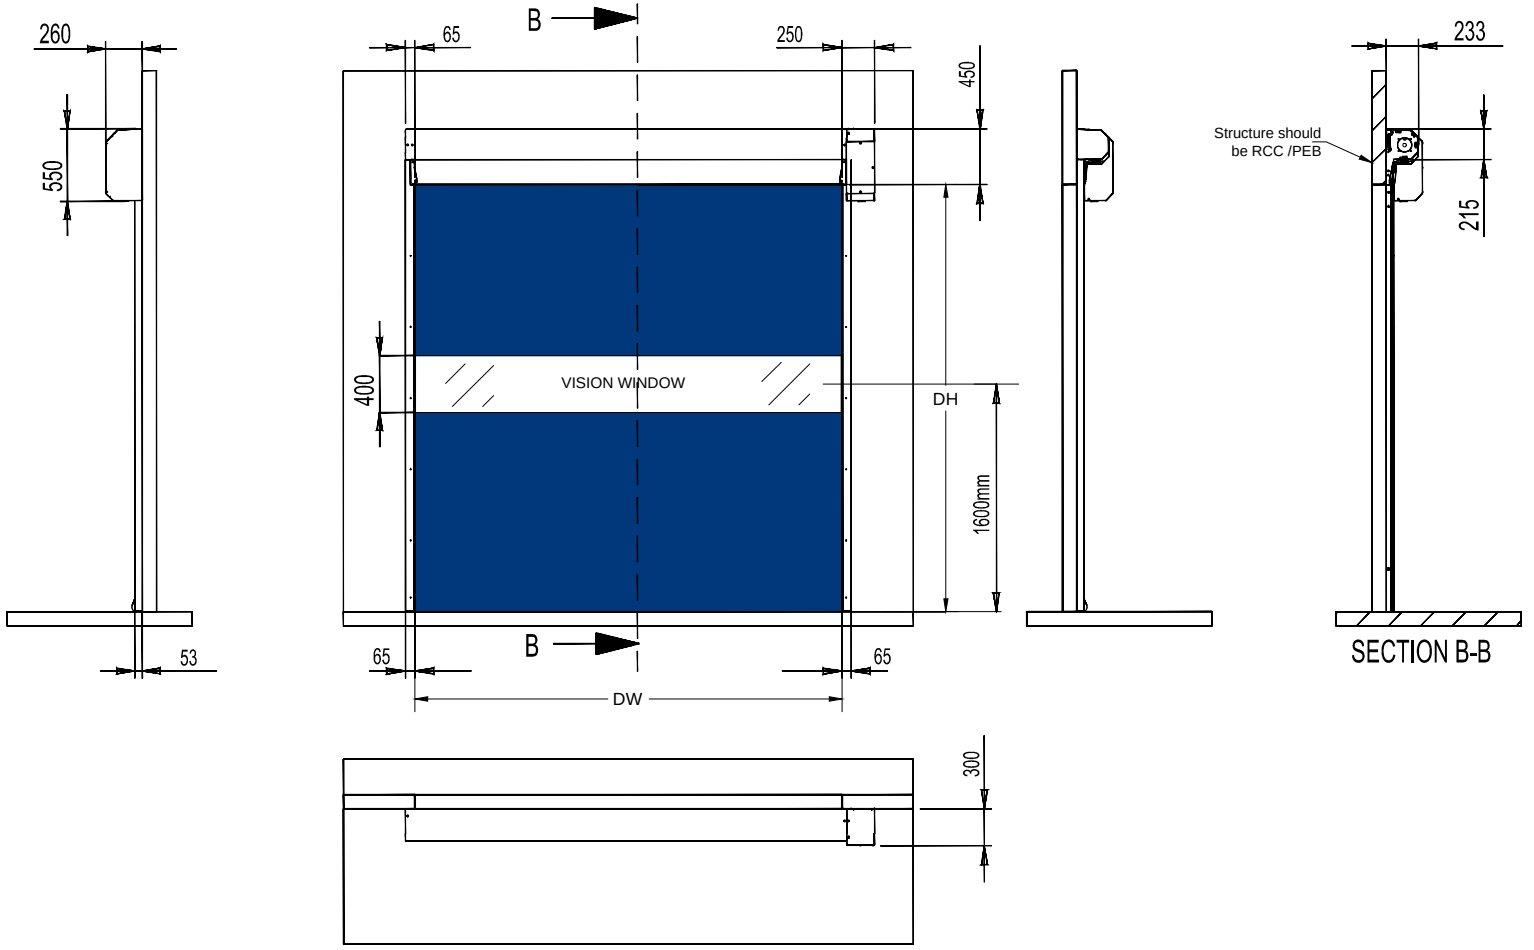


RAL COLOR - RAL 5002 (BLUE)

DOOR DIMENSION				
SR NO	DW	DH	MOTOR LOCATION	QUANTITY
1	1900	2300	RIGHT HAND SIDE	01

Note-
1. All Civil work will be in clients scope.
2. Client has to choose motor side (Right/left) according to the site conditions. Standard door comes with Right side Motor mounting.
3. All Construction in stainless steel AISI304

This drawing & designing is the property of NIHVA TECHNOLOGIES. Not to be sold or copied to any other concern.

TITLE: HIGH SPEED DOOR HS9020GHY.

NIHVA TECHNOLOGIES PVT. LTD. PUNE
Tel : 020 66304033
Email:- info@nihva.com
Website:- www.nihva.com

	NAME	SIGN	DATE
DRAWN	S.L		31/10/18
CHECK	P.A		31/10/18
APPROVAL	R.D		31/10/18

CLIENT -
PROJECT -
SITE -

If any queries contact : design@nihva.com
DWG. NO. : NIHVA/18-19/VDR/193 REV- 00
ALL DIMENSION ARE IN mm
SCALE: NTS WT: SHEET: 01 OF 01