[HSSD] High speed Sectional


Door – 3500mm x 4500 mm

Sheet ① of ②

23/01/2015

Note # 4

Show detail for new Plate with PEB member.

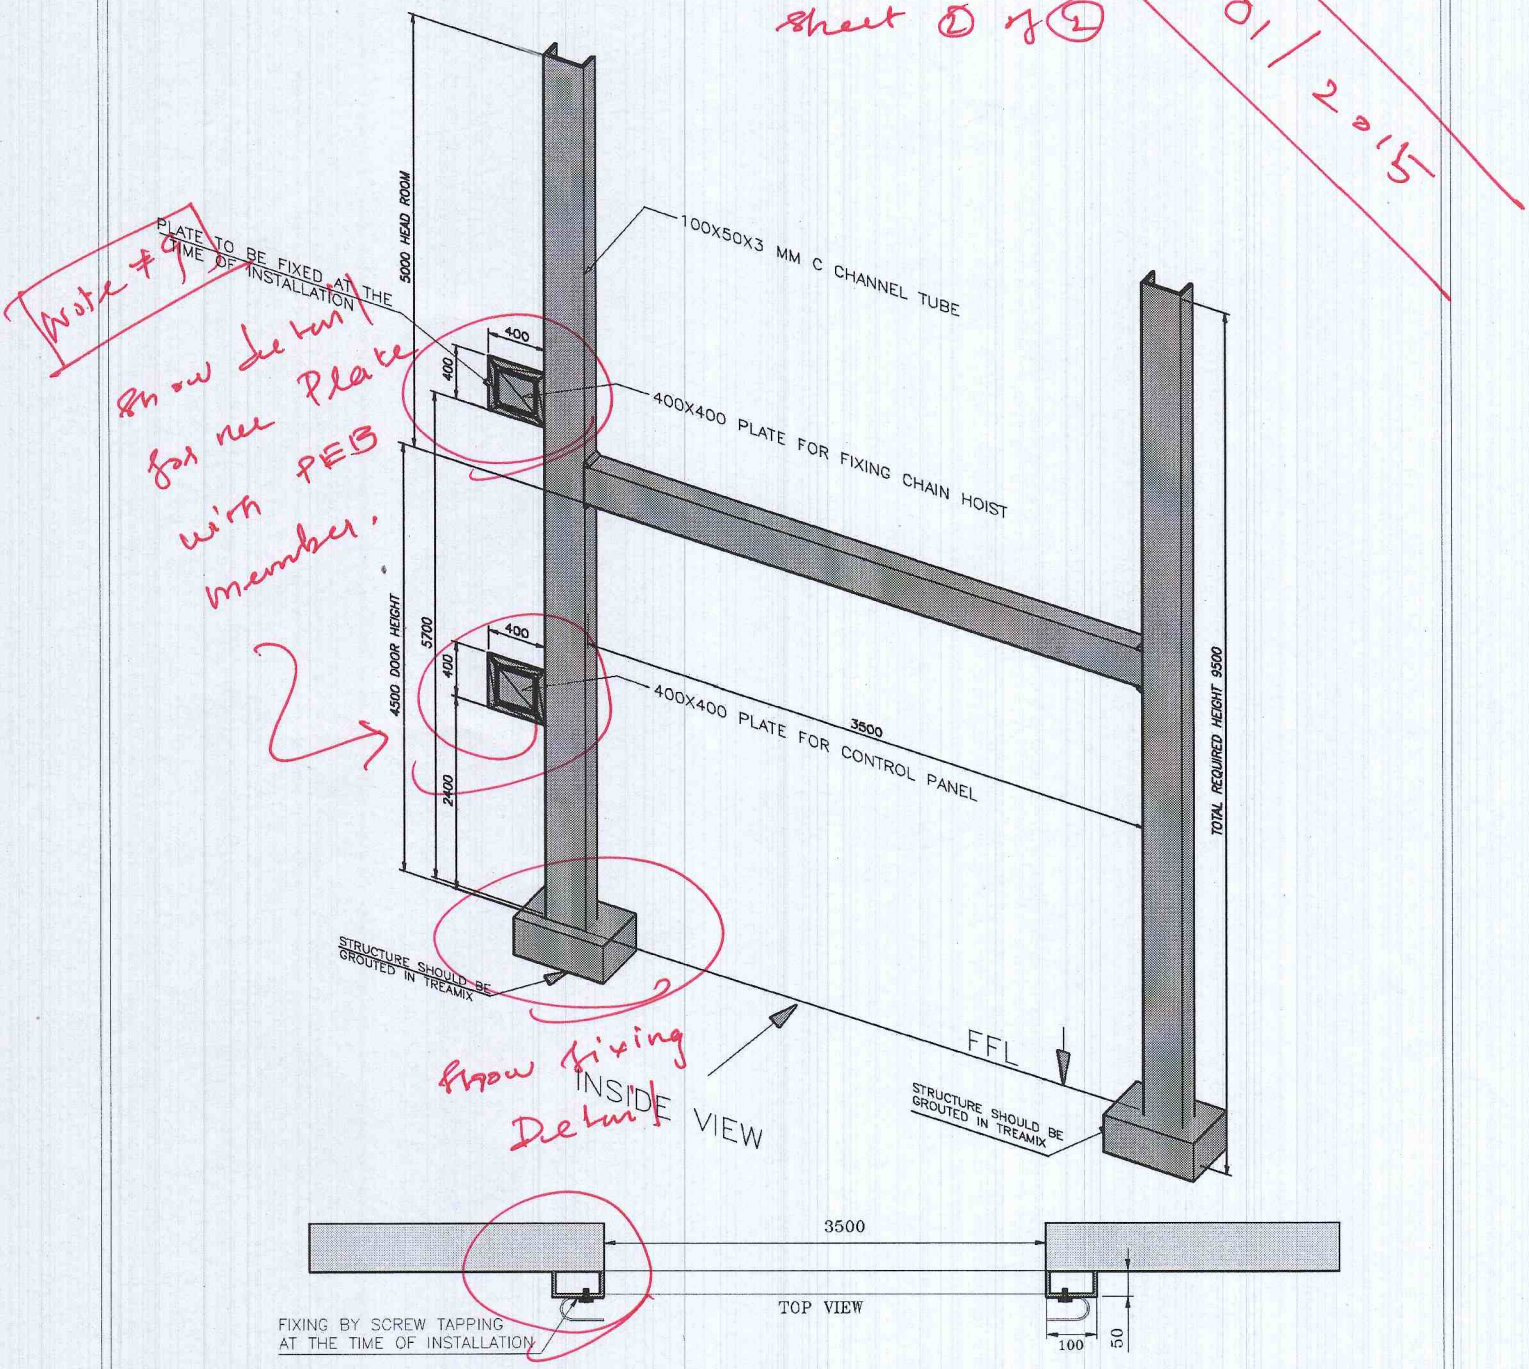

Show fixing Detail

structure should be bear approx. 600 k.g. weight. (wind pressure included)

This drawing & designing is the property of NIHVA TECHNOLOGIES. Not be sold or copy to any other concern.

TITLE: STRUCTURE FOR SECTIONAL DOOR	ALL DIMENSION ARE IN mm		NIHVA TECHNOLOGIES PVT. LTD.	NIHVA TECHNOLOGY PVT. LTD. PUNE Tel : 020 66304033 Email:– info@nihva.com Website:– www.nihva.com
		SIGN	DATE	
	DRAWN	ABHIJIT	22/01/15	CLIENT -REWARD
CLIENT APPROVAL	CHECK	ANIL	22/01/15	PROJECT-IR PROJECT AHEMADABAAD
	ENG			SITE -
	APPRD.			DWG. NO. - NVA/REWARD/02/RE02
	MFG			SCALE: 01 WT: SHEET: 01
	Ref. No.			If any queries contact : projects@nihva.com