


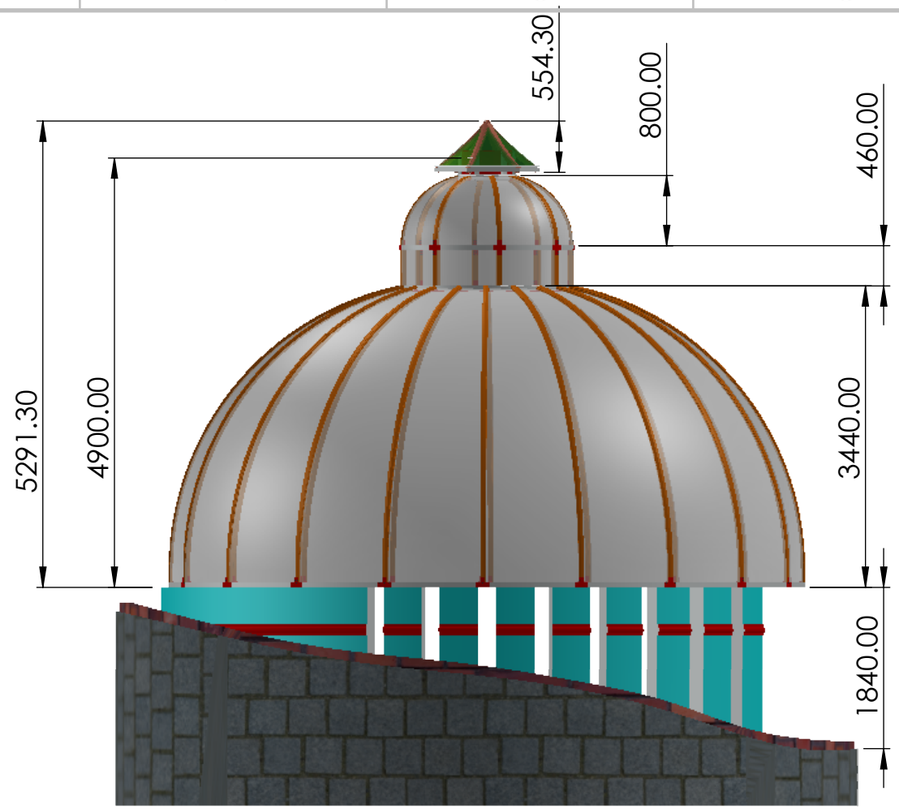


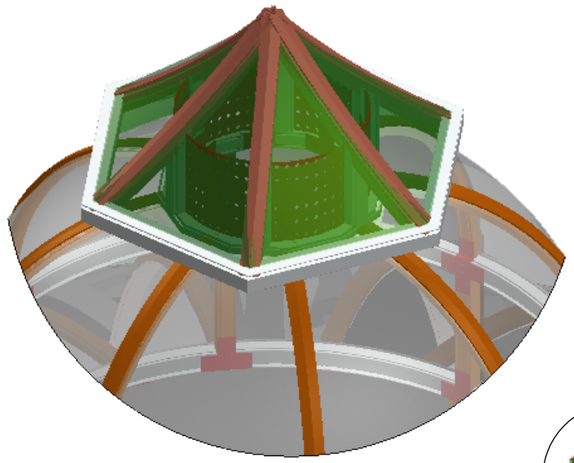

DETAIL A
SCALE 1 : 18

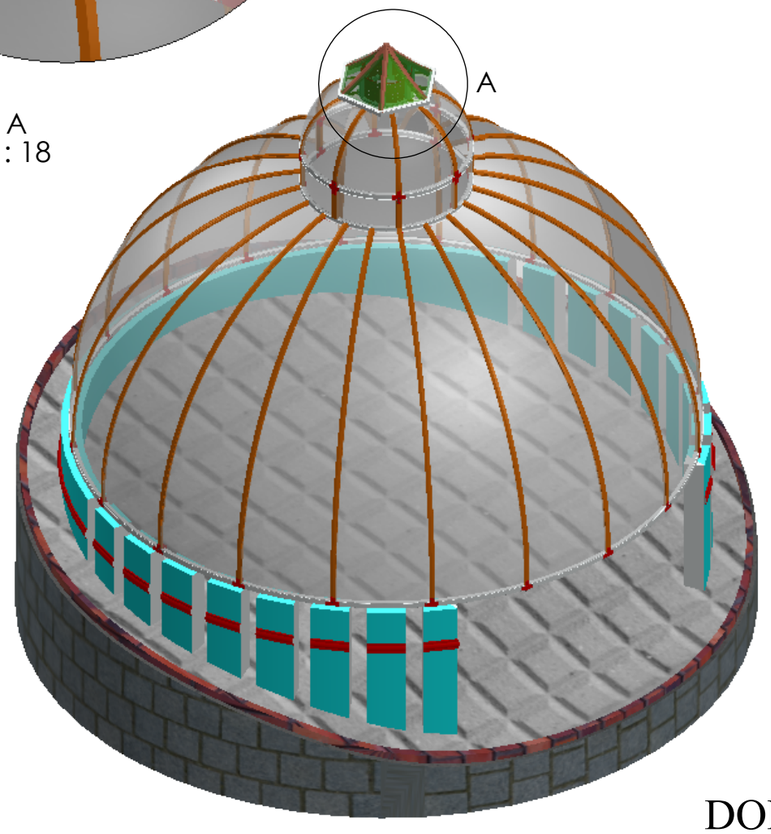


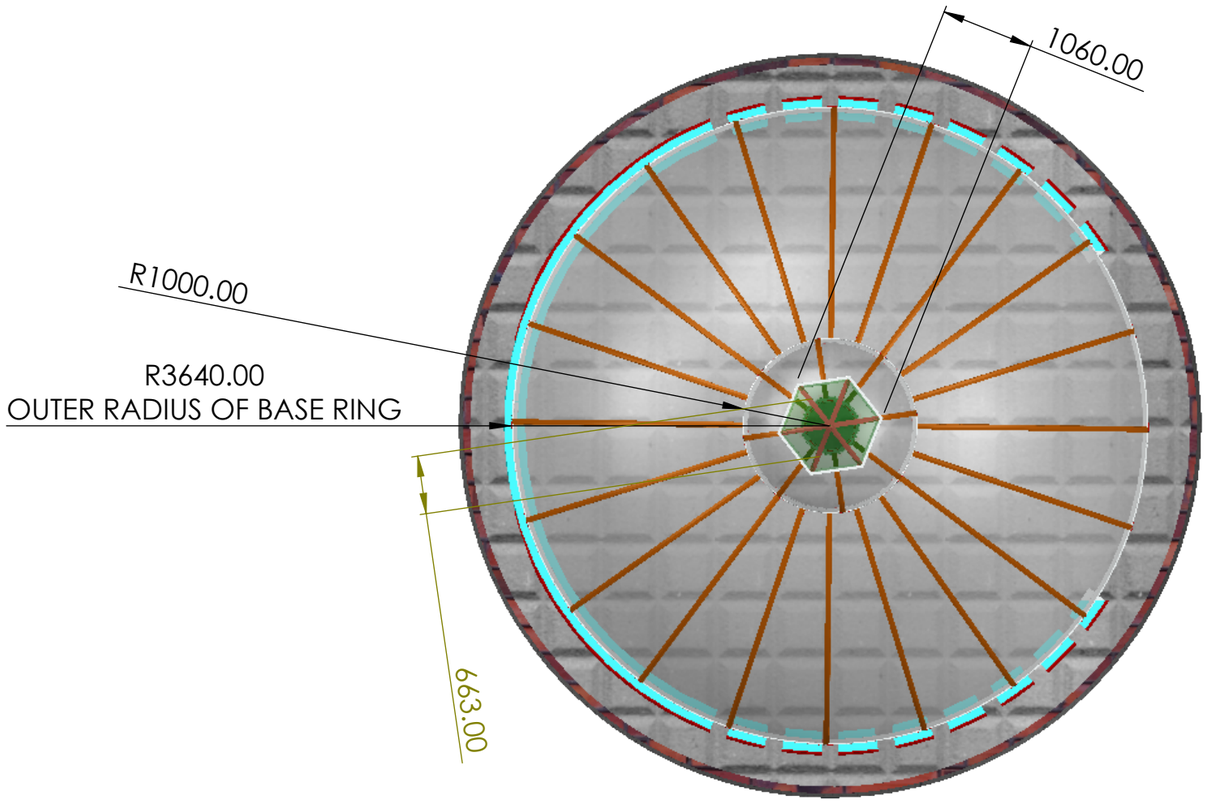

DOME


TITLE - ROOF AUTOMATION				NIHVA TECHNOLOGIES PVT.LTD.PUNE
DWG NO - NTPL-278-PM-001-00-00-00				Website - www.nihva.com
	NAME	SIGNATURE	DATE	PROJECT NO - NTPL-278-PM
DRAWN	V.W		15-05-25	PRODUCT - DOME
CHK'D	S.W.		15-05-25	SITE LOCATION - LONAVLA
APPV'D	V.T.		15-05-25	
if any queries contact - supportautomation@nihva.com				REVISION -01 / QTY - 1
ALL DIMENSION ARE IN mm		A3		SCALE / SHEET 1 OF 20

ITEM NO.	PART NUMBER	DESCRIPTION	QTY.
1	..REV03BASE RING	AL 6063_T4	1
2	..REV03VERTICAL SUPPORT PROFILE ABOVE BASE	AL 6063_T4	20
3	..REV03TOP RING SUPPORT	AL 6063_T4	2
4	..REV03VERTICAL SUPPORT ABOBE TOP RING 1	AL 6063_T4	8
5	..REV03TOP VERTICAL SUPPORT 2	AL 6063_T4	8
6	..REV03POLYGOANL SHAPE BY WELDIND	AL 6063_T4	1
7	..REV03POLYCARBONET SHEET1	POLYCARBONET	20
8	..REV03POLYCARBONET SHEET2	POLYCARBONET	8
9	..REV03VIJAY_T PLATE ASM	SS-304	24
10	..REV03New upper plus bend plate	SS-304	8
11	..REV03PLUS PLATE ASM	SS-304	8
12	..REV03REV 01New upper bend vertical support joining plate ASM	SS-304	8
13	..REV03REV 02VIJAY_T PLATE ASM	SS 304	21
14	REV 02New upper BEND vertical support ABOVE BASE RINGjoining plate ASM	SS-304	20
15	..REV03POLYCARBONET SHEET3	POLYCARBONET	8
16	..HEXAGONAL SAHPE MS 60*30*1.5MM THK	MS	1
17	..VERTICAL TUBE FOR CAP SHAPE SUPPORT MS-60*30*1.5MM THK	MS	6
18	..TOP CONE SHAPE VERTICAL TUBE	MS	6
19	..MESH	SS	1
20	..TOP CAP PC SHEET	POLYCARBONET	6
21	LOCKING PLATE INSIDE ASM	SS -304	20
22	..REV03VIJAY_Rivet_iso_15977_4_x_16_0	RIVET M4X16	160
23	T PLATE	SS304 -117.5X156X3 MM THK	1
24	..REV03REV 01New UPPER BEND VERTICAL SUPPORT Joining Plate	SS 304 - 135.64*156*3MM THK	1

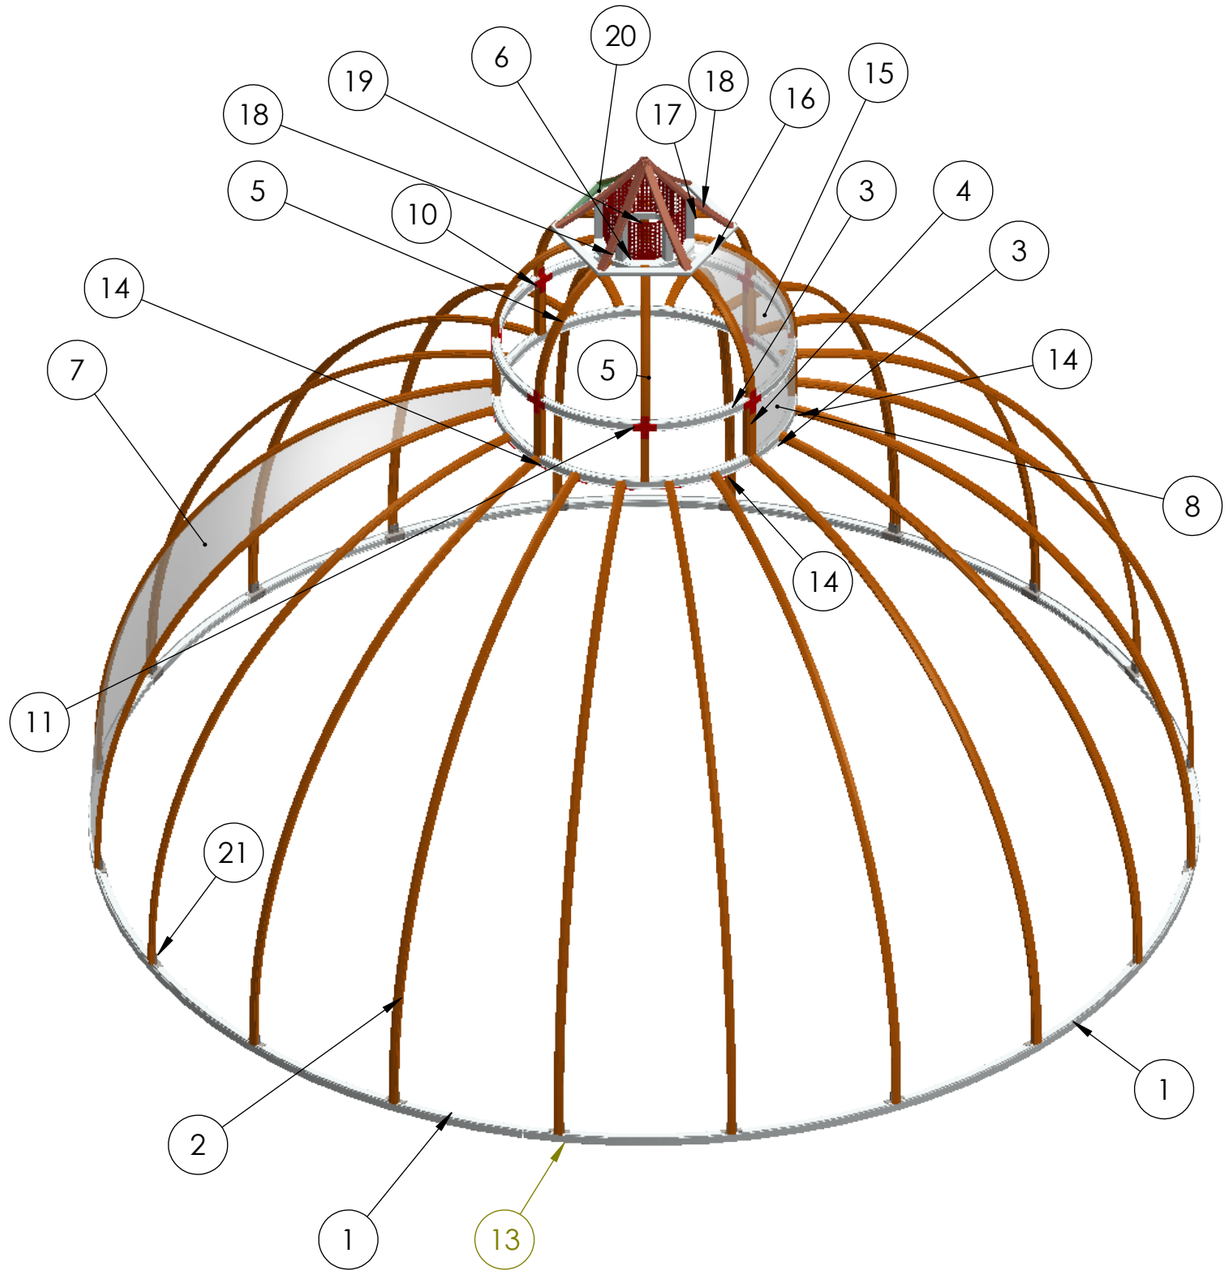

TITLE - ROOF AUTOMATION				NIHVA TECHNOLOGIES PVT.LTD.PUNE
DWG NO - NTPL-278-PM-001-00-00-00				Website - www.nihva.com
	NAME	SIGNATURE	DATE	PROJECT NO - NTPL-278-PM
DRAWN	V.W		15-05-25	PRODUCT -DOME
CHK'D	S.W.		15-05-25	SITE LOCATION - LONAVLA
APPV'D	V.T.		15-05-25	
if any queries contact - supportautomation@nihva.com				REVISION - 01 / QTY - 1
ALL DIMENSION ARE IN mm		A3		SCALE / SHEET 2 OF 20


ITEM NO.	PART NUMBER	DESCRIPTION	QTY.
1	..REV03BASE RING	AL 6063_T4	1
2	..REV03VERTICAL SUPPORT PROFILE ABOVE BASE	AL 6063_T4	20
3	..REV03TOP RING SUPPORT	AL 6063_T4	1
4	..REV03POLYCARBONET SHEET1	POLYCARBONET	20
5	..REV03REV 02VIJAY_T PLATE ASM	SS 304	21
6	REV 02New upper BEND vertical support ABOVE BASE RINGjoining plate ASM	SS-304	19
7	LOCKING PLATE INSIDE ASM	SS -304	20

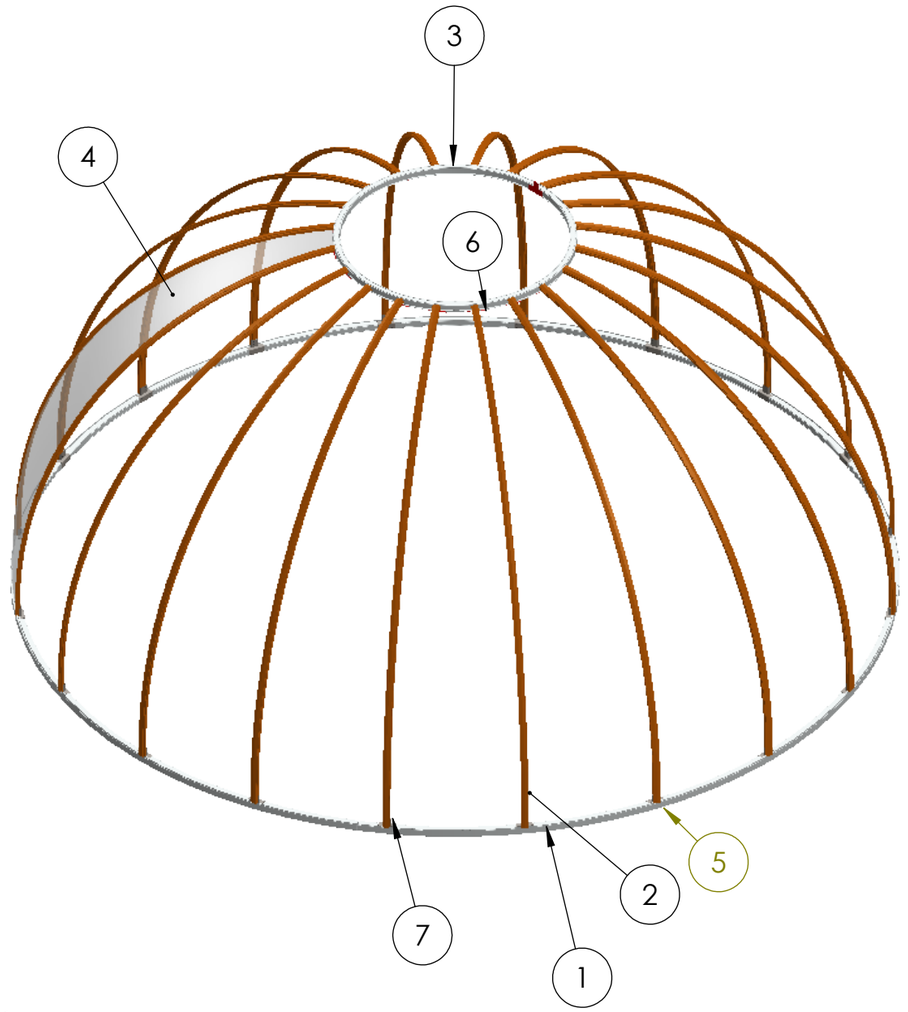


NOTE:
DOME SUB ASSEMBLY 01

TITLE - RETRACTABLE ROOF				NIHVA Technologies Pvt. Ltd.	NIHVA TECHNOLOGIES PVT.LTD.PUNE Website - www.nihva.com
DWG NO - NTPL-278-PM-001-01-00-00					
	NAME	SIGNATURE	DATE	PROJECT NO - NTPL-278-PM	
DRAWN	V.W		15-05-2025	PRODUCT - RETRACTABLE ROOF	
CHK'D	S.W.		15-05-2025	SITE LOCATION - LONAVLA	
APPV'D	V.T.		15-05-2025		
if any queries contact - supportautomation@nihva.com				REVISION - 01	QTY - 1
ALL DIMENSION ARE IN mm			A3	SCALE	SHEET 3 OF 20

ITEM NO.	PART NUMBER	DESCRIPTION	QTY.
1	REV03BASE RING	AL 6063_T4	1

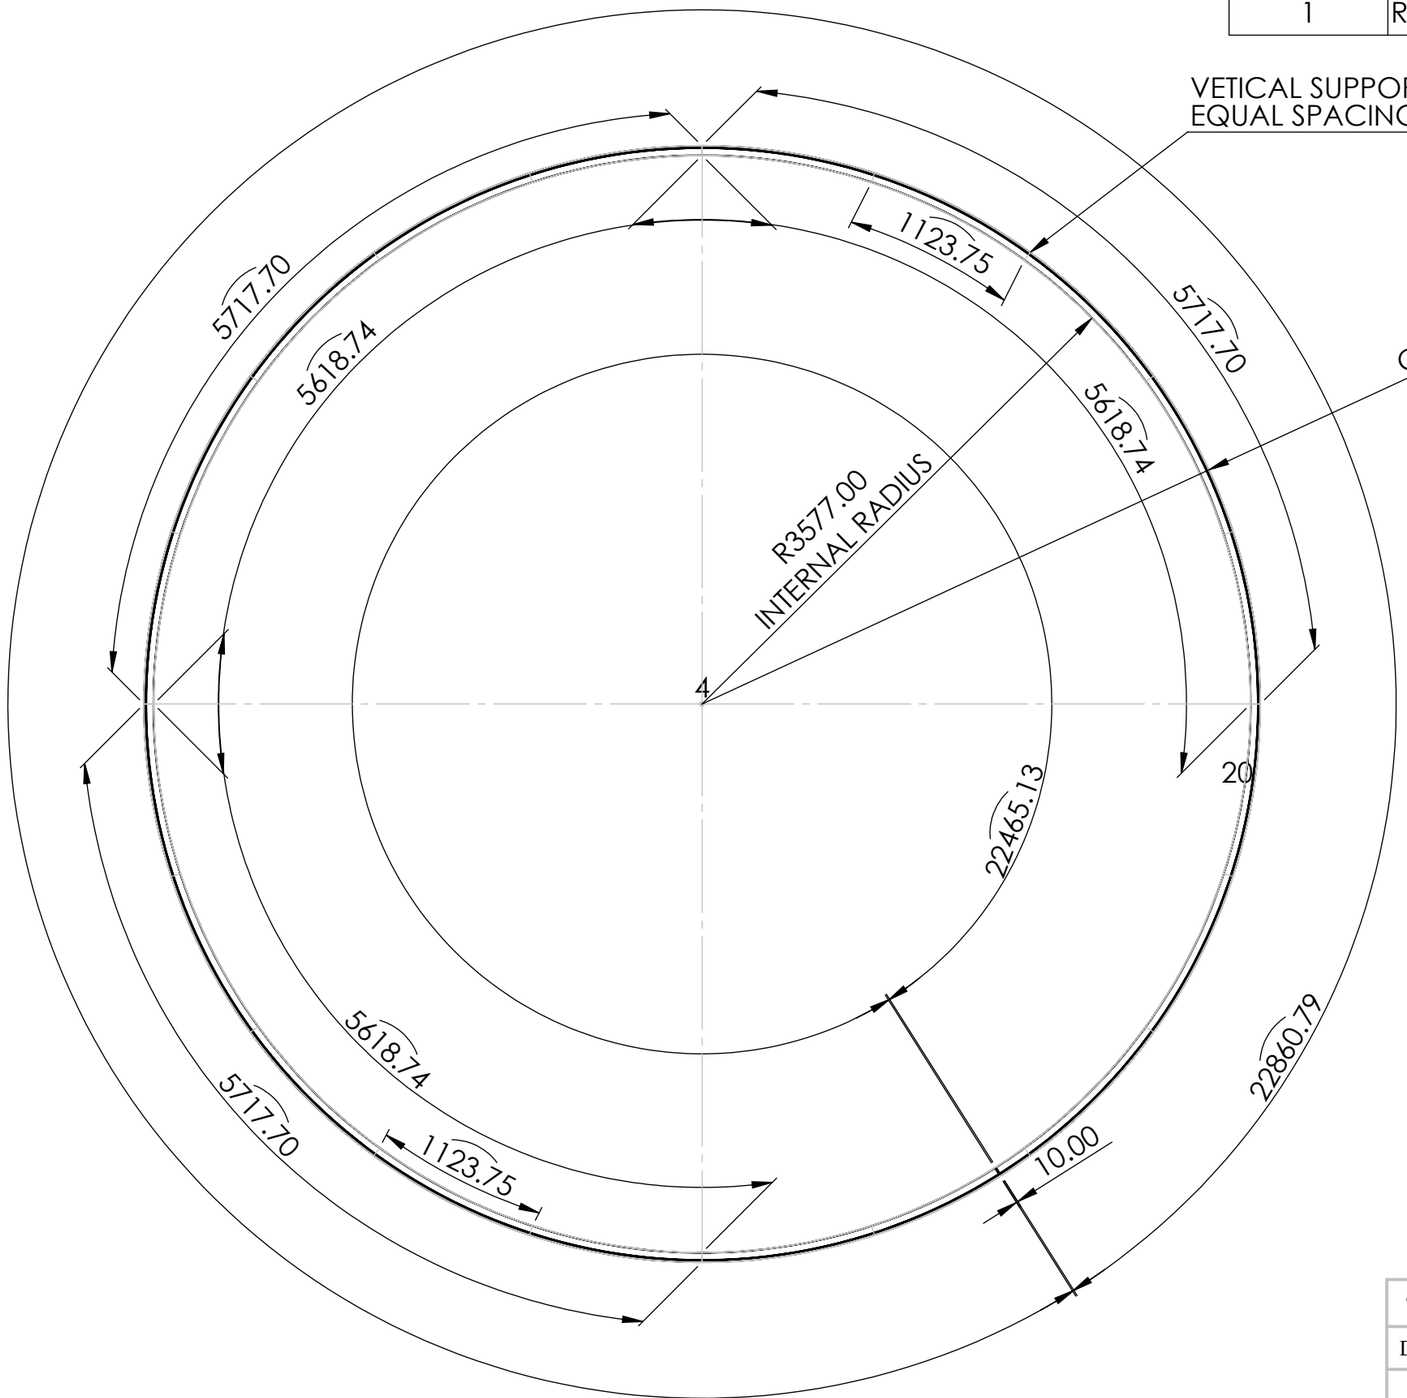


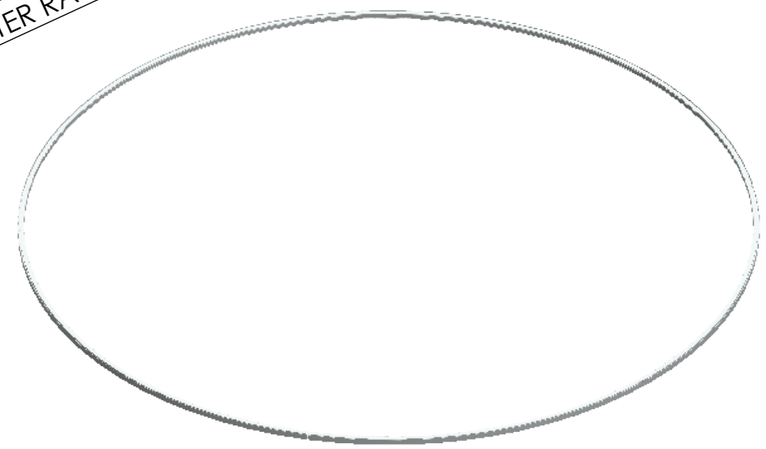


NOTE
BASE RING
USE PROFILE GNT-006

TITLE -ROOF AUTOMATION				NIHVA TECHNOLOGIES PVT.LTD.PUNE
DWG NO - NTPL-278-PM-001-01-01-01				Website - www.nihva.com
	NAME	SIGNATURE	DATE	PROJECT NO - NTPL-278-PM
DRAWN	V.W		15-05-25	PRODUCT - DOME
CHK'D	S.W.		15-05-25	SITE LOCATION - LONAVLA
APPV'D	V.T.		15-05-25	
if any queries contact - supportautomation@nihva.com				REVISION - 01 / QTY - 1
ALL DIMENSION ARE IN mm			A3	SCALE / SHEET 4 OF 20

ITEM NO.	PART NUMBER	DESCRIPTION	QTY.
1	..REV03VERTICAL SUPPORT PROFILE ABOVE BASE	AL 6063_T4	20

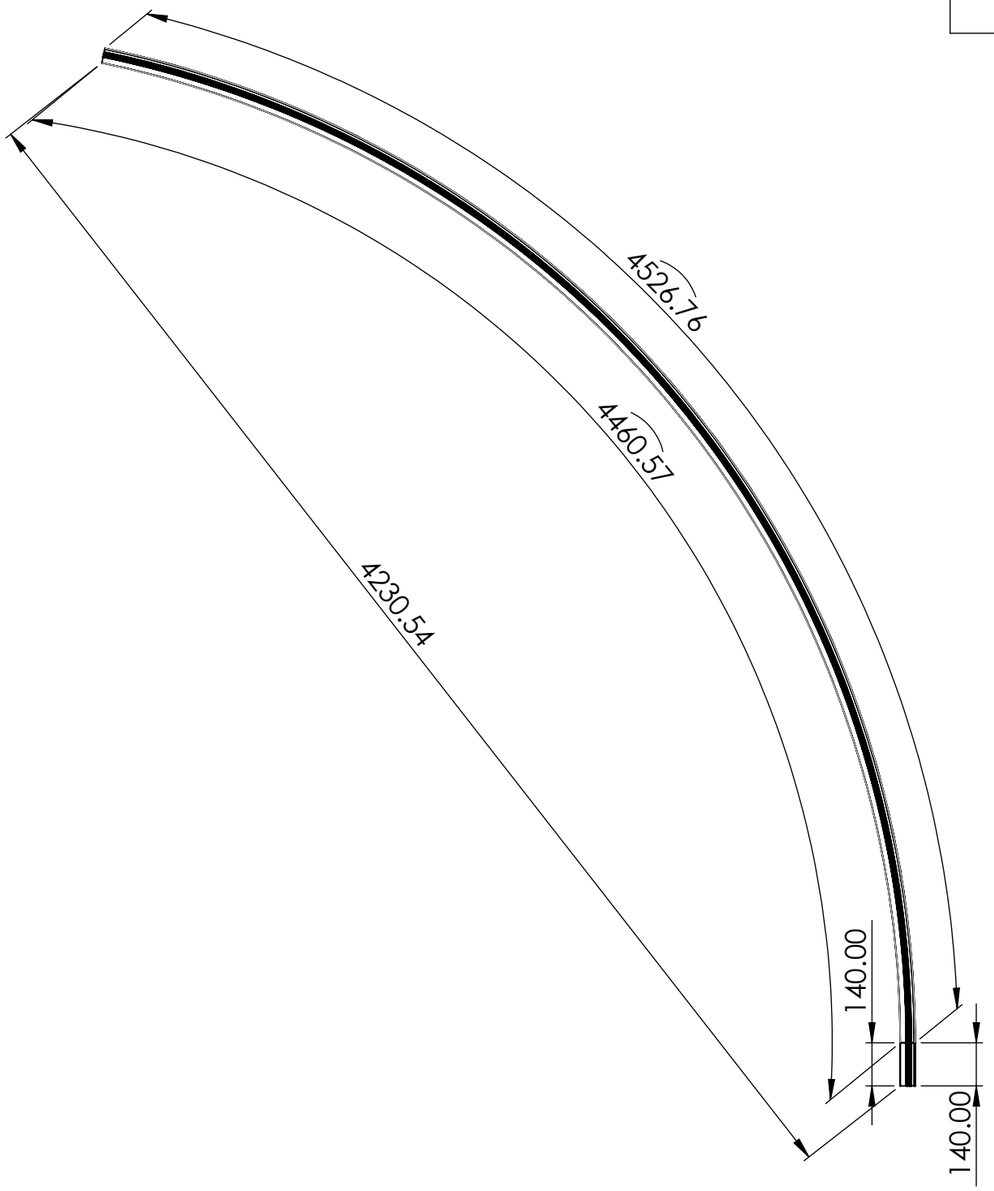


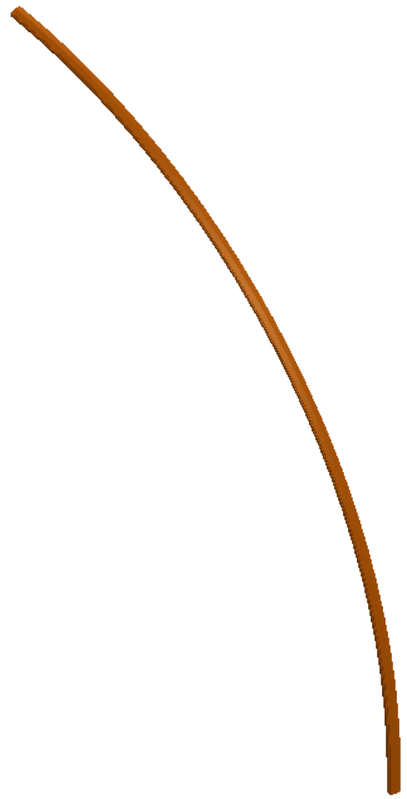


NOTE
VERTICAL SUPPORT PROFILE ABOVE BASE RING
USE PROFILE GNT-009

TITLE - ROOF AUTOMATION				NIHVA TECHNOLOGIES PVT.LTD.PUNE
DWG NO - NTPL-278-PM-001-01-02-02				Website - www.nihva.com
	NAME	SIGNATURE	DATE	PROJECT NO - NTPL-278-PM
DRAWN	V.W		15-05-25	PRODUCT - DOME
CHK'D	S.W.		15-05-25	SITE LOCATION - LONAVLA
APPV'D	V.T.		15-05-25	
if any queries contact - supportautomation@nihva.com				REVISION - 01 / QTY - 1
ALL DIMENSION ARE IN mm			A3	SCALE / SHEET 5 OF 20

ITEM NO.	PART NUMBER	DESCRIPTION	QTY.
1	..REV03TOP RING SUPPORT	AL 6063_T4	2

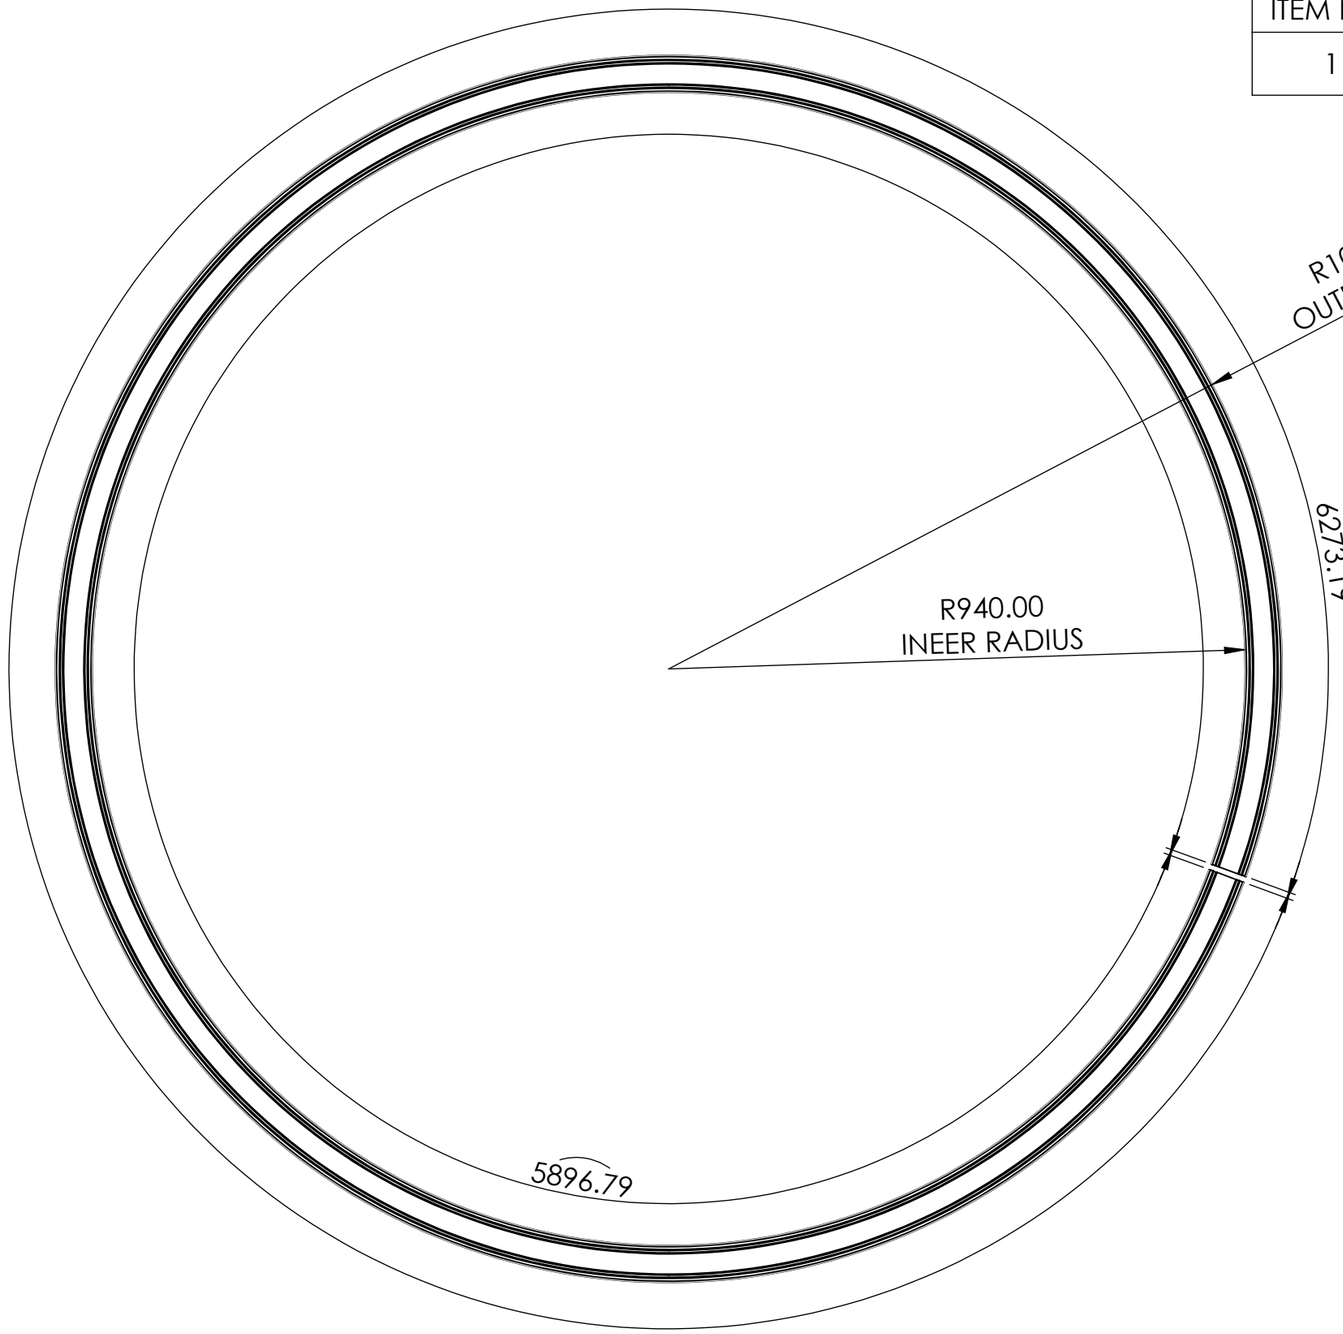


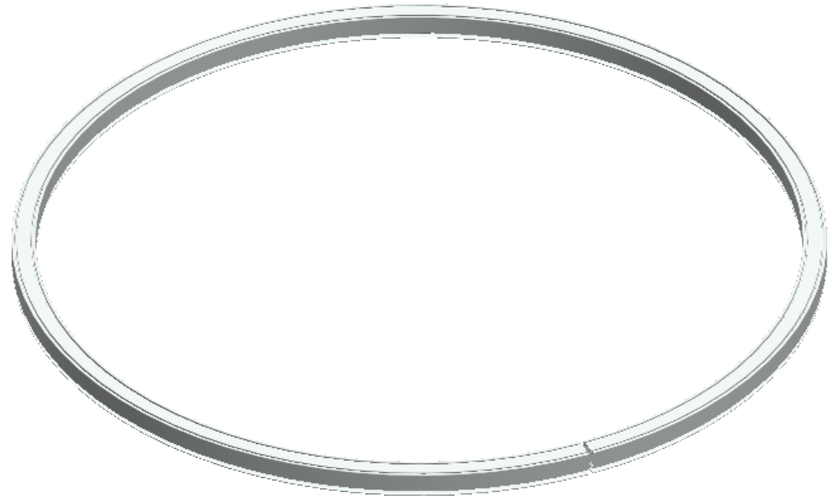


NOTE
TOP RING SUPPORT
USE PROFILE GNT-006

TITLE - ROOF AUTOMATION				NIHVA Technologies Pvt. Ltd.	NIHVA TECHNOLOGIES PVT.LTD.PUNE Website - www.nihva.com
DWG NO - NTPL-278-PM-001-01-03-03				PROJECT NO - NTPL-278-PM	
	NAME	SIGNATURE	DATE	PRODUCT - DOME	
DRAWN	V.W		15-05-25	SITE LOCATION - LONAVLA	
CHK'D	S.W.		15-05-25		
APPV'D	V.T.		15-05-25		
if any queries contact - supportautomation@nihva.com				REVISION - 01	QTY - 1
ALL DIMENSION ARE IN mm			A3	SCALE	SHEET 6 OF 20

ITEM NO.	PART NUMBER	DESCRIPTION	QTY.
1	T PLATE	SS304 -117.5X156X3 MM THK	50

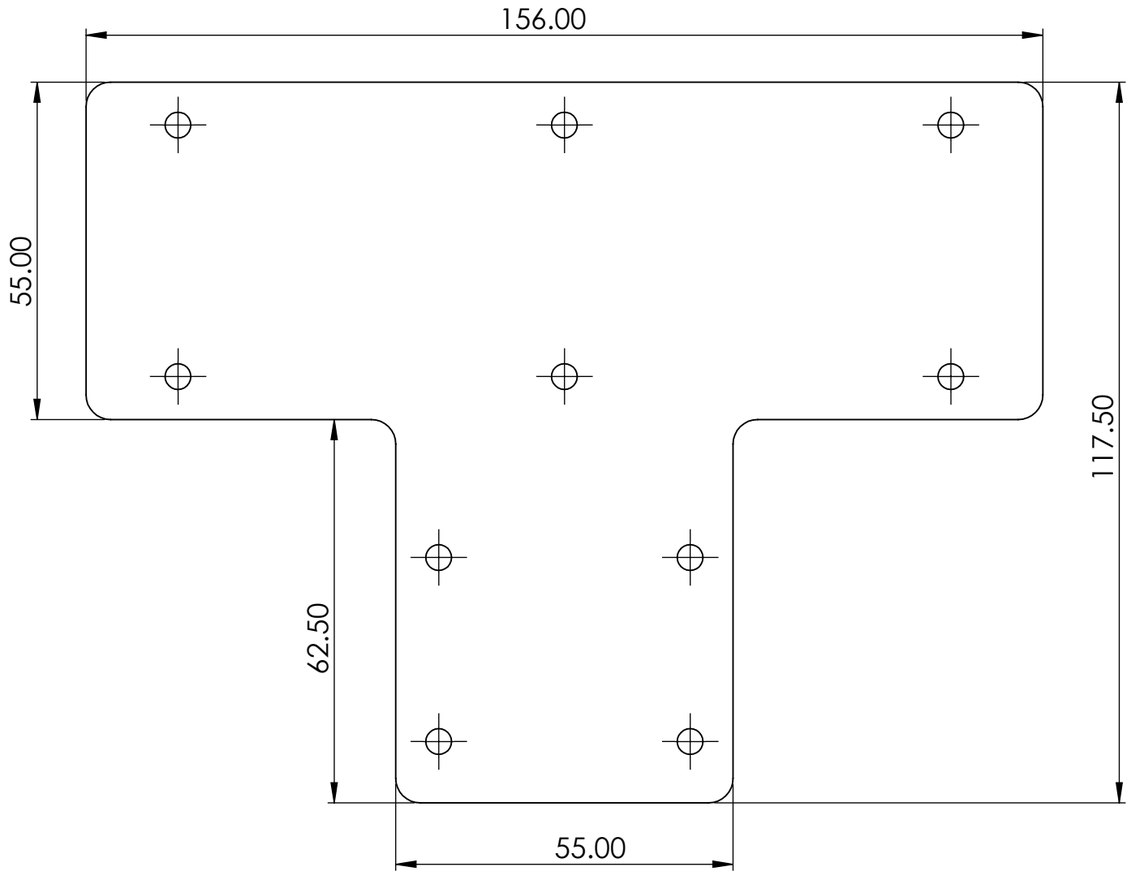


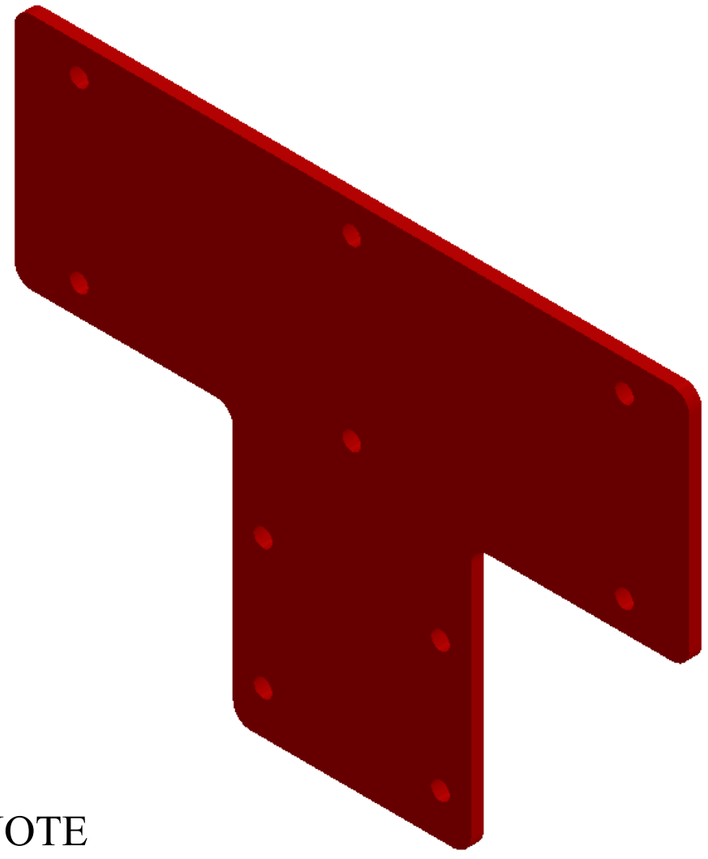



NOTE
T PLATE
LASER CUTTING

TITLE - ROOF AUTOMATION				NIHVA TECHNOLOGIES PVT.LTD.PUNE
DWG NO - NTPL-278-PM-001-01-05-05				Website - www.nihva.com
	NAME	SIGNATURE	DATE	PROJECT NO - NTPL-278-PM
DRAWN	V.W		15-05-25	PRODUCT - DOME
CHK'D	S.W.		15-05-25	SITE LOCATION - LONAVLA
APPV'D	V.T.		15-05-25	
if any queries contact - supportautomation@nihva.com				REVISION - 01 / QTY - 1
ALL DIMENSION ARE IN mm			A3	SCALE / SHEET 7 OF 20

ITEM NO.	PART NUMBER	DESCRIPTION	QTY.
1	..REV03REV 01New UPPER BEND VERTICAL SUPPORT Joining Plate		30
		Sheet	1

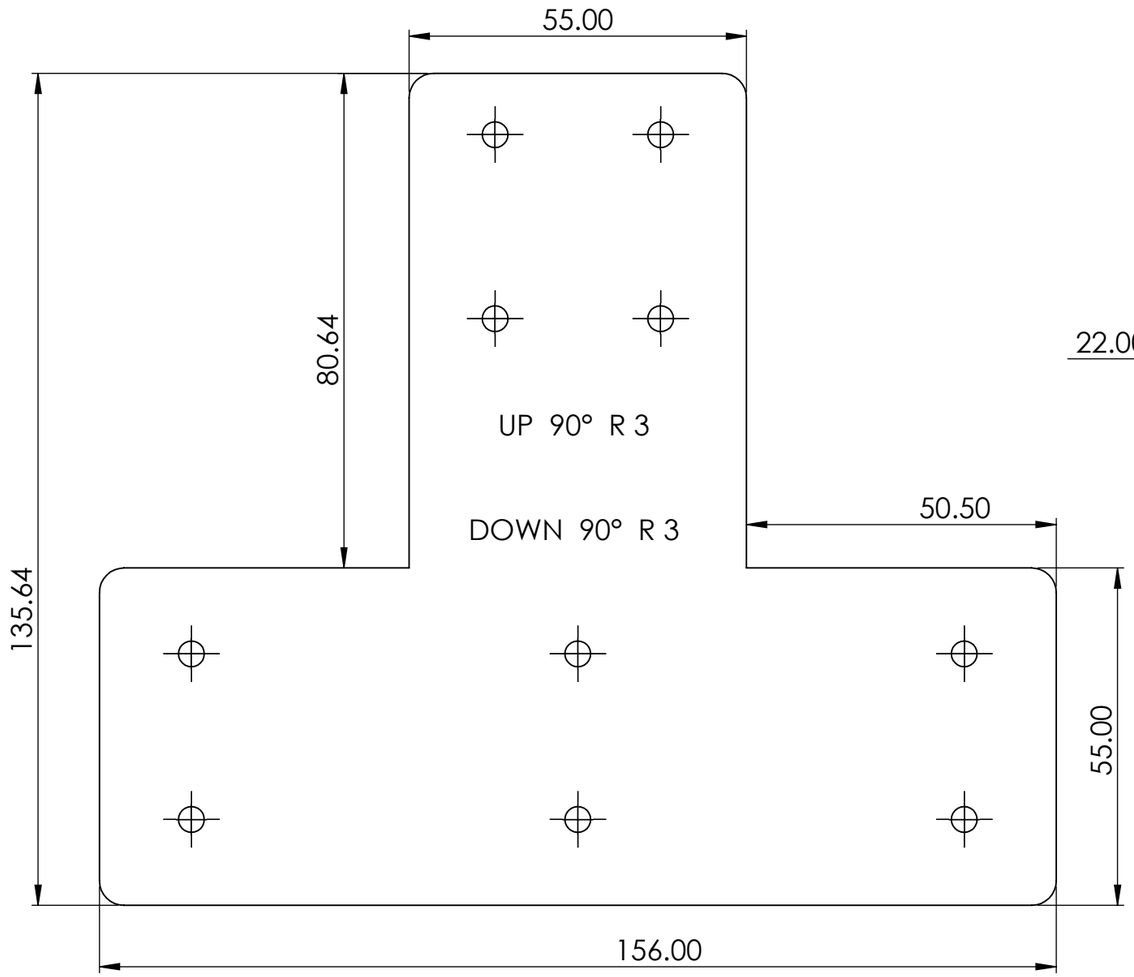

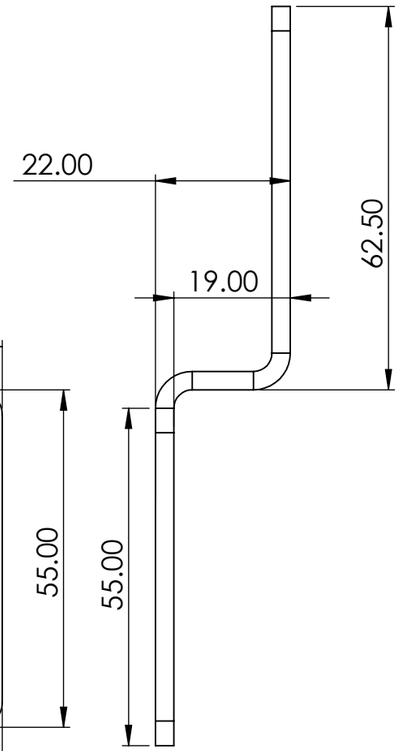


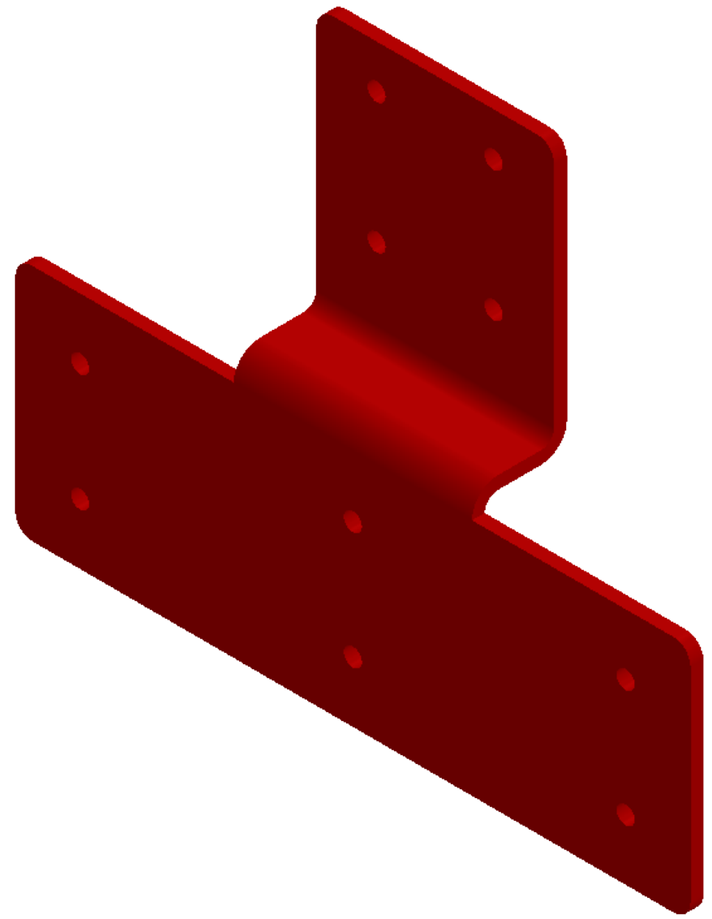



NOTE
NEW UPPER BEND VERTICAL SUPPORT JOINING PLATE
LASER CUTTING


TITLE - ROOF AUTOMATION				NIHVA TECHNOLOGIES PVT.LTD.PUNE
DWG NO - NTPL-278-PM-001-01-06-06				Website - www.nihva.com
	NAME	SIGNATURE	DATE	PROJECT NO - NTPL-278-PM
DRAWN	V.W		15-05-25	PRODUCT - DOME
CHK'D	S.W.		15-05-25	SITE LOCATION - LONAVLA
APPV'D	V.T.		15-05-25	
if any queries contact - supportautomation@nihva.com				REVISION - 01 / QTY - 1
ALL DIMENSION ARE IN mm		A3		SCALE / SHEET 8 OF 20


ITEM NO.	PART NUMBER	DESCRIPTION	QTY.
1	LOCKING PLATE INSIDE ASM	SS -304	20

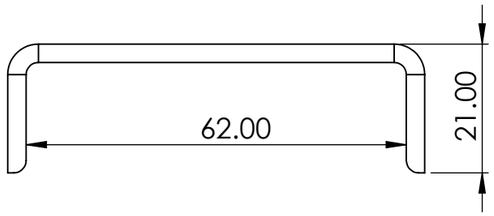

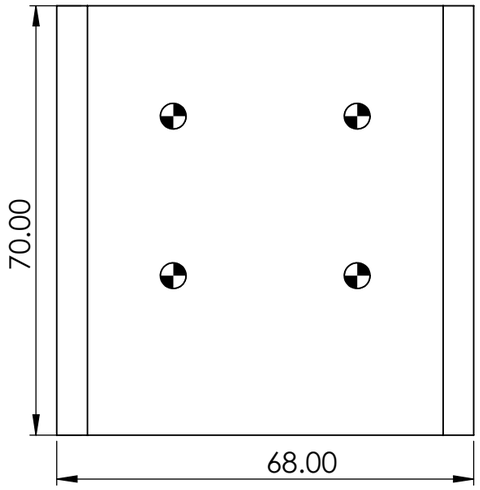

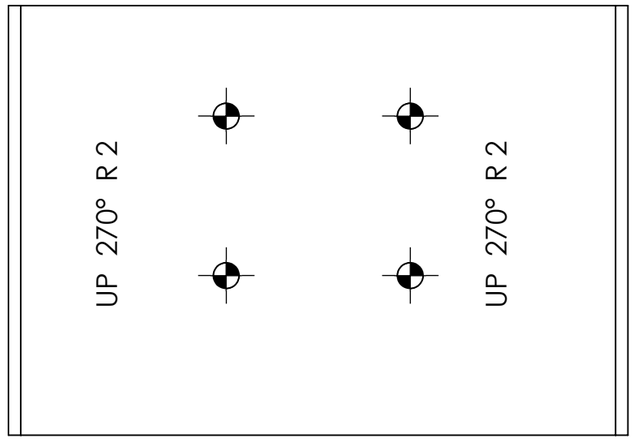

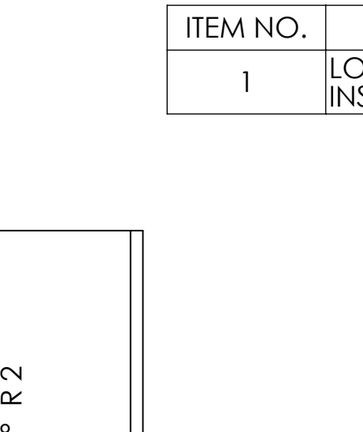


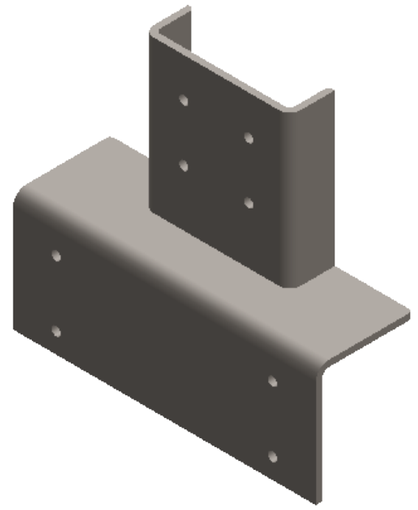

NOTE :
LOCKING PLATE
LASER CUTTING


TITLE - RETRACTABLE ROOF				NIHVA TECHNOLOGIES PVT.LTD.PUNE
DWG NO - NTPL-278-PM-001-01-07-07				Website - www.nihva.com
	NAME	SIGNATURE	DATE	PROJECT NO - NTPL-278-PM
DRAWN	V.W		15-05-25	PRODUCT - RETRACTABLE ROOF
CHK'D	S.W.		15-05-25	SITE LOCATION - LONAVLA
APPV'D	V.T.		15-05-25	
if any queries contact - supportautomation@nihva.com				REVISION - 01 / QTY - 1
ALL DIMENSION ARE IN mm			A3	SCALE / SHEET 9 OF 20


ITEM NO.	PART NUMBER	DESCRIPTION	QTY.
1	..REV03TOP RING SUPPORT	AL 6063_T4	2
2	..REV03VERTICAL SUPPORT ABOBE TOP RING 1	AL 6063_T4	8
3	..REV03TOP VERTICAL SUPPORT 2	AL 6063_T4	15
4	..REV03POLYGOANL SHAPE BY WELDIND	AL 6063_T4	1
5	..REV03POLYCARBO NET SHEET2	POLYCARBONET	8
6	..REV03New upper plus bend plate	SS-304	8
7	..REV03PLUS PLATE ASM	SS-304	8
8	..REV03REV 02VIJAY_T PLATE ASM	SS 304	8
9	..REV03POLYCARBO NET SHEET3	POLYCARBONET	8
10	..MESH	SS	1
11	..VERTICAL TUBE FOR CAP SHAPE SUPPORT MS-60*30*1.5MM THK	MS	6
12	T PLATE	SS304 -117.5X156X3 MM THK	8
13	..REV03REV 01New UPPER BEND VERTICAL SUPPORT Joining Plate	SS 304 - 135.64*156*3MM THK	8

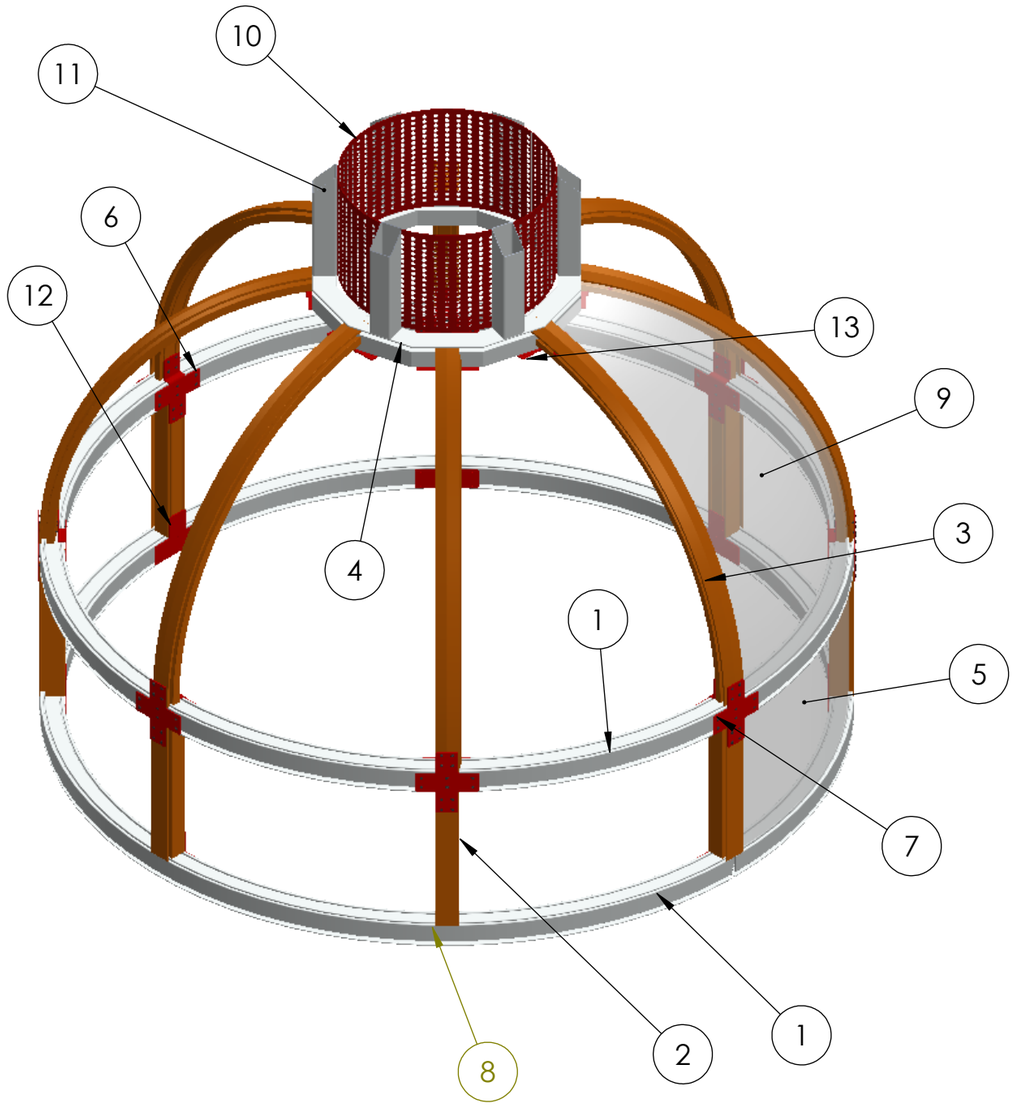

TITLE - RETRACTABLE ROOF				NIHVA TECHNOLOGIES PVT.LTD.PUNE
DWG NO - NTPL-278-PM-001-00-00-00				Website - www.nihva.com
	NAME	SIGNATURE	DATE	PROJECT NO - NTPL-278-PM
DRAWN	V.W		28-04-2025	PRODUCT - RETRACTABLE ROOF
CHK'D	S.W.		28-04-2025	SITE LOCATION - LONAVLA
APPV'D	V.T.		28-04-2025	
if any queries contact - supportautomation@nihva.com				REVISION - QTY - 1
ALL DIMENSION ARE IN mm			A3	SCALE SHEET 10 OF 20

ITEM NO.	PART NUMBER	DESCRIPTION	QTY.
1	..REV03VERTICAL SUPPORT ABOBE TOP RING 1	AL 6063_T4	8

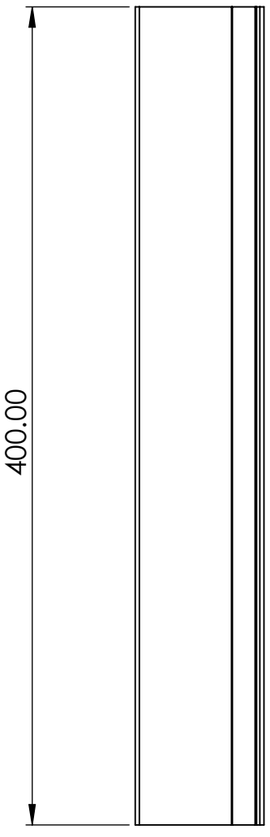


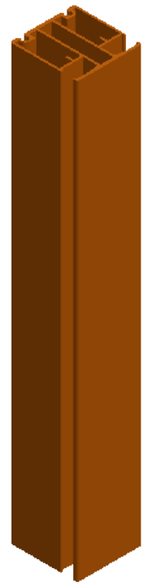

NOTE
VERTICAL SUPPORT ABOBE TOP RING 1
USE PROFILE GNT-006

TITLE - ROOF AUTOMATION				NIHVA TECHNOLOGIES PVT.LTD.PUNE
DWG NO - NTPL-278-PM-001-02-02-02				Website - www.nihva.com
	NAME	SIGNATURE	DATE	PROJECT NO - NTPL-278-PM
DRAWN	V.W		15-05-25	PRODUCT - DOME
CHK'D	S.W.		15-05-25	SITE LOCATION - LONAVLA
APPV'D	V.T.		15-05-25	
if any queries contact - supportautomation@nihva.com				REVISION - 01 / QTY - 1
ALL DIMENSION ARE IN mm			A3	SCALE / SHEET 11 OF 20

ITEM NO.	PART NUMBER	DESCRIPTION	QTY.
1	..REV03TOP VERTICAL SUPPORT 2	AL 6063_T4	8

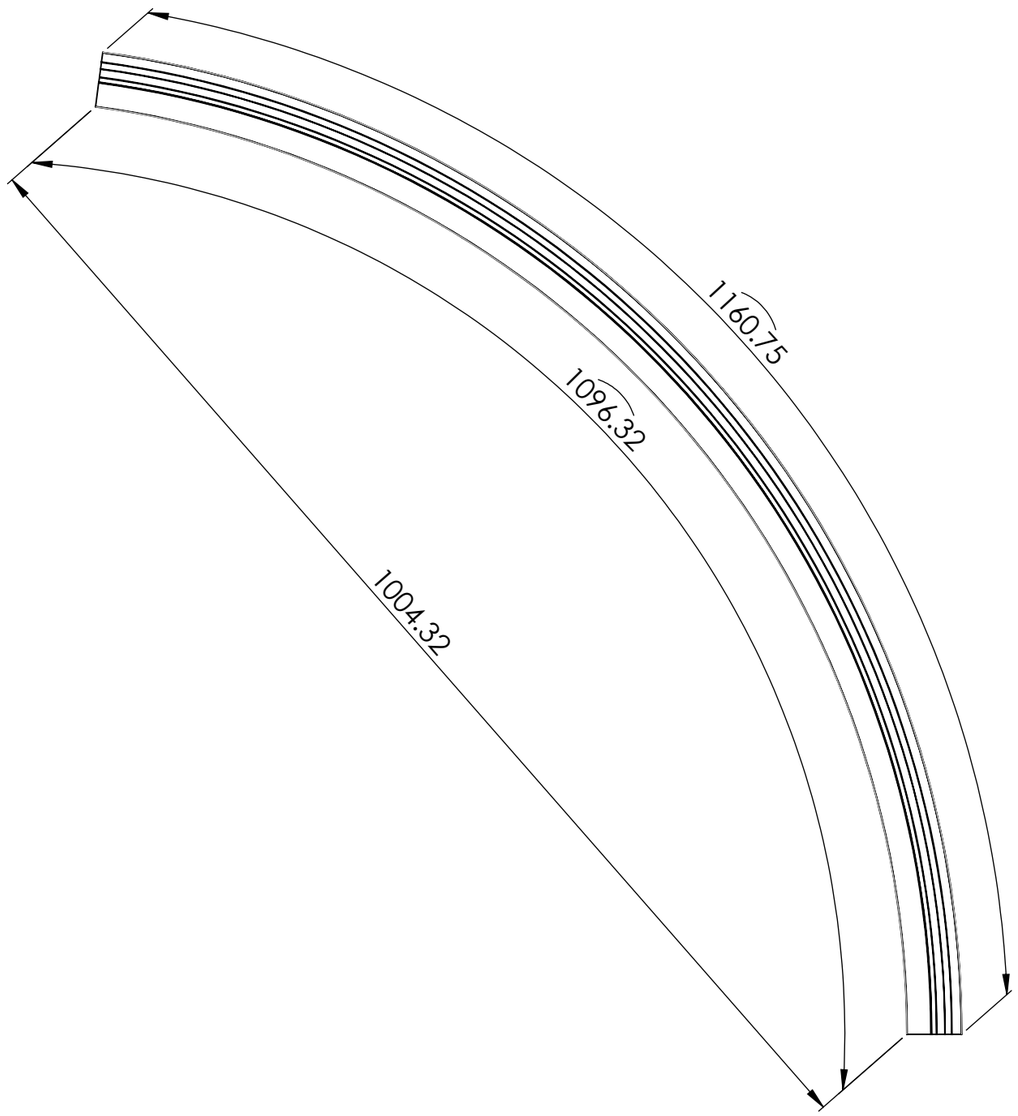





NOTE
VERTICAL SUPPORT 2
USE PROFILE GNT-009

TITLE - ROOF AUTOMATION				NIHVA TECHNOLOGIES PVT.LTD.PUNE
DWG NO - NTPL-278-PM-001-02-03-03				Website - www.nihva.com
	NAME	SIGNATURE	DATE	PROJECT NO - NTPL-278-PM
DRAWN	V.W		15-05-25	PRODUCT - DOME
CHK'D	S.W.		15-05-25	SITE LOCATION - LONAVLA
APPV'D	V.T.		15-05-25	
if any queries contact - supportautomation@nihva.com				REVISION - 01 / QTY - 1
ALL DIMENSION ARE IN mm			A3	SCALE / SHEET 12 OF 20

ITEM NO.	PART NUMBER	DESCRIPTION	QTY.
1	..REV03POLYGOANL SHAPE BY WELDIND	AL 6063_T4	1

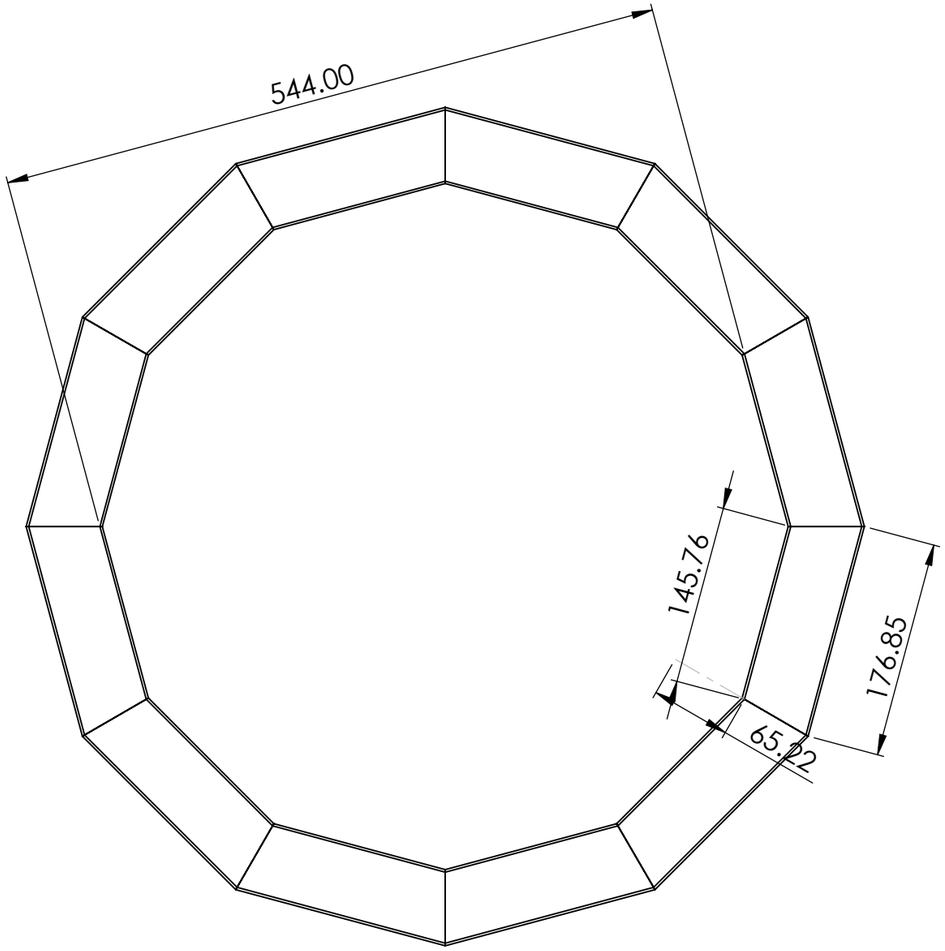


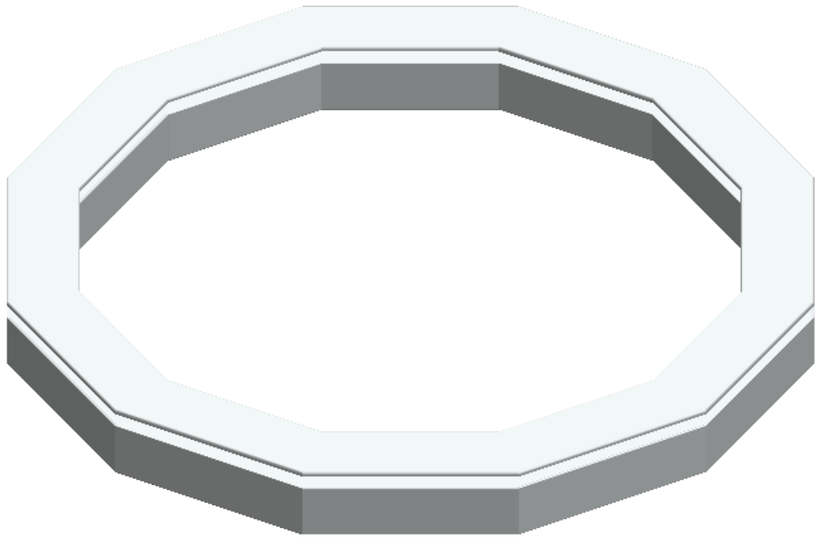



NOTE
POLYGONAL SHAPE BY WELDING
USE PROFILE GNT-006

TITLE - ROOF AUTOMATION				NIHVA TECHNOLOGIES PVT.LTD.PUNE
DWG NO - NTPL-278-PM-001-02-04-04				Website - www.nihva.com
	NAME	SIGNATURE	DATE	PROJECT NO - NTPL-278-PM
DRAWN	V.W		15-05-25	PRODUCT - DOME
CHK'D	S.W.		15-05-25	SITE LOCATION - LONAVLA
APPV'D	V.T.		15-05-25	
if any queries contact - supportautomation@nihva.com				REVISION - 01 / QTY - 1
ALL DIMENSION ARE IN mm		A3		SCALE / SHEET 13 OF 20

ITEM NO.	PART NUMBER	DESCRIPTION	QTY.
1	..REV03New Upper Plus bend plate	SS 304 - 197.14*156*3MM THK	8
2	..REV03VIJAY_Rivet_iso_15977_4_x_16_0	RIVET M4X16	14

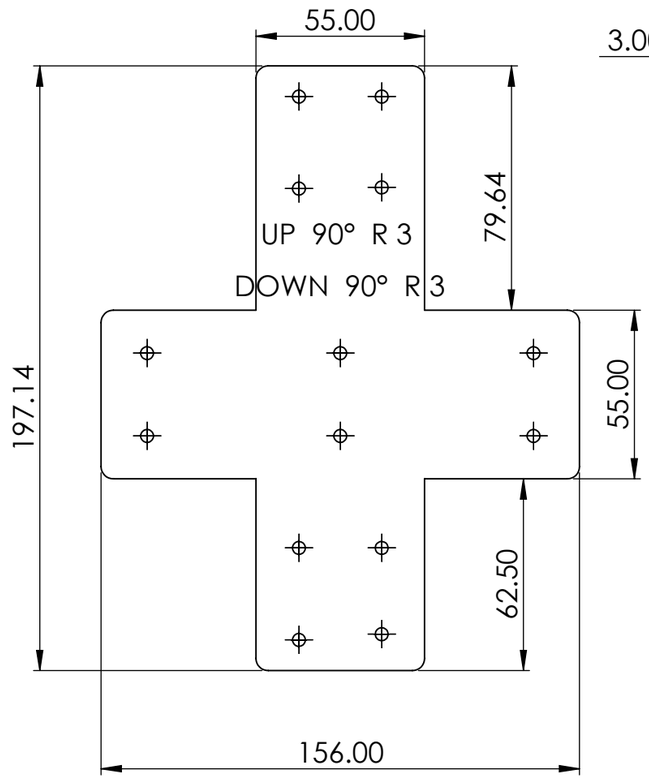

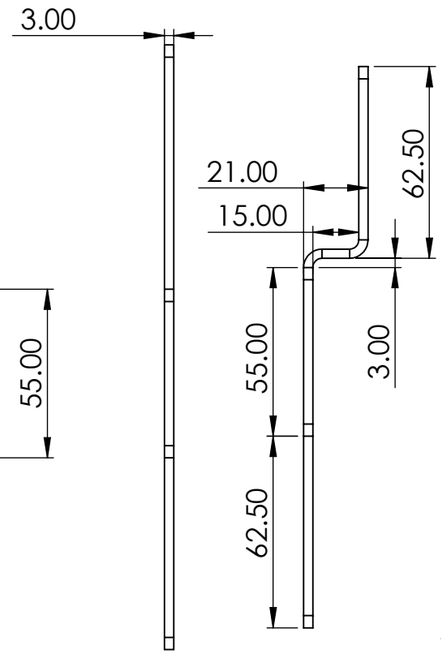


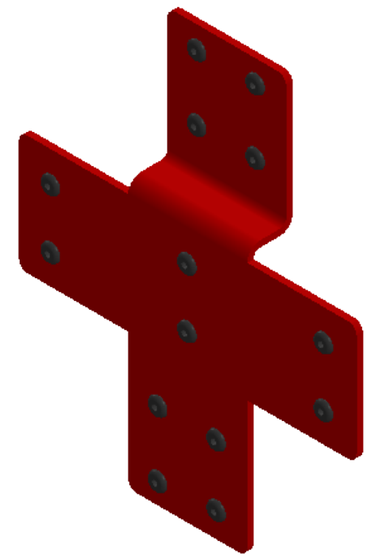


NOTE
NEW UPPER PLUS BEND PLATE
LASER CUTTING

TITLE - ROOF AUTOMATION				NIHVA TECHNOLOGIES PVT.LTD.PUNE
DWG NO - NTPL-278-PM-001-02-06-06				Website - www.nihva.com
	NAME	SIGNATURE	DATE	PROJECT NO - NTPL-278-PM
DRAWN	V.W		15-05-25	PRODUCT - DOME
CHK'D	S.W.		15-05-25	SITE LOCATION - DOME
APPV'D	V.T.		15-05-25	
if any queries contact - supportautomation@nihva.com				REVISION - 01 / QTY - 1
ALL DIMENSION ARE IN mm		A3		SCALE / SHEET 14 OF 20

ITEM NO.	PART NUMBER	DESCRIPTION	QTY.
1	..REV03NEW PIUS PALTE	SS 304 - 180*156*3MM THK	8
2	..REV03VIJAY_Rivet_iso_15977_4_x_16_0	RIVET M4X16	14

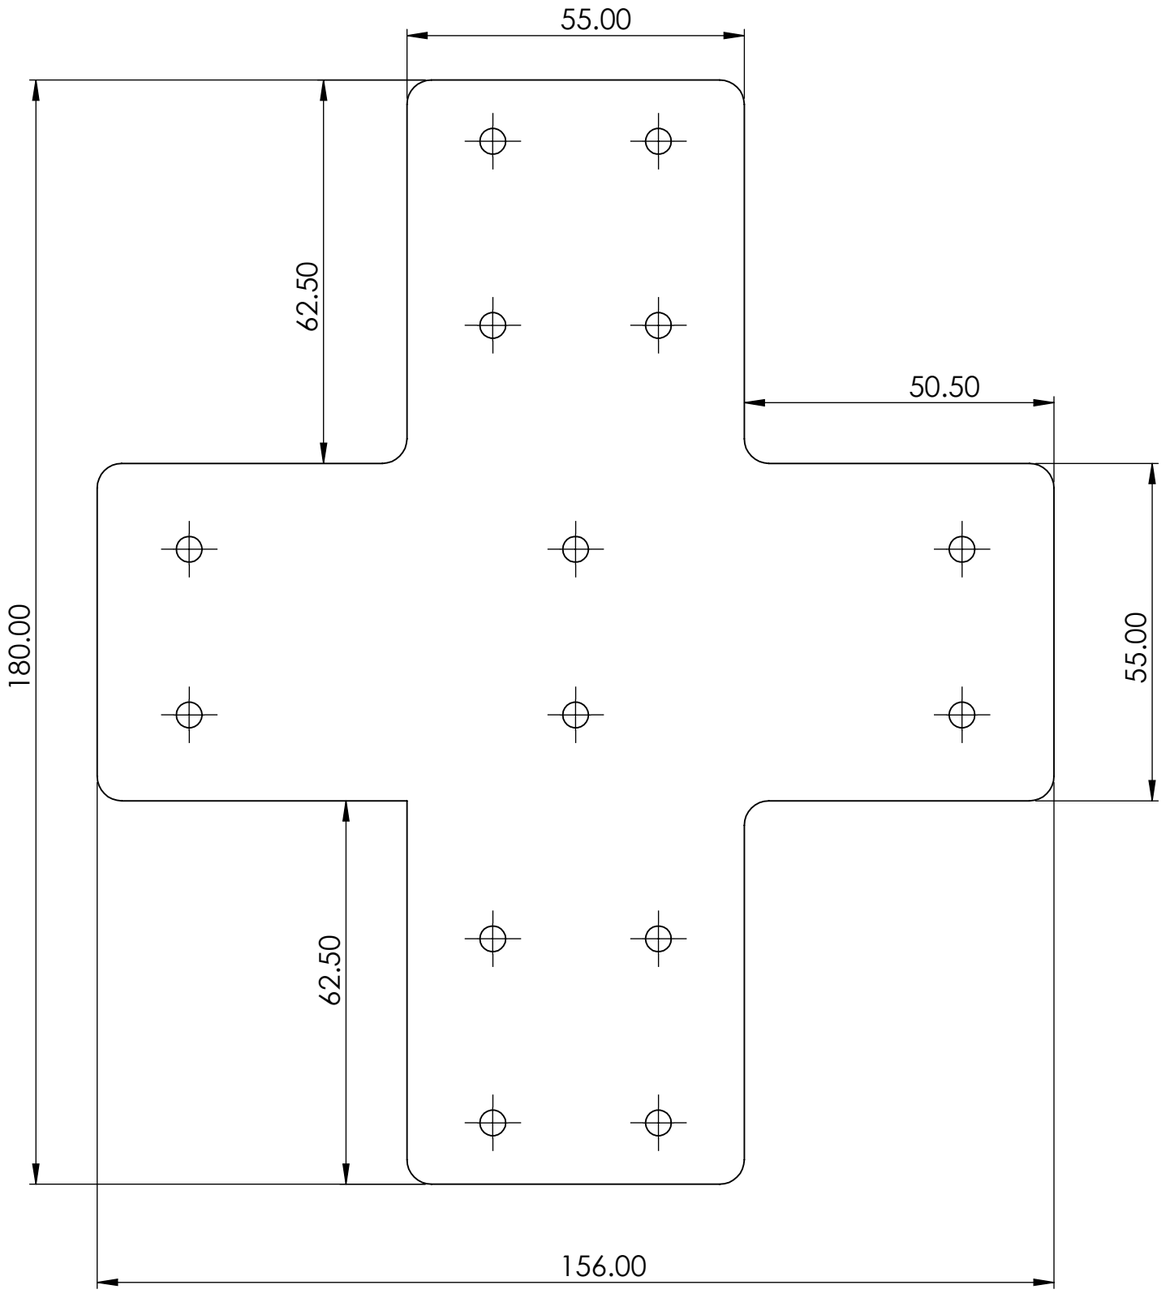


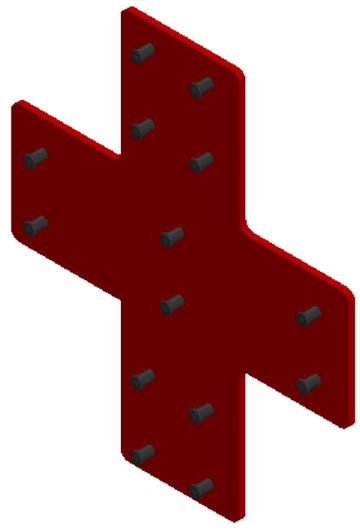



NOTE
NEW PLUS PLATE
LASER CUTTING

TITLE - ROOF AUTOMATION				NIHVA Technologies Pvt. Ltd.	NIHVA TECHNOLOGIES PVT.LTD.PUNE Website - www.nihva.com
DWG NO - NTPL-278-PM-001-02-07-07					
	NAME	SIGNATURE	DATE	PROJECT NO - NTPL-278-PM	
DRAWN	V.W		15-05-25	PRODUCT - DOME	
CHK'D	S.W.		15-05-25	SITE LOCATION - LONAVLA	
APPV'D	V.T.		15-05-25		
if any queries contact - supportautomation@nihva.com				REVISION - 01	QTY - 1
ALL DIMENSION ARE IN mm		A3		SCALE	SHEET 15 OF 20

ITEM NO.	PART NUMBER	DESCRIPTION	QTY.
1	..MESH	SS	1
		Sheet	1

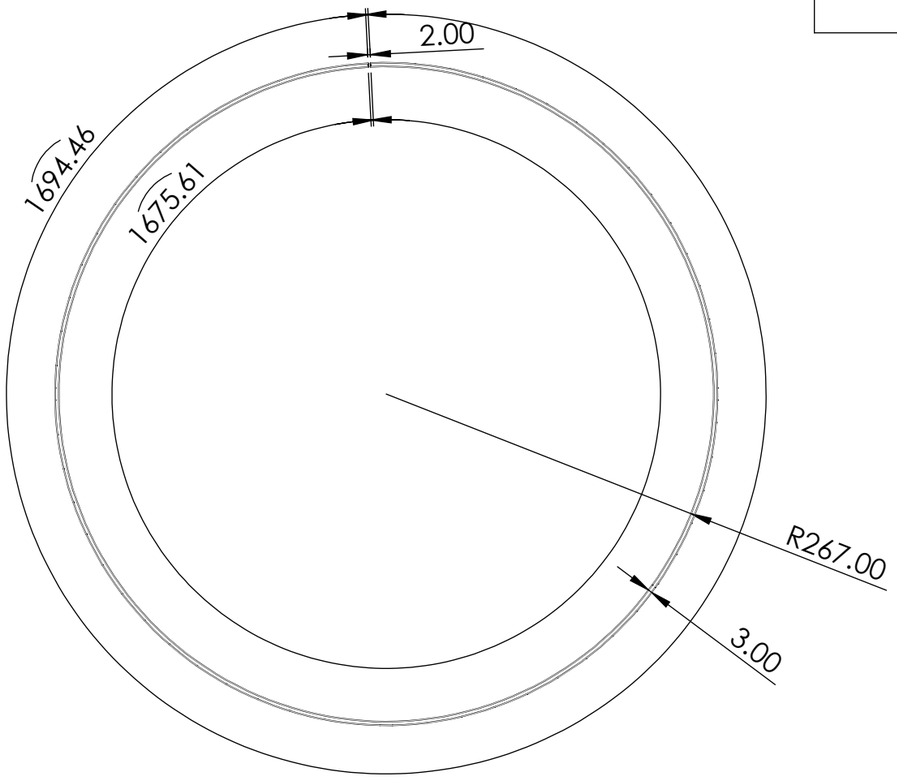


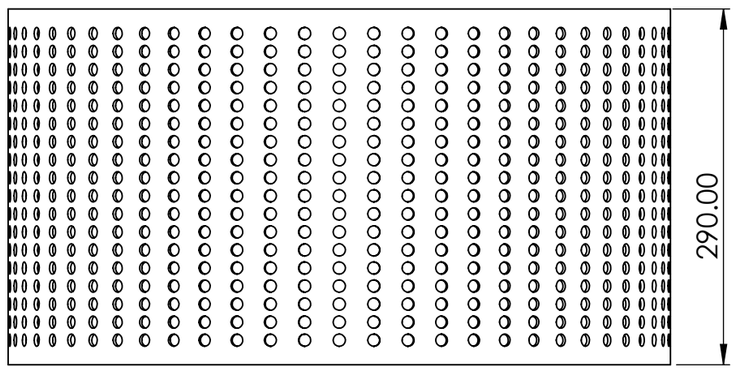

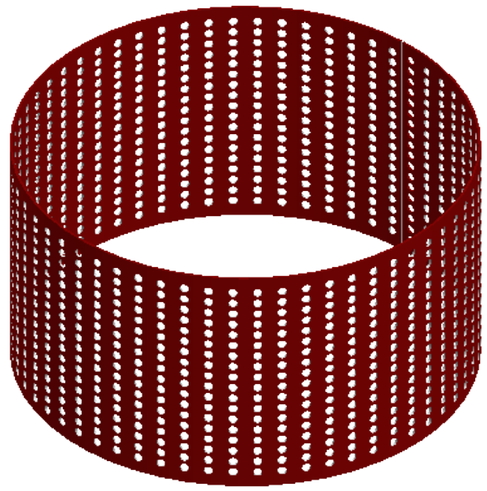


NOTE
MESH
THIS MESH IS PROVIDED FOR VENTIALTION

TITLE - ROOF AUTOMATION				NIHVA TECHNOLOGIES PVT.LTD.PUNE
DWG NO - NTPL-278-PM-001-02-10-10				Website - www.nihva.com
	NAME	SIGNATURE	DATE	PROJECT NO - NTPL-278-PM
DRAWN	V.W		15-05-25	PRODUCT - DOME
CHK'D	S.W.		15-05-25	SITE LOCATION - LONAVLA
APPV'D	V.T.		15-05-25	
if any queries contact - supportautomation@nihva.com				REVISION - 01 / QTY - 1
ALL DIMENSION ARE IN mm		A3		SCALE / SHEET 16 OF 20

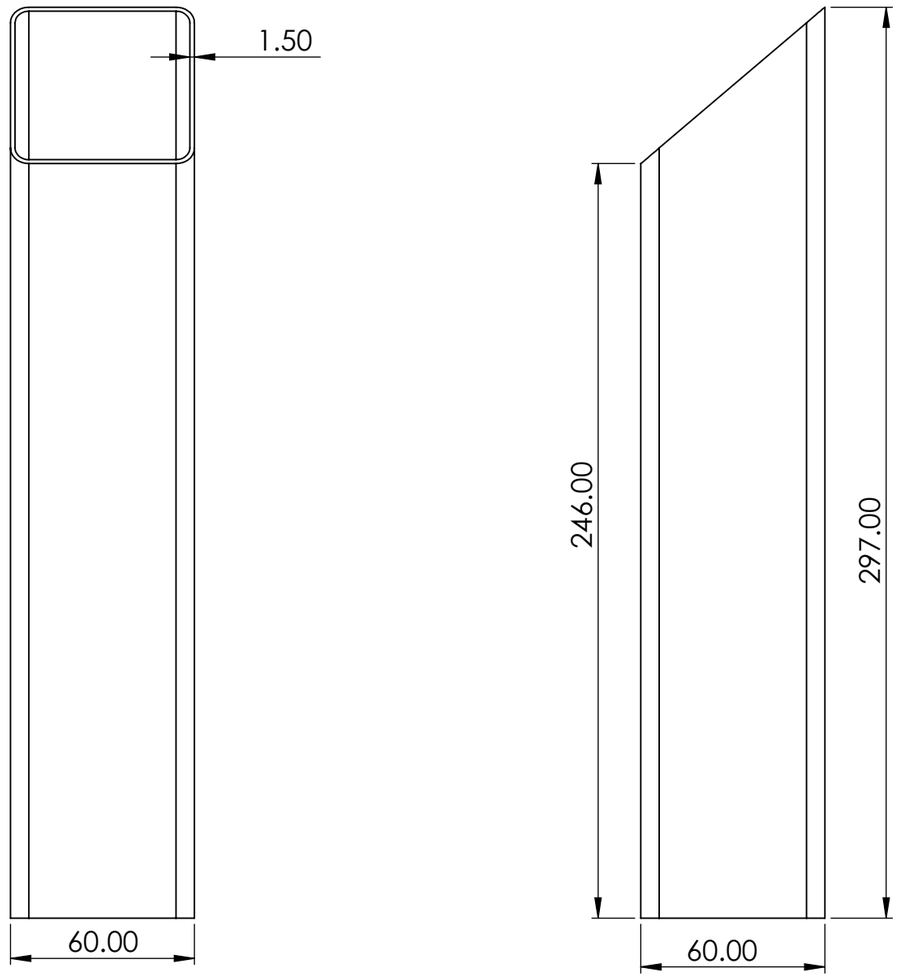


ITEM NO.	PART NUMBER	DESCRIPTION	QTY.
1	..VERTICAL TUBE FOR CAP SHAPE SUPPORT MS-60*30*1.5MM THK	MS	6
		TUBE, SQUARE 60.000000 X 60.000000 X 1.500000	1

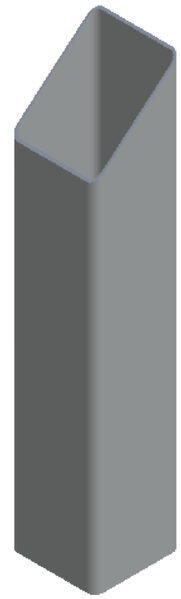

NOTE
VERTICAL TIBE CAP SUPPORT
MS -60*60*1.5MM THK

TITLE - ROOF AUTOMATIOM				NIHVA TECHNOLOGIES PVT.LTD.PUNE
DWG NO - NTPL-278-PM-001-02-11-11				Website - www.nihva.com
	NAME	SIGNATURE	DATE	PROJECT NO - NTPL-278-PM
DRAWN	V.W		15-05-25	PRODUCT - DOME
CHK'D	S.W.		15-05-25	SITE LOCATION - LONAVLA
APPV'D	V.T.		15-05-25	
if any queries contact - supportautomation@nihva.com				REVISION - 01 / QTY - 1
ALL DIMENSION ARE IN mm		A3		SCALE / SHEET 17 OF 20


ITEM NO.	PART NUMBER	DESCRIPTION	QTY.
1	..HEXAGONAL SAHPE MS 60*30*1.5MM THK	MS	1
2	..TOP CONE SHAPE VERTICAL TUBE	MS	6
3	..TOP CAP PC SHEET	POLYCARBONET	6
11	T PLATE	SS304 -117.5X156X3 MM THK	1
12	..REV03REV 01New UPPER BEND VERTICAL SUPPORT Joining Plate	SS 304 - 135.64*156*3MM THK	1

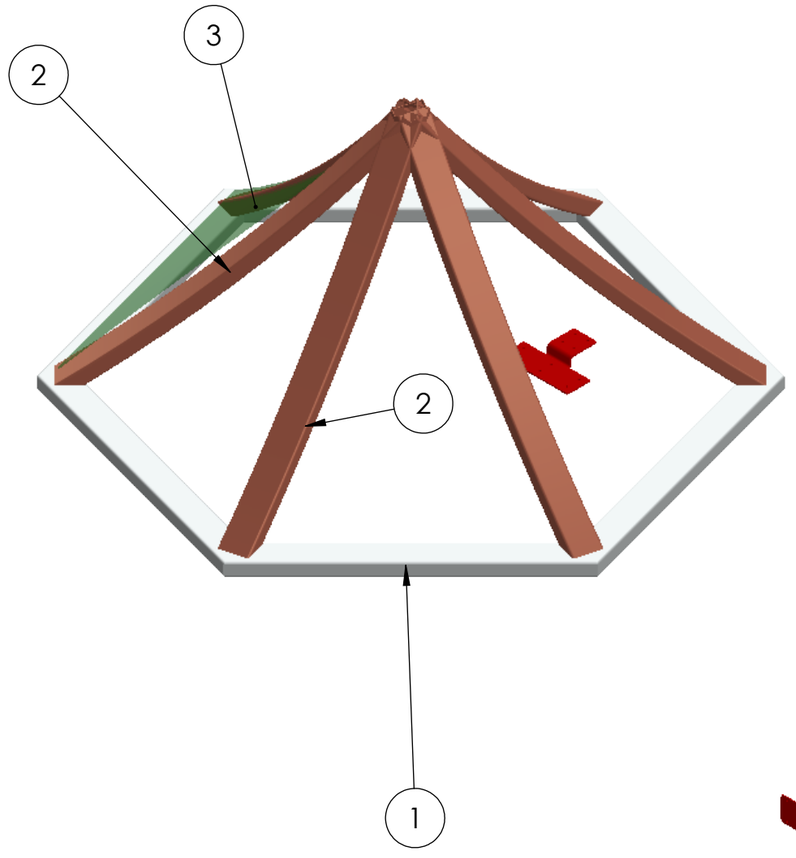


NOTE:
DOME CAP ISO VIEW
ALL MADE UP MS TUBE
SUB ASSEMBLY NO 03

TITLE - RETRACTABLE ROOF				NIHVA TECHNOLOGIES PVT.LTD.PUNE
DWG NO - NTPL-278-PM-001-00-00-00				Website - www.nihva.com
	NAME	SIGNATURE	DATE	PROJECT NO - NTPL-278-PM
DRAWN	V.W		28-04-2025	PRODUCT - RETRACTABLE ROOF
CHK'D	S.W.		28-04-2025	SITE LOCATION - LONAVLA
APPV'D	V.T.		28-04-2025	
if any queries contact - supportautomation@nihva.com				REVISION - QTY - 1
ALL DIMENSION ARE IN mm		A3		SCALE SHEET 18 OF 20

ITEM NO.	PART NUMBER	DESCRIPTION	QTY.
1	..HEXAGONAL SAHPE MS 60*30*1.5MM THK	MS	1

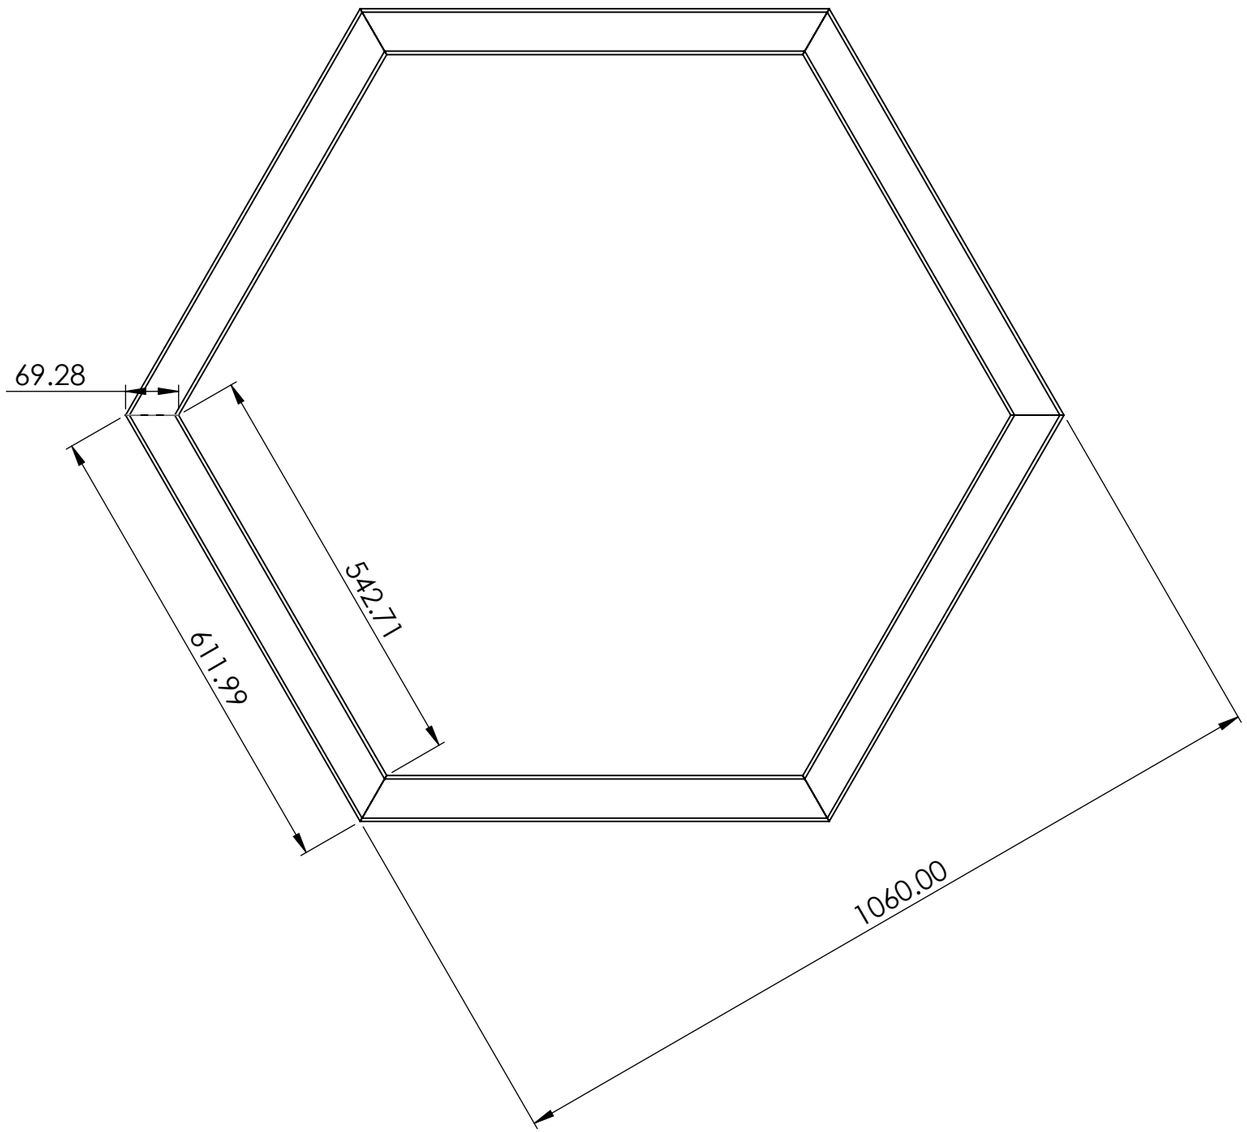


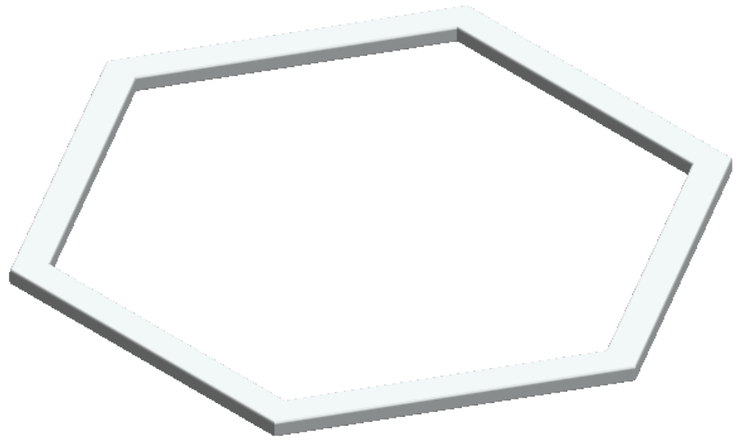


NOTE
HEXAGONAL SHAPE BY WELDIND
MS - 60*30*1.5MM THK

TITLE -ROOF AUTOMATION				NIHVA TECHNOLOGIES PVT.LTD.PUNE Website - www.nihva.com	
DWG NO - NTPL-278-PM-001-03-01-01					
	NAME	SIGNATURE	DATE	PROJECT NO - NTPL-278-PM	
DRAWN	V.W		15-05-25	PRODUCT - DOME	
CHK'D	S.W.		15-05-25	SITE LOCATION - LONAVLA	
APPV'D	V.T.		15-05-25		
if any queries contact - supportautomation@nihva.com				REVISION - 01	QTY - 1
ALL DIMENSION ARE IN mm			A3	SCALE	SHEET 19 OF 20

ITEM NO.	PART NUMBER	DESCRIPTION	QTY.
1	..VERTICAL TUBE FOR CAP SHAPE SUPPORT MS 60*30*1.5MM THK	MS	6

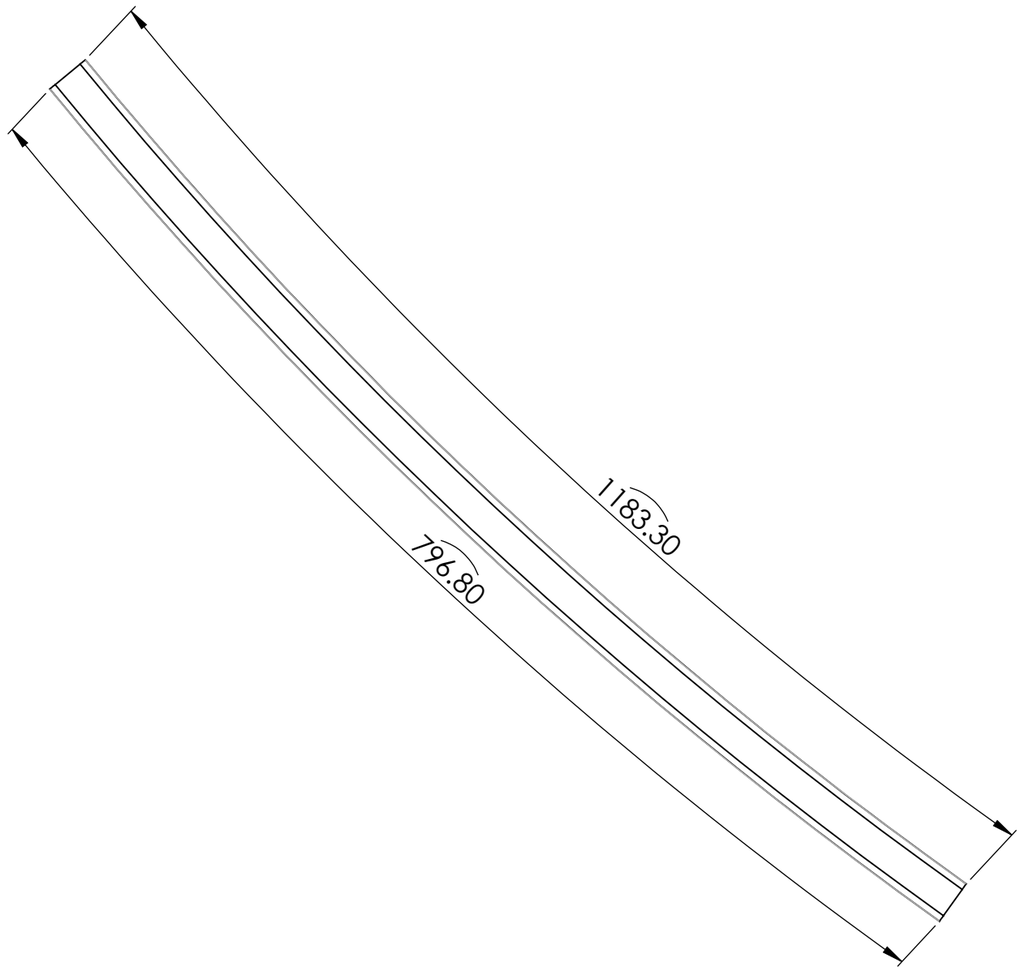

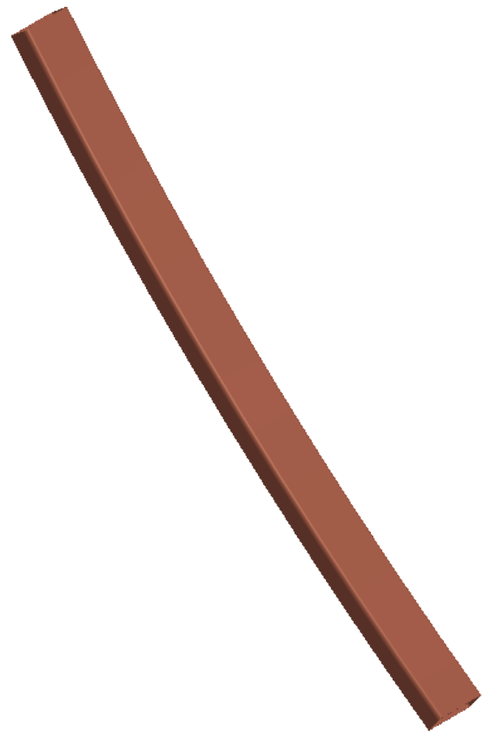

NOTE
CAP VERTICAL SUPPORT SQ TUBE
MS - 60*30*1.5M THK

TITLE - ROOF AUTOMATION				NIHVA TECHNOLOGIES PVT.LTD.PUNE	
DWG NO - NTPL-278-PM-001-03-02-02				Website - www.nihva.com	
	NAME	SIGNATURE	DATE	PROJECT NO - NTPL-278-PM	
DRAWN	V.W		15-05-25	PRODUCT - DOME	
CHK'D	S.W.		15-05-25	SITE LOCATION - LONAVLA	
APPV'D	V.T.		15-05-25		
if any queries contact - supportautomation@nihva.com				REVISION - 01	QTY - 1
ALL DIMENSION ARE IN mm		A3		SCALE	SHEET 20 OF 20