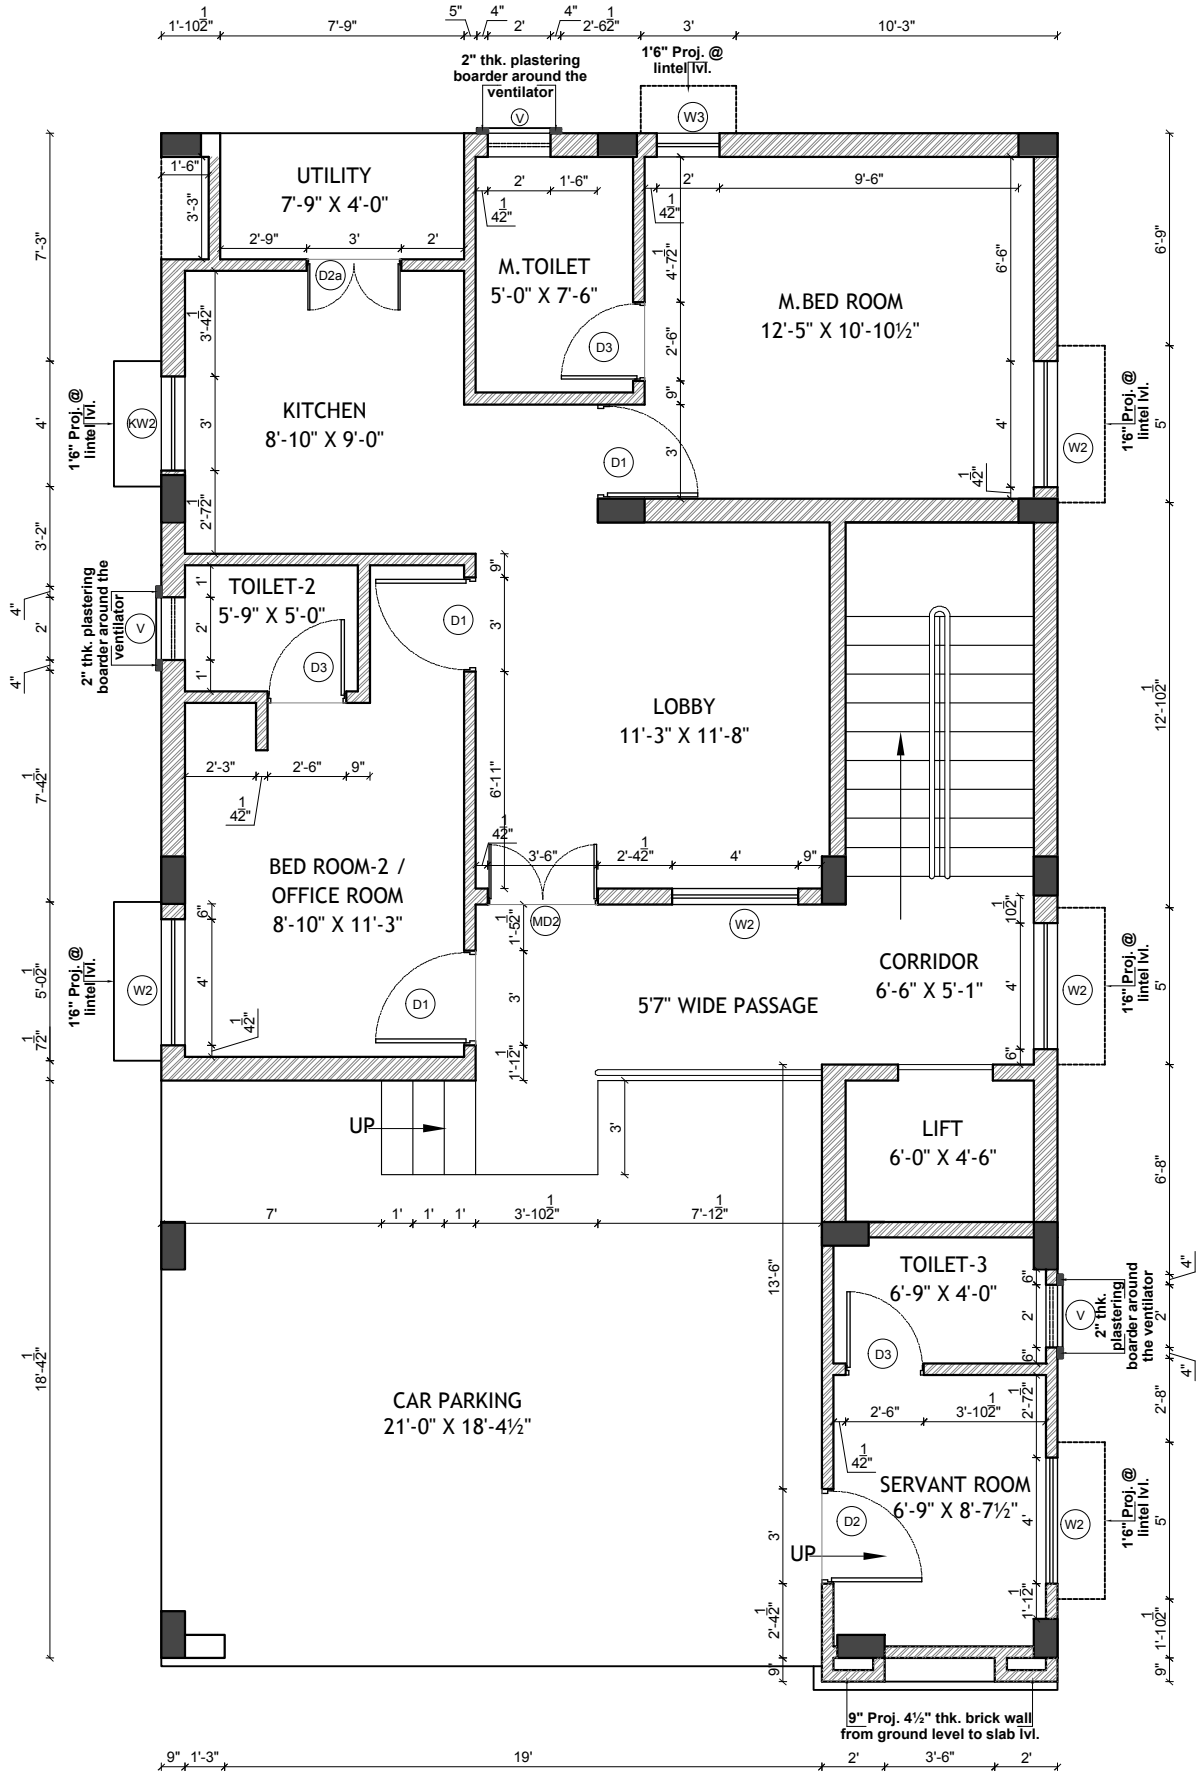


General Notes
1. This design & drawings are property of ARK Architects & interior designers. 2. All dimensions are in feet and inches, unless otherwise specified. 3. In case of any discrepancy, immediately notify the Architect. 4. Only written dimensions are to be followed. Do not scale the drawing. 5. Please refer the Coordinated drawings. 6. This drawing shall supercede its previous revisions if any.


Revisions		
No.	Revision/Issue	Date

Type of Drawing :

Project No:
2021_014
Sheet Title :
GROUND FLOOR BRICK MARKING PLAN
Project & Location:
Dr. PRAVEEN RESIDENCE @ TAGARAPUVALASA

Date:	Scale:
20-08-2021	NTS
Orientation:	Sheet no:
NORTH N	**A-501**

Checked by :	JN
Drafted by :	Rama

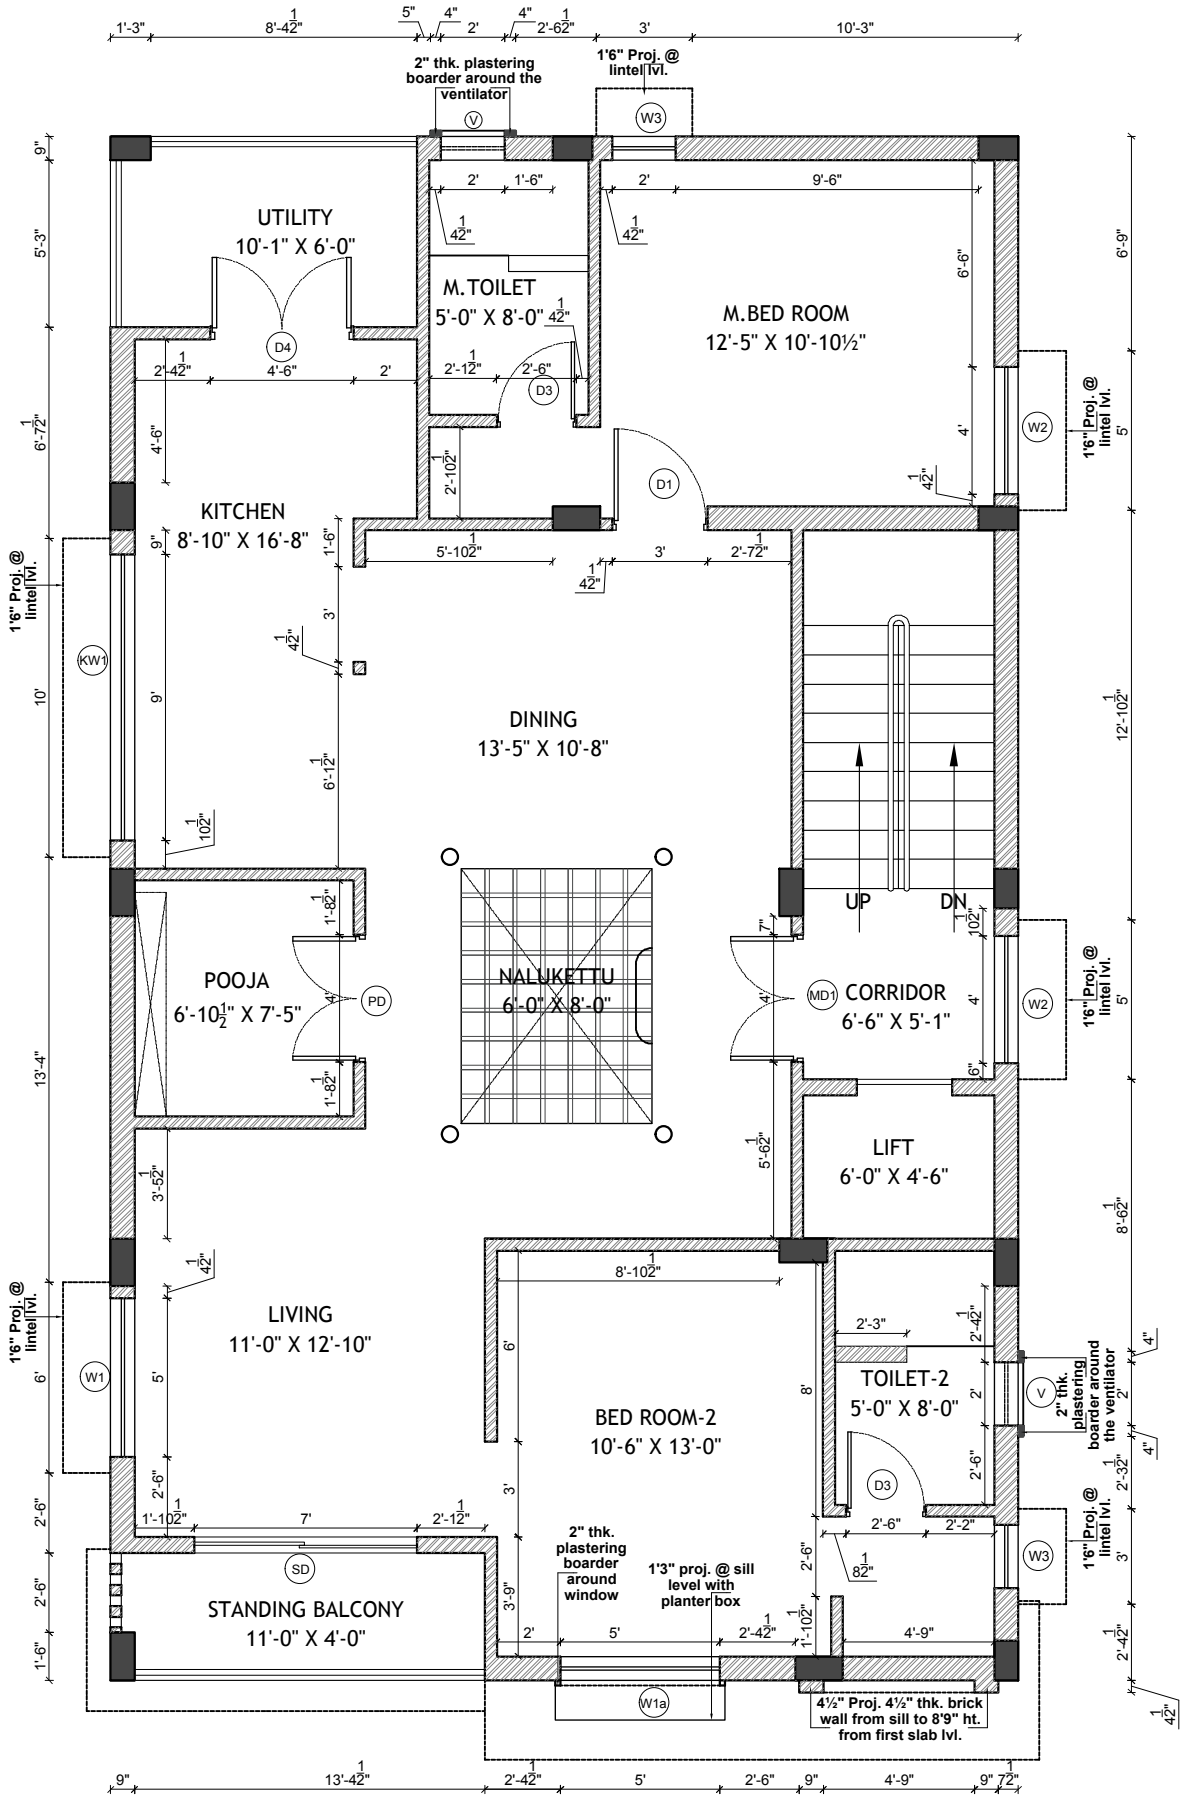

General Notes
1. This design & drawings are property of ARK Architects & interior designers.
2. All dimensions are in feet and inches, unless otherwise specified.
3. In case of any discrepancy, immediately notify the Architect.
4. Only written dimensions are to be followed. Do not scale the drawing.
5. Please refer the Coordinated drawings.
6. This drawing shall supercede its previous revisions if any.


Revisions		
No.	Revision/Issue	Date

Type of Drawing :

Project No:	2021_014
Sheet Title :	FIRST FLOOR BRICK MARKING PLAN
Project & Location:	Dr. PRAVEEN RESIDENCE @ TAGARAPUVALASA

Date:	20-08-2021
Scale:	NTS
Orientation:	NORTH
Sheet no:	A-502

Checked by :	JN
Drafted by :	Rama

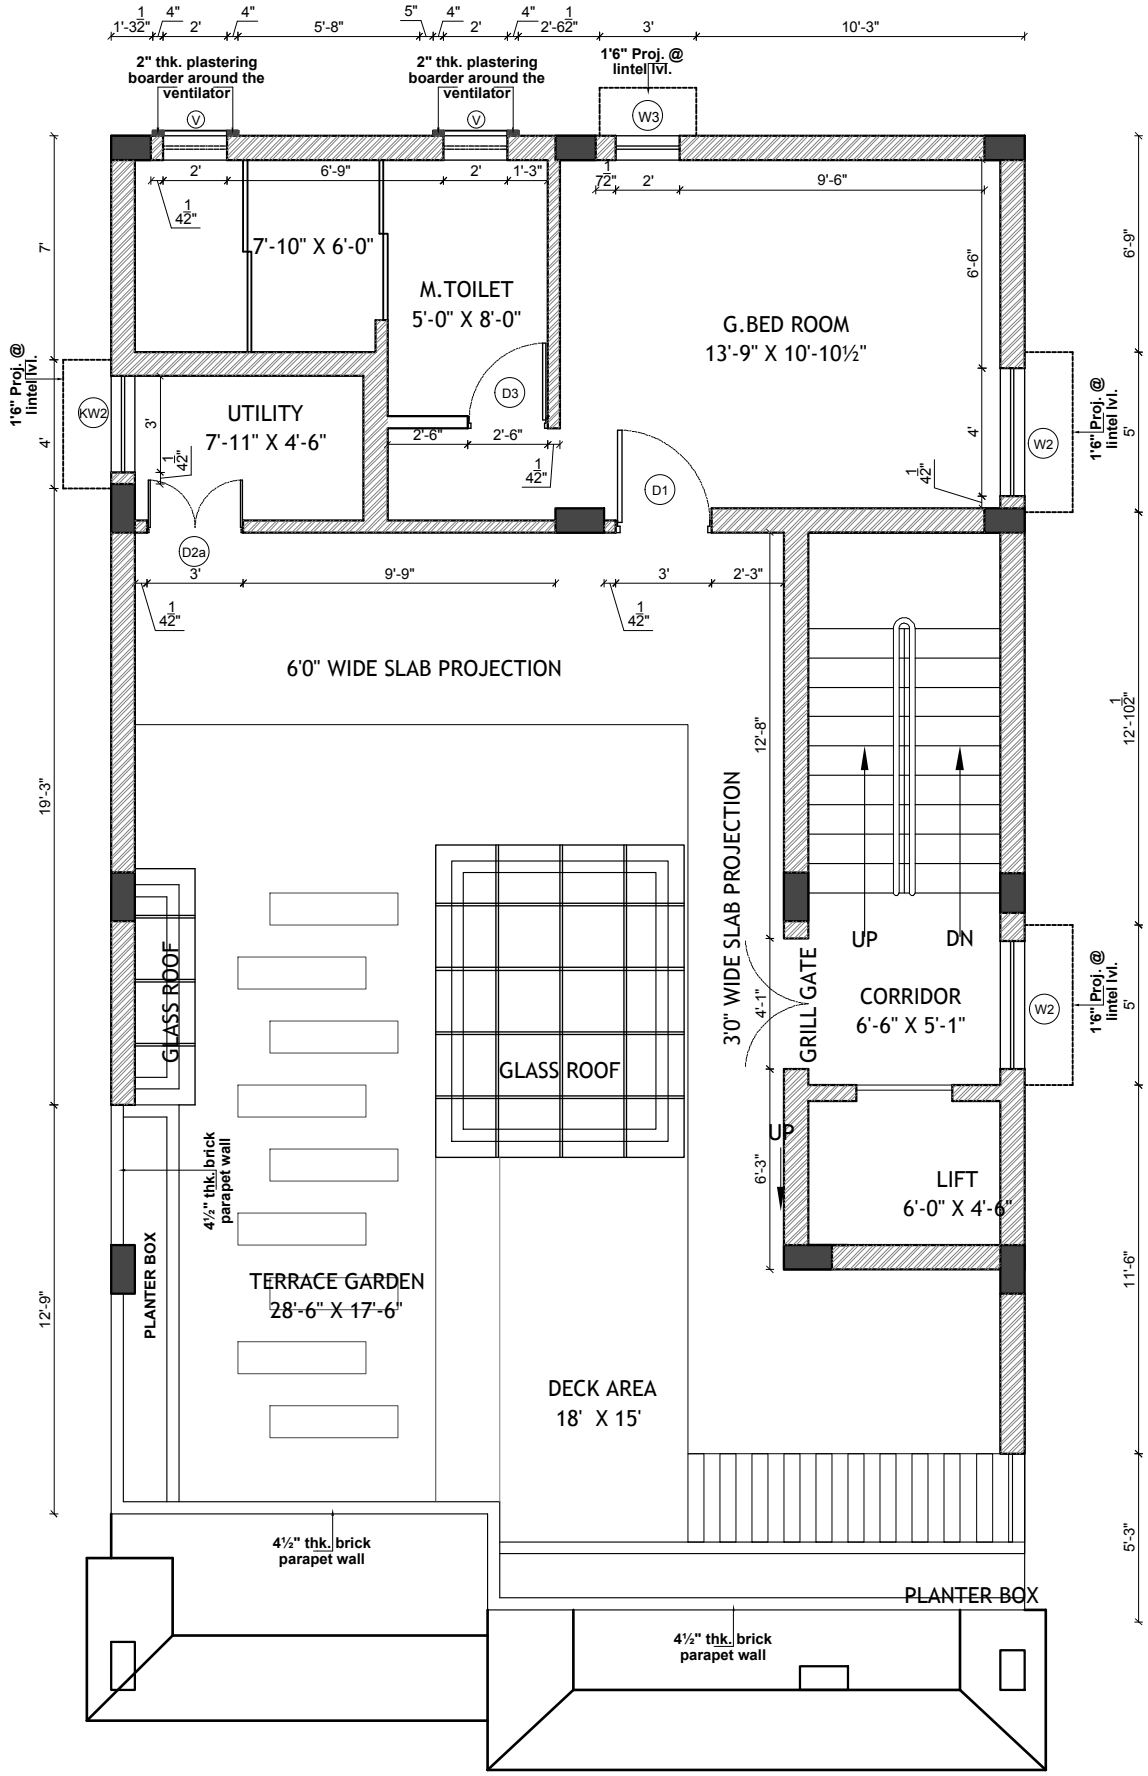

General Notes

1. This design & drawings are property of ARK Architects & interior designers.
2. All dimensions are in feet and inches, unless otherwise specified.
3. In case of any discrepancy, immediately notify the Architect.
4. Only written dimensions are to be followed. Do not scale the drawing.
5. Please refer the Coordinated drawings.
6. This drawing shall supercede its previous revisions if any.

Revisions		
No.	Revision/Issue	Date

Type of Drawing :


Project No: 2021_014

Sheet Title : **SECOND FLOOR BRICK MARKING PLAN**

Project & Location: **Dr. PRAVEEN RESIDENCE @ TAGARAPUVALASA**

Date:	Scale:
20-08-2021	NTS
Orientation:	Sheet no:
NORTH N	**A-503**

Checked by :	JN
Drafted by :	Rama

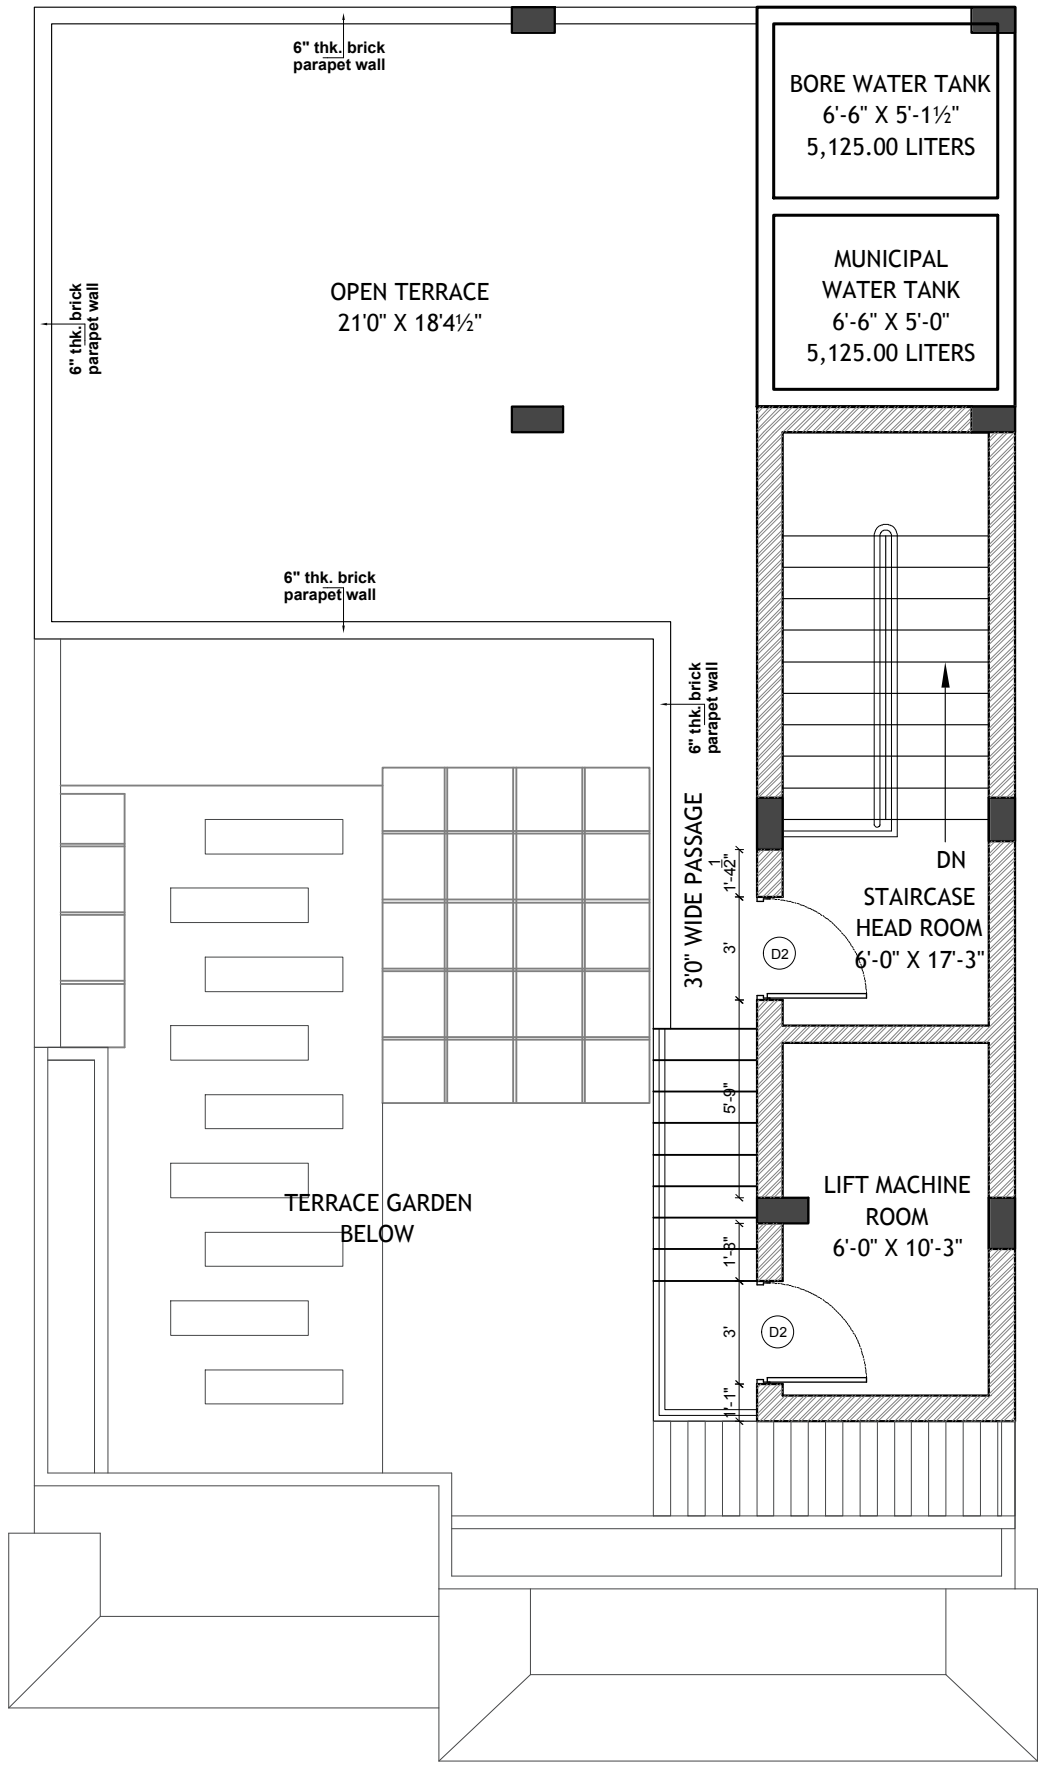

General Notes

1. This design & drawings are property of ARK Architects & interior designers.
2. All dimensions are in feet and inches, unless otherwise specified.
3. In case of any discrepancy, immediately notify the Architect.
4. Only written dimensions are to be followed. Do not scale the drawing.
5. Please refer the Coordinated drawings.
6. This drawing shall supercede its previous revisions if any.

Revisions		
No.	Revision/Issue	Date

Type of Drawing :

Project No:	2021_014
Sheet Title :	**TERRACE FLOOR BRICK MARKING PLAN**
Project & Location:	**Dr. PRAVEEN RESIDENCE @ TAGARAPUVALASA**

Date:	20-08-2021
Scale:	NTS
Orientation:	NORTH N
Sheet no:	**A-504**

Checked by :	JN
Drafted by :	Rama