



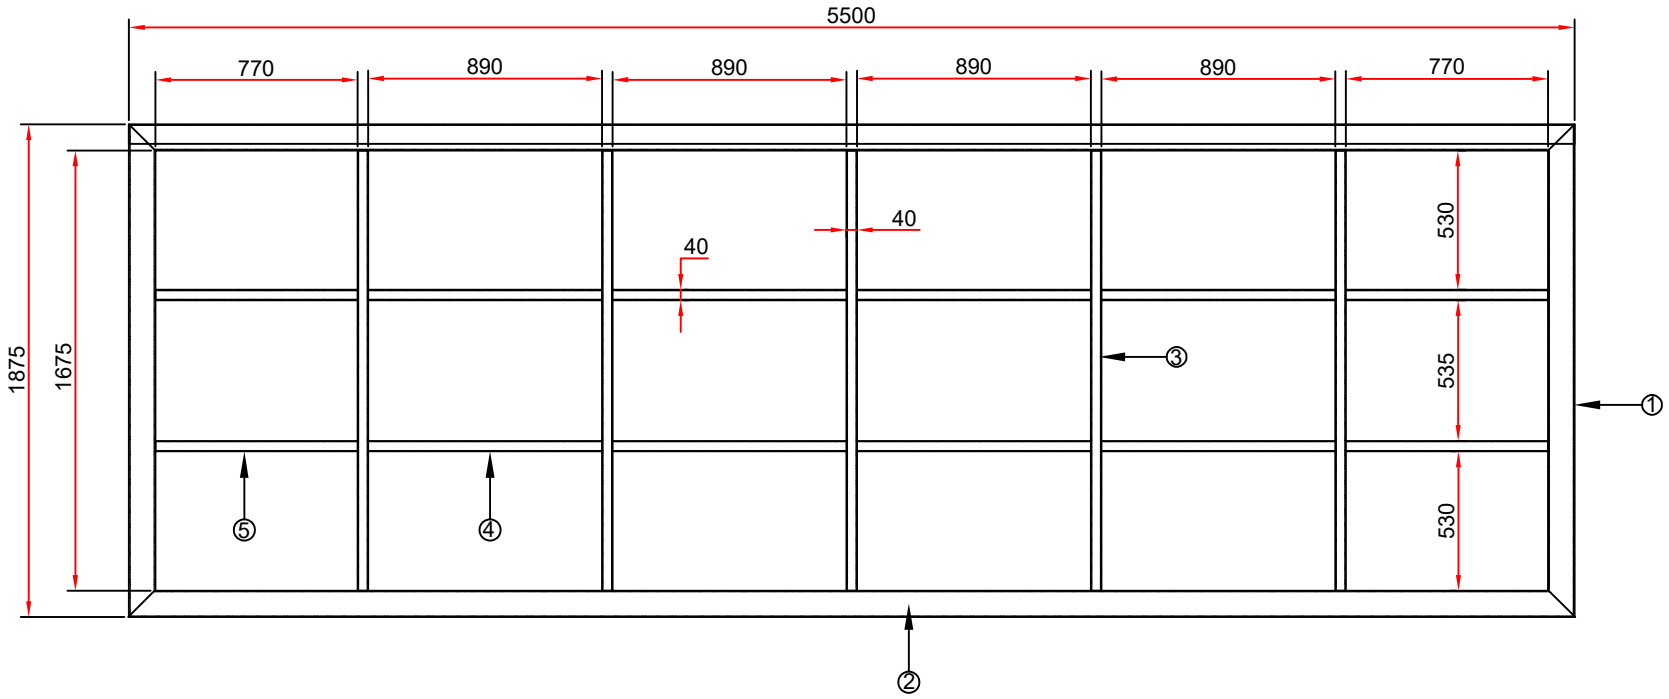

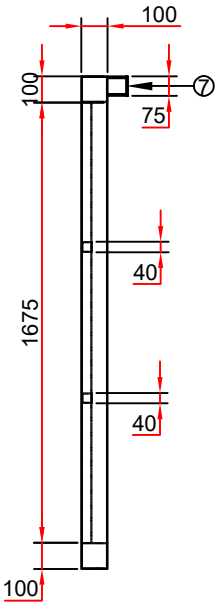

Note:-
1.All Dimension are in MM
2.Kindly Maintain the Given dimension

BOM			
SL NO.	DESCRIPTION	SPECIFICATION	QTY
1	MS SQ. TUBE	100X100X4X1875L	2NOS
2	MS SQ. TUBE	100X100X4X5500L	2NOS
3	MS SQ. TUBE	40X40X3.2X1675L	5NOS
4	MS SQ. TUBE	40X40X3.2X890L	8NOS
5	MS SQ. TUBE	40X40X3.2X770L	4NOS
6	MS FLAT	75X8X70L	2NOS
7	MS FLAT	75X8X5500L	1NO

Rev No.	Revision	Date	Revised By

This drawing & design is the property of NIHVA TECHNOLOGIES. Not to be sold or copied to any other concern.

TITLE:- Master Sliding Leaf (E17 GATE)

	NAME	DATE	SIGN
DRAWN	SUJATA	20/07/2022	
CHECK	M.S	20/07/2022	
APPRD.	A.K	20/07/2022	


If any queries contact : design@nihva.com


ALL DIMENSION ARE IN mm


NIHVA
NIHVA TECHNOLOGIES PVT. LTD.

NIHVA TECHNOLOGIES PVT. LTD. PUNE
Tel : 020 66304033
Email:- info@nihva.com
Website:- www.nihva.com

CLIENT - OC Specialities
LOCATION - Solapur
PRODUCT - Master Sliding Leaf | QTY-01
DWG NO:- NIHVA/22-23/CLT/0037 | REV-00
SCALE: NTS | SCALE:-- 1:1 | SHEET: 01 OF 01

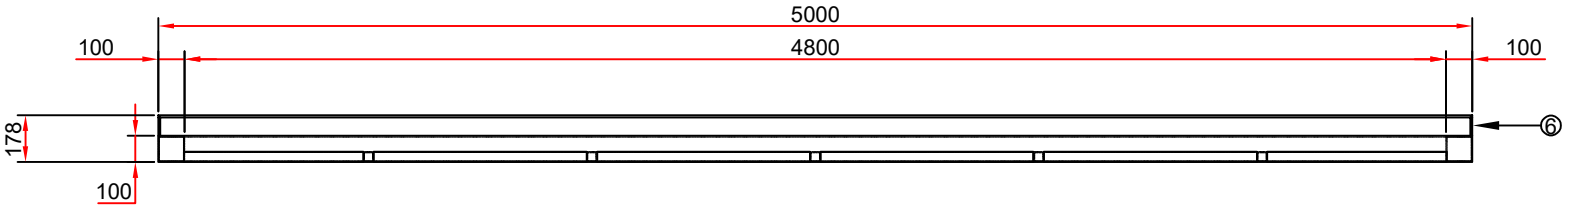

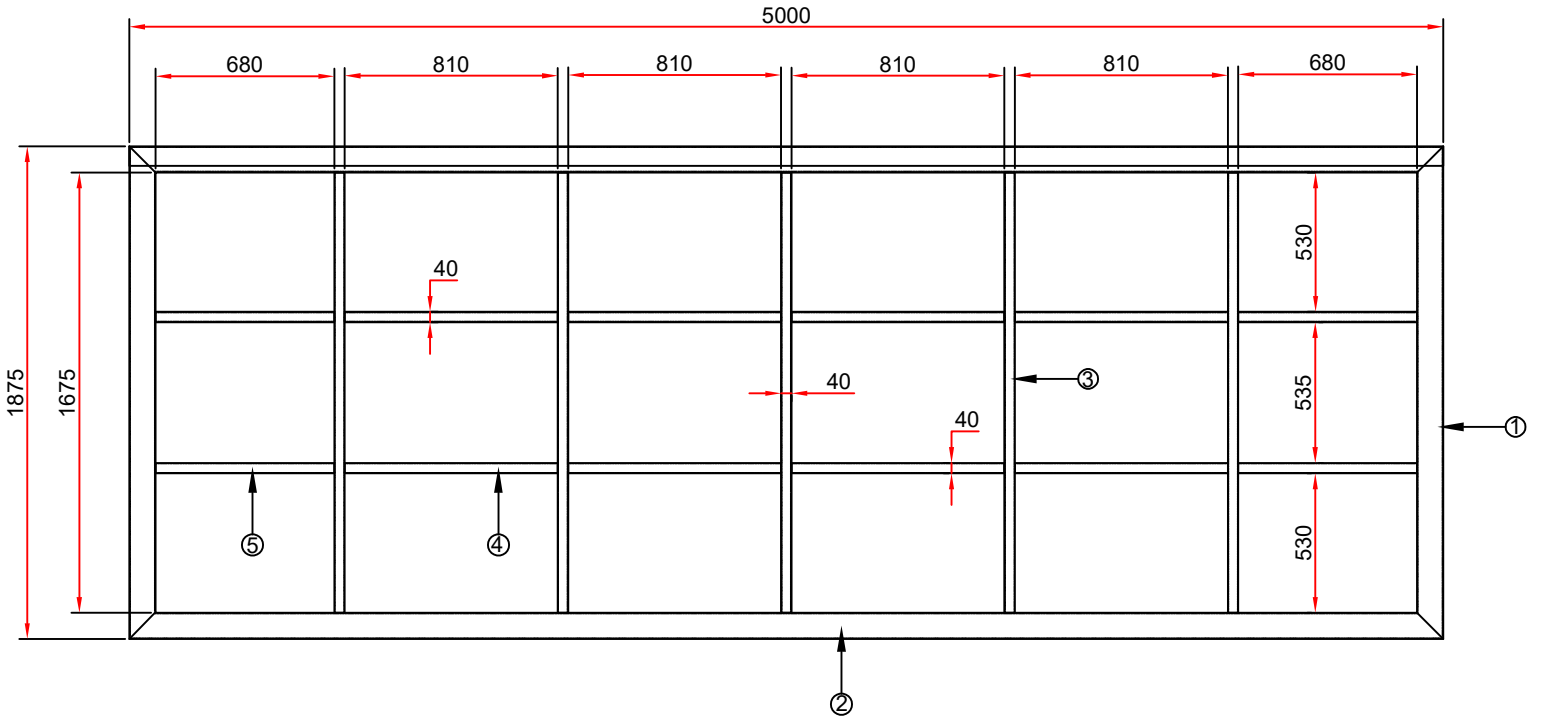

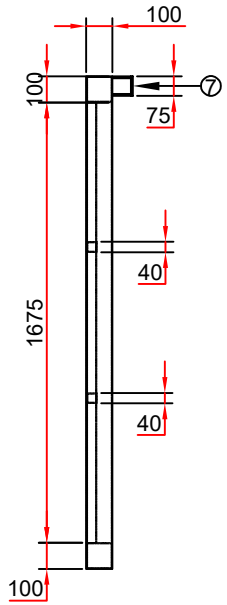

Note:-
1.All Dimension are in MM
2.Kindly Maintain the Given dimension

BOM FOR SINGLE LEAF			
SL NO.	DESCRIPTION	SPECIFICATION	QTY
1	MS SQ. TUBE	100X100X4X1875L	2NOS
2	MS SQ. TUBE	100X100X4X5000L	2NOS
3	MS SQ. TUBE	40X40X3.2X1675L	5NOS
4	MS SQ. TUBE	40X40X3.2X810L	8NOS
5	MS SQ. TUBE	40X40X3.2X680L	4NOS
6	MS FLAT	75X8X70L	2NOS
7	MS FLAT	75X8X5000L	1NO

Rev No.	Revision	Date	Revised By

QTY- 02Nos

This drawing & design is the property of NIHVA TECHNOLOGIES. Not to be sold or copied to any other concern.

TITLE:- Sliding Leaf1 (E17 GATE)

NIHVA TECHNOLOGIES PVT. LTD.


NIHVA TECHNOLOGIES PVT. LTD. PUNE
Tel : 020 66304033
Email:- info@nihva.com
Website:- www.nihva.com


	NAME	DATE	SIGN
DRAWN	SUJATA	20/07/2022	
CHECK	M.S	20/07/2022	
APPRD.	A.K	20/07/2022	


If any queries contact : design@nihva.com

ALL DIMENSION ARE IN mm

CLIENT - OC Specialities
LOCATION - Solapur
PRODUCT - Sliding Leaf | QTY-02
DWG NO:- NIHVA/22-23/CLT/0038 | REV-00
SCALE: NTS | SCALE:-- 1:1 | SHEET: 01 OF 01

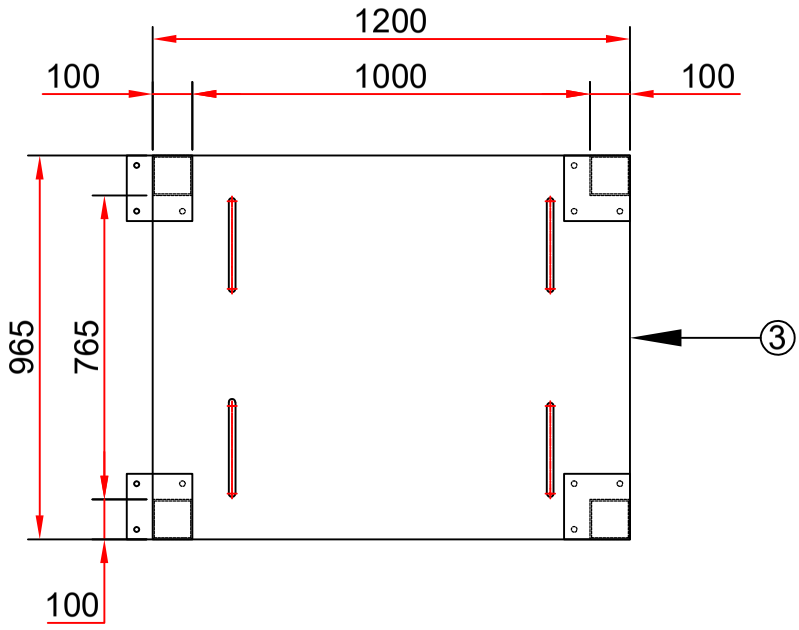

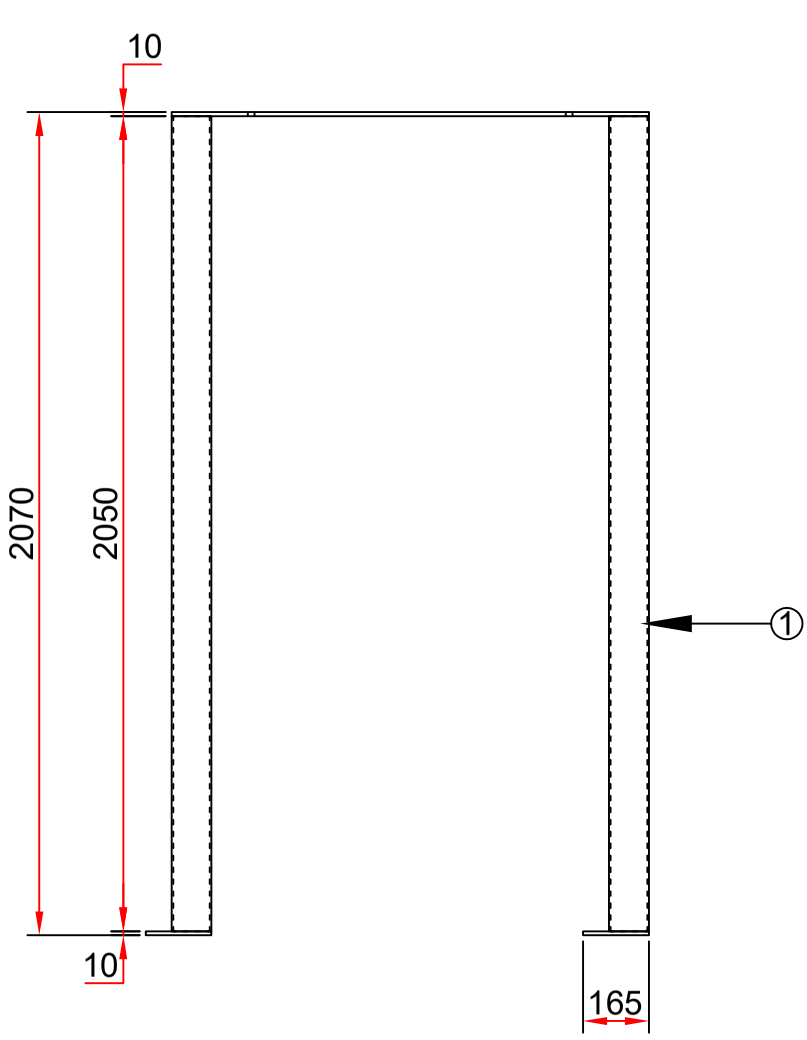

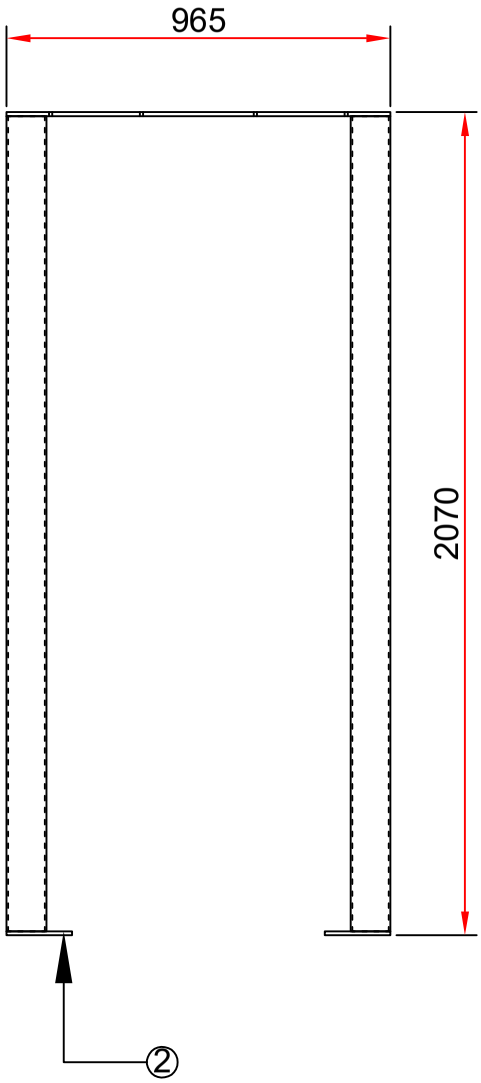

BOM FOR POST			
SL NO.	DESCRIPTION	SPECIFICATION	QTY
1	MS SQ. TUBE	100X100X4X2050L	4NOS
2	POST SUPPORT PLATE	165X165X10THK	4NOS
3	ROLLER SUPPORT PLATE	1200X965X10THK	1NO

Rev No.	Revision	Date	Revised By

This drawing & design is the property of NIHVA TECHNOLOGIES. Not to be sold or copied to any other concern.

TITLE:- POST (E17 GATE)

NIHVA TECHNOLOGIES PVT. LTD.

NIHVA TECHNOLOGIES PVT. LTD. PUNE
Tel : 020 66304033
Email:- info@nihva.com
Website:- www.nihva.com

	NAME	DATE	SIGN
DRAWN	SUJATA	20/07/2022	
CHECK	M.S	20/07/2022	
APPRD.	A.K	20/07/2022	

If any queries contact : design@nihva.com

ALL DIMENSION ARE IN mm


CLIENT - OC Specialities

LOCATION - Solapur

PRODUCT - | QTY:-1 NO

DWG NO:-NIHVA/22-23/MFG/0039 | REV- 0

SCALE: NTS | SCALE:-- 1:1 | SHEET: 01 OF 01

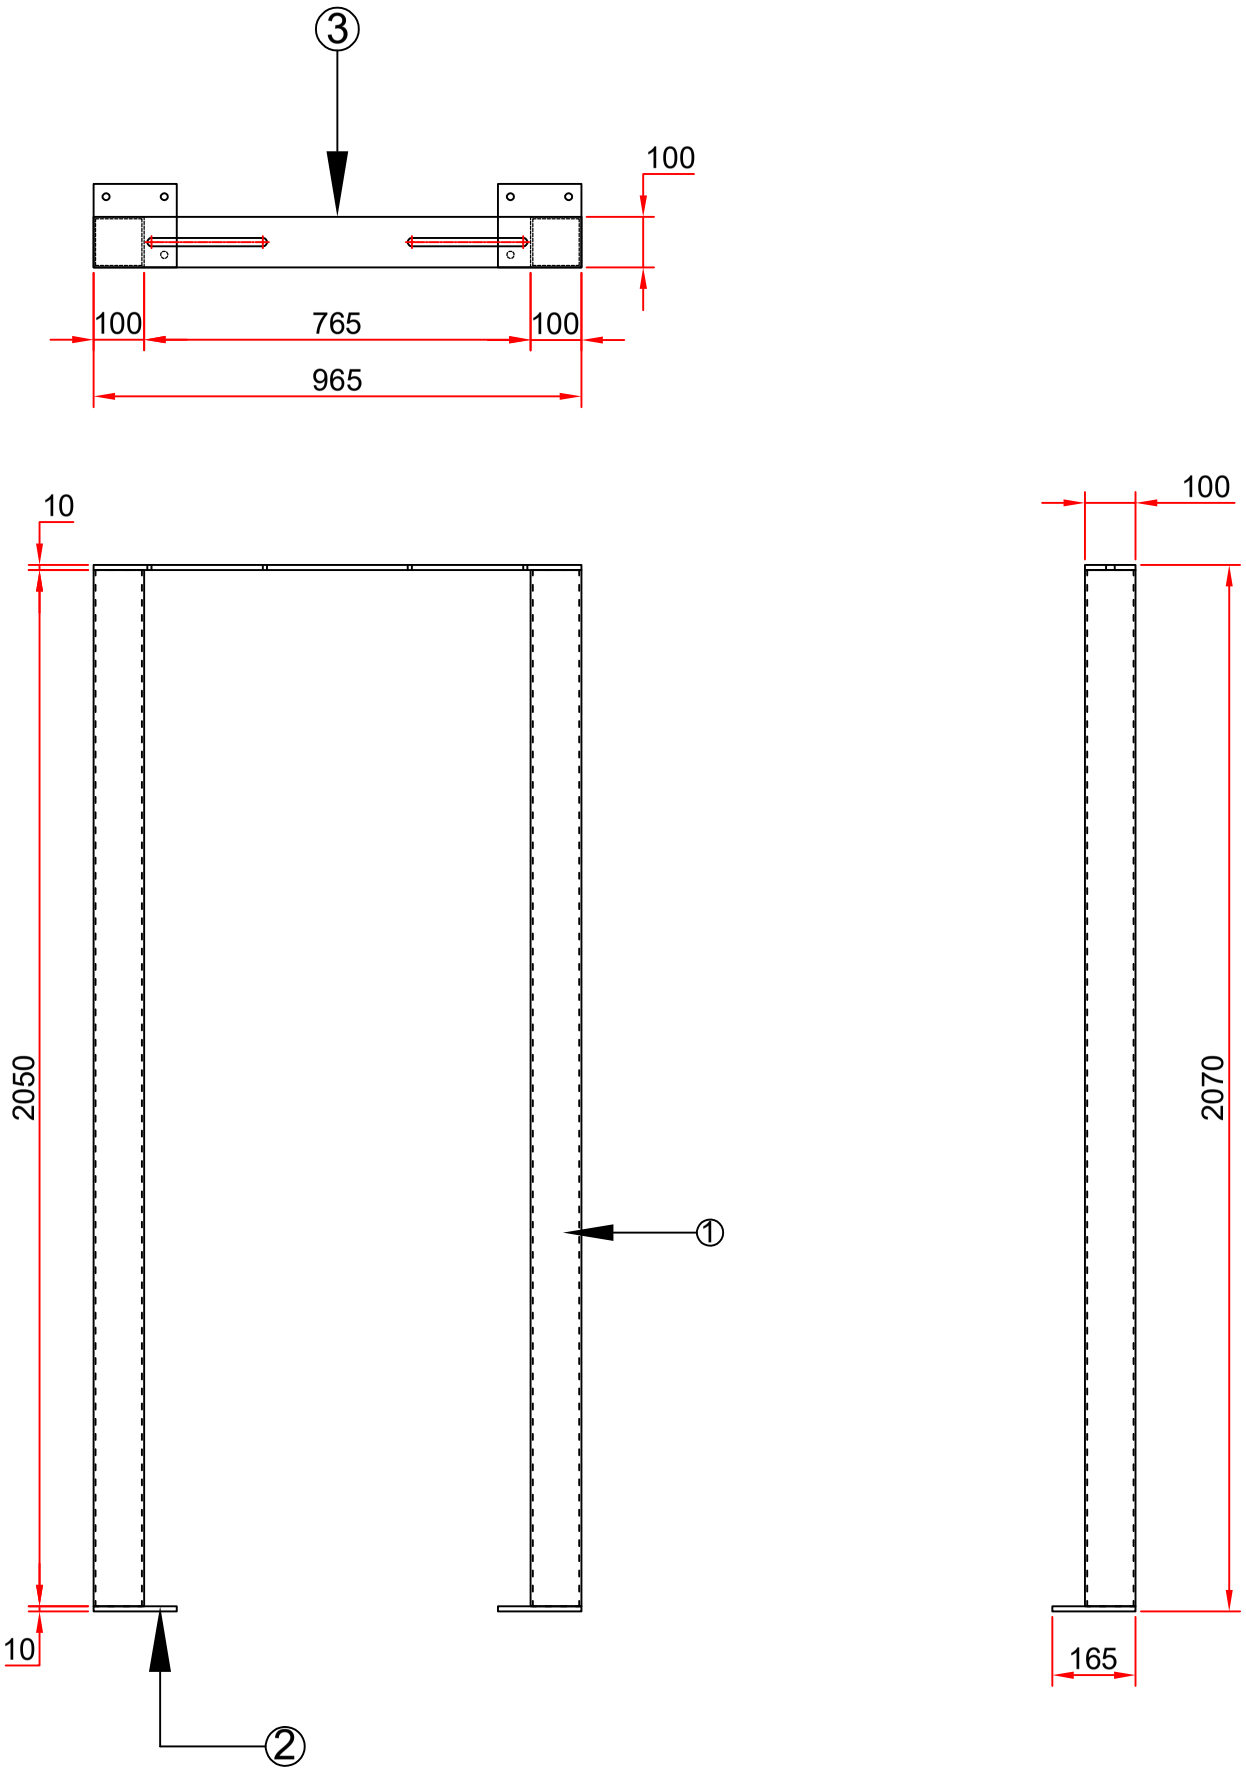

BOM FOR POST			
SL NO.	DESCRIPTION	SPECIFICATION	QTY
1	MS SQ. TUBE	100X100X4X2050L	2NOS
2	POST SUPPORT PLATE	165X165X10THK	2NOS
3	ROLLER SUPPORT PLATE	965X100X10THK	1NO

Rev No.	Revision	Date	Revised By

This drawing & design is the property of NIHVA TECHNOLOGIES. Not to be sold or copied to any other concern.

TITLE:- POST (E17 GATE)

NIHVA TECHNOLOGIES PVT. LTD.

NIHVA TECHNOLOGIES PVT. LTD. PUNE
Tel : 020 66304033
Email:- info@nihva.com
Website:- www.nihva.com

	NAME	DATE	SIGN
DRAWN	SUJATA	20/07/2022	
CHECK	M.S	20/07/2022	
APPRD.	A.K	20/07/2022	

If any queries contact : design@nihva.com

ALL DIMENSION ARE IN mm


CLIENT - OC Specialities


LOCATION - Solapur


PRODUCT - End Post1 | QTY:-1 NO

DWG NO:-NIHVA/22-23/MFG/0040 | REV- 0

SCALE: NTS | SCALE:-- 1:1 | SHEET: 01 OF 01

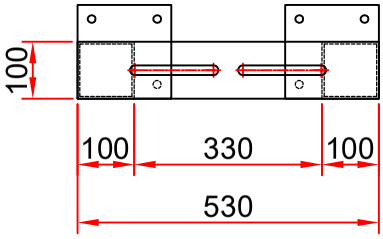

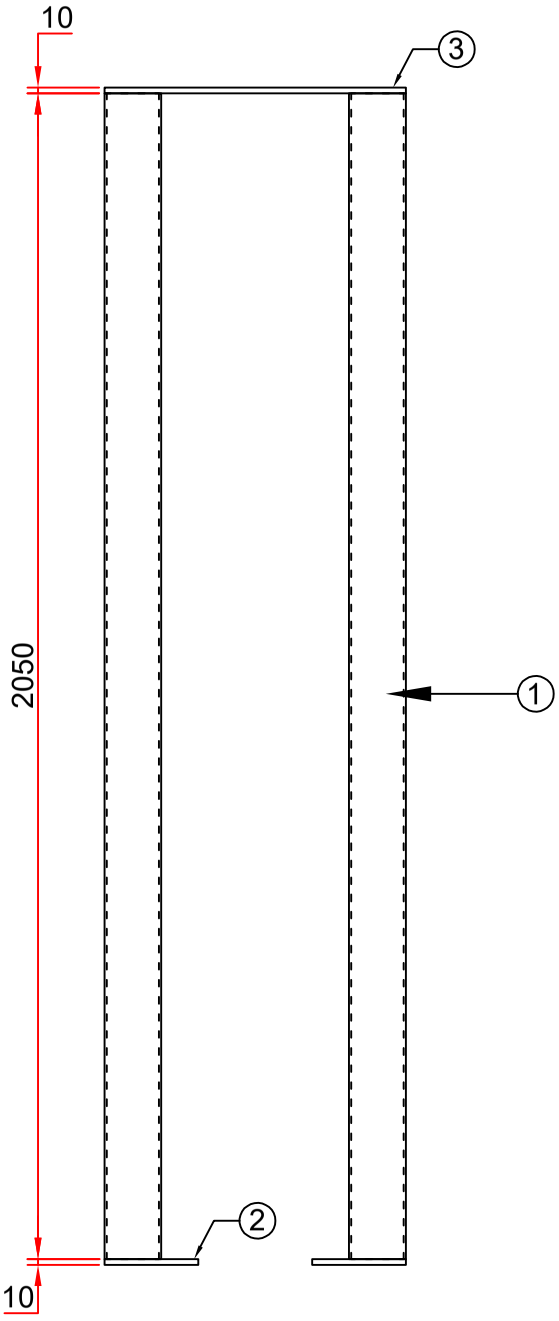

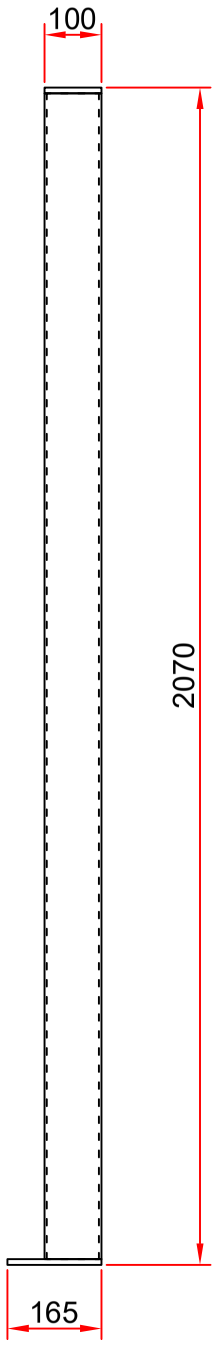

BOM FOR POST			
SL NO.	DESCRIPTION	SPECIFICATION	QTY
1	MS SQ. TUBE	100X100X4X2050L	2NOS
2	POST SUPPORT PLATE	165X165X10THK	2NOS
3	ROLLER SUPPORT PLATE	530X100X10THK	1NO

Rev No.	Revision	Date	Revised By

This drawing & design is the property of NIHVA TECHNOLOGIES. Not to be sold or copied to any other concern.

TITLE:- POST (E17 GATE)

NIHVA TECHNOLOGIES PVT. LTD.

NIHVA TECHNOLOGIES PVT. LTD. PUNE
Tel : 020 66304033
Email:- info@nihva.com
Website:- www.nihva.com

	NAME	DATE	SIGN
DRAWN	SUJATA	20/07/2022	
CHECK	M.S	20/07/2022	
APPRD.	A.K	20/07/2022	

If any queries contact : design@nihva.com

ALL DIMENSION ARE IN mm


CLIENT - OC Specialities


LOCATION - Solapur


PRODUCT - End Post 2 | QTY:-1 NO


DWG NO:-NIHVA/22-23/MFG/0041 | REV- 0

SCALE: NTS | SCALE:-- 1:1 | SHEET: 01 OF 01

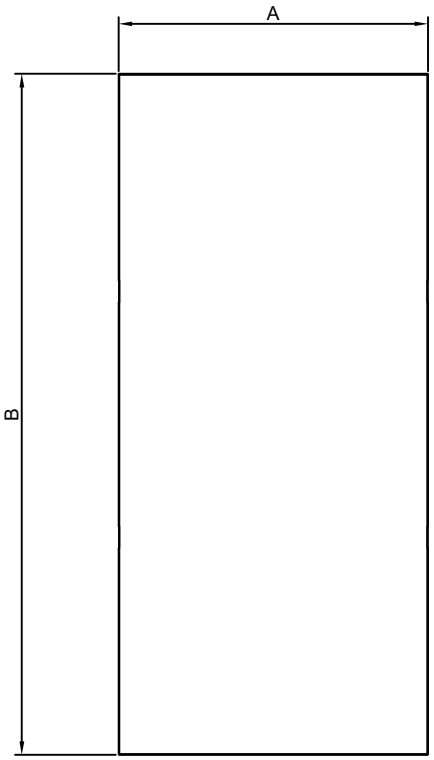

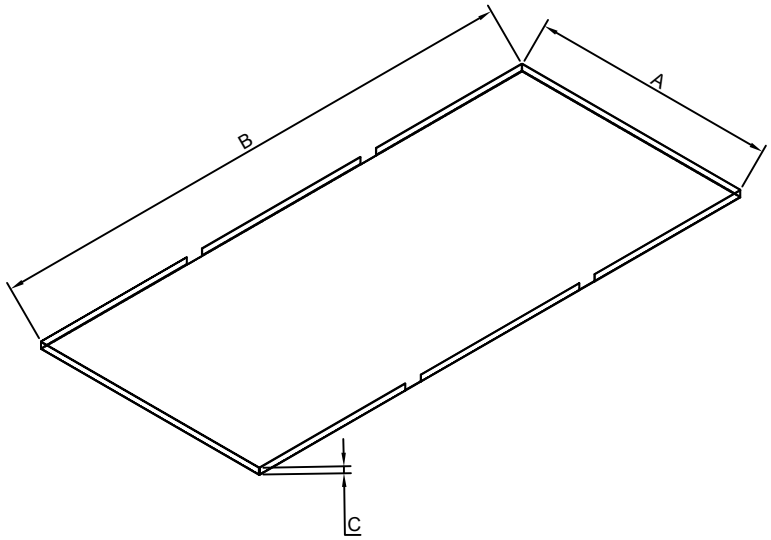

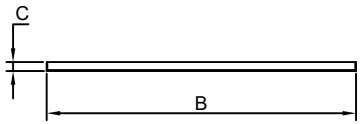

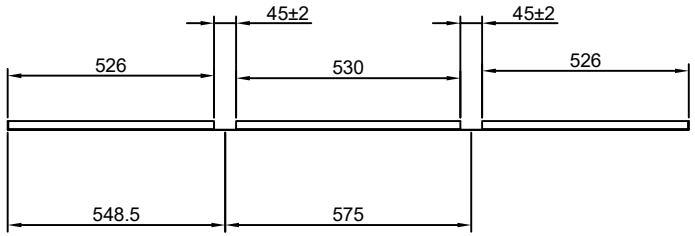

NOTE:-

1.ALL DIMENSION ARE IN MM.

2.KINDLY MAINTAIN THE DIMESTION OF THE TRAY.

3.IF HAVE ANY QUERIES DO LET ME KNOW.

DIMENSIONS FOR TRAY					
SL NO.	A±2	B±2	C	THICKNESS	QTY
1	767	1672	25	1.2	2NOS
2	887	1672	25	1.2	4NOS
3	677	1672	25	1.2	4NOS
4	807	1672	25	1.2	8NOS

This drawing & design is the property of NIHVA TECHNOLOGIES. Not to be sold or copied to any other concern.

TITLE:- TRAY (E17 GATE)

NIHVA TECHNOLOGIES PVT. LTD.

NIHVA TECHNOLOGIES PVT. LTD. PUNE
Tel : 020 66304033
Email:- info@nihva.com
Website:- www.nihva.com

	NAME	DATE	SIGN
DRAWN	SUJATA	21/07/2022	
CHECK	M.S	21/07/2022	
APPRD.	A.K	21/07/2022	

If any queries contact : design@nihva.com

ALL DIMENSION ARE IN mm


CLIENT - Nihva Technologies Pvt Ltd

LOCATION - Pune

PRODUCT - Tray | QTY-

DWG NO:- NIHVA/22-23/VDR/0043 | REV-00

SCALE: NTS | SCALE:-- 1:1 | SHEET: 01 OF 01

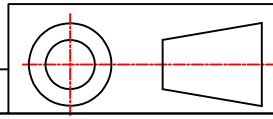

Rev No.	Revision	Date	Revised By