

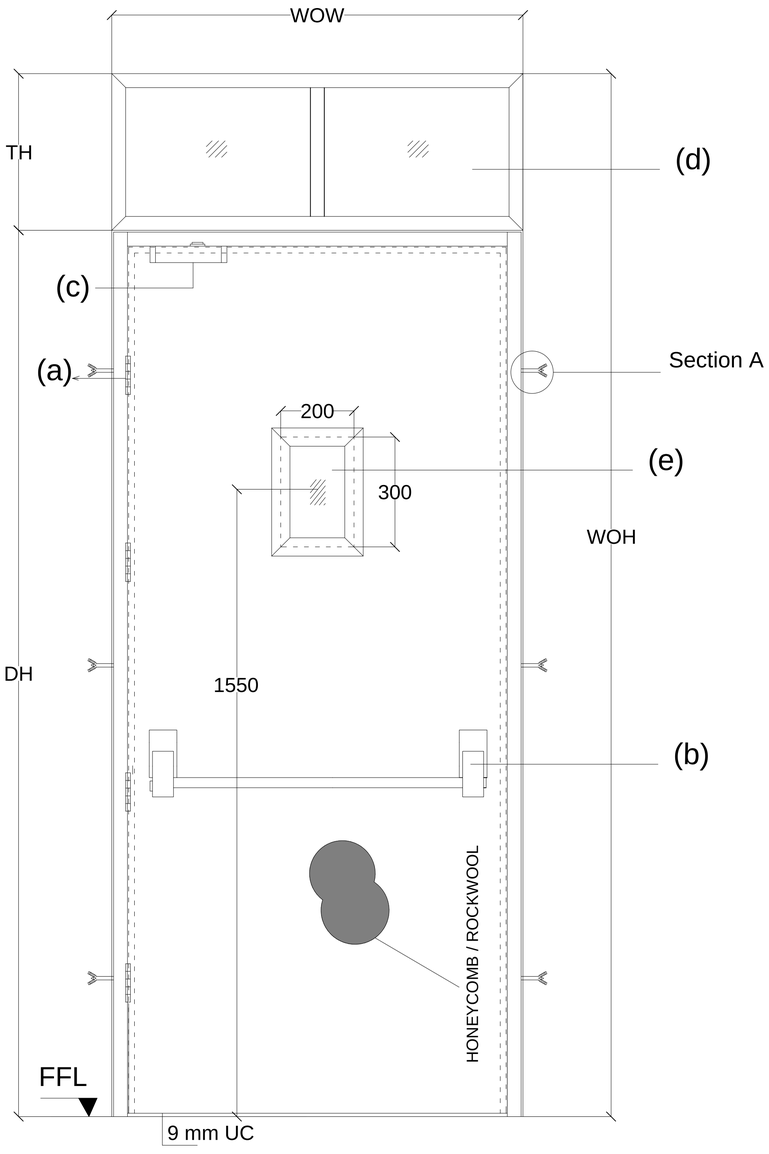


ELEVATION

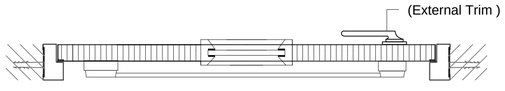

Top View

Abbrevation's:
WOW-Wall Opening Width
WOH-Wall Opening Height
DH- Door Height
UC-Under Cut
FFL-Finished Floor Level

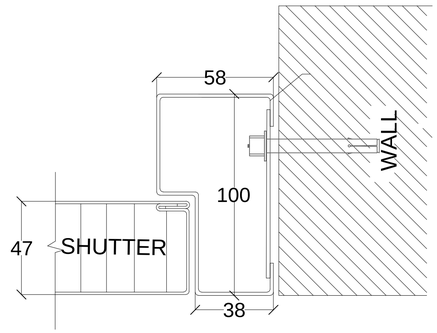

ASSESORIES DETALES

(a) HINGES: SS hinges 100x75x3mm

(b) LOCK : Mortise Lock with half cylinder.
Panic Bar
Outer trim

(c) DOOR CLOSER : F 8500

(d) FIXED GLASS(5mm THK.) WITH FRAME.

(e) VISION PANEL- 5mm THK. FIRE GLASS SIZE- 200X300mm.

Shutter thickness : 47 mm
Frame Sheet thick : 1.20mm
Shutter sheet thick : 0.80mm
Fixing : On Soliid Brick plasterd wall with Anchors

NOTE:- *All Dimensions are in mm.
*Tolerance:-All Linear Dimensions ±3mm,Others ±0.5mm.
*The Drawing Is For Location of Hardware only. Drawing Does Not Represent The Hardware For More Clarity, Please Go Through Hardware Broucher.

Fire door size

WOW	WOH	DH	TH	TYPE 1	TYPE 2	TYPE 3	TYPE 4	QUANTITY
1191	3000	2400	600					1
1180	3121	2400	721					1
1180	3029	2400	629					1
1195	3033	2400	633					1
1205	3017	2400	617					1
1194	2958	2400	558					1
1192	3000	2400	600					1

NOTE- CLIENT SHOULD SELECT DOOR TYPE FROM DOOR HANDLING SHEET & COLOR OF DOOR.

This drawing & designing is the property of NIHVA TECHNOLOGIES. Not to be sold or copied to any other concern.

TITLE
FIRE RATED DOORS
WITH FIXED GLASS

NIHVA TECHNOLOGIES PVT. LTD.
NIHVA TECHNOLOGIES PVT. LTD. PUNE
Tel : 020 66304033
Email:- info@nihva.com
Website:- www.nihva.com

	SIGN	DATE
DRAWN	OMKAR	11/07/17
CHECK	SHEKHAR	11/07/17
REV.	00	
APPROVAL		

If any queries contact : projects@nihva.com

ALL DIMENSION ARE IN mm

CLIENT - VAICHAL CONSTRUCTION
PROJECT - TAGMA CENTRE
SITE - CHAKAN
DWG. NO. : NIHVA/17-18/0128
SCALE: NTS | WT: | SHEET: 01 OF 01