
CLIENT												
WEIGHT ESTIMATION SHEET												
CLIENT			SJ Contracts							DATE	16-08-2024	
PROJECT			Swing Gate							LOCATION	Pune	
FINISH SIZE			7.5 m x 2.1 m							PREPARED BY	Sumit	
SR	**DESC**	**DETAILS**	**MATERIAL GRADE**	**SP.GRAVITY**	**WIDTH**	**HEIGHT**	**THICKNESS**	**LENGTH**	**UOM**	**QUANTITY**	**WEIGHT**	**REMARK**
1	SINGLE LEAF (3.650 M X 2.1 M)	Tube - Outer Frame	MS	7.85	75	75	3	11500	mm	1	78	191
		Vertical Inner Support - Tube	MS	7.85	25	25	2	78000	mm	1	113	Weight OF leaf
2		Post	MS	7.85	250	250	6.3	7500	mm	1	362	
4	Accessories	Bottom wheel	STD	7.85					No's	2		
		Handle	MS	7.85					No's	2		
		Heavy duty hinges	STD						No's	6		
		Manual Lock	STD						No's	1		
									Weight For Required Qty	1	552	
									Weight Including Safety Factor	1.5	828	
Motor Selection = According		286.0	kg									
CD between 2 Tube = 175mm												

REFERENCE IMAGE

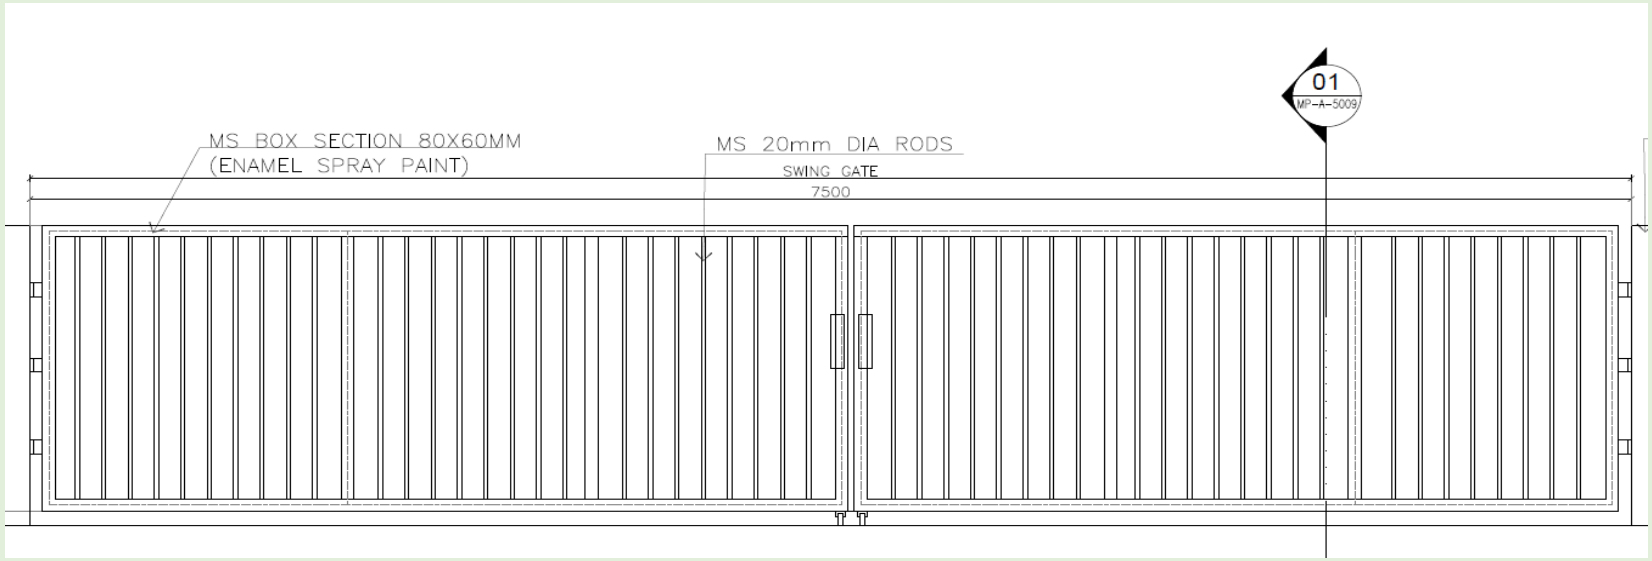

CLIENT												
WEIGHT ESTIMATION SHEET												
CLIENT			SJ Contracts							DATE	16-08-2024	
PROJECT			Wicket Gate							LOCATION	Pune	
FINISH SIZE			1.2 m x 1.5 m							PREPARED BY	Sumit	
SR	**DESC**	**DETAILS**	**MATERIAL GRADE**	**SP.GRAVITY**	**WIDTH**	**HEIGHT**	**THICKNESS**	**LENGTH**	**UOM**	**QUANTITY**	**WEIGHT**	**REMARK**
1	SINGLE LEAF (1.2 M X 1.8 M)	Tube - Outer Frame	MS	7.85	100	100	3	7200	mm	1	66	94 Weight OF leaf
		Vertical Inner Support - Tube	MS	7.85	25	25	2	19500	mm	1	28	
2		Post	MS	7.85	250	250	6.3	2500	mm	1	121	
3	Accessories	Hinges	MS	7.85					No's	2	0	
		Manual Lock	MS	7.85					No's	1	0	
									Weight For Required Qty		1	214
									Weight Including Safety Factor		1.5	322
Mode Of Operation = Manual												
CD between 2 Tube = 150mm												

REFERENCE IMAGE

