





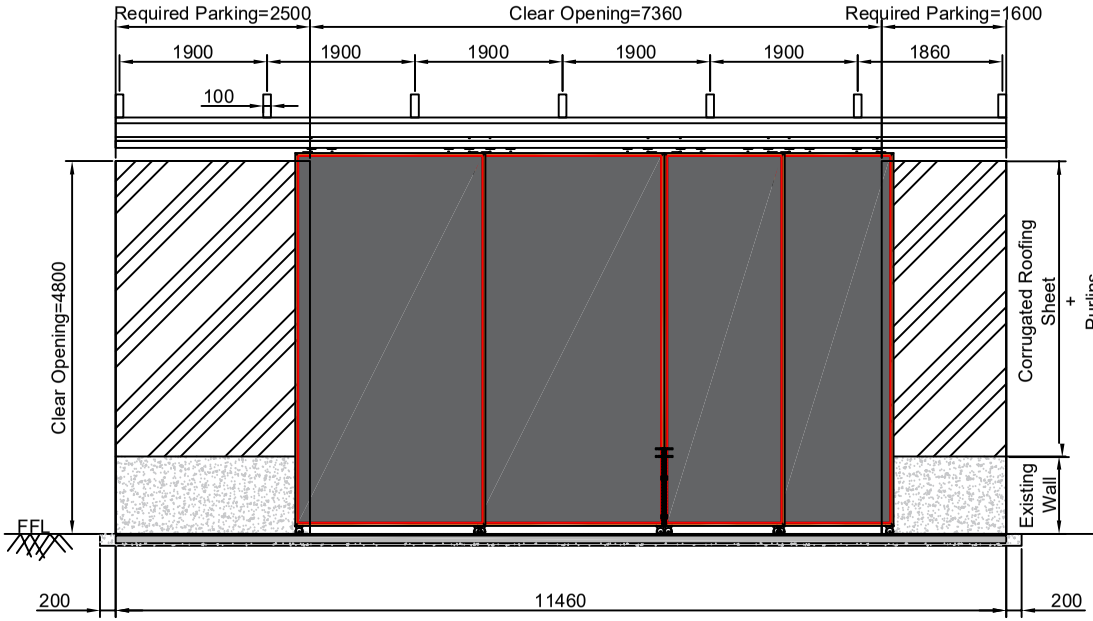

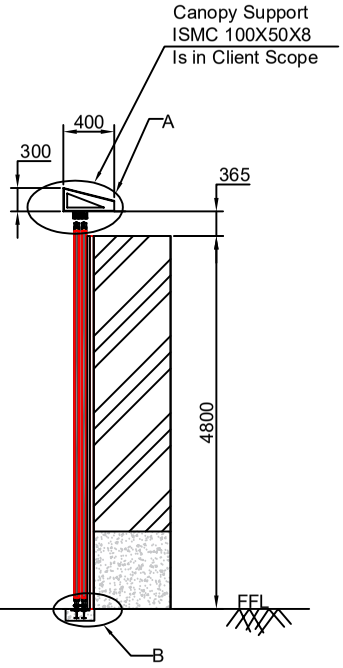

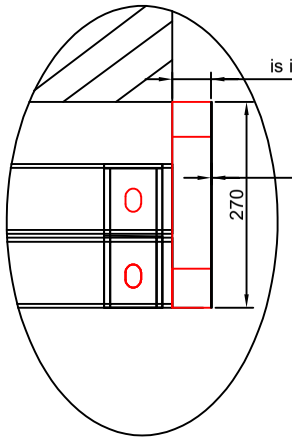


Detail C

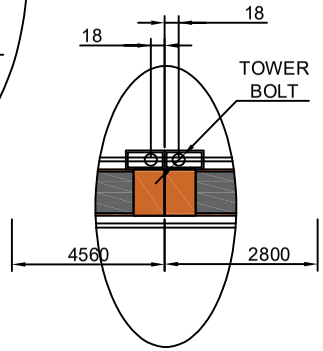


Client scope
*Front Gutter, Bollard and fire extinguisher unit need to be shift. * roof need to be shifted by 365 mm *Civil foundation need to be done for tracks

Color code	Color
5018	Turquoise blue

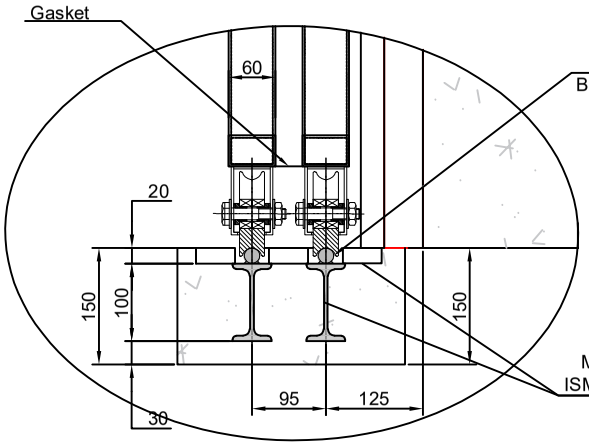

Detail A

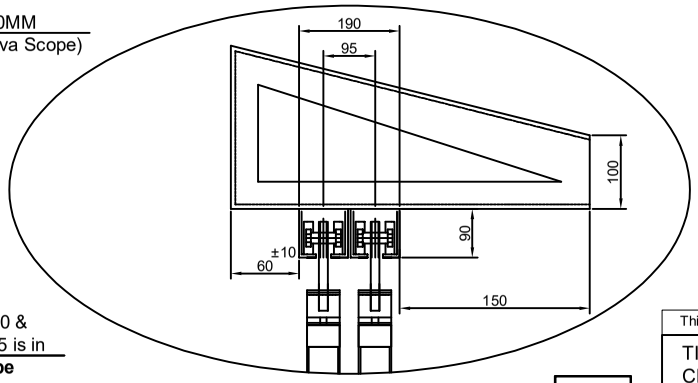

Detail B

Note:--

1. All dimension are in MM
2. All Civil work will be in client scope
3. Manufacturing,civil and installation tolerance will be ±10mm
4. Top and Bottom track should be in parallal within ±3mm
5. Nihva Supervisor on site for Monitoring/Checking of civil work

This drawing & design is the property of NIHVA TECHNOLOGIES. Not to be sold or copied to any other concern.

TITLE:-4LEAF-BOTH SIDE CRM DOOR-13				NIHVA TECHNOLOGIES PVT. LTD. PUNE Tel : 020 66304033 Email:- info@nihva.com Website:- www.nihva.com	
	NAME	DATE	SIGN		
DRAWN	SUJATA	13/05/2022		CLIENT - LESTECH	
CHECK	M.SUTAR	13/05/2022		LOCATION - POSCO MANGAON	
APPRD.	V.TARAK	13/05/2022		PRODUCT - SLIDING DOOR	
If any queries contact : design@nihva.com				DWG NO:-NIHVA/22-23/CLT/0037	REV- 0
ALL DIMENSION ARE IN mm				SCALE: NTS	SCALE:-- 1:1 | SHEET: 01 OF 01

Rev No.	Revision	Date	Revised By