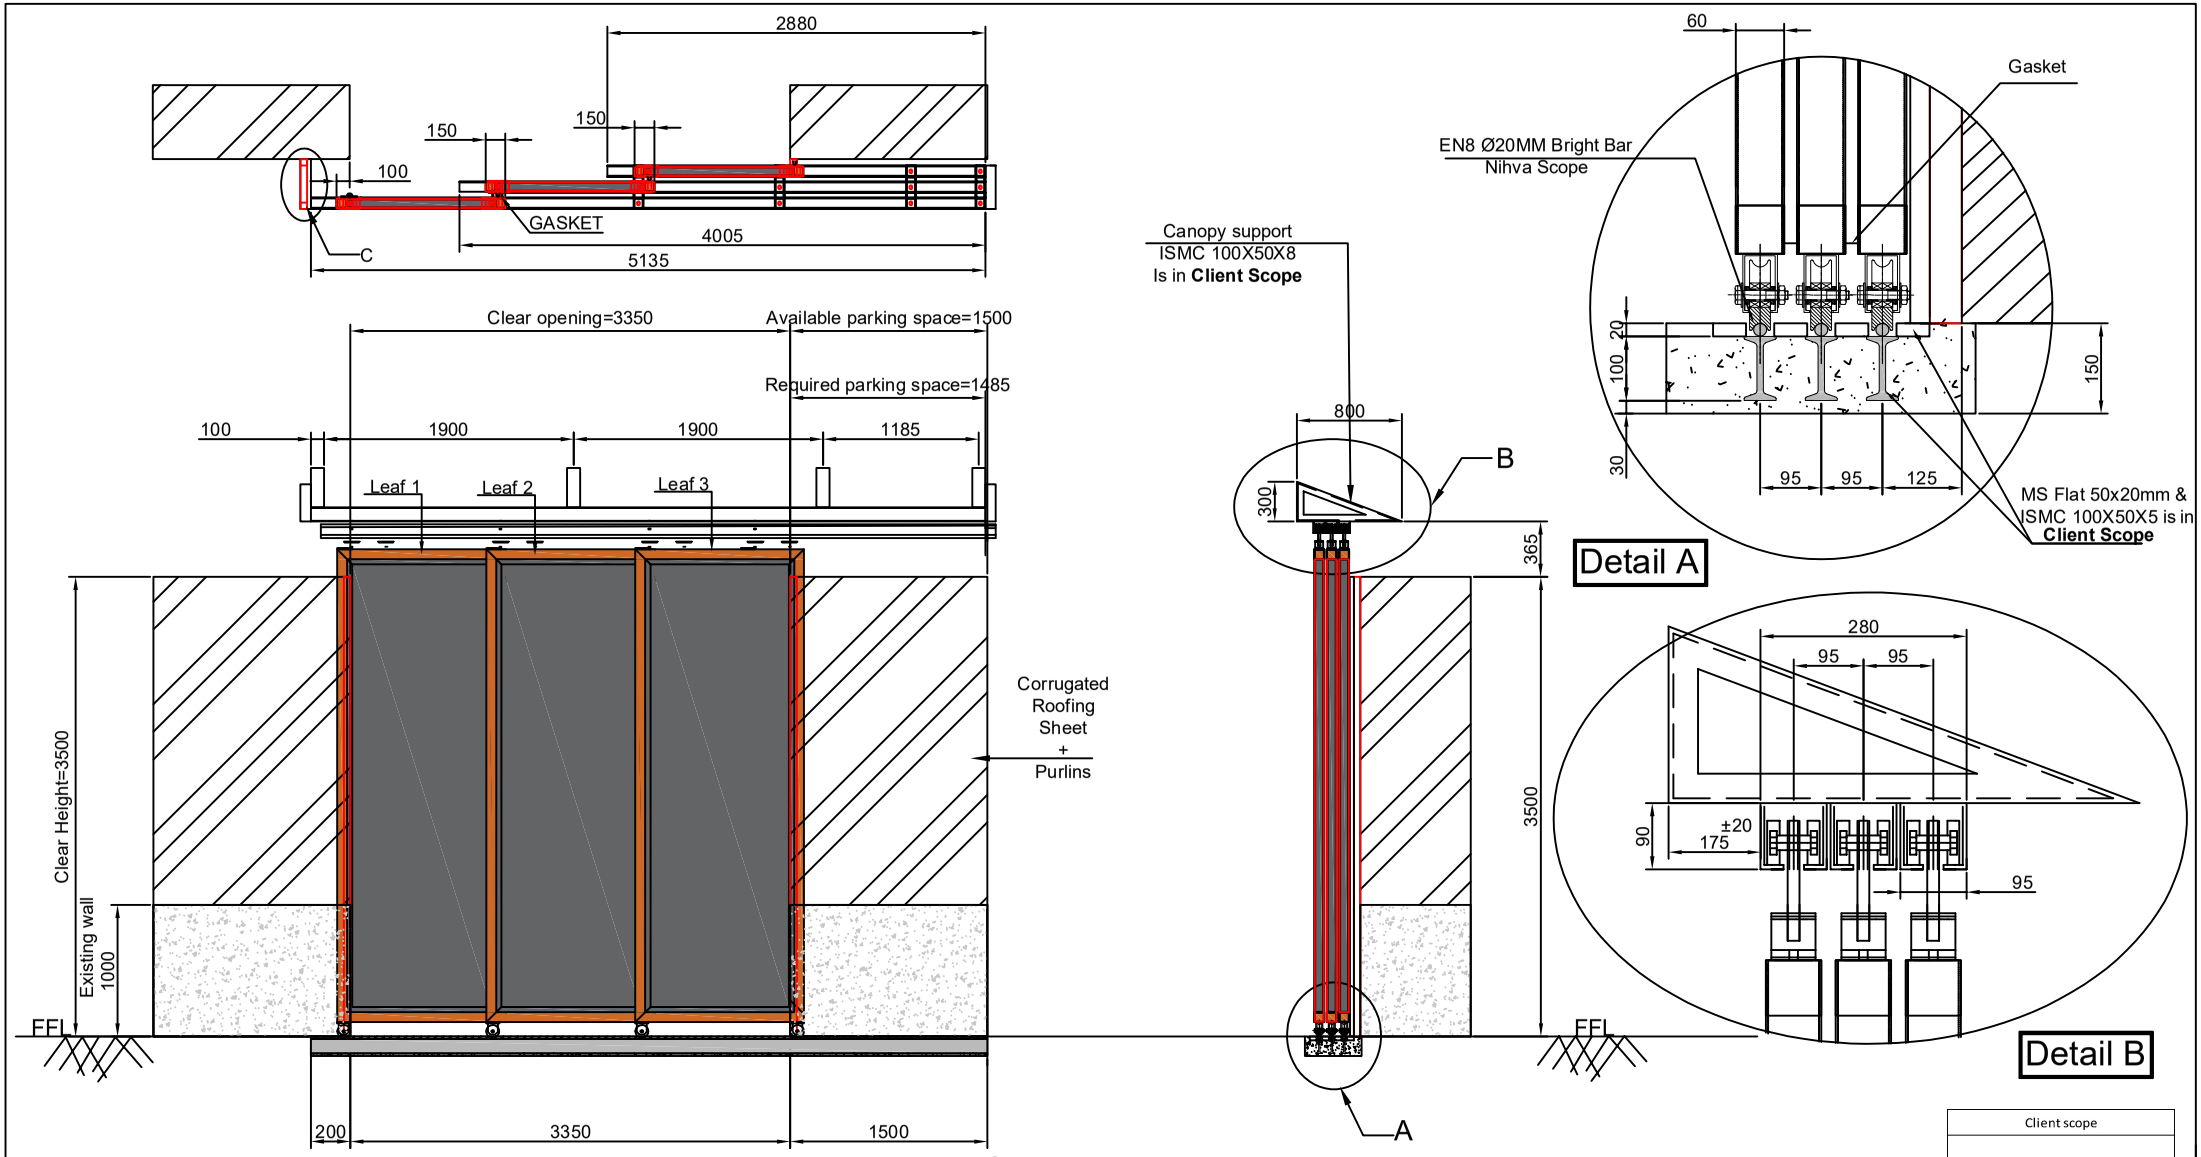


Note:-

1.All dimension are in MM

2.Manufacturing,civil and installation tolerance will be ±10mm

3.Top and Bottom track should be in parallal within ±3mm

4.Nihva Supervisor on site for Monitoring/Checking of civil work

Color code	Color
5018	Turquoise blue

Client scope
*Roof need to be shift at top 365mm *Drainage area need to be remove frome left side appox.200mm *Gutter area need to be remove *Civil foundation need to be done for tracks

This drawing & design is the property of NIHVA TECHNOLOGIES. Not to be sold or copied to any other concern.

TITLE:-3LEAF RIGHT SIDE
CRM-04 /Gate 13

NIHVA TECHNOLOGIES PVT. LTD.
NIHVA TECHNOLOGIES PVT. PUNE
Tel : 020 66304033
Email:- info@nihva.com
Website:- www.nihva.com

	NAME	DATE	SIGN
DRAWN	SUJATA	30/04/2022	
CHECK	M.SUTAR	30/04/2022	
APPRD.	V.TARAK	30/04/2022	

CLIENT - LESTECH
LOCATION - POSCO MANGAON
PRODUCT - SLIDING DOOR
If any queries contact : design@nihva.com
DWG NO:-NIHVA/22-23/CLT/0018 REV- 1
ALL DIMENSION ARE IN mm
SCALE: NTS SCALE:-- 1:1 SHEET: 01 OF 01

Rev No.	Revision	Date	Revised By
00	Released drawing	29/04/2022	Sujata
1.	Revised as per Client Comments	02/05/2022	Sujata