

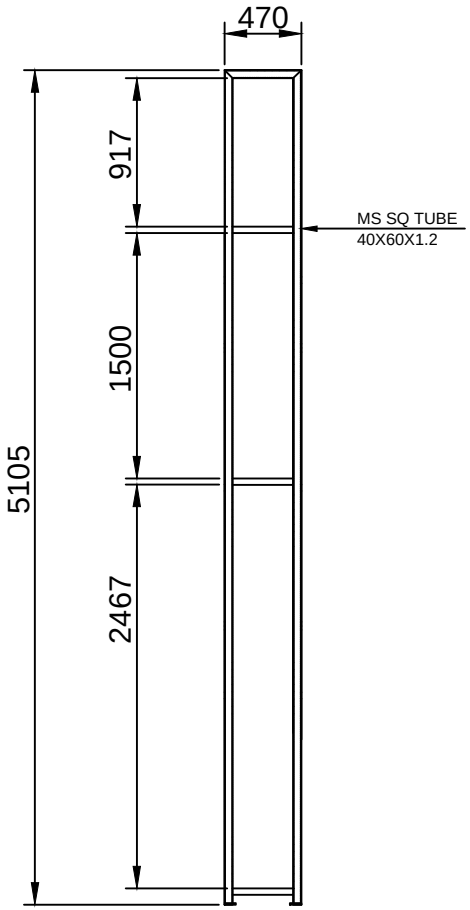


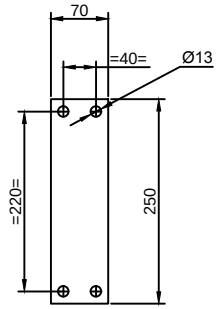


MATERIAL:MS PLATE
THK:10MM
QTY:04NOS

CRM DOOR 01

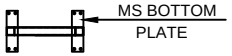

QTY:02NOS

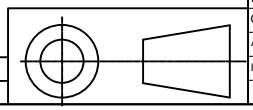

This drawing & design is the property of NIHVA TECHNOLOGIES. Not to be sold or copied to any other concern.

4 LEAF RIGHT SIDE CRM DOOR 01/GATE 09			NIHVA TECHNOLOGIES PVT. LTD. PUNE Tel : 020 66304033 Email:- info@nihva.com Website:- www.nihva.com
	NAME	DATE	
DRAWN	KISHAN	16/05/2022	CLIENT - NIHVA TECHNOLOGIES PVT LTD
CHECK	M.SUTAR	16/05/2022	LOCATION -
APPRD.	V.TARAK	16/05/2022	PRODUCT - SLIDING DOOR- END CLOSER
If any queries contact : design@nihva.com			DWG NO:-NIHVA/22-23/CLT/
ALL DIMENSION ARE IN mm			SCALE: NTS SCALE:-- 1:1 SHEET:

Rev No.	Revision	Date	Revised By