



# SECTION II

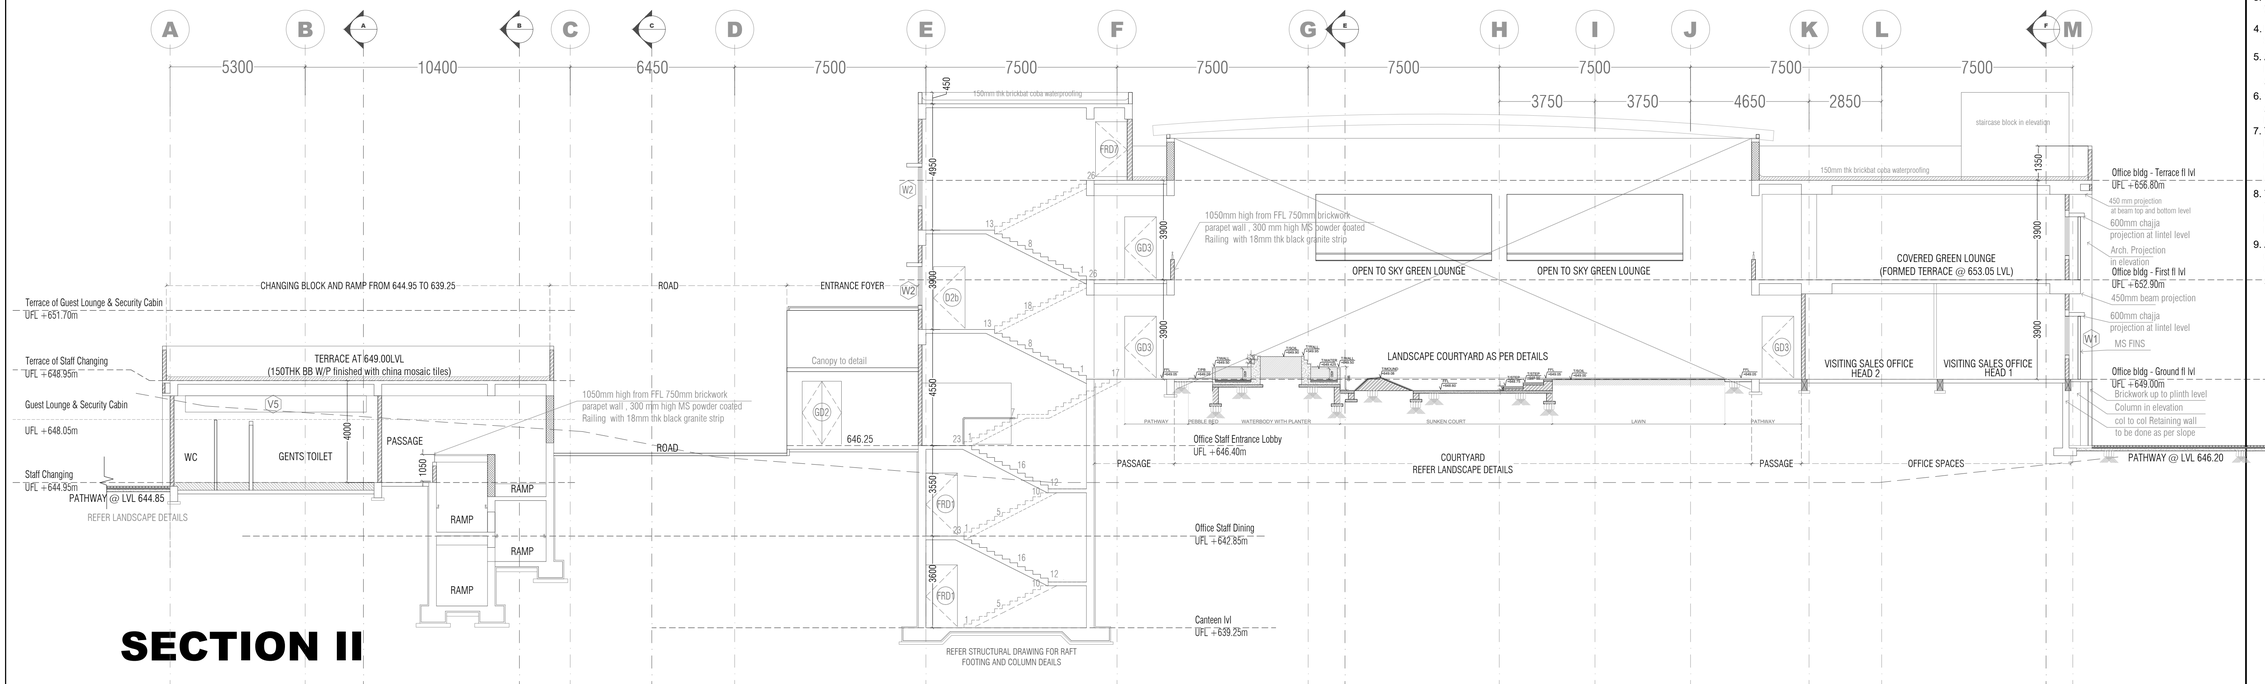


# SECTION JJ

## OFFICE & ANCILLARY BLDG.

**NOTES :**

1. ALL DIMENSIONS ARE IN MM UNLESS OTHERWISE MENTIONED
2. ONLY WRITTEN DIMENSIONS SHALL BE FOLLOWED
3. DIMENSIONS SHALL BE CHECKED AND CORRELATED WITH STRUCTURAL DRAWINGS
4. LARGER SCALED DRAWINGS SUPERSEDE SMALLER SCALED DRAWINGS
5. ANY DISCREPANCY IN THE DRAWING SHALL BE IMMEDIATELY BROUGHT TO THE NOTICE OF THE ARCHITECT
6. NO WORK ON SITE SHALL PROCEED WITHOUT THE APPROVAL OF **FOURTH DIMENSION ARCHITECTS PVT. LTD**
7. THIS DRAWING IS THE SOLE PROPERTY OF **FOURTH DIMENSION ARCHITECTS PVT. LTD** AND IS NOT TO BE REPRODUCED OR COPIED IN PART OR WHOLE IN ANY FORM AND ON COMPLETION OF PROJECT SHALL BE RETURNED TO ARCHITECS
8. THIS DRAWING CONTAINS COPYRIGHT MATERIAL AND TRADE SECRET INFORMATION BELONGING TO **FOURTH DIMENSION ARCHITECTS PVT LTD** AND ITS CLIENT AS NOTED ABOVE
9. ANY UNAUTHORIZED USE , DISCLOSURE DISSEMINATION OR DUPLICATION OF ANY OF THE INFORMATION CONTAINED HEREIN MAY RESULT IN LIABILITY UNDER APPLICABLE LAW.

| NO | REVISION | DATE |
|---|---|---|
| | | |

**LEGEND :**

| | |
|---|---|
| 150 MM THK WALL | EXTERNAL & MAIN DIVISION WALLS |
| 300 MM SUNK | |
| 200 MM SUNK | |
| 150 MM SUNK | |

ALL SINGLE LAYER EXTERNAL WALLS 150THK AAC BLOCK MASONRY WALL
100 THK AAC BLOCK MASONRY SHOWN AS
300 THK AAC BLOCK MASONRY SHOWN AS
ALL TOILET INTERNAL WALLS 100THK AAC BLOCK MASONRY WALL UNLESS MENTIONED.

**PROJECT :**

PROPOSED PLANT FOR WILO MATHER & PLATT Pumps Pvt. Ltd. LIMITED, AT CHORDIA INDUSTRIAL PARK, SHIRWAL, SATARA.

**CLIENT :**

**WILO MATHER & PLATT PUMPS PVT. LTD.**


**FOURTH DIMENSION ARCHITECTS PVT. LTD.**
FDAPL ARCHITECTS, PLANNERS, INTERIOR, LANDSCAPE DESIGNERS & LEISURE CONSULTANTS
FD House, Lane No 8, Prabhat Road,
Deccan Gymkhana, Pune – 411004.
Telephone No's : 020- 41000999, +91 9922921701 / 02;
Fax +91-02041000888


**TITLE : SECTION H & SECTION I**

**DRAWING STATUS: FOR TENDER**

| | | |
|---|---|---|
| DATE | : 25-Mar-22 | **NORTH** |
| SCALE | : AS MENTIONED | |
| JOB NO. | : W-IND-0320 | |
| DRAWN BY | : NUPOOR | |
| CHECK BY | : TEJAL | |

| **DRAWING NO :** | **REVISION NO :** |
|---|---|
| OB-A-405 | R0 |