


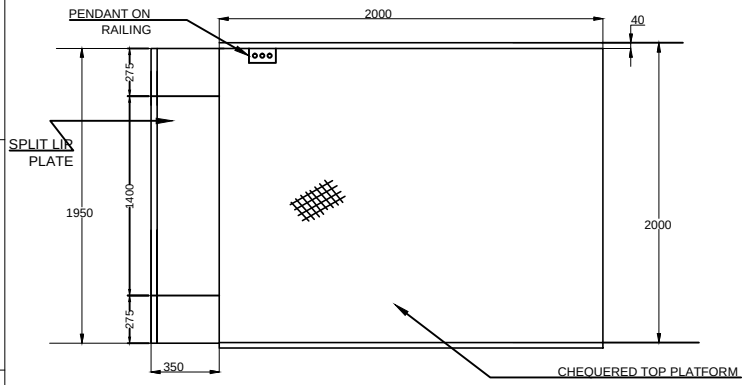


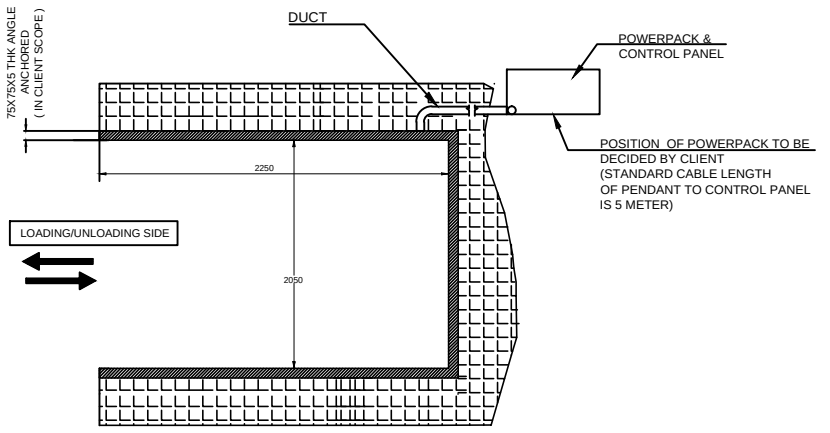

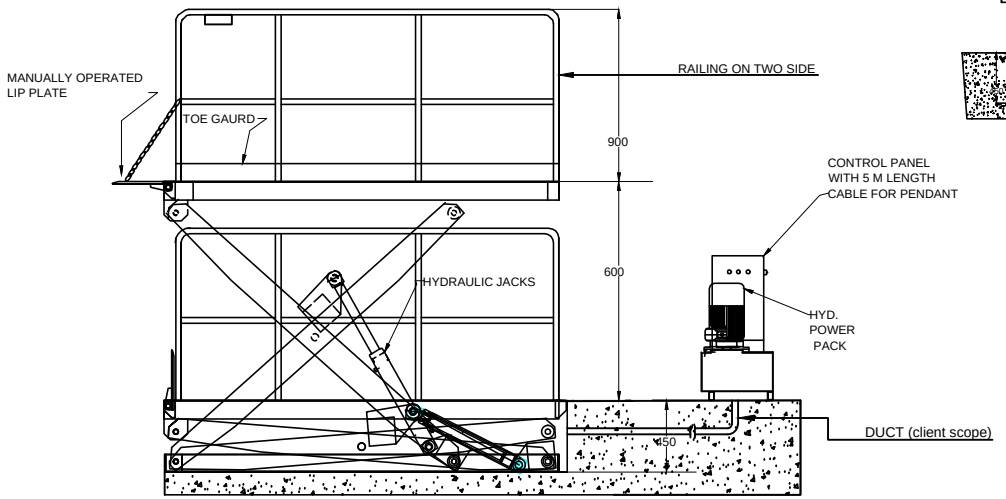

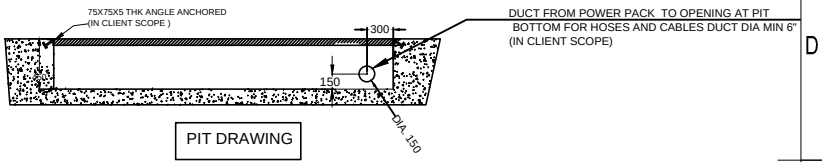

PIT DRAWING

R01	S.M.S.	9.12.2020	(1) LIFT HEIGHT CHANGED TO 600MM (2) SPLIT LIP
REV NO	DRAWN	DATE	REMARK

SPECIFICATION OF PIT MOUNTED HYDRAULIC SCISSOR LIFT- R00		
SR NO	PARAMETER	DESCRIPTION
1	CAPACITY	2 TON
2	PLATFORM SIZE(CHEQUERED)	2000mm(L) X 2000mm(W)
3	SHUT HEIGHT	450 mm
4	LIFT HEIGHT	600 mm
5	TOTAL HEIGHT	1050 mm
6	RAILING HEIGHT (2 SIDE)	900 mm
7	MANUAL LIP(1 SIDE)(PLAIN & SPLIT)	1950(L) X 350(W)
8	PIT SIZE	2250(L)X2050(W)
9	CONTROL PANEL	STANDARD
10	POWERPACK	3 HP, 3 PHASE AC
11	PENDANT	PUSH BUTTON MOUNTED ON RAILING
12	FEATURE	LIFT CUT-OFF SWITCH

RAL CODE PAINT (NIHVA STANDARD) , KINDLY INFORM IF OTHER. | RAL 1004 GOLDEN YELLOW

NOTE :
1. PIT FOR SCISSOR LIFT HAS TO BE DIAGONALLY WITHIN 3-5 MM
2. BASE OF THE PIT HAS TO BE IN WATER LEVEL AND RIGHT ANGLE TO THE VERTICAL SIDE WALLS
3. PROPER ARRANGEMENT FOR ROUTING HOSES AND CABLES HAVE TO BE MADE DEPENDING ON SITE CONDITIONS AND POSITION OF POWER PACK & IN CLIENT SCOPE.
4. COVERING REQUIRED FOR HOSES, PANEL , AND CABLES RELATED CIVIL WORK IS IN CLIENTS SCOPE ALSO PROPER DRAINAGE SYSTEM SHOULD BE PROVIDED FOR THE PIT.
5. PIT , DUCT FOR HOSE, CABLE & ALL REQUIRED CIVIL WORK IS IN CLIENT SCOPE.
6. LEVEL OF THE PIT SHOULD BE PLAIN & AT LEAST TAKE LOAD OF 6000KG.

This drawing & design is the property of NIHVA TECHNOLOGIES. Not to be sold or copied to any other concern.

TITLE PIT MOUNTED HYDRAULIC SCISOR LIFT

	NAME	SIGN	DATE
DRAWN	SIDDHESHWAR		26.11.2020
CHECK			
APPRD.			

If any queries contact : projectsupport@nihva.com

ALL DIMENSION ARE IN mm

NIHVA TECHNOLOGIES PVT. LTD.
NIHVA TECHNOLOGIES PVT. LTD. PUNE
Tel : 020 66304033
Email:- info@nihva.com
Website:- www.nihva.com

CLIENT - ADVIK HI-TECH PVT LTD

PROJECT - ADVIK HI-TECH PVT LTD

SITE LOCATION - CHAKAN ,PUNE

DWG. NO. : NIHVA/20-21/0095 | REV- R01

SCALE: NTS | WT: | SHEET: