



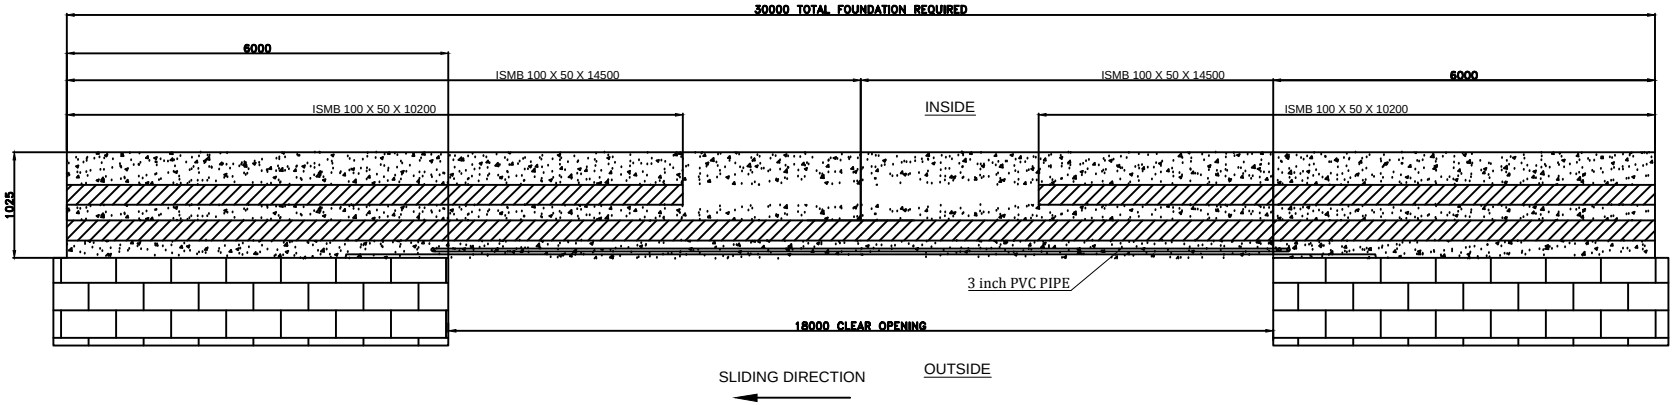

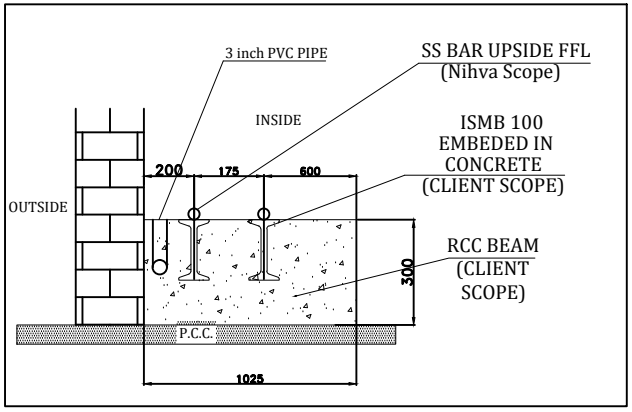

18 MTR TELESCOPIC GATE FOUNDATION

1. ISMB 100 X 50 X 10200L = 2 NOS
2. ISMB 100 X 50 X 14500L = 2 NOS

This drawing & design is the property of NIHVA TECHNOLOGIES. Not to be sold or copied to any other concern.

TITLE	FOUNDATION FOR 18MTR SLIDING GATE			NIHVA TECHNOLOGIES PVT. LTD. PUNE Tel : 020 66304033 Email:- info@nihva.com Website:- www.nihva.com	
	NAME	SIGN	DATE		
DRAWN	P.V.A		11.10.19	CLIENT - ASHOK CONSTRUCTION	
CHECK				PROJECT - JOHN DEERE	
REV.				SITE LOCATION - RANJANGAON	
APPROVAL				DWG. NO. : NIHVA/19-20/0122	
If any queries contact : projects@nihva.com				SCALE: NTS	WT: SHEET: 01 OF 01
ALL DIMENSION ARE IN mm					