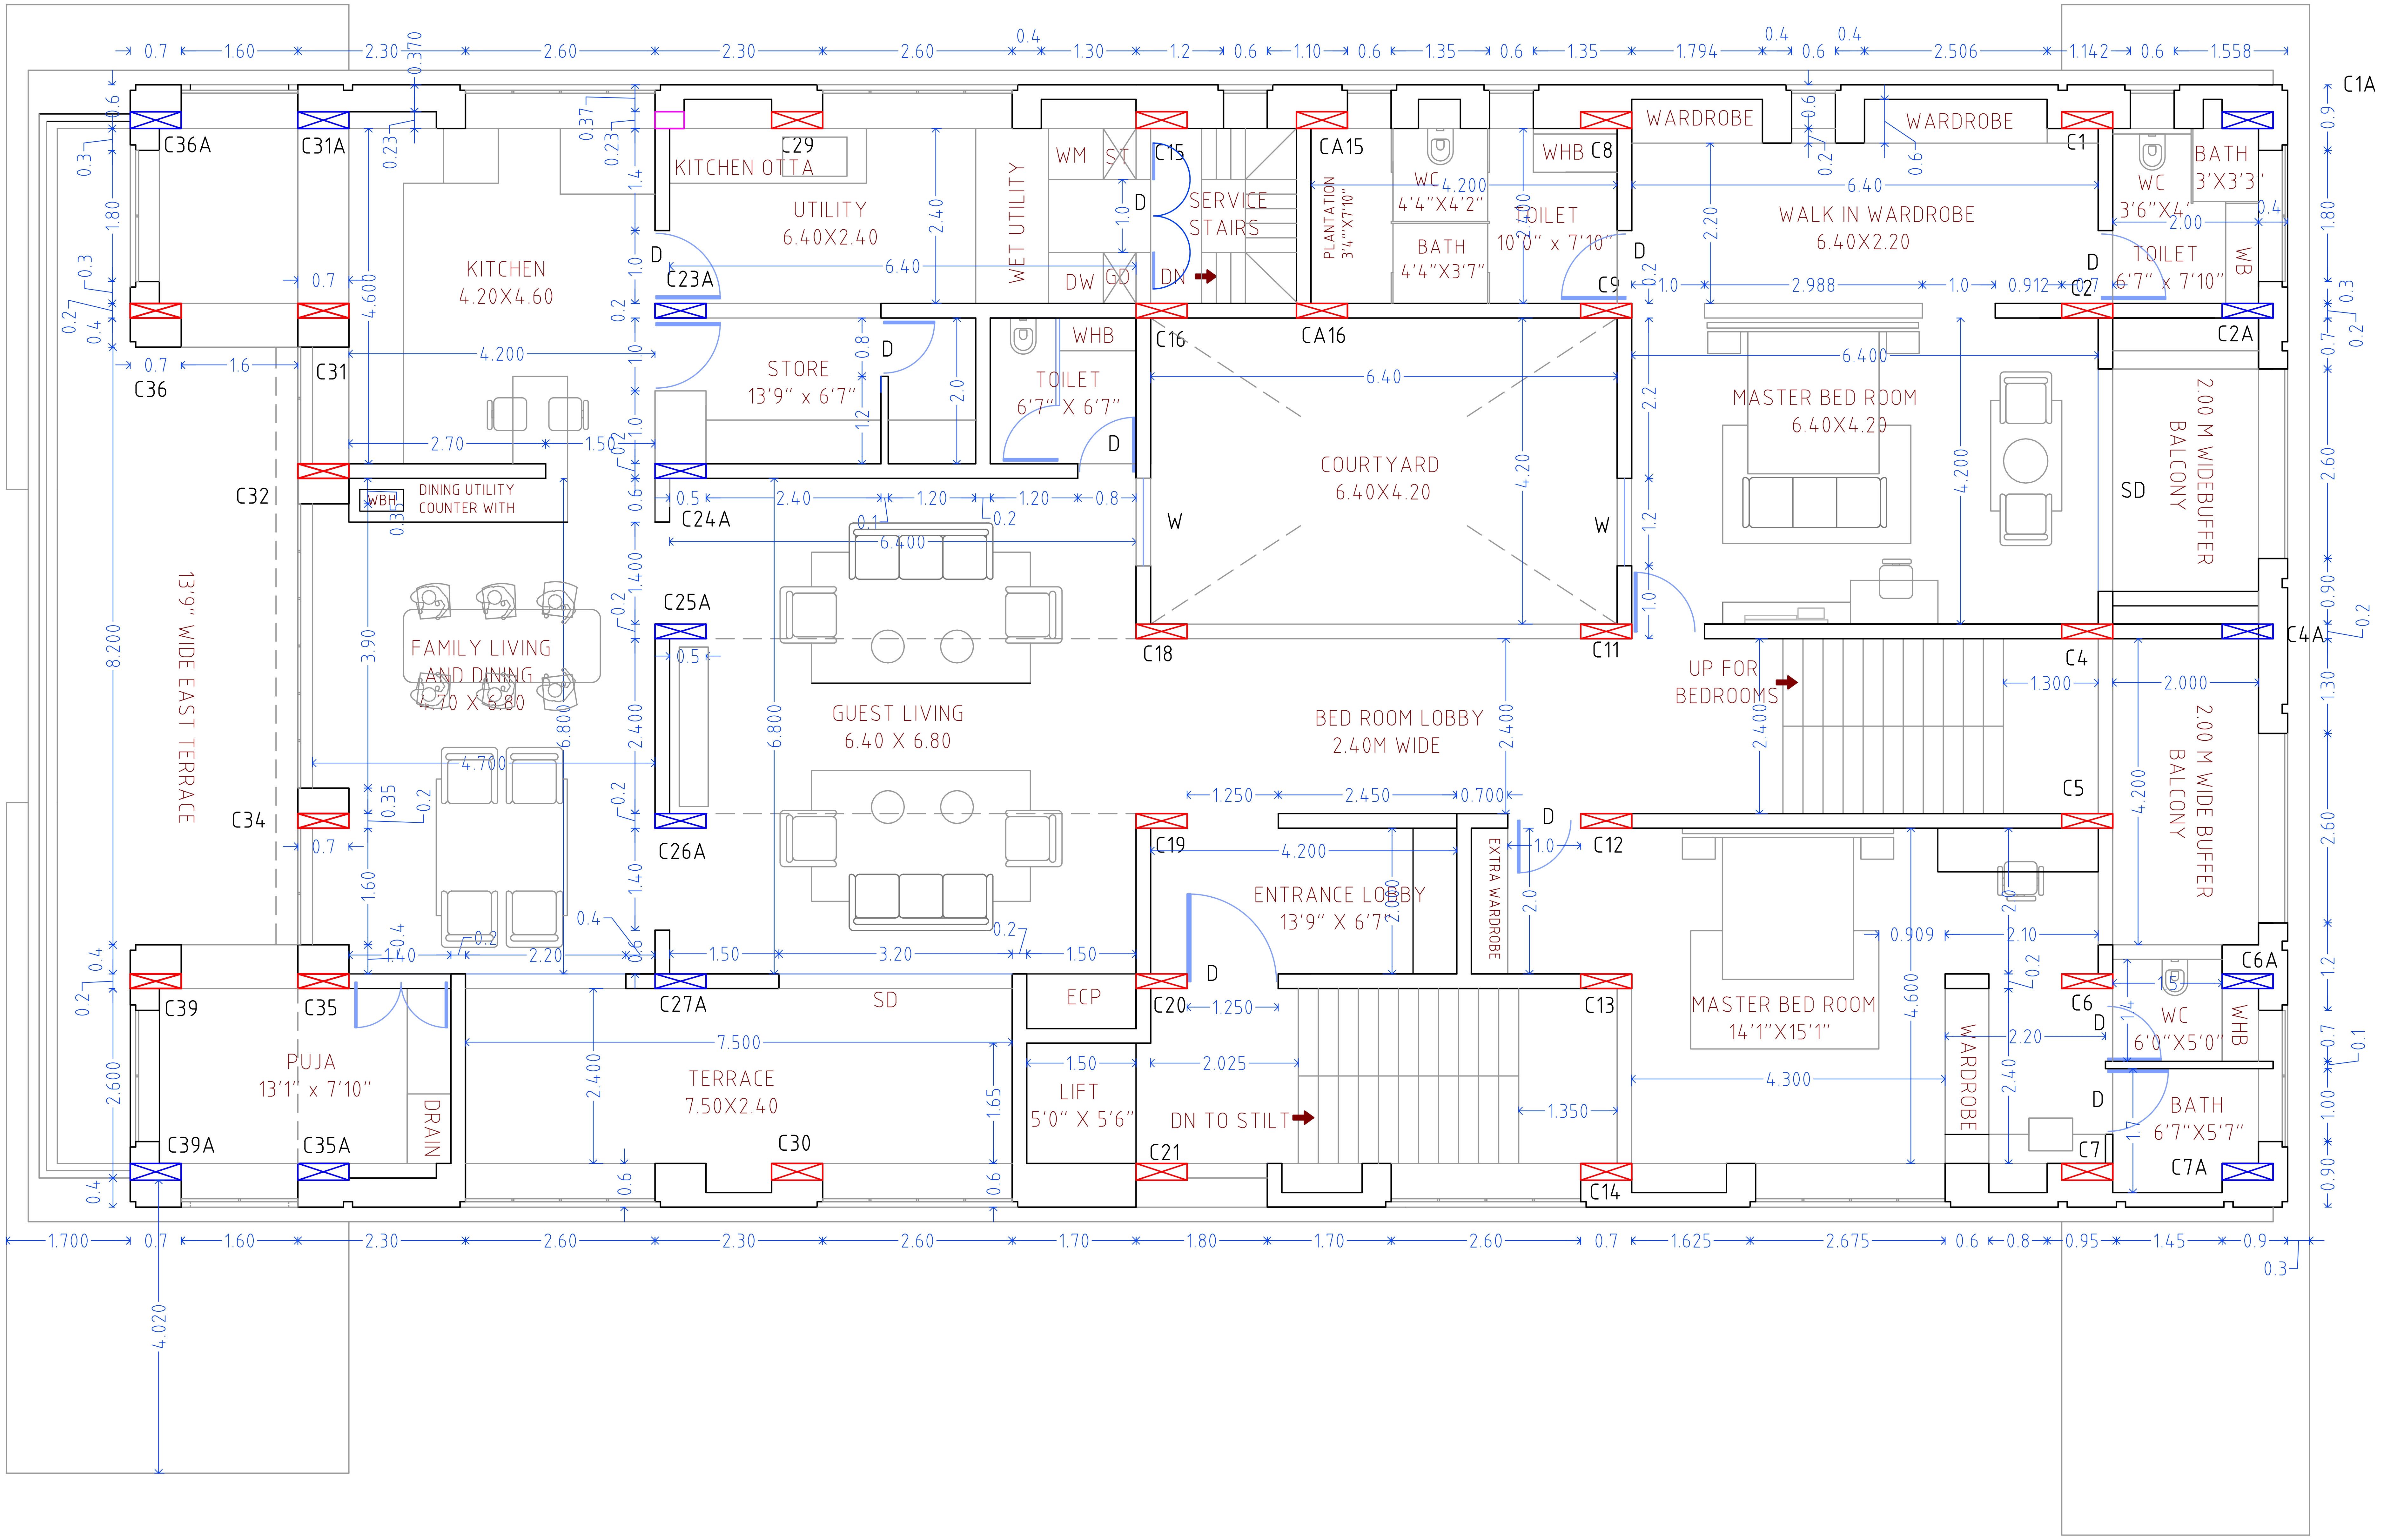
13'9" WIDE EAST TERRACE
KITCHEN
4.20X4.60
KITCHEN OTTA
UTILITY
6.40X2.40
WET UTILITY
WM
ST
DW
GD
SERVICE
STAIRS
DN
PLANTATION
3'4""X7'10"
WC
4'4"X4'2"
BATH
4'4"X3'7"
TOILET
10'0" x 7'10"
WHB
WARDROBE
WALK IN WARDROBE
6.40X2.20
BATH
3'X3'3'
WC
3'6"X4'
TOILET
6'7" x 7'10"
WB
STORE
13'9" x 6'7"
TOILET
6'7" X 6'7"
WHB
COURTYARD
6.40X4.20
W
MASTER BED ROOM
6.40X4.20
2.00 M WIDEBUFFER
BALCONY
SD
DINING UTILITY
COUNTER WITH
WBH
FAMILY LIVING
AND DINING
4.70 X 6.80
GUEST LIVING
6.40 X 6.80
BED ROOM LOBBY
2.40M WIDE
UP FOR
BEDROOMS
2.00 M WIDE BUFFER
BALCONY
ENTRANCE LOBBY
13'9" X 6'7"
EXTRA WARDROBE
MASTER BED ROOM
14'1"X15'1"
WARDROBE
WC
6'0"X5'0"
WHB
BATH
6'7"X5'7"
PUJA
13'1" x 7'10"
DRAIN
TERRACE
7.50X2.40
SD
ECP
LIFT
5'0" X 5'6"
DN TO STILT
D
C1A
C36A
C31A
C29
C23A
C15
CA15
C8
C1
C36
C31
C32
C24A
C16
CA16
C9
C2
C2A
C25A
C18
C11
C4A
C4
C34
C26A
C19
C12
C5
C39
C35
C27A
C20
C13
C6
C6A
C39A
C35A
C30
C21
C14
C7
C7A
N

LEVEL 2 PLAN

841___MR.KAILAS SOMANI___RAW WD______WD2_____02-11-2022___1:100___AP-1DWG-WD&RCC-WD___A3L___MSK___---