




TERRACE TOP SKYLIGHT V1

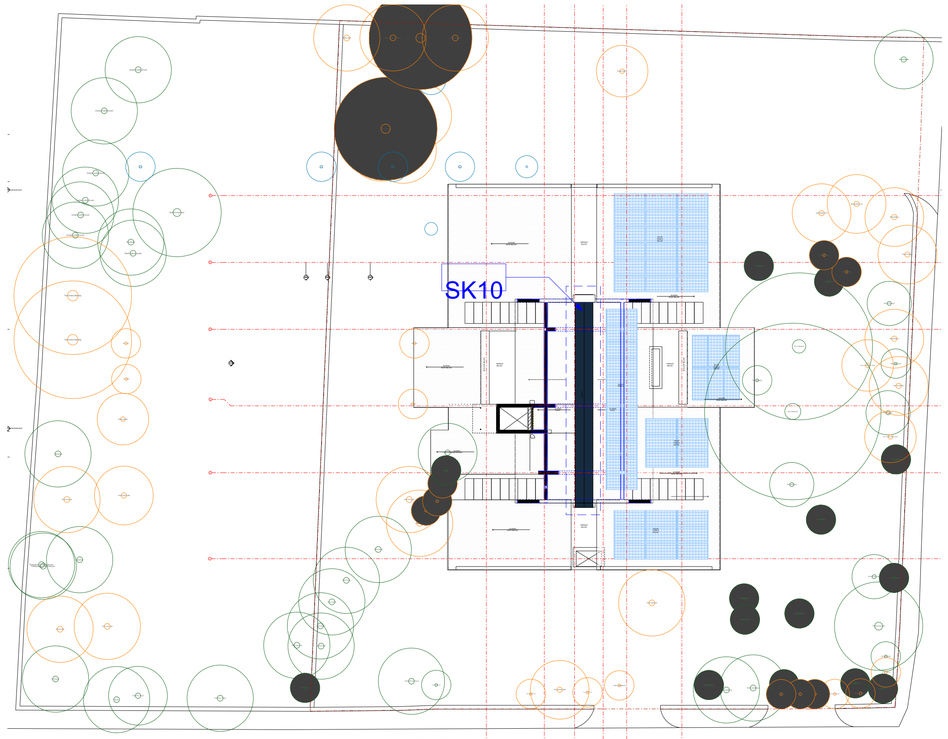

4. Top Terrace Level 1:50

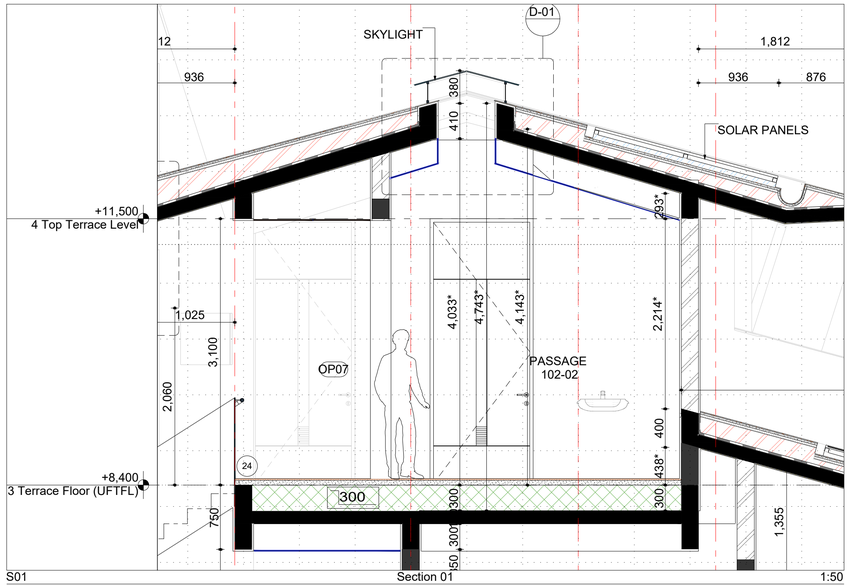


S01 Section 01 1:50

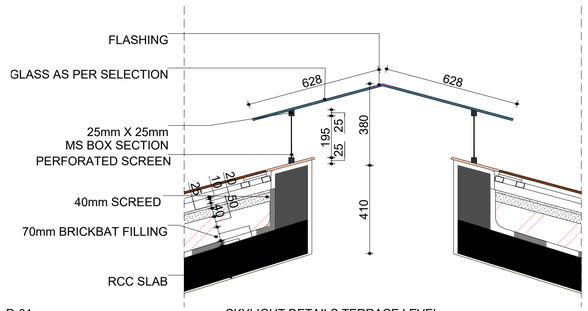

D-01 SKYLIGHT DETAILS TERRACE LEVEL 1:20

SKYLIGHT SCHEDULE

Home Story Name	Space	Nomenclature	Glass Length (mm)	Glass Width (mm)	Glass Area (SQ.FT.)	Quantity
Top Terrace Level, Taper Skylight						
	Top Terrace Central Skylight	SK - 10	14,490	1,214	189	1

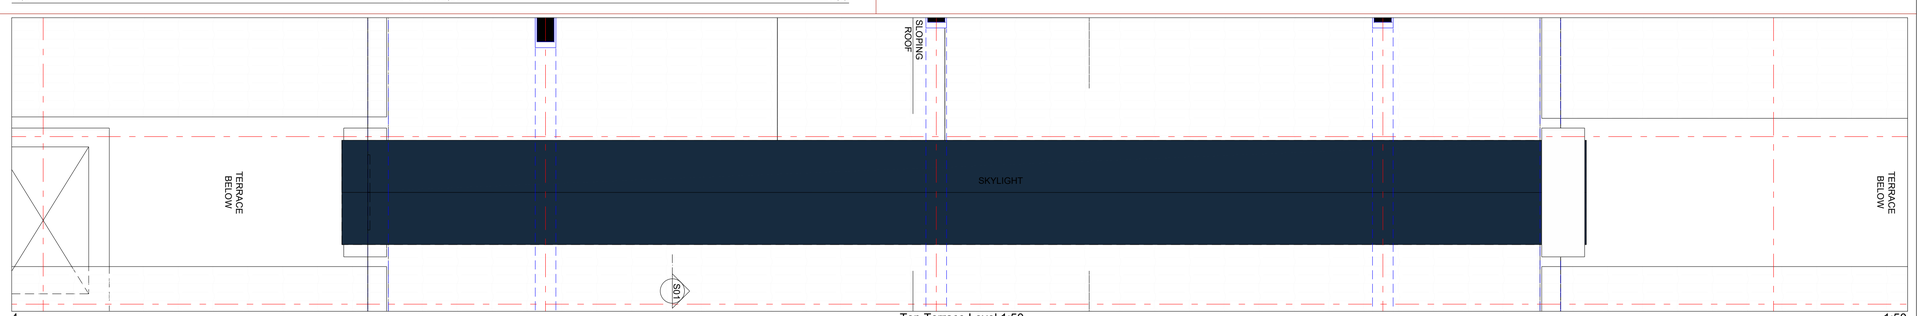

4. Top Terrace Level 1:50 1:50