


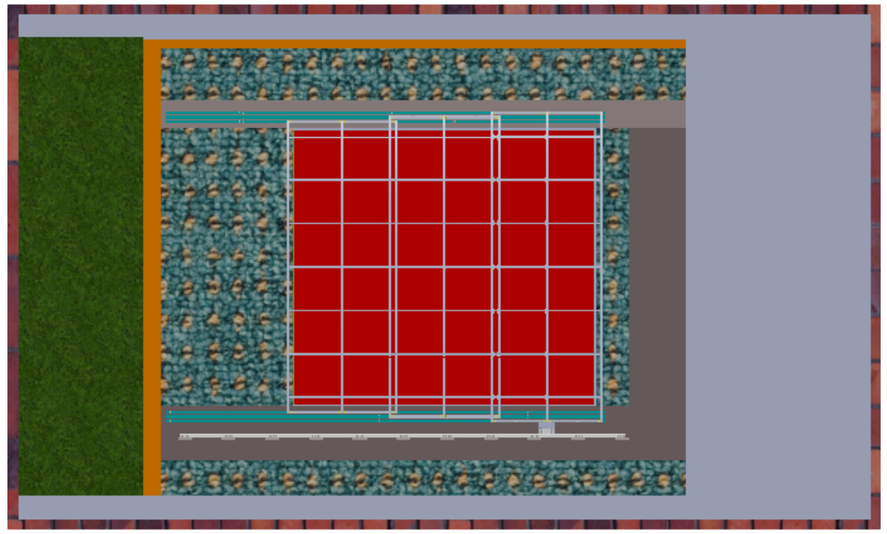


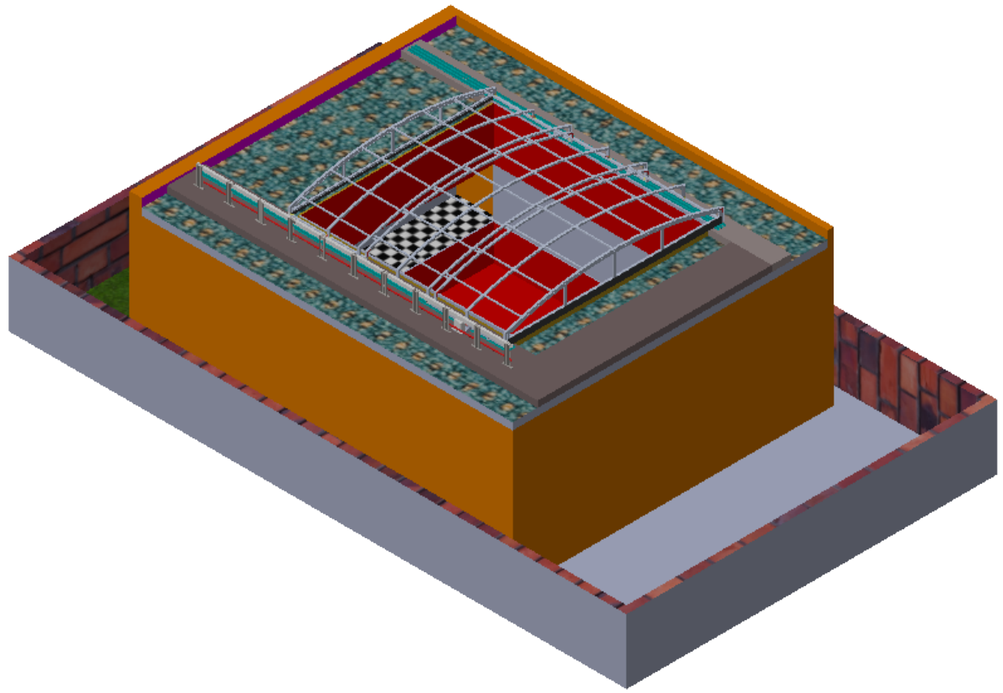


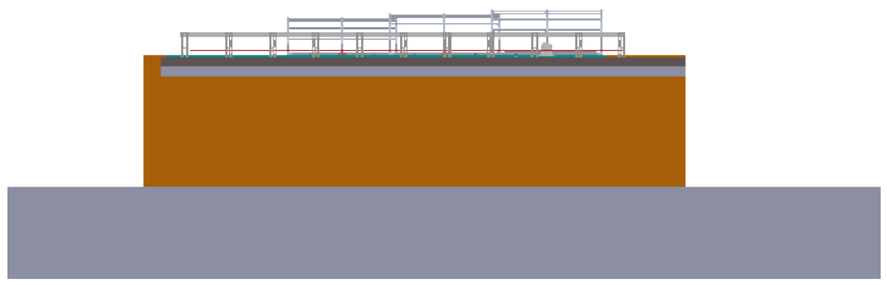


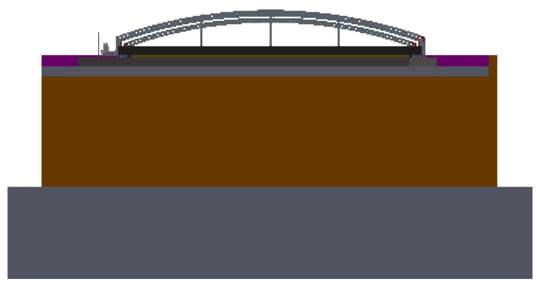



TITLE - RETRACTABLE ROOF				NIHVA TECHNOLOGIES PVT.LTD.PUNE Website - www.nihva.com
DWG NO - NTPL268-PM			QTY - 1	
	NAME	SIGNATURE	DATE	PROJECT NO - NTPL268-PM- AD
DRAWN	S.W		03-03-2025	PRODUCT - RETRACTABLE ROOF
CHK'D	P.M.		03-03-2025	SITE LOCATION - GUJARAT
APPV'D	V.T.		03-03-2025	
if any queries contact - supportautomation@nihva.com				REVISION -
ALL DIMENSION ARE IN mm			A3	SCALE - SHEET 1 OF 5

ITEM NO.	PART NUMBER	DESCRIPTION	QTY.
1	REV_01SALAVI MAM NTPL-268-PM-PANEL_01	PANEL_01 FRAME	1
2	AL Support tube SQ TUBE 40X40X1.5 MM L-734 MM	AL INTERMEDIAT SUPPORT TUBE	14
3	REV_01SALAVI MAM rivet_iso_15977_4_x_16_0	RIVET M4X16	16
4	T PLATE	JOINING PLATE	4
5	L PALTE	JOINING PLATE	8
6	L ANGLE PLATE	JOINING PLATE	8
7	REV_01SALAVI MAM PROFILE L ANGLE WELDING PLATE	JOINING PLATE	4
8	REV_01SALAVI MAM BEARING BLOCK ASM WITH SHOULDER BOLT	SLIDING BLOCK	4
9	REV_01SALAVI MAM ENCLOSURE NTPL-268-PM-PANEL_01	ENCLOSURE _01	1
10	REV_01EPDM RUBBER		1
11	PROFILE WELDING PLATE AL	AL 6063-T4	2

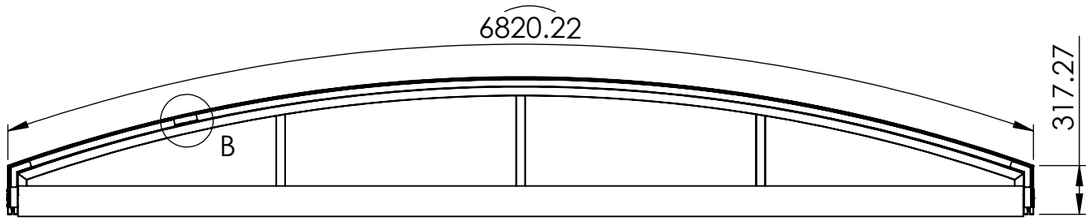

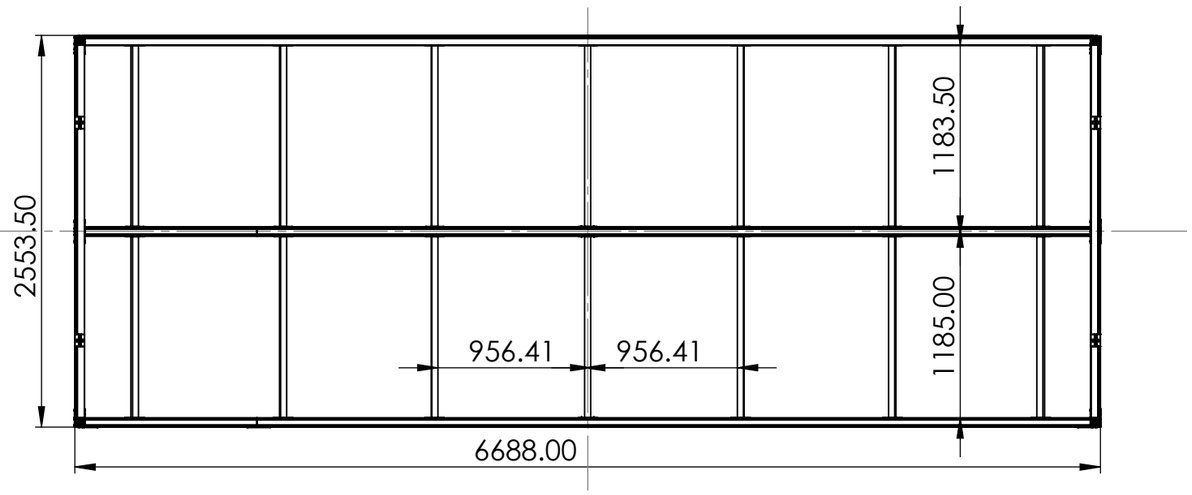

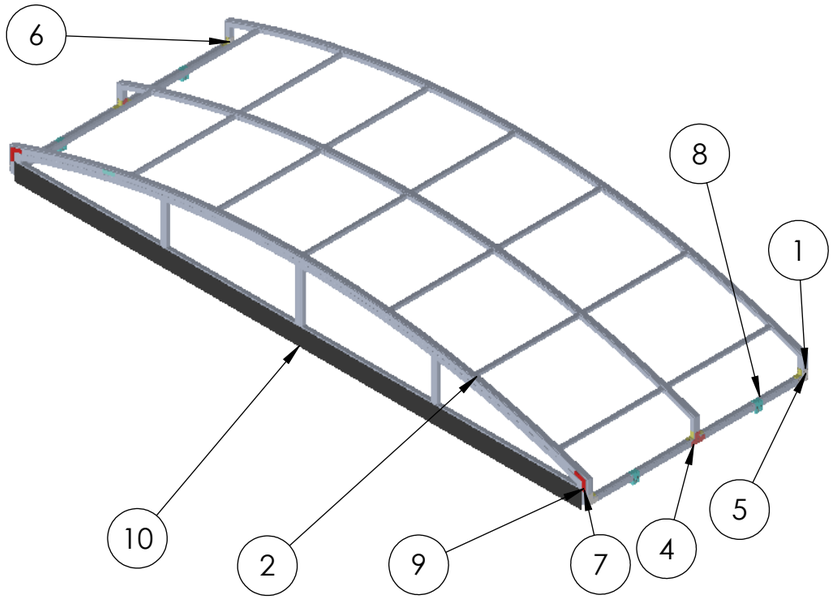

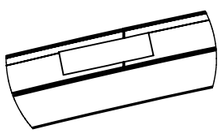


DETAIL B
SCALE 1 : 10


WELDING PLATE
PROFILE WELDING PLATE


PANEL NO 1 ASM

TITLE - RETRACTABLE ROOF				NIHVA TECHNOLOGIES PVT.LTD.PUNE Website - www.nihva.com
DWG NO - NTPL276-PM			QTY - 1	
	NAME	SIGNATURE	DATE	PROJECT NO - NTPL276-PM
DRAWN	S.W		16-05-2025	PRODUCT - RETRACTABLE ROOF
CHK'D	P.M.		16-05-2025	SITE LOCATION - GUJARAT
APPV'D	V.T.		16-05-2025	
if any queries contact - supportautomation@nihva.com				REVISION -
ALL DIMENSION ARE IN mm			A3	SCALE - SHEET 2 OF 5

ITEM NO.	PART NUMBER	DESCRIPTION	QTY.
1	REV_01SALAVI MAM NTPL-268-PM-PANEL_02	PANEL_02 FRAME	1
2	AL Support tube SQ TUBE 40X40X1.5 MM L-734 MM	AL INTERMEDIAT SUPPORT TUBE	14
3	REV_01SALAVI MAM rivet_iso_15977_4_x_16_0	RIVET M4X16	15
4	T PLATE	JOINING PLATE	4
5	L PALTE	JOINING PLATE	8
6	L ANGLE PLATE	JOINING PLATE	8
7	REV_01SALAVI MAM PROFILE L ANGLE WELDING PLATE	JOINING PLATE	4
8	REV_01SALAVI MAM BEARING BLOCK ASM WITH SHOULDER BOLT	SLIDING BLOCK	4

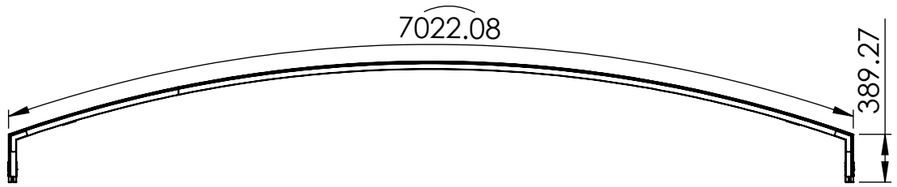


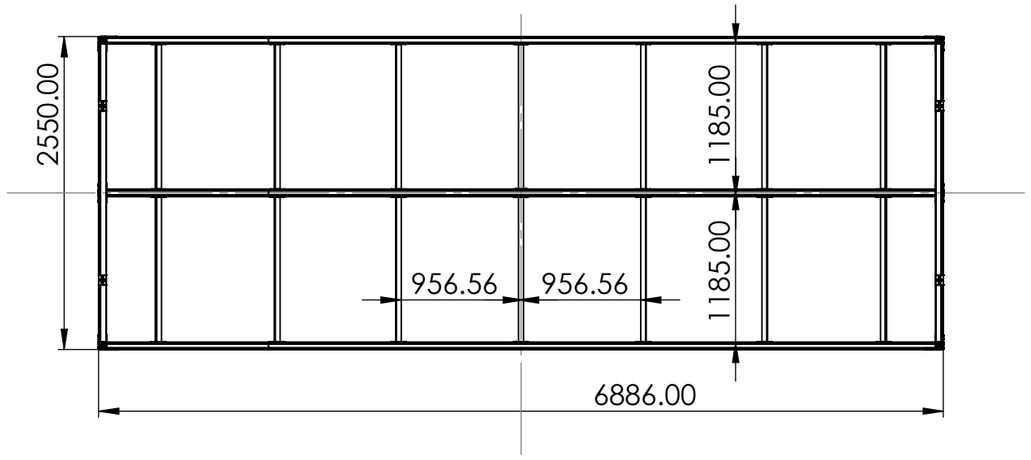


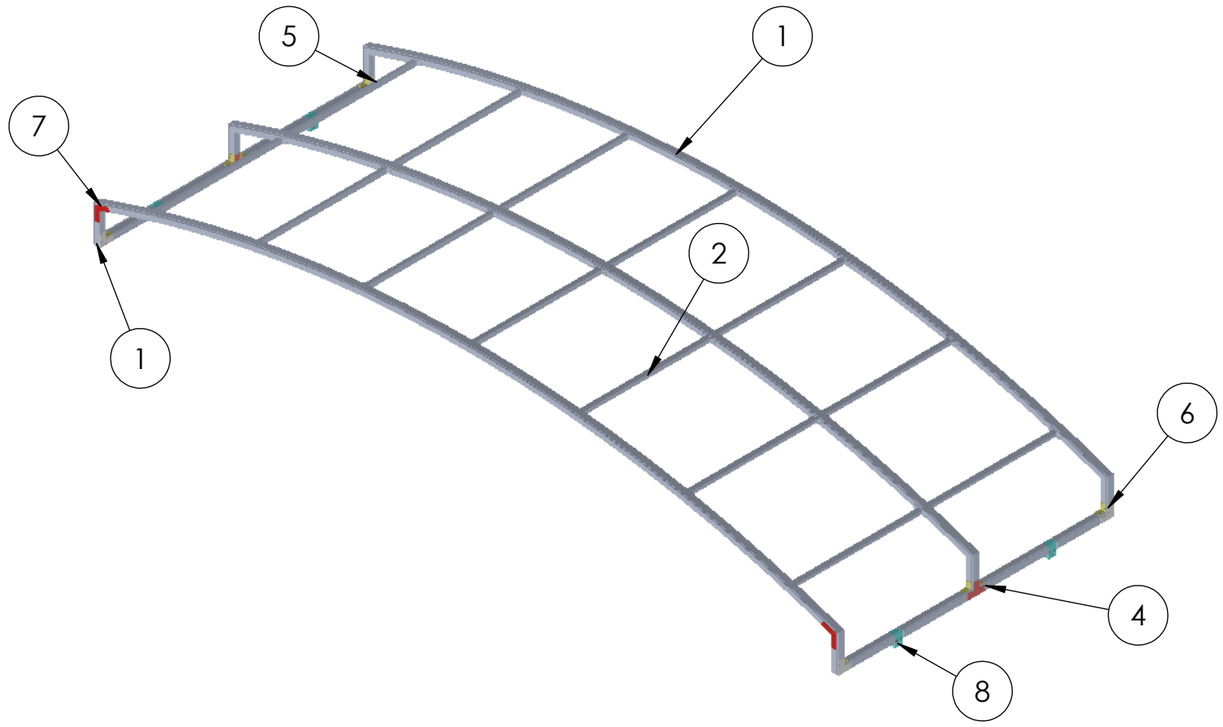


NOTE:
PANEL NO 02 ASM

TITLE - RETRACTABLE ROOF				NIHVA TECHNOLOGIES PVT.LTD.PUNE
DWG NO - NTPL276-PM			QTY - 1	Website - www.nihva.com
	NAME	SIGNATURE	DATE	PROJECT NO - NTPL276-PM
DRAWN	S.W		16-05-2025	PRODUCT - RETRACTABLE ROOF
CHK'D	P.M.		16-05-2025	SITE LOCATION - GUJARAT
APPV'D	V.T.		16-05-2025	
if any queries contact - supportautomation@nihva.com				REVISION -
ALL DIMENSION ARE IN mm			A3	SCALE - SHEET 3 OF 5

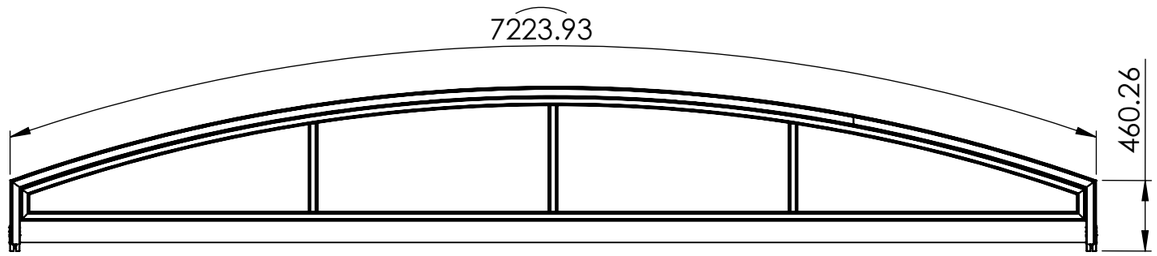

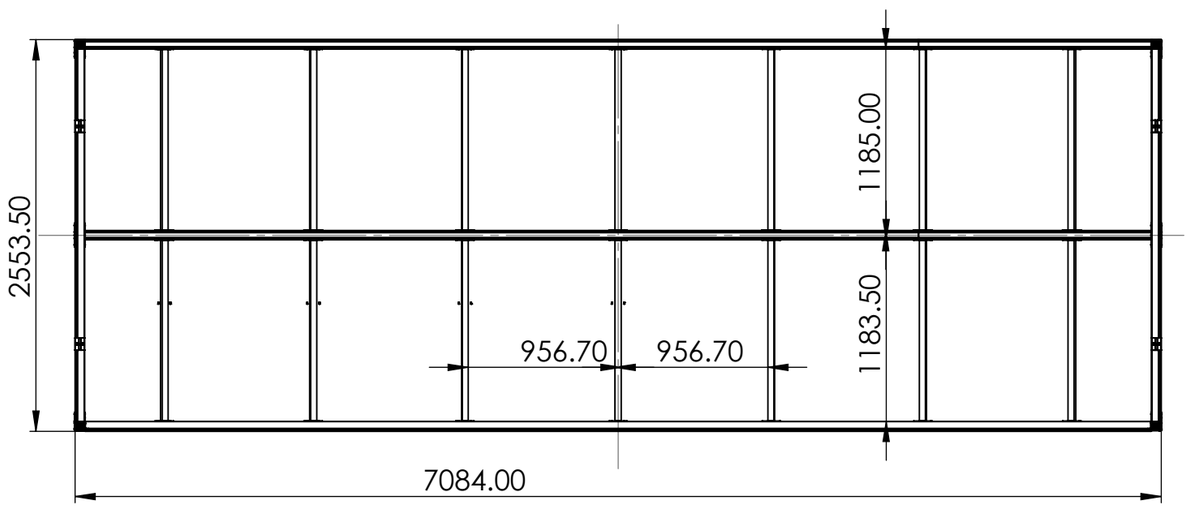


ITEM NO.	PART NUMBER	DESCRIPTION	QTY.
1	REV_01SALAVI MAM NTPL-268-PM-PANEL_03	PANEL_03 FRAME	1
2	AL Support tube SQ TUBE 40X40X1.5 MM L-734 MM	AL INTERMEDIAT SUPPORT TUBE	14
3	REV_01SALAVI MAM rivet_iso_15977_4_x_16_0	RIVET M4X16	32
4	T PLATE	JOINING PLATE	4
5	L PALTE	JOINING PLATE	8
6	L ANGLE PLATE	JOINING PLATE	8
7	REV_01SALAVI MAM PROFILE L ANGLE WELDING PLATE	JOINING PLATE	1
8	REV_01SALAVI MAM BEARING BLOCK ASM WITH SHOULDER BOLT	SLIDING BLOCK	4
9	REV_01SALAVI MAM ENCLOSURE NTPL-268-PM-PANEL_03	ENCLOSURE _03	1
10	REV_01EPDM RUBBER_BIG PANEL		1

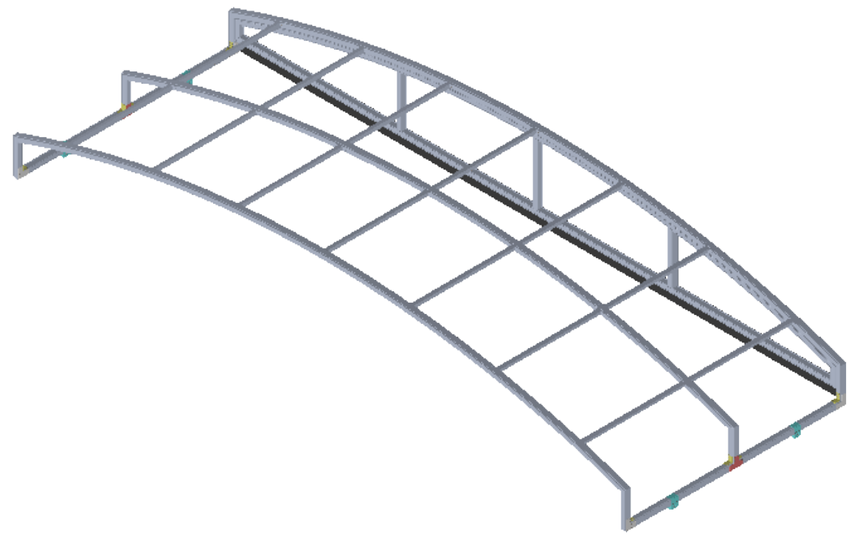

NOTE
PANEL NO 03 ASM

TITLE - RETRACTABLE ROOF				NIHVA TECHNOLOGIES PVT.LTD.PUNE
DWG NO - NTPL276-PM			QTY - 1	Website - www.nihva.com
	NAME	SIGNATURE	DATE	PROJECT NO - NTPL276-PM
DRAWN	S.W		16-05-2025	PRODUCT - RETRACTABLE ROOF
CHK'D	P.M.		16-05-2025	SITE LOCATION - GUJARAT
APPV'D	V.T.		16-05-2025	
if any queries contact - supportautomation@nihva.com				REVISION -
ALL DIMENSION ARE IN mm			A3	SCALE - SHEET 4 OF 5

ITEM NO.	PART NUMBER	DESCRIPTION	QTY.
1	PROFILE WELDING PLATE AL	AL 6063-T4	1

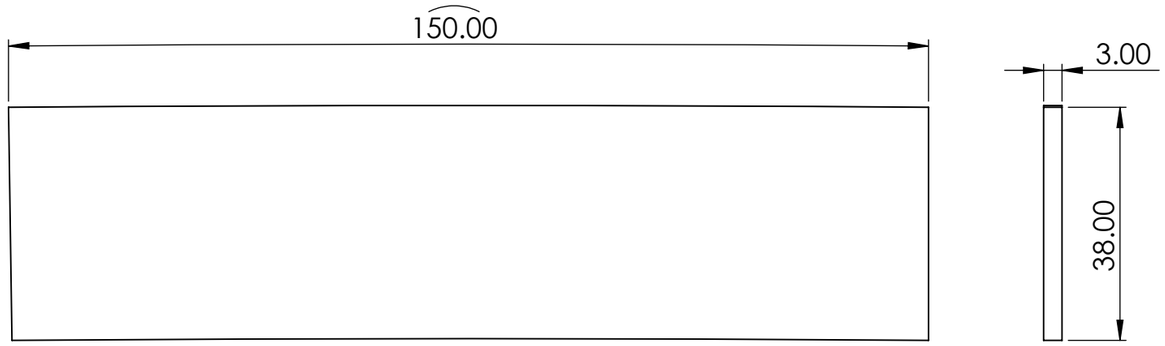

NOTE:
PROFILE WELDING PLATE AL-6063 T4
ALL PROFILE WELD THIS PLATE IS USED
LASER CUTTING
WELD PLATE 150*38*3MM THK

TITLE - RETRACTABLE ROOF				NIHVA TECHNOLOGIES PVT.LTD.PUNE
DWG NO - NTPL276-PM			QTY - 1	Website - www.nihva.com
	NAME	SIGNATURE	DATE	PROJECT NO - NTPL276-PM
DRAWN	S.W		16-05-2025	PRODUCT - RETRACTABLE ROOF
CHK'D	P.M.		16-05-2025	SITE LOCATION - GUJARAT
APPV'D	V.T.		16-05-2025	
if any queries contact - supportautomation@nihva.com				REVISION -
ALL DIMENSION ARE IN mm			A3	SCALE - SHEET 5 OF 5