

DRAWING

REV DESCRIPTION	DATE	REV NO
	20-11-2025	REV 00
1.		

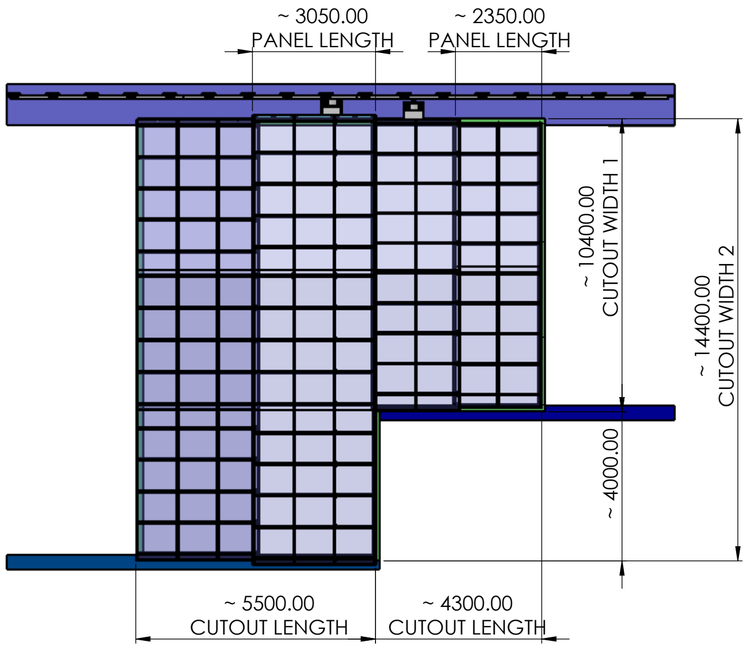

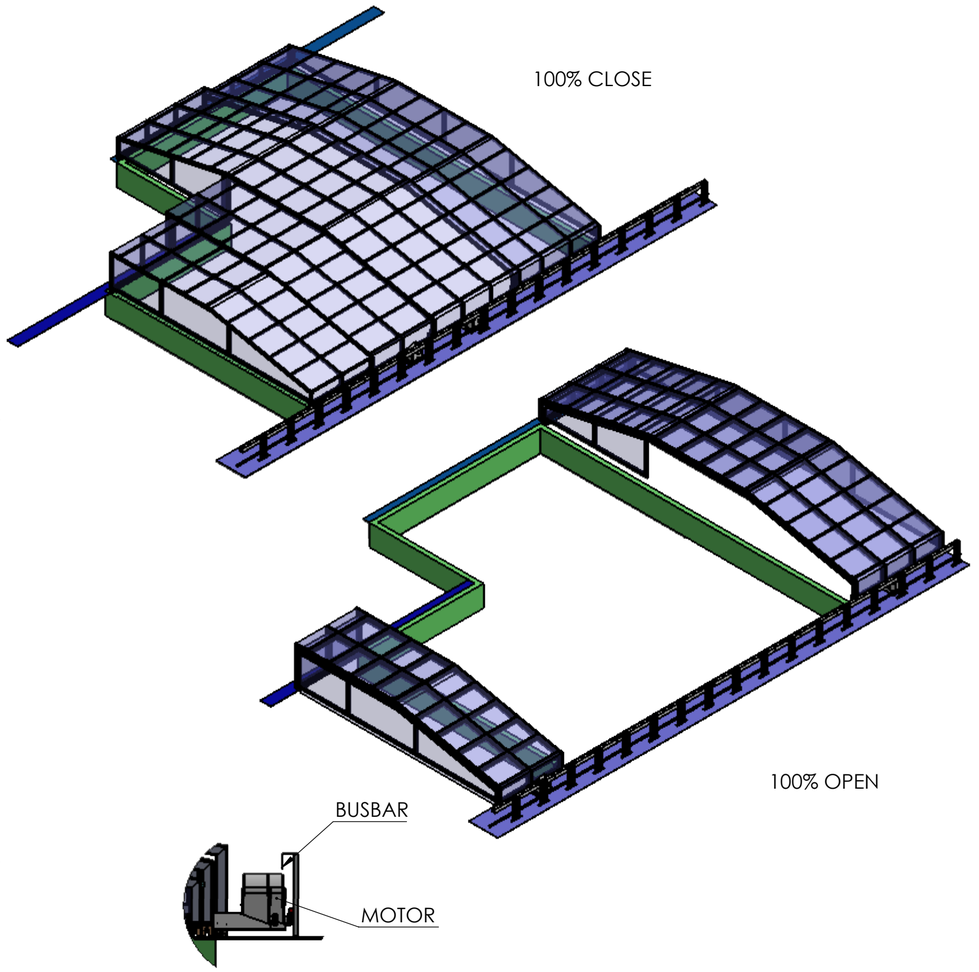

DETAIL B
SCALE 1 : 30

SLIDING DIRECTION





TECHANICAL SPECIFICATIONS

ROOF COVERING MATERIAL	3 MM PC SHEET
GUIDE RAILS	GUIDE RAILS T-75-1B (M.S)
ROLLING WHEEL	NIHVA MAKE
MOTOR	NICE RB
PANEL STRUCTURE	M.S RECT. TUBE
HARDWARE	SS 304
MECHANISAM	RACK AND PINION

NOTE : THIS DRAWING ONELY FOR CONCEPT

SPECIAL INSTRUCTION'S :

TITLE - ROOF AUTOMATION

DWG NO - NTPL-000-PM-001-00-00-00

NIHVA Technologies Pvt. Ltd.

NIHVA TECHNOLOGIES PVT.LTD.PUNE
Website - www.nihva.com

	NAME	SIGNATURE	DATE
DRAWN	J.P.		20-11-2025
CHK'D	B.S.		20-11-2025
APPV'D	V.T.		20-11-2025

PRODUCT - RETRACTABLE ROOF

PROJECT NO - NTPL-000-PM | REVISION - 00

SITE LOCATION - HYDERABAD

MATRIAL - | QTY - 1

If any queries contact - Design@nihva.com

ALL DIMENSION ARE IN mm | A2

PROJECTION METHOD:

SCALE :

SHEET 1 OF 1