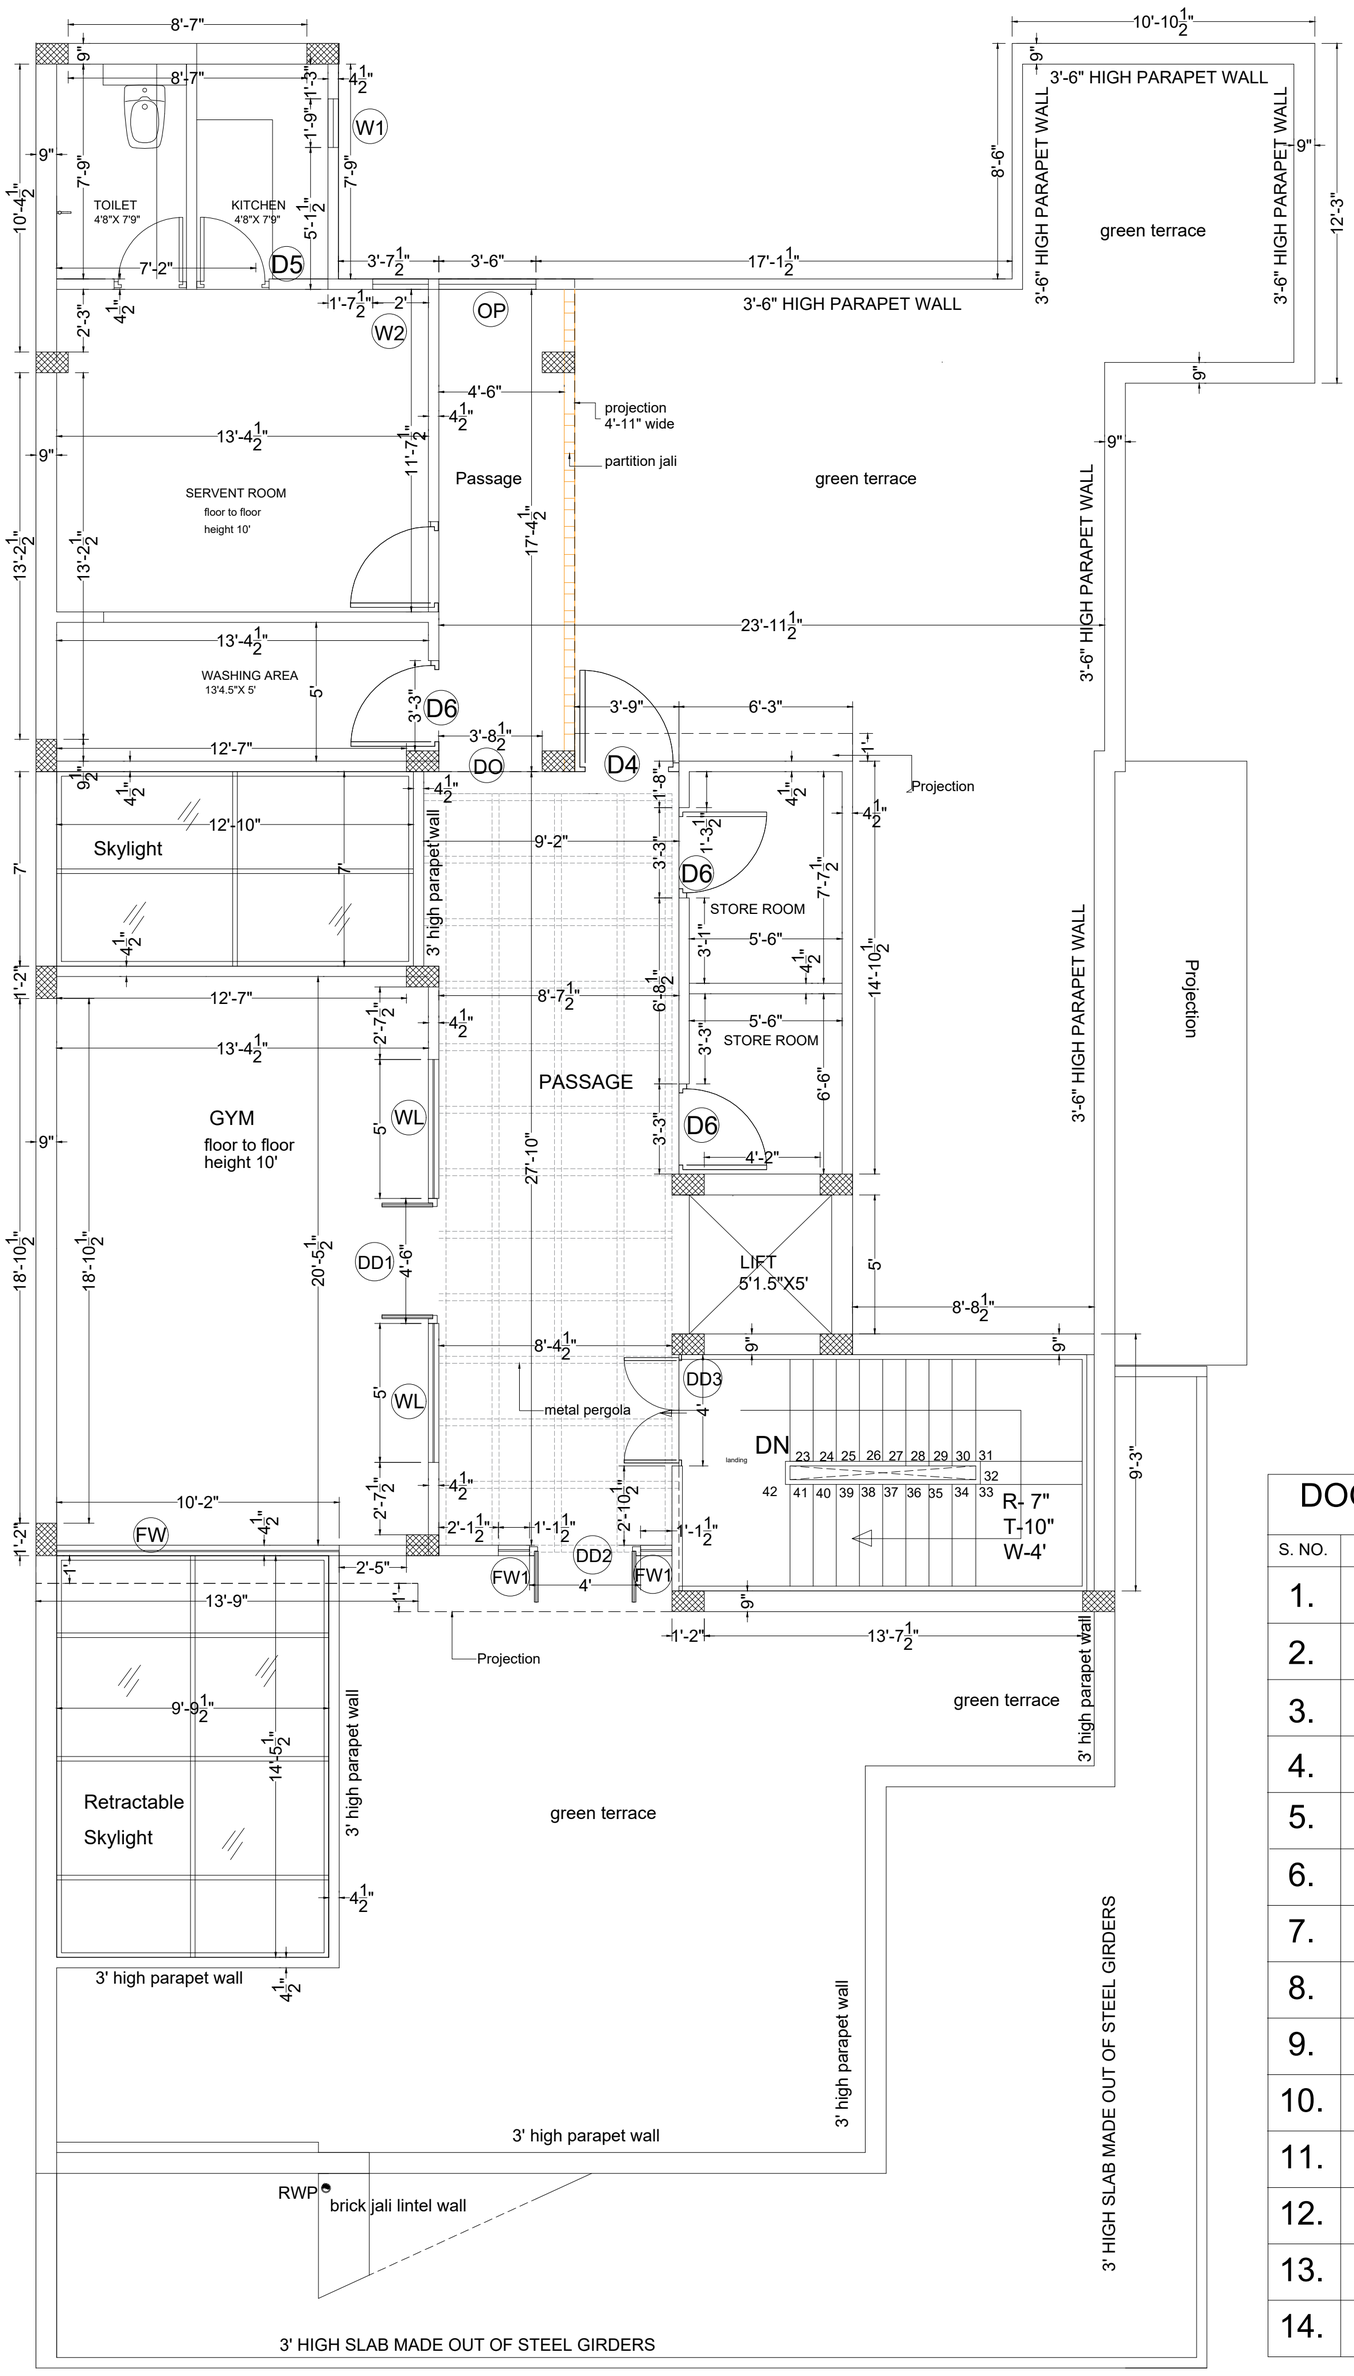


TERRACE LEVEL

DOOR & WINDOW SCHEDULE (TERRACE FLOOR)

S. NO.	TYPE	SIZE	SILL	LINTEL	NO.
1.	DD1	4'-6" X 7'		7'	
2.	DD2	4' X 7'		7'	
3.	DD3	4' X 7'		7'	
4.	DO	$3'\text{-}8\frac{1}{2}"$ X 7'		7'	
5.	OP	3'-6" X 3'-6"'		7'	
6.	D6	3'-3" X 7'		7'	
7.	D5	2'-7" X 7'		7'	
8.	D4	3'-9" X 7'		7'	
9.	W1	1'-9" X 4'	3'	7'	
10.	W2	2' X 4'	3'	7'	
11.	WL	5' X 4'	3'	7'	
12.	FW	10'-2" X 3'-6"	3'-6"	7'	
13.	FW1	$1'\text{-}1\frac{1}{2}"$ X 7'		7'	
14.					