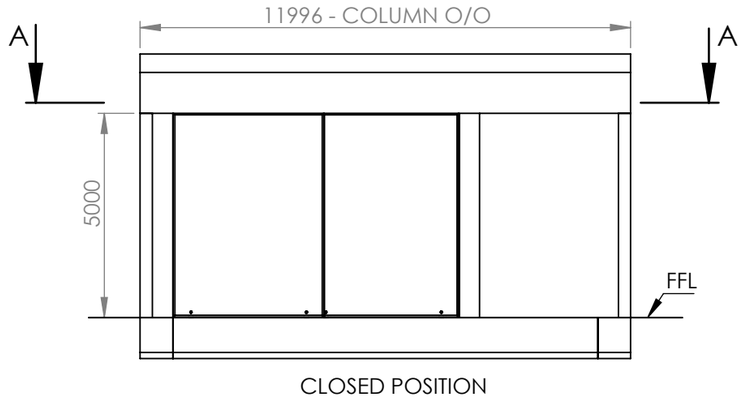
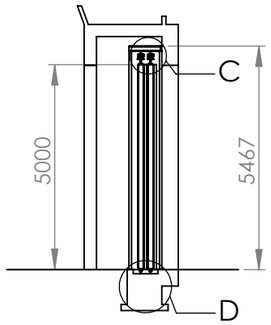
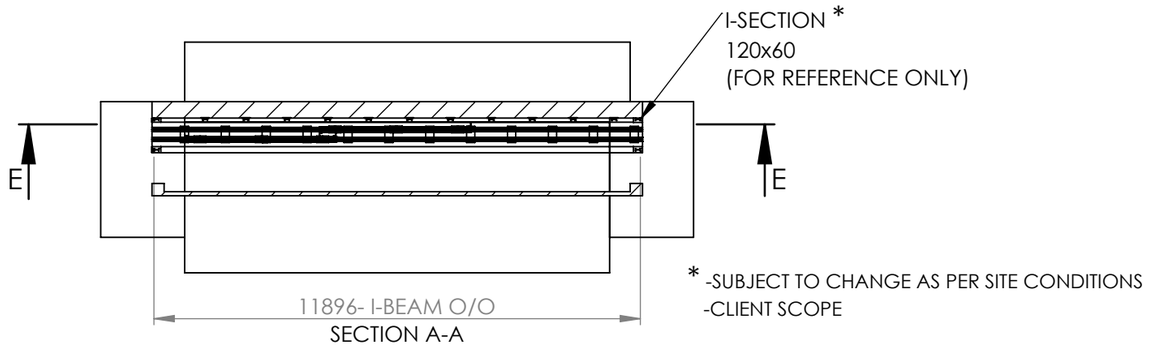


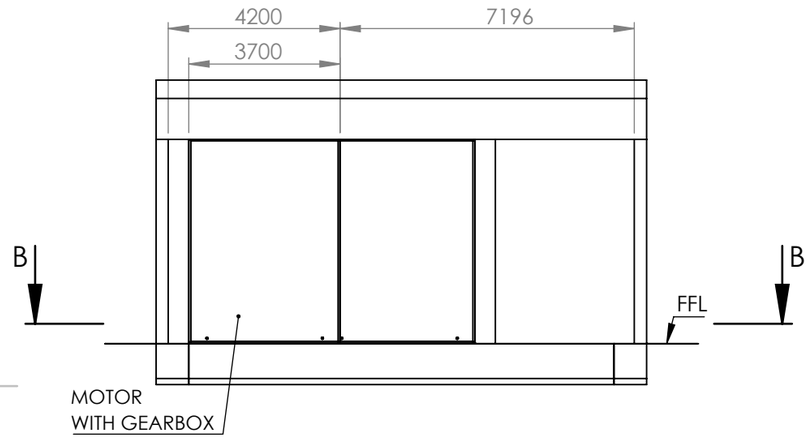

CLOSED POSITION

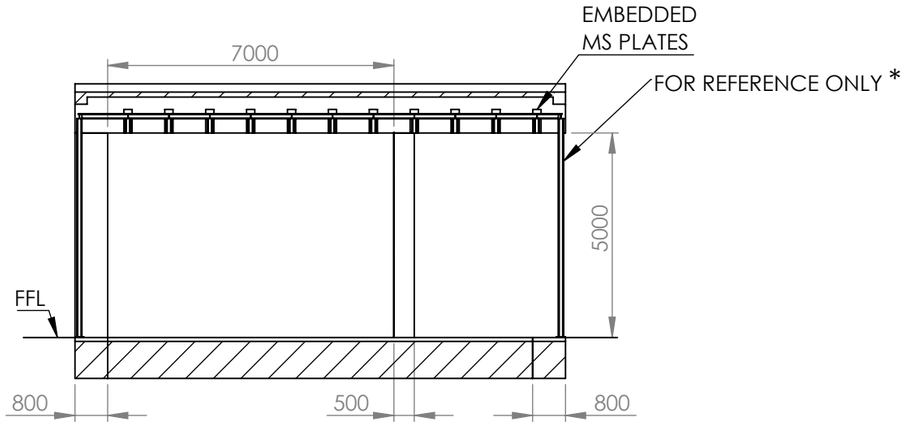


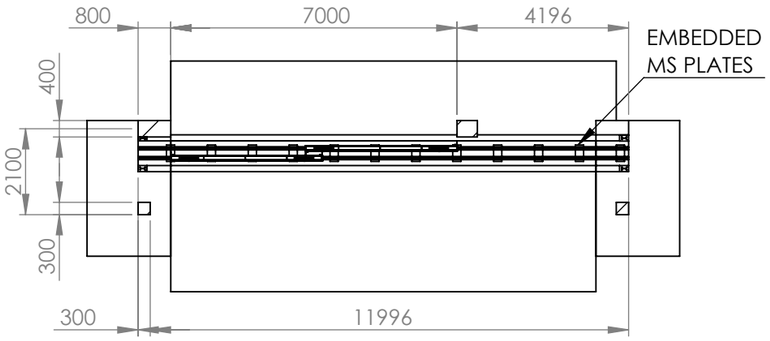

SECTION A-A

* -SUBJECT TO CHANGE AS PER SITE CONDITIONS
-CLIENT SCOPE

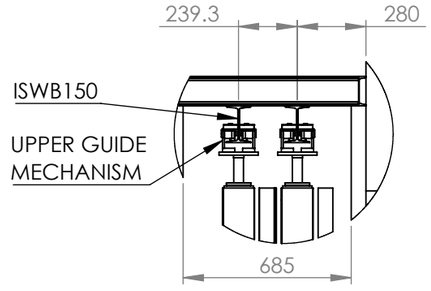


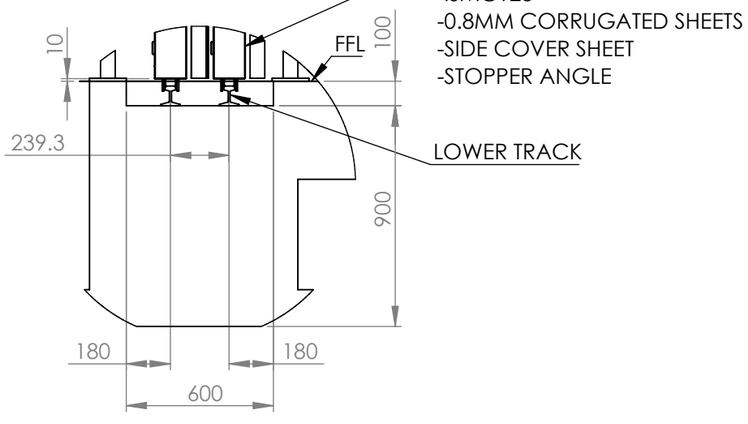

SECTION E-E



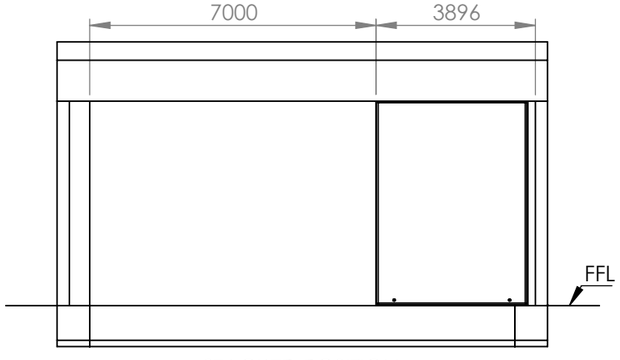

SECTION B-B



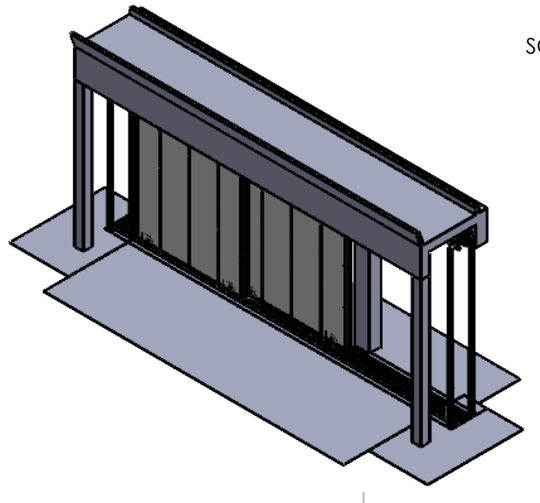

DETAIL C
SCALE 1 : 25




DETAIL D
SCALE 1 : 25




STACKED POSITION



| TITLE : HANGING SLIDING DOOR | | | | NIHVA TECHNOLOGIES PVT LTD |
|---|---|---|---|---|
| | NAME | SIGN | DATE | CLIENT NAME : ISRO |
| DRAWN | BHARATI SABALE | | 23-12-2024 | PRODUCT NAME : HANGING SLIDING DOOR |
| CHK'D | SURAJ WARALE | | 23-12-2024 | SITE LOCATION : ALUVA, KERALA |
| APPV'D | VIJAY T | | 23-12-2024 | DWG NO. GA — A3 — REVISION : 1 |
| | | DIMENSIONS ARE IN MILLIMETERS | | SCALE: — SHEET 1 OF 1 |