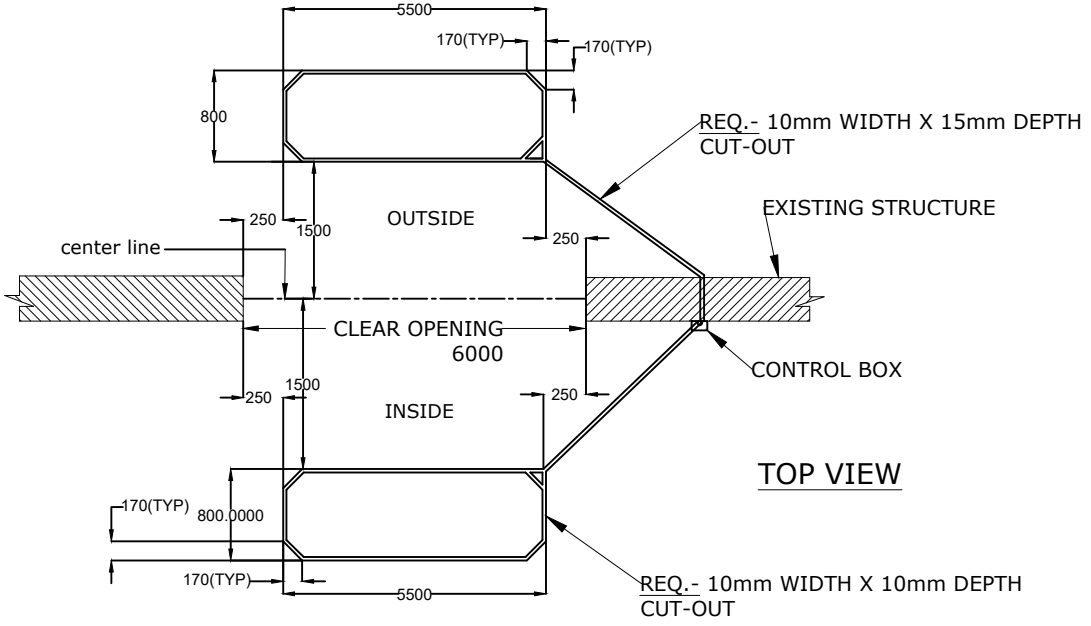


CLEAR WIDTH (CW)	CLEAR HEIGHT (CH)	QUANTITY
6000	6000	01

This drawing & design is the property of NIHVA TECHNOLOGIES. Not to be sold or copied to any other concern.

TITLE:- FLOOR CUT-OUT FOR LOOP DETECTOR FOR HIGH SPEED DOOR

NIHVA TECHNOLOGIES PVT. LTD. PUNE
Tel : 020 66304033
Email:- info@nihva.com
Website:- www.nihva.com

	NAME	DATE	SIGN
DRAWN	S.J	13/07/2024	
CHECK	B.B	13/07/2024	
APPRD.	V.T	13/07/2024	

CLIENT -

LOCATION -

PRODUCT - HSD | QTY:- 01

If any queries contact : design@nihva.com | DWG NO:-NIHVA/24-25/00XX | REV- 0

ALL DIMENSION ARE IN mm | SCALE: NTS | SCALE:-- 1:1 | SHEET: 01 OF 01