


ELEVATION VIEW

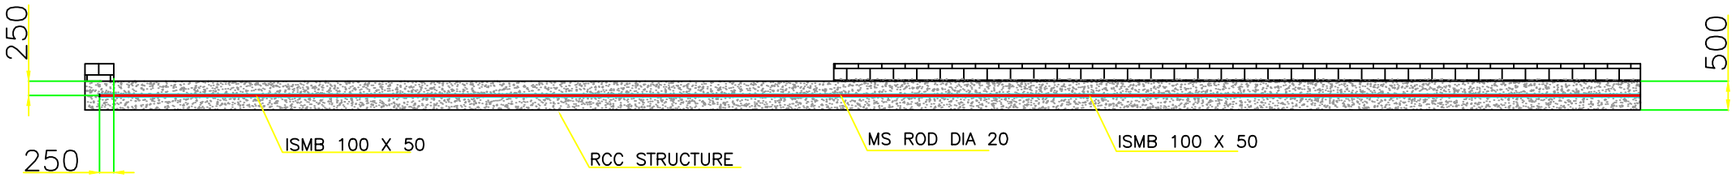

PLAN

Note-
1. All dimension are in mm.
2. All civil work is under client scope.

This drawing & design is the property of NIHVA TECHNOLOGIES. Not to be sold or copied to any other concern.

MANUAL SLIDING GATE				NIHVA TECHNOLOGIES PVT. LTD. PUNE Tel : 020 66304033 Email:- info@nihva.com Website:- www.nihva.com
		SIGN	DATE	
DRAWN	G.P.		25/12/2021	CLIENT -M/s FUJI SILVERTECH CONCRETE P. LTD.
CHECK	A.K.		25/12/2021	LOCATION - AURANGABAD
APPRD.	V.T.		25/12/2021	PRODUCT - FOUNDATION DWG
If any queries contact : design@nihva.com				NIHVA\21-22\CLT\0293 / REV- 00
ALL DIMENSION ARE IN mm				SCALE: NTS / SHEET: 01 OF 01