




SLIDING GATE PLAN OPEN POSITION

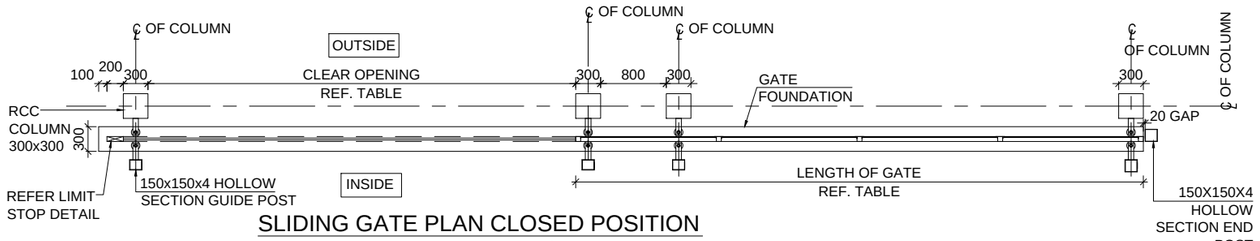


SLIDING GATE PLAN CLOSED POSITION

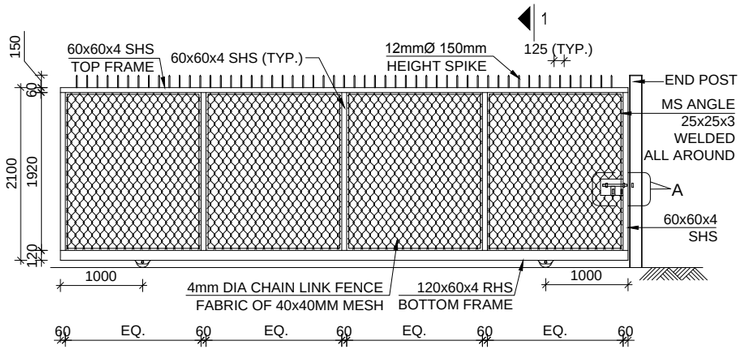


CHAIN LINK FENCE SLIDING GATE ELEVATION

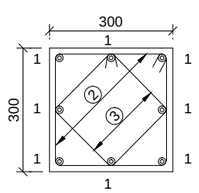



SEC. 2-2

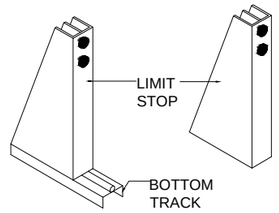

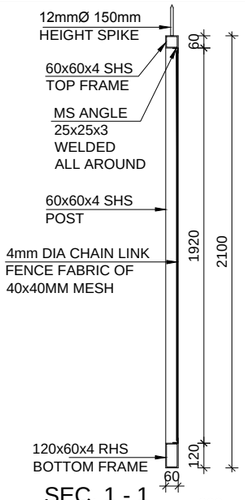


SEC. 1 - 1

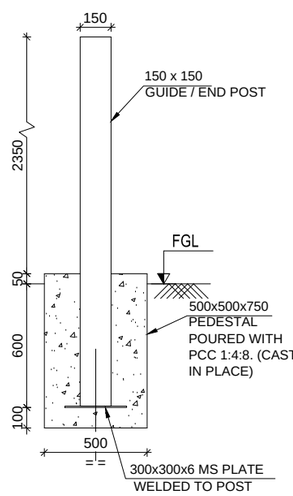


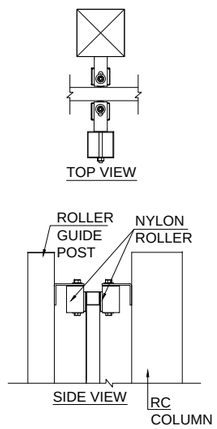


ROLLER DETAILS

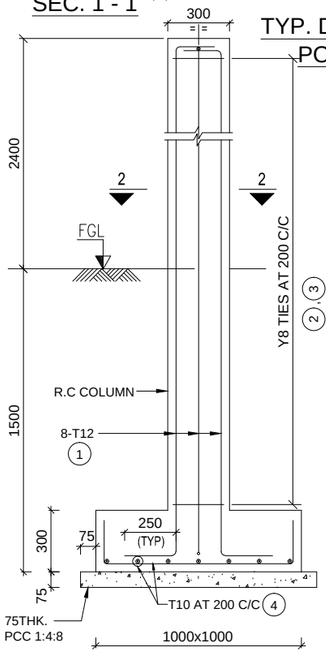


TYP. DET. OF GUIDE / END POST FOUNDATION

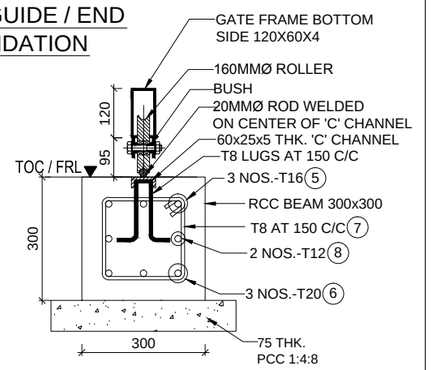

GATE FOUNDATION DETAILS

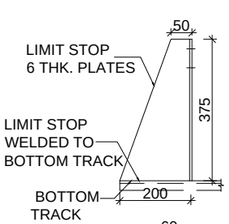


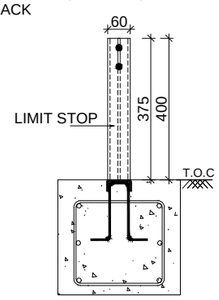

LIMIT STOP DETAILS

SCHEDULE OF MANUAL ROLLING CHAIN LINK FENCE GATE

GATE ID	CLEAR OPENING (mm)	TRACK EXTENSION (mm)	LENGTGH OF GATE (mm)	COLUMN LOCATION				T.O.C OF FOUNDATION
				CENTRE OF COLUMN -C1		CENTRE OF COLUMN -C4		
				NORTH	EAST	NORTH	EAST	
13	10400	10700	12100	3178607.155	729864.884	3178586.831	729855.231	+213.600

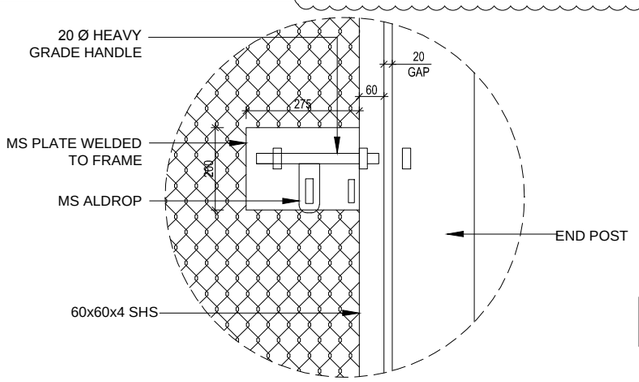

DETAIL - A

INPUT TO VENDOR

COLUMN / FOUNDATION DETAIL

LEGEND:

FGL - FORMED GROUND LEVEL
FRL - FINISHED ROAD LEVEL
SHS - SQUARE HOLLOW SECTION
RHS - RECTANGULAR HOLLOW SECTION
T.O.C - TOP OF CONCRETE

NOTES:

1. ALL DIMENSIONS ARE IN MILLIMETERS AND LEVELS ARE IN METERS.
2. GRADE OF CONCRETE SHALL BE M35.
3. CLEAR COVER TO REINFORCEMENT SHALL BE 40mm FOR GATE FOUNDATION AND 40mm FOR COLUMN.
4. T-DENOTES HIGH YIELD STRENGTH DEFORMED BAR HAVING YIELD STRENGTH NOT LESS THAN 500 N/sq.mm. CONFORMING TO IS:1786-2008.
5. ALL STRUCTURAL STEEL SECTIONS / PLATES SHALL BE OF GRADE 250 MPA CONFIRMING TO IS: 2062-2006.
6. HOLLOW SECTIONS SHALL BE OF GRADE 310 MPA CONFIRMING TO IS: 4923-1997.
7. FOR LAYOUT OF ROAD, FENCE & GATES REFER DWG. NO. O12205-C-DP-03-RD-0010 & 0011, O12205-C-DP-03-RD-0023 TO 0028, O12205-C-DP-03-RD-0044 TO 0073.
8. FRL / FGL SHALL BE LOCALLY MATCHED WITH T.O.C OF FOUNDATION .
9. DETAILS SHOWN ARE FOR PREPARING SHOP DWG. WHICH MAY SUBJECT TO CHANGE AS PER VENDOR STANDARD DETAIL IN CONSULTATION WITH CLIENT.

CHECKED BY	SIGN	DATE	CHECKED BY	SIGN	DATE	CHECKED BY	SIGN	DATE
ARCHITECTURE		09.02.15	HVAC		09.02.15	GIS		
CIVIL & STRUCTURAL		09.02.15	FPS		09.02.15	GEOTECH.		
ELECTRICAL		09.02.15	PIPING					
ELV SYSTEM		09.02.15	PHE		09.02.15			

DESIGNER OF RECORD
JOHN SANDEEP | 09/02/2015
NAME | DATE
L&T CONSTRUCTION

ITR
Retrieved | 09/02/15
NAME | DATE

US Army Corps of Engineers®
ALASKA DISTRICT

MARK	DESCRIPTION	DATE	APPR.
C	ISSUED FOR 100% FORMAL SUBMISSION	09.02.2015	RBS
B	ISSUED FOR 100% FORMAL SUBMISSION	15.10.2014	RBS
A	ISSUED FOR 100% CLIENTS APPROVAL	25.06.2014	SB

This drawing is the property of L&T Construction. B&F-EDRC, and must not be passed on to any person or body not authorised by us to receive it nor be copied or otherwise made use either in full or in part by such person or body without our prior permission in writing.

DSGN. BY:	PAKR	23.06.2014	
DRWN BY:	MSRK	24.06.2014	
CHKD BY:	RJS	25.06.2014	
APP'D BY:	SB	25.06.2014	PLOT SCALE: 1:50,1:20,1:10
SIZE: A2	REV: C	RELEASED FOR: CLIENT'S APPROVAL	

PRIME CONTRACTOR:
BOEING INTERNATIONAL CORPORATION INDIA PVT. LTD

L&T Construction
Building a Tomorrow

PROJECT:
C-17 BEDDOWN FACILITIES- HINDAN AFS

TITLE:
EXTERNAL DEVELOPMENT
NUM. & RC. DETAILS OF MANUAL ROLLING CHAIN LINK FENCE GATE

DRAWING NO.
O12205-C-DP-03-NR-0181

REFERENCE NO.
03-C-0181
SHEET OF

FEBRUARY 09, 2015 100%