


SCISSOR LIFT SIZE	WIDTH (W)	LENGTH (L)	HEIGHT (H)	LIP (C) LENGTH
	2000	2500	500	400

PIT DIMENSION	WIDTH (W 1)	LENGTH (L 1)	DEPTH (D)	ALL DIMENSIONS ARE IN mm
	2050	2550	505	

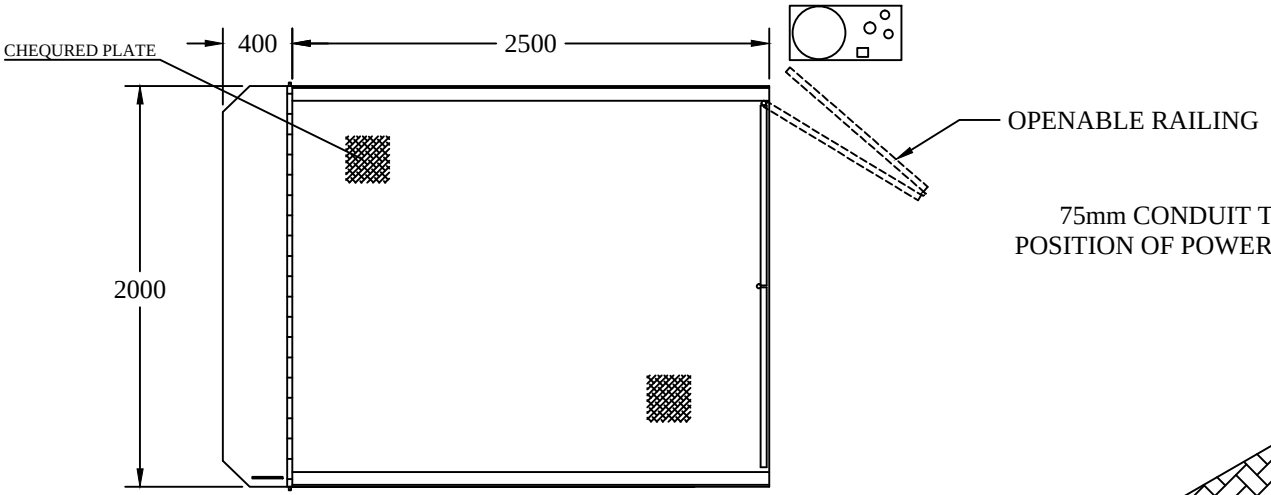

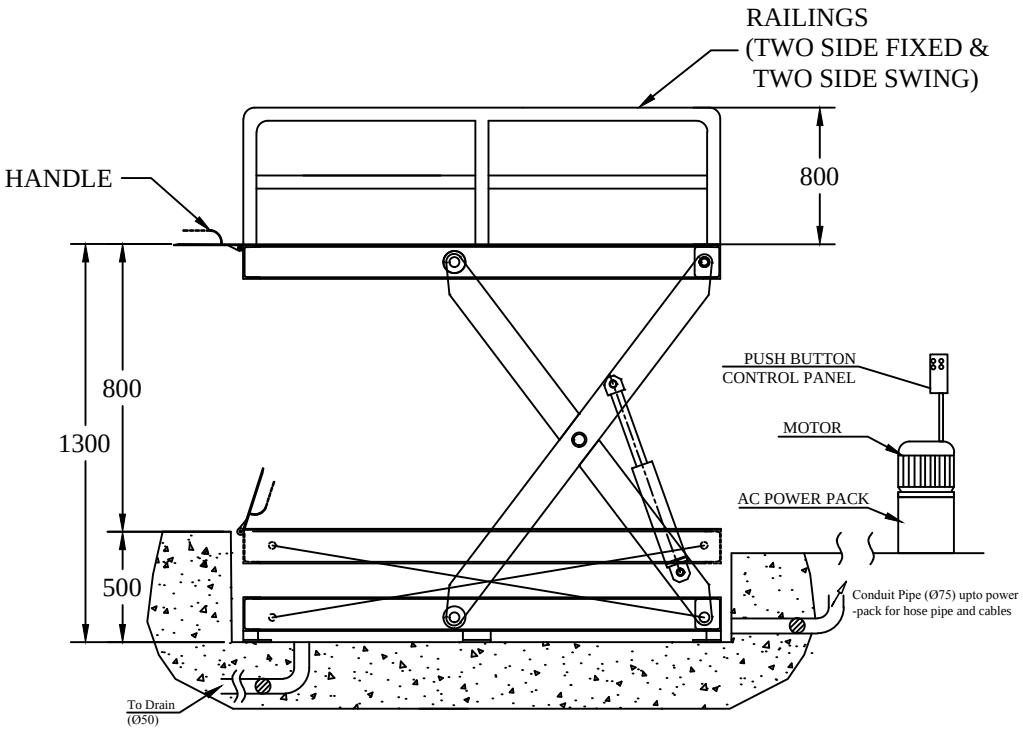

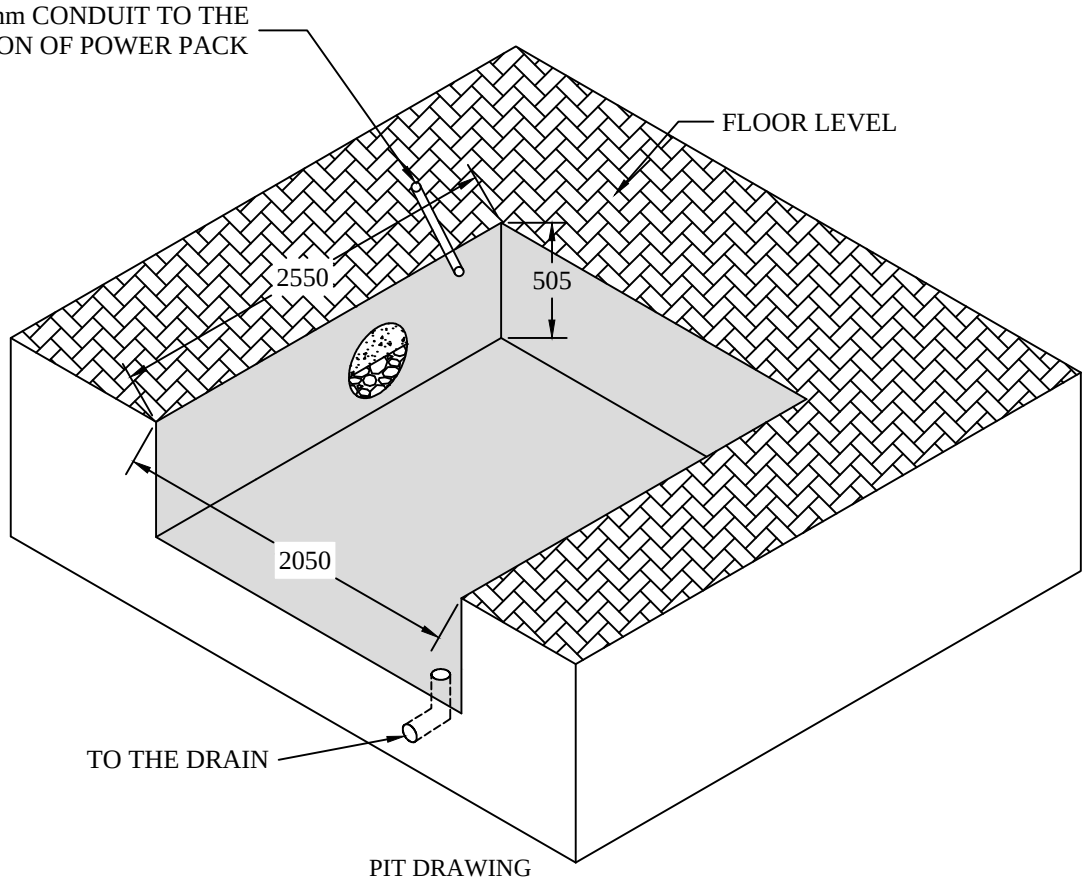

PIT DRAWING

SCISSOR LIFT- 1500KG CAPACITY

REVISION 2- PIT DRAWING MODIFIED ACCORDING TO SITE PLAN.

This drawing & designing is the property of NIHVA TECHNOLOGIES. Not be sold or copy to any other concern.

TITLE	SCISSOR LIFT		
	SIGN	DATE	
DRAWN	OMKAR	20/12/16	CLIENT - EMCURE PHARMACEUTICALS
CHECK	SAGAR P.	20/12/16	PROJECT -
REV.	2		SITE - SANAND, GUJRAT
APPROVAL			DWG. NO. : NIHVA/16-17/0094/R02
If any queries contact : projects@nihva.com			SCALE: NTS / WT: / SHEET: 01 OF 01
ALL DIMENSION ARE IN mm			

NIHVA TECHNOLOGIES PVT. LTD.
NIHVA TECHNOLOGY PVT. LTD. PUNE
Tel : 020 66304033
Email:- info@nihva.com
Website:- www.nihva.com