


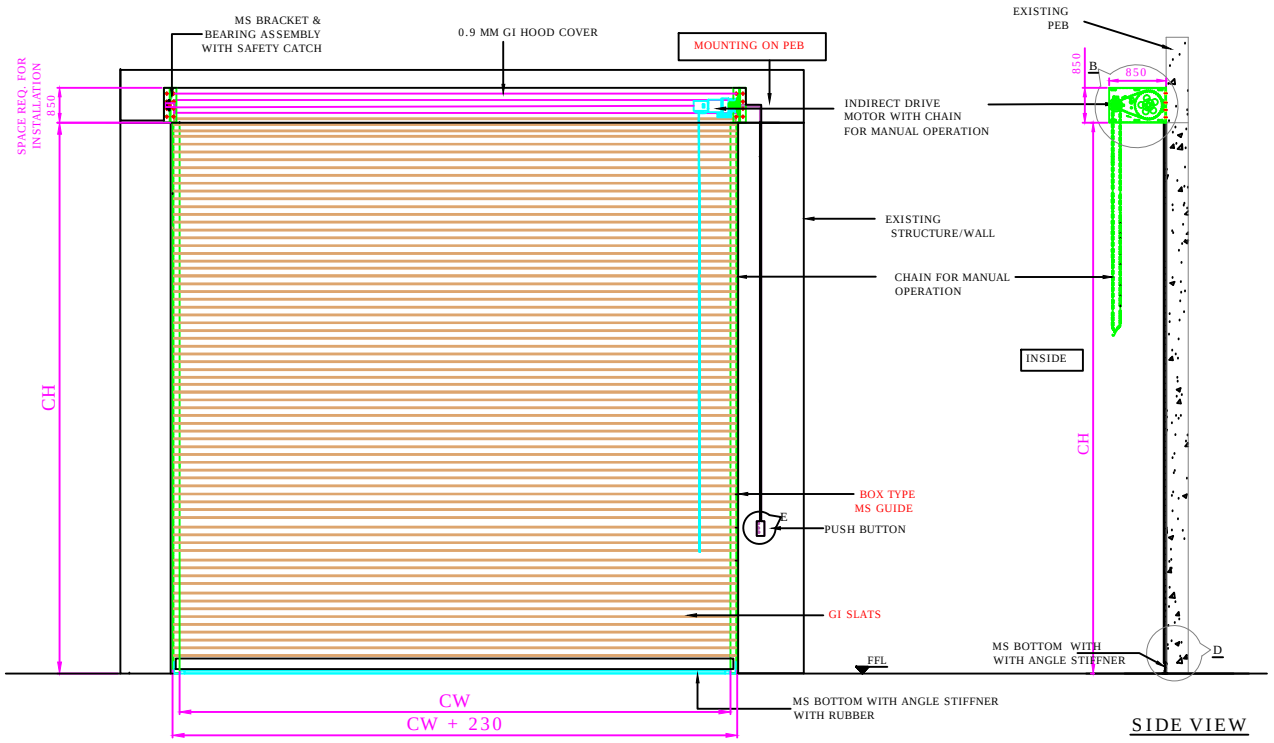


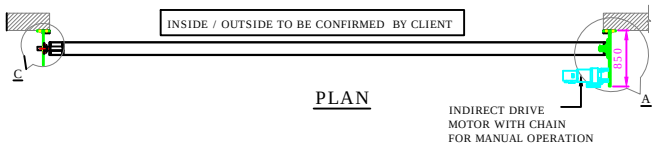


PLAN

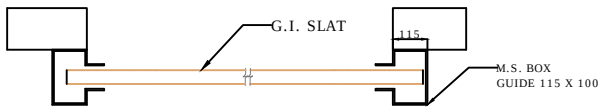


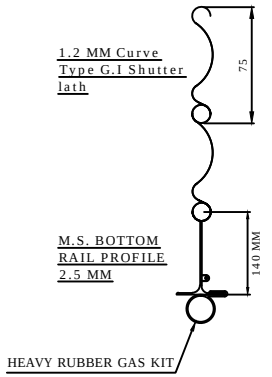


DETAILS : D

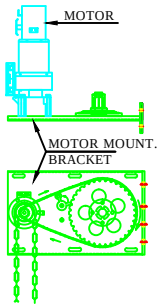

DETAILS : A & B

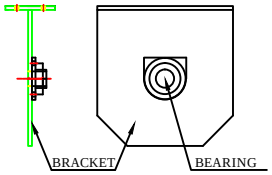

DETAILS : C

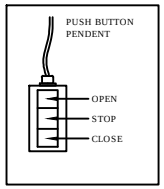

DETAILS : E

RAL CODE	SHADE	COLOUR
RAL 9001	CREAM	
RAL 9002	GREY WHITE	
RAL 9010	PURE WHITE	
RAL 5002	ULTRAMARINE BLUE	
RAL 7035	LIGHT GREY	
RAL 7001	SILVER GREY	

SR NO	CLEAR WIDTH(CW)	CLEAR HEIGHT(CH)	QTY	LOCATION	RAL CODE
6	6110	6205	1	A-GRET	
5	6070	6250	1	G-GRET	
4	6070	8000	1	G-19	
3	6060	8000	1	H-19	
2	6060	8000	1	F-1	
1	6070	8000	1	B-1	

NOTES-

(1) KINDLY REFER PROVIDED STANDARD RAL SHADE TABLE & PROVIDE CONFIRMATION OF RAL CODE FOR POWDER COATING. IF OTHER THAN SPECIFIED , KINDLY MENTION .

(2) LOCATION OF MOTORIZED ROLLING SHUTTER TO BE CONFIRMED BY CLIENT , KINDLY PROVIDE GA DRAWING OF LAYOUT.

(3) MS STRUCTURE , FITTING & ALL CIVIL WORK IS IN CLIENT SCOPE.

(4) SHUTTER WILL BE ONLY INSTALLED AFTER READINESS OF STRUCTURE AS PER DRAWING PROVIDED.

(5) SPACE OF 850 mm ABOVE CLEAR HEIGHT IS REQUIRED FOR INSTALLATION OF MOTORIZED ROLLING SHUTTER . IN CASE SPACE IS NOT AVAILABLE , REDUCTION IN CLEAR HEIGHT IS REQUIRED .

This drawing & design is the property of NIHVA TECHNOLOGIES. Not to be sold or copied to any other concern.

TITLE- GI SLAT MOTORIZED ROLLING SHUTTER

	NAME	SIGN	DATE
DRAWN	SIDDHESHWAR		28.11.2020
CHECK	SIDDHESHWAR		28.11.2020
APPRD.			

If any queries contact : projectsupport@nihva.com

ALL DIMENSION ARE IN mm

NIHVA TECHNOLOGIES PVT. LTD.
NIHVA TECHNOLOGIES PVT. LTD. PUNE
Tel : 020 66304033
Email:- info@nihva.com
Website:- www.nihva.com

CLIENT - GS PEB & CIVIL WORKS PVT LTD

PROJECT - SANY HEAVY INDUSTRY INDIA PVT LTD

SITE LOCATION - PUNE

DWG. NO. : NIHVA/20-21/0069 REV- R00

SCALE: NTS WT: SHEET: