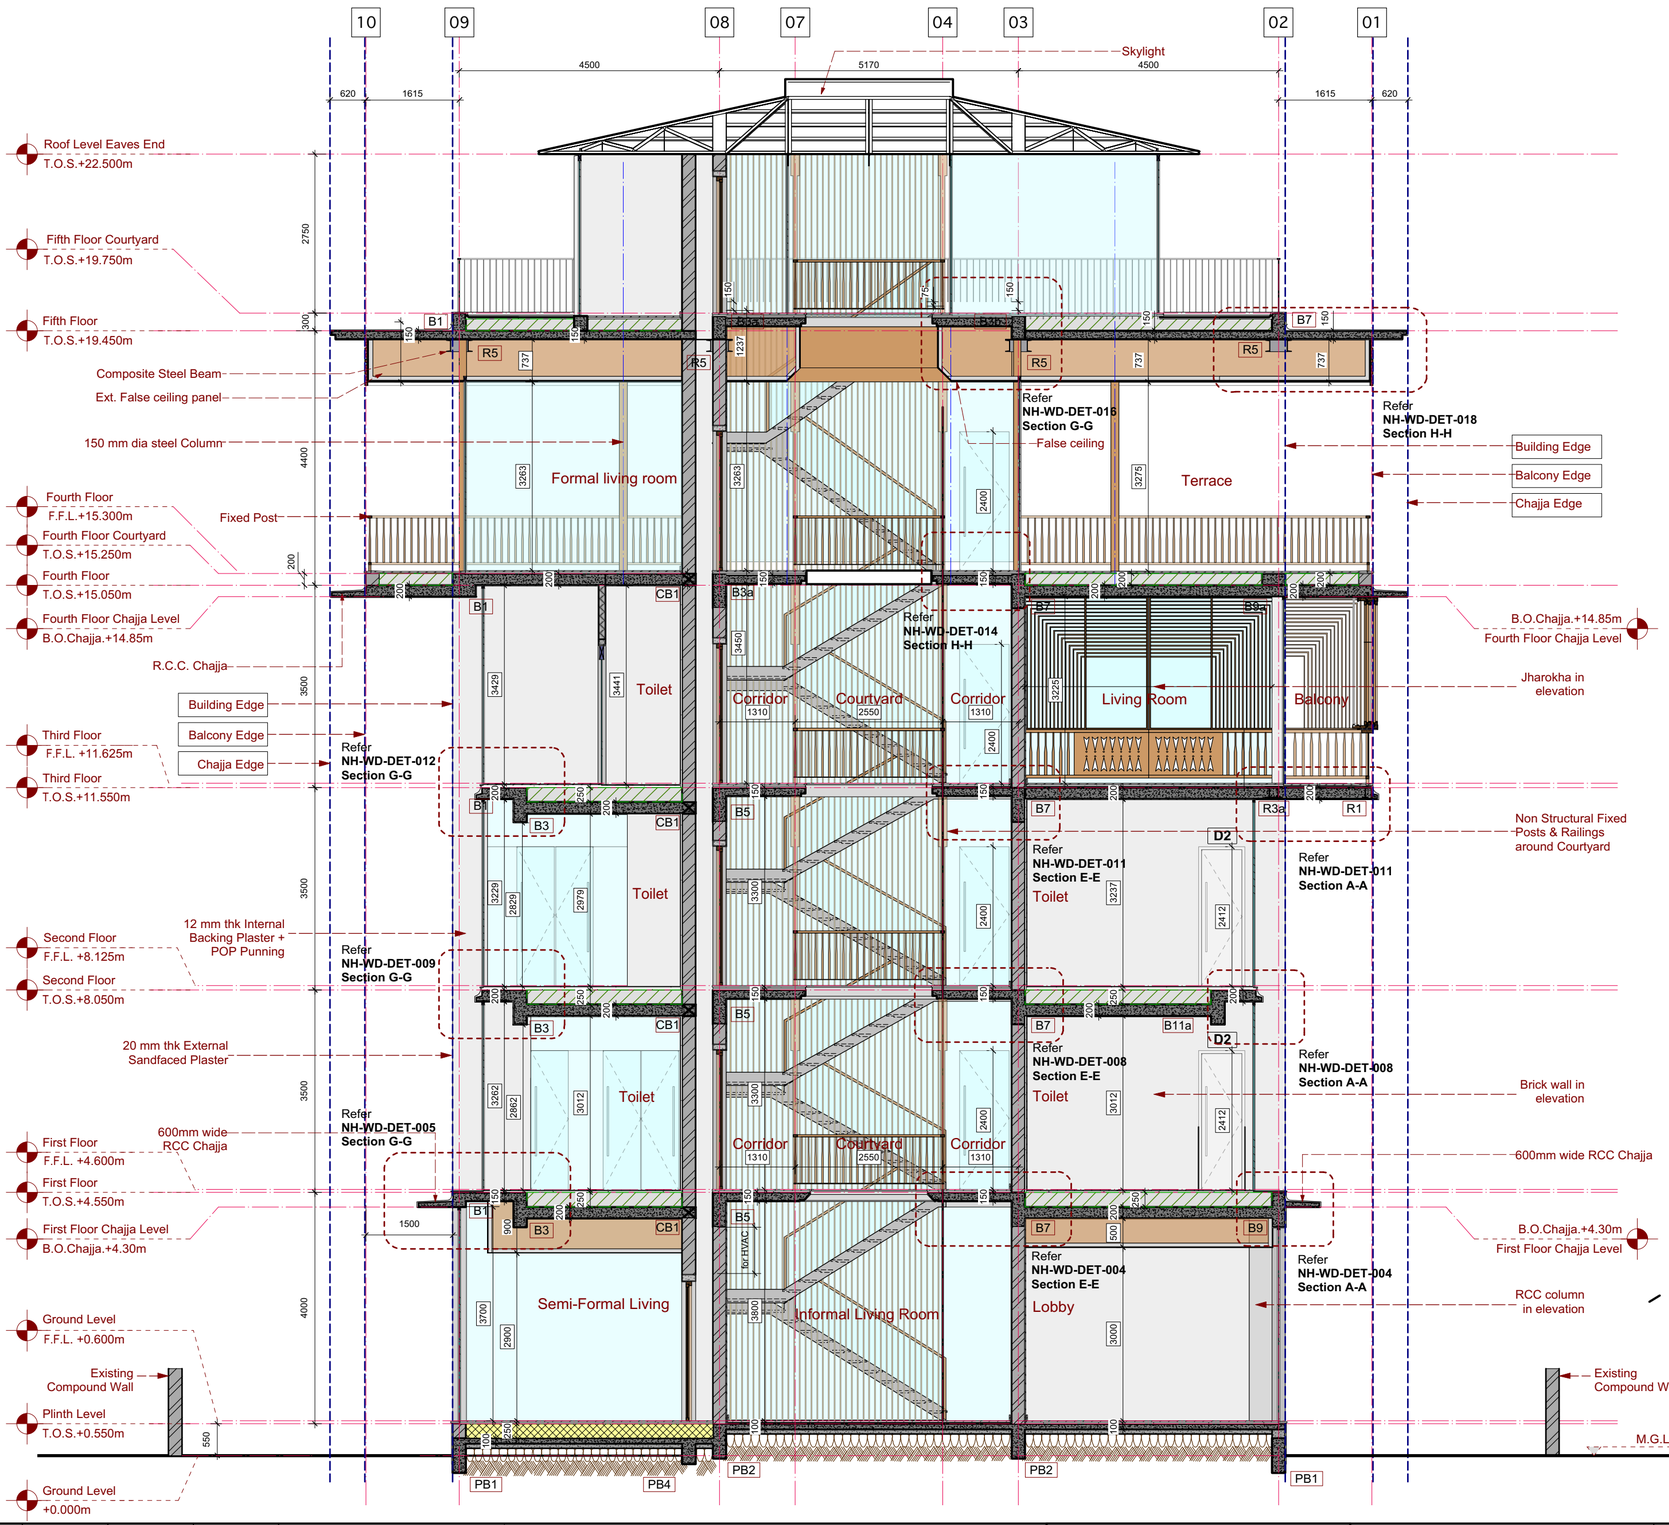


Note:

1. All Plinth Beams to be revised as per final Structural Drawings.
2. Staircase and Courtyard Railings have not been shown in the drawings for clarity.
3. Refer latest revision for relevant detailed drawings.
4. Refer latest revision of ID detailed drawing as mentioned

MATERIAL LEGEND

	Wooden screen and glass sandwiched window shutter
	230mm thk Brick wall
	115mm thk Brick wall
	200mm thk Light weight AAC wall
	100mm thk Light weight AAC wall
	Brick Bat Coba
	Brick Bat Coba with Waterproofing
	RCC Slab / Beams
	PCC non-structural

FOR REFERENCE ONLY

ARCHITECT:

SJK ARCHITECTS

302-303,VEENA KILLEDAR INDL.EST, ,10/14,PAIS STREET, BYCULLA-WEST, MUMBAI-400 011
TEL.NO.: 022- 2300 8766, 022-23008761
FAX.NO. : 022-2309 0983
email: design @sjkarchitect.com

This "drawing" is the copyright of **SJK Architects** and shall not be used for any purpose other than that for which it has been loaned.

STRUCTURAL:

MANJUNATH & CO. CONSULTING ENGINEERS #236 5th CROSS, K.G. NAGAR, BANGALORE - 560019 TEL.NO.: 080- 26616610 email: manjaxe2010@gmail.com

MEP:

MEPTEK CONSULTANTS Complete MEP Design Solutions

-2,665, Millennium, Veer Savarkar Marg, Dadar (W), Mumbai-400028. nimish.shah@meptekconsultants.com

PMC:

GENERAL NOTES:

1. All Dimensions Are In MILLIMETERS Unless Otherwise Specified.
2. All Dimensions Specified Are UnFinished Dimensions, Unless Otherwise specified.
3. All structural dimensions shall be referred as per Consultants' drawings.
4. DO NOT SCALE Drawing
5. Any Discrepancies In the Drawings Shall Be Brought To The Notice Of The Architect,Prior to Execution.

SPECIFIC NOTES / LEGEND:

1. All Boxed Dimensions are finished dimensions (i.e. after plaster, dado etc). Remaining are unfinished dimensions.
2. All External surfaces of walls shall have 20mm thk External Sandfaced Plaster.
3. All Internal surfaces of walls shall have 12mm thk Backing Coat of Plaster + POP Punning. (Except toilet walls, which will receive waterproofing and dado finish).

KEY PLAN

REVISION NOTES:

PROJECT:

NAGPUR HOUSE

CLIENT:

JAIN FAMILY

REV NO: R0
DATE OF REVISION:

DRAWING NO: NH-DD-SEC-001-R0

DRAWING TITLE:

SECTION 6-6

DATE OF ISSUE: 10-02-2021

SCALE: 1:75 **SHEET SIZE:** A2

PURPOSE : REFERENCE ONLY