



PRODUCED BY AN AUTODESK EDUCATIONAL PRODUCT

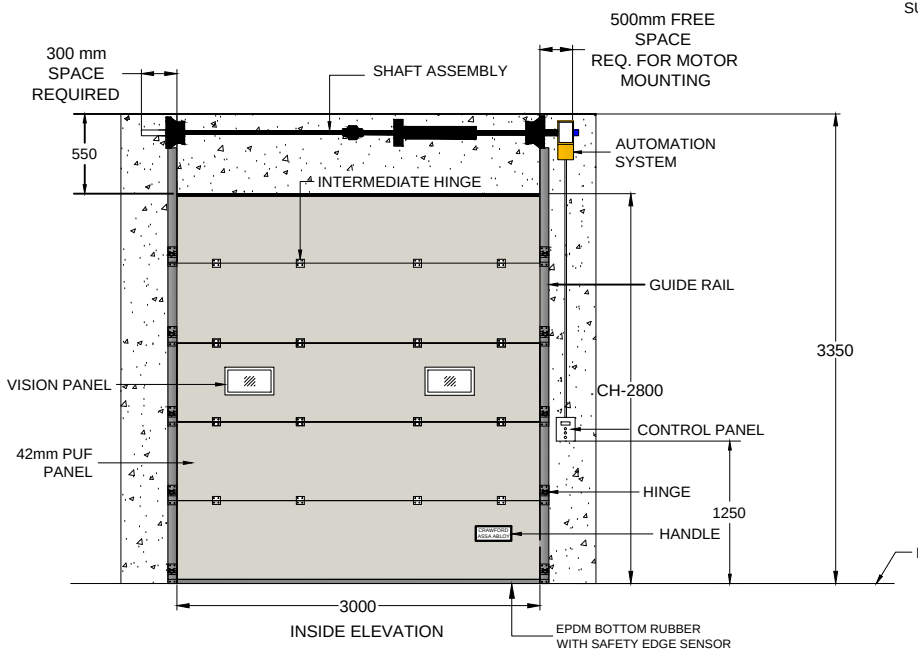

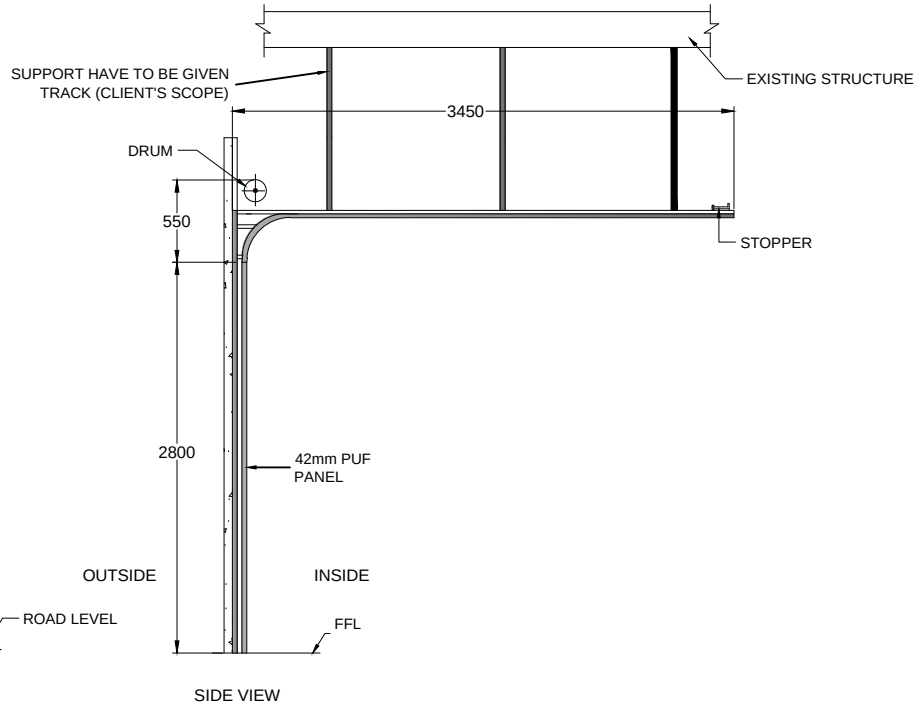

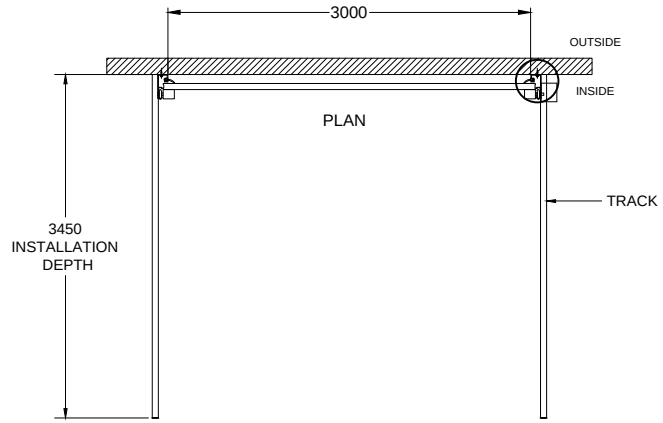

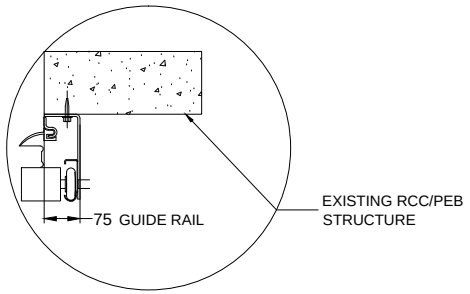

STANDARD COLORS AVAILABLE
FOR THE SECTIONAL DOOR PANELS

- ☐ 1.RAL 9002- GREY WHITE
- ☐ 2.RAL 7035 - LIGHT GREY
- ☐ 3.RAL 7015- SLATE GREY
- ☐ 4.RAL 7016 -ANTHRACITE GREY
- ☐ 5.RAL 3002- CARMINE RED
- ☐ 6.RAL 5002- ULTRAMARINE BLUE

SR NO	CLEAR WIDTH (CW)	CLEAR HEIGHT (CH)	QTY
01	3000mm	2800mm	01

NOTE-
1. ALL CIVIL WORK WILL BE CLIENT'S SCOPE.
2.STRUCTURE REQUIRED FOR DOOR IS IN CLIENT'S SCOPE.
3.CLIENT SHOULD CONFIRM RAL COLOR SHADE.

TOLERANCE:±10mm

This drawing & design is the property of NIHVA TECHNOLOGIES. Not to be sold or copied to any other concern.

TITLE: SECTIONAL DOOR OPTION 01

	NAME	SIGN	DATE
DRAWN	SURAJ		20/09/18
CHECK	VIKRANT		20/09/18
APPROVAL	R.D		20/09/18

NIHVA TECHNOLOGIES PVT. LTD.
NIHVA TECHNOLOGIES PVT. LTD. PUNE
Tel : 020 66304033
Email:- info@nihva.com
Website:- www.nihva.com

CLIENT -SYNERGY
PROJECT -TCS Mihan project
SITE LOCATION - NAGPUR.
If any queries contact : design@nihva.com
DWG. NO. : NIHVA/18-19/0131
REV: 0
ALL DIMENSION ARE IN mm
SCALE: NTS
WT:
SHEET: 01 OF 01

PRODUCED BY AN AUTODESK EDUCATIONAL PRODUCT

PRODUCED BY AN AUTODESK EDUCATIONAL PRODUCT