




DETAIL H, SCALE (1:20)

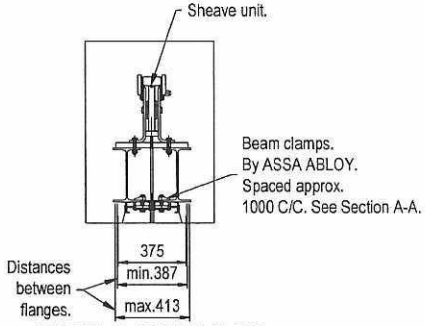


DETAIL J, SCALE (1:20)

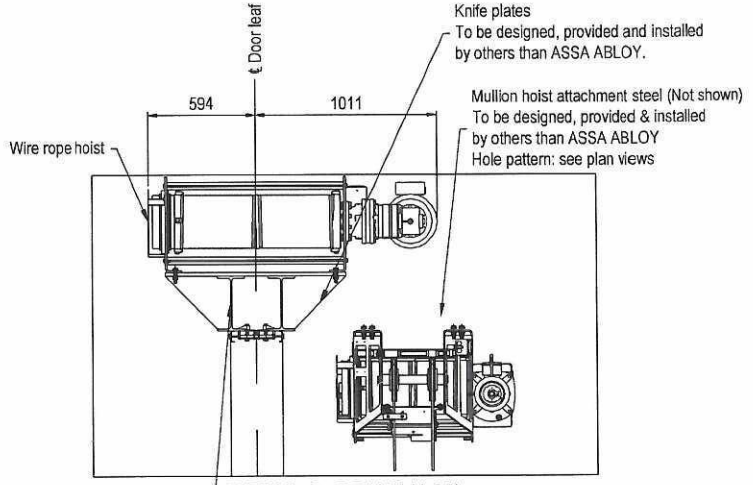


DETAIL G, SCALE (1:20)

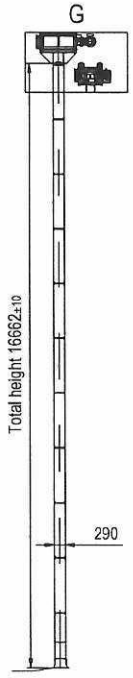

SECTION D-D

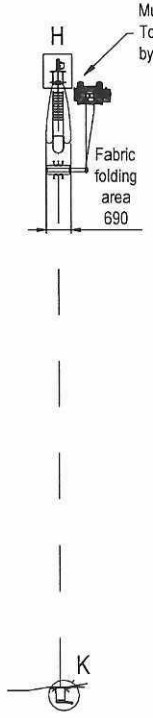


SECTION E-E

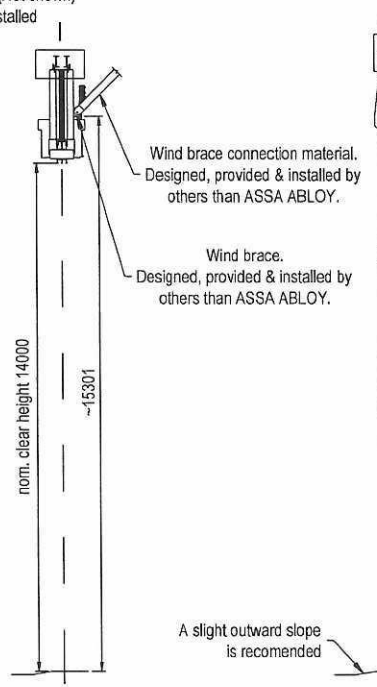


SECTION F-F

SECTION G-G

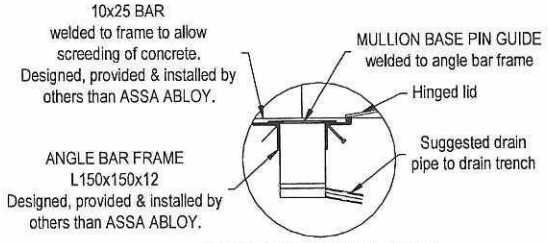

DETAIL K, SCALE (1:20)

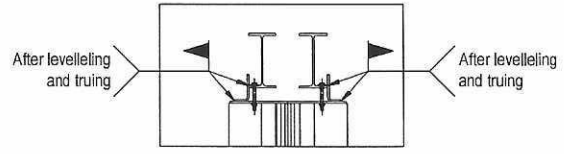

DETAIL I, SCALE (1:20)

DOOR IDENTITY NUMBER: 84801001

LOAD DIAGRAM & NOTES, ref. to drwng. no. 77450

INTERFACE, PLAN VIEWS ref. to drwng. no. 77448

INTERFACE, ELEVATION ref. to drwng. no. 77447

NIHIVA TECHNOLOGIES PVT. LTD. PUNE

DESIGNED EB		SIZE A2	SCALE 1:100
CODE 84801		If not otherwise stated	
ITEM NO		Tolerances ISO 2768-m EN ISO 13920-B	
DATE 2022-08-31		Cutting class ISO 9013-442	
ASSA ABLOY		Weld class ISO 5817-C	
		Surface finish Smooth raw surface	

GMR Aero Technic Hangar2
India
Megadoor 99000x14700/14000
Interface, sections

DRAWING NO 77449

REVISION --

PLOT DATE

This document is the property of ASSA ABLOY Entrance Systems AB and shall not without our written permission be copied, imparted to a third party or used for any other unauthorized purpose.