| | | |
|---|---|---|
| HP / ENGINEERS INDIA LIMITED (A Govt. of India Undertaking) | **Residue Upgradation Facility (RUF)**<br>**EPCC-3 Package for**<br>**Visakh Refinery Modernization Project (VRMP)** | L&T Hydrocarbon Engineering<br>**L&T- CHIYODA LIMITED** |
| **Title: Data Civil drawing for Dock Leveller**<br>**Doc. No.: B016-RUF-LT-504-MP-DW-NTPL(1)-13005** | | **Rev. No.: 00**<br>**Page No: 1 of 4** |

| | | |
|---|---|---|
| **OWNER** | : | **HINDUSTAN PETROLEUM CORPORATION LIMITED (HPCL)** |
| **PMC** | : | **ENGINEERS INDIA LIMITED, NEW DELHI (EIL)** |
| **UNIT** | : | **504** |
| **PMC JOB NO.** | : | **B016** |
| **EQUIPMENT DESCRIPTION** | : | **DOCK LEVELLER** |
| **EQUIPMENT TAG** | : | **XXXXXXXXXXXXX** |
| **P. R. NO.** | : | **XXXXXXXXXXXXX** |
| **VENDOR NAME** | : | **NIHVA TECHNOLOGIES PVT LTD** |
| **VENDOR DOCUMENT NO.** | : | **NIHVA_20-21_0158** |

| **DOCUMENT SUBMISSION STATUS – LTHE/VENDOR** | **REVIEW STATUS** | |
|---|---|---|
| | **LTHE** | **EIL** |
| DOC. CATEGORY: (USE TICK MARK)<br>☑ R ☐ I | ☐ Code 1 – No Comments. Proceed With Manufacture / Fabrication / Construction As Per The Document.<br>☐ Code 2 – Proceed With Manufacture/Fabrication/Construction As Per Commented Document. Revised Document Required.<br>☐ Review Code 3 – Document Does Not Conform To Basic Requirements As Marked. Resubmit For Review<br>☐ Code R– Document Is Retained For Records. Proceed With Manufacture / Fabrication<br>☐ Code V- Void ( Submission Required / Not Required) | ☐ Code 1 – No Comments. Proceed With Manufacture / Fabrication / Construction As Per The Document.<br>☐ Code 2 – Proceed With Manufacture/Fabrication/Construction As Per Commented Document. Revised Document Required.<br>☐ Review Code 3 – Document Does Not Conform To Basic Requirements As Marked. Resubmit For Review<br>☐ Code R– Document Is Retained For Records. Proceed With Manufacture / Fabrication<br>☐ Code V- Void ( Submission Required / Not Required) |
| **ISSUED FOR**<br>☐ INFORMATION<br>☑ REVIEW<br>☐ CONSTRUCTION<br>☐ AS BUILT | DISCIPLINE / SIGN / DATE | DISCIPLINE / SIGN / DATE |

| Revision No. | Description | Prepared by | Reviewed by | Approved by | Reviewed by | Approved by | Approved Date |
|---|---|---|---|---|---|---|---|
| | | | | | | | |
| | | | | | | | |
| | | | | | | | |
| 00 | Issued for Approval | Vikrant J | Amit K | Amit K | | | 31-05-2021 |

ALL RIGHTS RESERVED

THIS DOCUMENT AND ANY DATA AND INFORMATION CONTAINED THEREIN ARE CONFIDENTIAL AND THE PROPERTY OF L&T HYDROCARBON ENGINEERING (LTHE) AND THE COPYRIGHT THEREIN IS VESTED IN LTHE NO PART OF THIS DOCUMENT, DATA, OR INFORMATION SHALL BE DISCLOSED TO OTHERS OR REPRODUCED IN ANY MANNER OR USED FOR ANY PURPOSE WHATSOEVER, EXCEPT WITH THE PRIOR WRITTEN PERMISSION OF LTHE.

## REVISION HISTORY SHEET


| REV. NO. | REV. DATE | REVISED PAGE | REVISION DESCRIPTION |
|---|---|---|---|
| 00 | 31-05 | NA | ISSUED FOR APPROVAL |
| | | | |
| | | | |
ALL RIGHTS RESERVED


THIS DOCUMENT AND ANY DATA AND INFORMATION CONTAINED THEREIN ARE CONFIDENTIAL AND THE PROPERTY OF L&T HYDROCARBON ENGINEERING (LTHE) AND THE COPYRIGHT THEREIN IS VESTED IN LTHE NO PART OF THIS DOCUMENT, DATA, OR INFORMATION SHALL BE DISCLOSED TO OTHERS OR REPRODUCED IN ANY MANNER OR USED FOR ANY PURPOSE WHATSOEVER, EXCEPT WITH THE PRIOR WRITTEN PERMISSION OF LTHE.


ALL RIGHTS RESERVED
THIS DOCUMENT AND ANY DATA AND INFORMATION CONTAINED THEREIN ARE CONFIDENTIAL AND THE PROPERTY OF L&T HYDROCARBON ENGINEERING, LTD AND THE COPYRIGHT THEREIN IS VESTED IN L&T HYDROCARBON ENGINEERING, LTD. THIS DOCUMENT IS NOT TO BE REPRODUCED, MODIFIED, ADAPTED, PUBLISHED, TRANSLATED IN ANY MATERIAL FORM IN WHOLE OR IN PART OR STORED IN A RETRIEVAL SYSTEM OR TRANSMITTED IN ANY FORM OR BY ANY MEANS ELECTRONIC, MECHANICAL, PHOTOCOPYING, RECORDING OR OTHERWISE OR USED FOR ANY PURPOSE WHATSOEVER, EXCEPT WITH THE PRIOR WRITTEN PERMISSION OF LTHE.


DWG. NO.

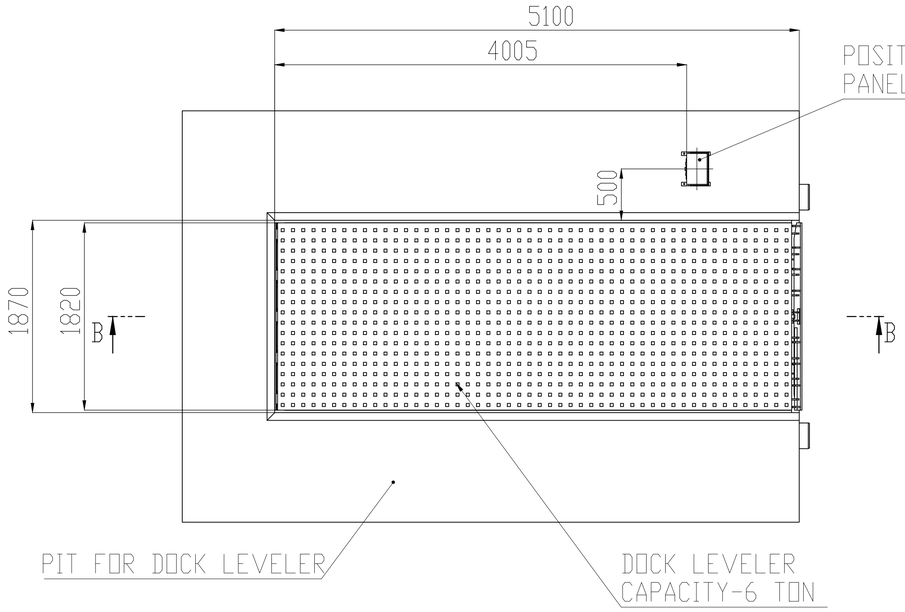

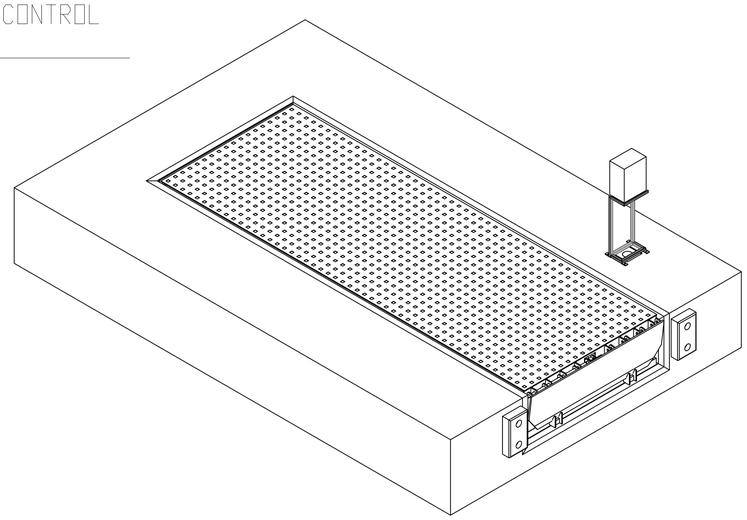

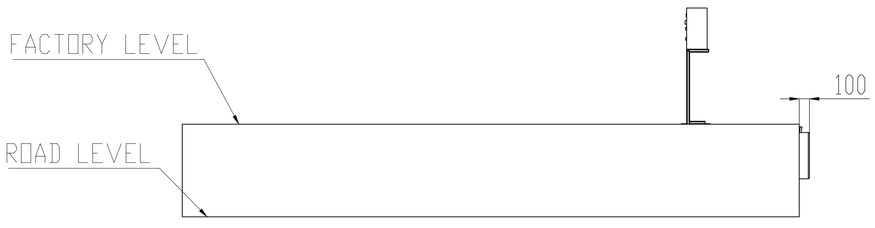
SECTION B-B
SCALE 1 : 28

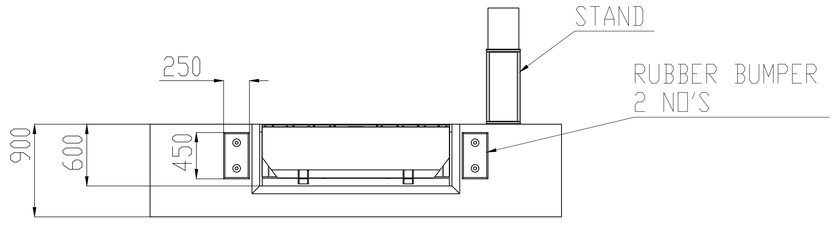PROJECT DESCRIPTION -
1. DOCK LEVELER - PIT MOUNTED ELECTRO-HYDRAULIC TYPE
2. CAPACITY- 6 TON POINT LOAD
3. QTY- 2 NOS
4. PRODUCT SIZE- 5100mm(L)X1820mm(W)X600mm(D)
5. PIT SIZE-5100mm(L)X1870mm(W)X600mm(D)

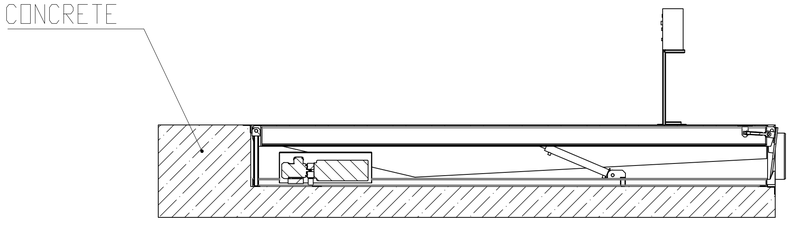**L&T - CHIYODA LIMITED**

- ☐ REVIEW CODE 1 – NO COMMENTS PROCEED WITH MANUFACTURE / FABRICATION/ CONSTRUCTION AS PER THE DOCUMENT.
- ☐ REVIEW CODE 2 – PROCEED WITH MANUFACTURE/ FABRICATION /CONSTRUCTION AS PER THE COMMENTED DOCUMENT. REVISED DOCUMENT REQUIRED.
- ☐ REVIEW CODE 3 – DOCUMENT DOES NOT CONFORM TO BASIC REQUIREMENTS AS MARKED. RESUBMIT FOR REVIEW.
- ☐ R – DOCUMENT IS RETAINED FOR RECORDS. PROCEED WITH MANUFACTURE / FABRICATION
- ☐ V-VOID

| COMMENTED BY | REVIEWED BY | APPROVED BY | DATE |
|---|---|---|---|
| | | | |

THIS REVIEW / APPROVAL DOES NOT RELIEVE THE VENDOR / MANUFACTURER OF THE FULL RESPONSIBILITY AS TO DESIGN CORRECTNESS OF DIMENSIONS & COMPLIANCE WITHALL APPLICABLE REGULATIONS AND WITH THE REQUIREMENTS MADE IN PURCHASER SPECIFICATIONS.

| DRAWING NO. | DRAWING TITLE | REV |
|---|---|---|
| | | |

REFERENCE DOCUMENTS / DRAWINGS

DRG. CATEGORY: (USE TICK MARK) ☐ R ☑ I — EIL REVIEW/APPROVAL CODE: — VPTL NO.:

SCH. DATE OF SUBMISSION

DOCUMENT STATUS
STATEMENT OF SUB: ☐ 1st ☐ 2nd ☐ 3rd
☐ FINAL FOR CODE-1 ☐ AS BUILT

ISSUED FOR
☐ AS BUILT ☑ INFORMATION
☐ CONSTRUCTION ☐ REVIEW

SIGN: DATE:

☐ REVIEW CODE 1 – NO COMMENTS PROCEED WITH MANUFACTURE / FABRICATION/ CONSTRUCTION AS PER THE DOCUMENT.
☐ REVIEW CODE 2 – PROCEED WITH MANUFACTURE / FABRICATION / CONSTRUCTION AS PER THE COMMENTED DOCUMENT. REVISED DOCUMENT REQUIRED.
☐ REVIEW CODE 3 – DOCUMENT DOES NOT CONFORM TO BASIC REQUIREMENTS AS MARKED. RESUBMIT FOR REVIEW.
☐ R – DOCUMENT IS RETAINED FOR RECORDS. PROCEED WITH MANUFACTURE / FABRICATION
☐ V-VOID

NAME DICIPLINE SIGN. DATE

| REV. | DESCRIPTION | DRN | CHECKED | APPROVED | REVIEWED | APPROVED | DATE |
|---|---|---|---|---|---|---|---|
| 00 | ISSUED FOR APPROVAL | SMS | VJ | AK | | | |

OWNER: HINDUSTAN PETROLEUM CORPORATION LIMITED
VISAKH REFINERY MODERNIZATION PROJECT
EPCC-03 PACKAGE FOR RESIDUE UP-GRADATION FACILITY (RUF)

PMC: इंजीनियर्स इंडिया लिमिटेड ENGINEERS INDIA LIMITED (A Govt. of India Undertaking)

LSTK CONTRACTOR: L&T Hydrocarbon Engineering

DETAILED ENGINEERING CENTER: L&T - CHIYODA LIMITED

VENDOR: NIHVA TECHNOLOGIES PVT LTD

VENDOR PO NO: REFINARY/75000-82256/VMM

VENDOR DWG. NO: NIHVA_20-21_0158

| DATE | SCALE |
|---|---|
| 31.05.21 | 1:1 |

TITLE: CIVIL DRAWING FOR DOCK LEVELER

DEPT: DESIGN

DRN BY: SMS

CHK BY: VJ

APP BY: AK

PROJECT: L&T-RUF

PWO NO.:

DRG. NO.: B016-RUF-LT-504-MP-DW-NTPL(1)-13005


SH. 1 OF 2

REV. 00


CAD REVISE THIS DRG. USING CAD SYSTEM ONLY FILE:

ALL RIGHTS RESERVED
THIS DOCUMENT AND ANY DATA AND INFORMATION CONTAINED THEREIN ARE CONFIDENTIAL AND THE PROPERTY OF L&T HYDROCARBON ENGINEERING (LTHE) AND THE COPYRIGHT THEREIN IS VESTED IN LTHE. NO PART OF THIS DOCUMENT OR ANY DATA AND INFORMATION CONTAINED THEREIN IS TO BE COPIED, REPRODUCED, DISCLOSED, TRANSMITTED, STORED IN ANY MANNER OR USED FOR ANY PURPOSE WHATSOEVER, EXCEPT WITH THE PRIOR WRITTEN PERMISSION OF LTHE.


DWG. NO.

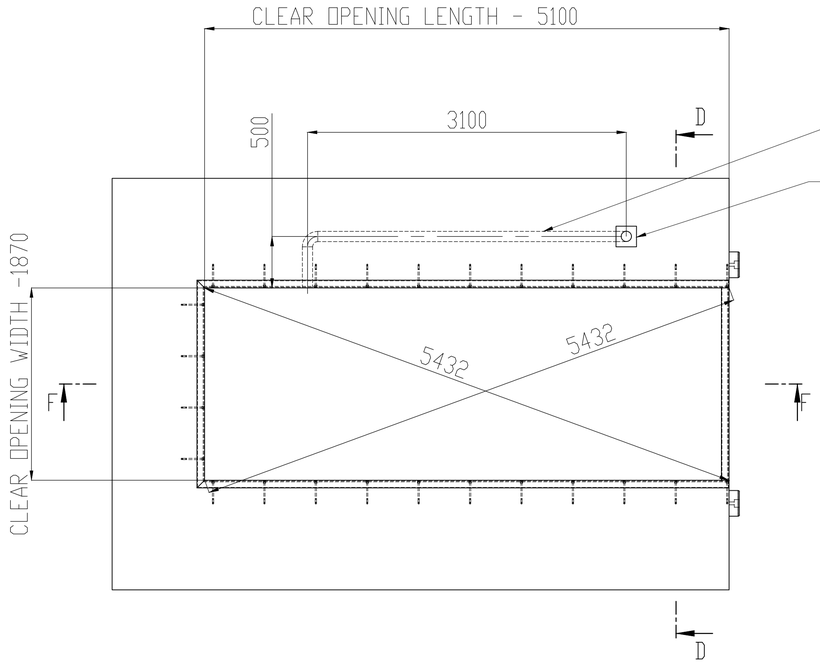



TOP VIEW OF DOCK PIT

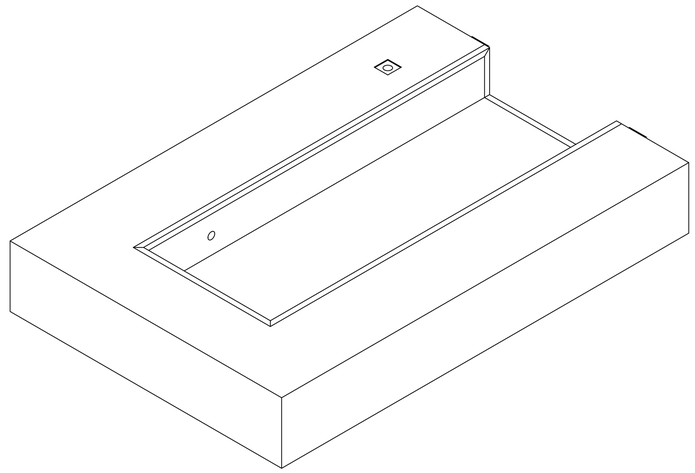


ISOMETRIC VIEW OF DOCK LEVELER PIT

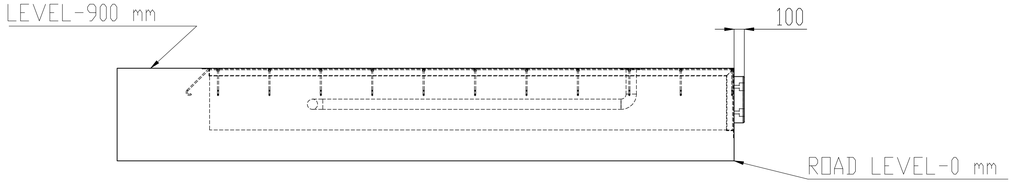



FRONT VIEW OF DOCK PIT

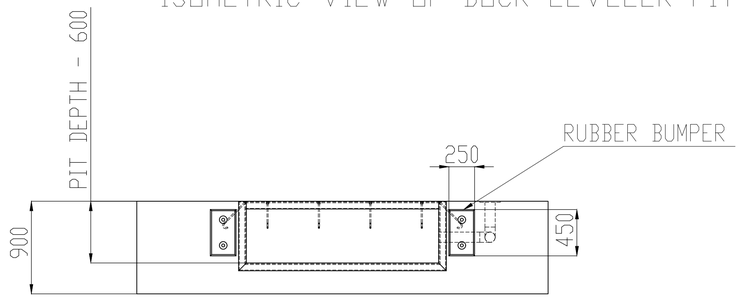



SIDE VIEW OF DOCK PIT

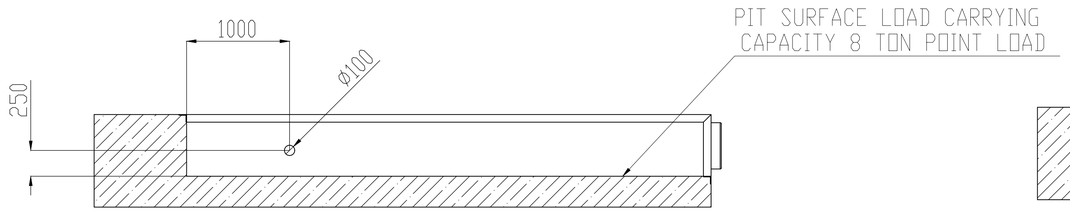


SECTION F-F
SCALE 1 : 28

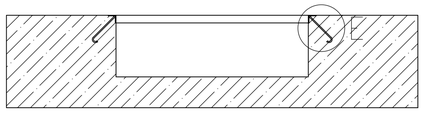

SECTION D-D
SCALE 1 : 28

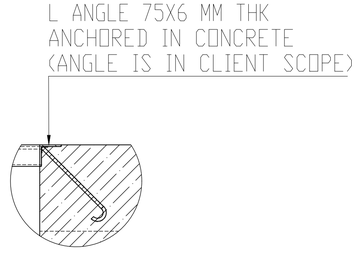


DETAIL E
SCALE 1 : 10

NOTES -
1. PIT & ALL CIVIL WORK IS CLIENT SCOPE .
2. AT ALL EDGES OF PIT ANGLE 75X6 MM THK(ANGLE IN CLIENT SCOPE ) TO BE ANCHORED IN CONCRETE .
3. PIT SURFACE SHOULD BE PLAIN & LOAD CARRYING CAPACITY FOR PIT SURFACE SHOULB OF 8 TON POINT LOAD .
4. MINIMUM 4 INCH DUCT DUCT TO BE PROVIDED FROM CONTROL PANEL TO PIT OPENING BY CLIENT FOR ELECTRICAL CABLE ROUTING . REQUIRED DUCT IS IN CLIENT SCOPE.
5. CONTROL PANEL IS PROVIDED WITH ELECTRICAL CABLE LENGTH OF 5 METER AS STANDARD . CONTROL PANEL SHOULD BE LOCATED NEAR DOCK LEVELER FOR EASY VIEW OF LIP RESTING ON VEHICLE .

**L&T - CHIYODA LIMITED**

- ☐ REVIEW CODE 1 – NO COMMENTS PROCEED WITH MANUFACTURE / FABRICATION/ CONSTRUCTION AS PER THE DOCUMENT.
- ☐ REVIEW CODE 2 – PROCEED WITH MANUFACTURE/ FABRICATION /CONSTRUCTION AS PER THE COMMENTED DOCUMENT. REVISED DOCUMENT REQUIRED.
- ☐ REVIEW CODE 3 – DOCUMENT DOES NOT CONFORM TO BASIC REQUIREMENTS AS MARKED. RESUBMIT FOR REVIEW.
- ☐ R – DOCUMENT IS RETAINED FOR RECORDS. PROCEED WITH MANUFACTURE / FABRICATION
- ☐ V-VOID

| COMMENTED BY | REVIEWED BY | APPROVED BY | DATE |
|---|---|---|---|
| | | | |

THIS REVIEW / APPROVAL DOES NOT RELIEVE THE VENDOR / MANUFACTURER OF THE FULL RESPONSIBILITY AS TO DESIGN CORRECTNESS OF DIMENSIONS & COMPLIANCE WITHALL APPLICABLE REGULATIONS AND WITH THE REQUIREMENTS MADE IN PURCHASER SPECIFICATIONS.

| DRAWING NO. | DRAWING TITLE | REV |
|---|---|---|
| | REFERENCE DOCUMENTS / DRAWINGS | |

DRG. CATEGORY: (USE TICK MARK) [R] [1]
EIL REVIEW/APPROVAL
VPTL NO.:
SCH. DATE OF SUBMISSION
CODE:

DOCUMENT STATUS
STATEMENT OF SUB: [1st] [2nd] [3rd]
☐ FINAL FOR CODE–1 ☐ AS BUILT

ISSUED FOR
☐ AS BUILT ☐ INFORMATION
☐ CONSTRUCTION ☐ REVIEW

SIGN: DATE:

- ☐ REVIEW CODE 1 – NO COMMENTS PROCEED WITH MANUFACTURE / FABRICATION/ CONSTRUCTION AS PER THE DOCUMENT.
- ☐ REVIEW CODE 2 – PROCEED WITH MANUFACTURE / FABRICATION / CONSTRUCTION AS PER THE COMMENTED DOCUMENT. REVISED DOCUMENT REQUIRED.
- ☐ REVIEW CODE 3 – DOCUMENT DOES NOT CONFORM TO BASIC REQUIREMENTS AS MARKED. RESUBMIT FOR REVIEW.
- ☐ R – DOCUMENT IS RETAINED FOR RECORDS. PROCEED WITH MANUFACTURE / FABRICATION
- ☐ V-VOID

NAME DICIPLINE SIGN, DATE

| REV. | DESCRIPTION | DRN | CHECKED | APPROVED | REVIEWED | APPROVED | DATE |
|---|---|---|---|---|---|---|---|
| 00 | ISSUED FOR APPROVAL | SMS | VJ | AK | | | |

OWNER: HINDUSTAN PETROLEUM CORPORATION LIMITED
VISAKH REFINERY MODERNIZATION PROJECT
EPCC-03 PACKAGE FOR RESIDUE UP-GRADATION FACILITY (RUF)

PMC : इंजीनियर्स इंडिया लिमिटेड ENGINEERS INDIA LIMITED (A Govt. of India Undertaking)

LSTK CONTRACTOR: L&T Hydrocarbon Engineering

DETAILED ENGINEERING CENTER: L&T - CHIYODA LIMITED

VENDOR : NIHVA TECHNOLOGIES PVT LTD

VENDOR PO NO: REFINARY/75000-82256/VMM

VENDOR DWG. NO: NIHVA_20-21_0158

| DATE | SCALE | TITLE: CIVIL DRAWING FOR DOCK LEVELER |
|---|---|---|
| 29.5.21 | 1:1 | |

| DEPT: DESIGN | | | |
|---|---|---|---|
| DRN BY: SMS | PROJECT: L&T-RUF | DRG. NO.: B016-RUF-LT-504-MP-DW-NTPL(1)-13005 | SH. 2 OF 2 |
| CHK BY: VJ | PWO NO.: | | REV. 00 |
| APP BY: AK | CAD #DWG THIS DRG. USING CAD SYSTEM ONLY | FILE: | |