



SECTION A-A'


GATE CLOSE INSIDE ELEVATION

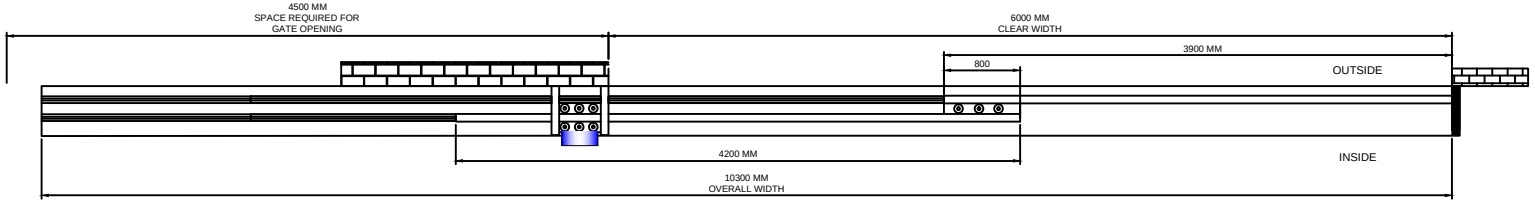


GATE CLOSE PLAN VIEW

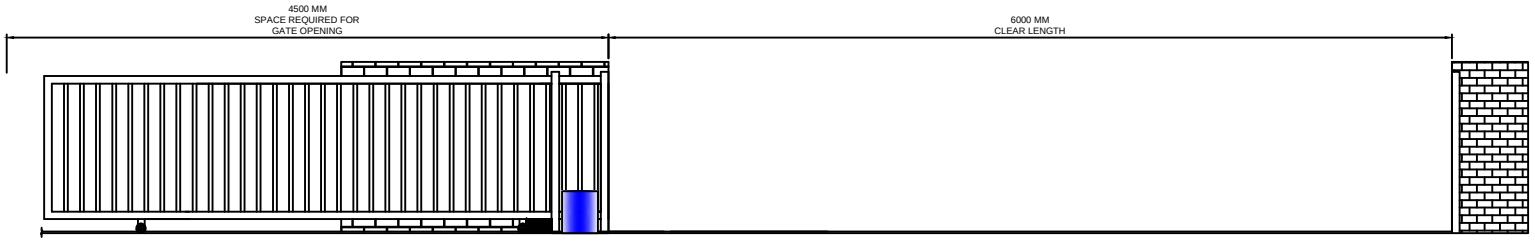


GATE OPEN INSIDE ELEVATION

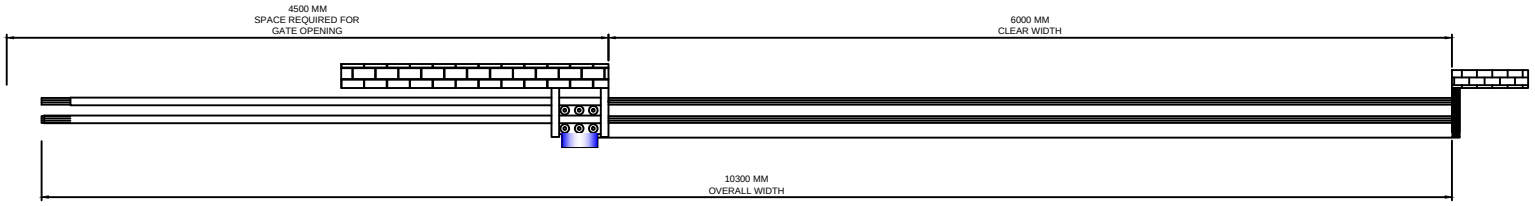

GATE OPEN PLAN VIEW

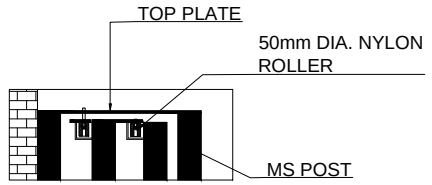

DETAIL VIEW OF B

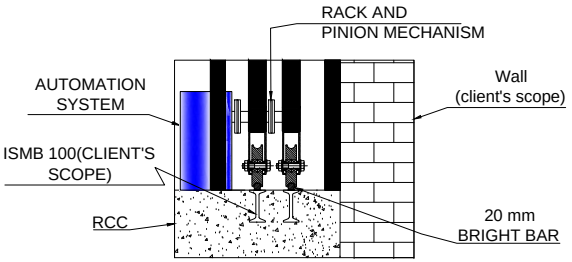

DETAIL VIEW OF A

CLEAR WIDTH	CLEAR HEIGHT	QUANTITY.
6000 MM	1800 MM	01 NO

NOTE:-
1.ALL REQUIRED CIVIL WORK BE IN CLIENTS SCOPE.
2.ONE COAT OF PRIMER & TWO COAT OF APPROVED RAL SHADE WILL BE GIVEN TO THE GATE.

This drawing & designing is the property of NIHVA TECHNOLOGIES. Not be sold or copy to any other concern.

TITLE: TWO LEAF TELESCOPIC SLIDING GATE

NIHVA TECHNOLOGY PVT. LTD. PUNE
Tel : 020 66304033
Email:- info@nihva.com
Website:- www.nihva.com

	NAME	SIGN	DATE
DRAWN	P.A		18.06.2020
CHECK	G.J		18.06.2020
REV.			
APPROVAL			

CLIENT - SHUBHSHREE ENGG. AND CONST. PVT. LTD.
PROJECT -
SITE -
DWG. NO. : NIHVA/20-21/0019
If any queries contact : projects@nihva.com
SCALE: 01 | WT: | SHEET: 01 OF 01
ALL DIMENSION ARE IN mm