

PARTS REQD. FOR TOWER BOLT ASM

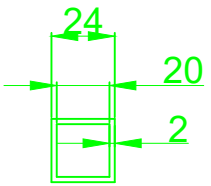

SQ, TUBE
24 X 2 MM THK X 50 L


SQ TUBE BUSH


QTY=05 NOS

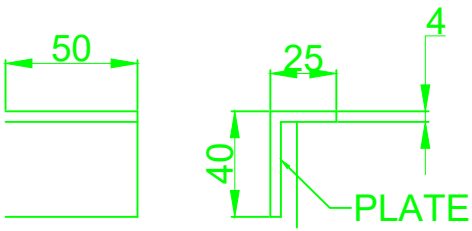


STOPPER L BRACKET

QTY=02 NOS

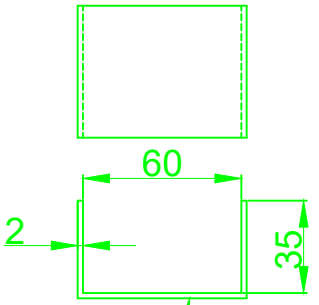


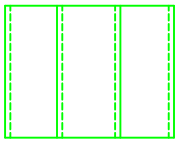

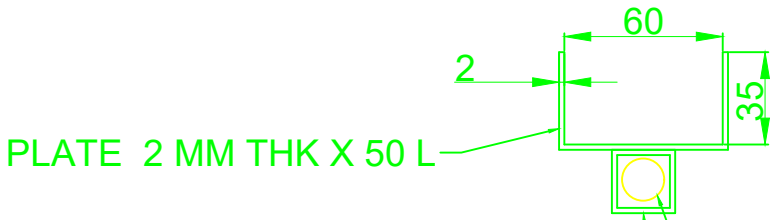

C BRACKET FOR MIDDLE DOOR

QTY=05 NOS

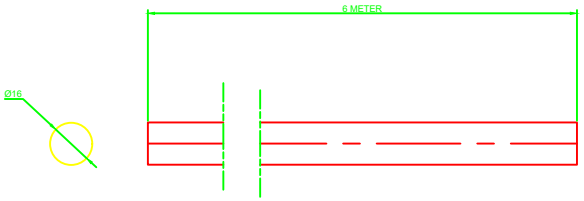

ROUND BAR DIA. 16 MM

QTY= 6 MTR

This drawing & design is the property of NIHVA TECHNOLOGIES. Not to be sold or copied to any other concern.

TITLE:- 4 LEAF CRM DOOR 01	NIHVA TECHNOLOGIES PVT. LTD.	NIHVA TECHNOLOGIES PVT. LTD. PUNE Tel : 020 66304033 Email:- info@nihva.com Website:- www.nihva.com	
	NAME	DATE	SIGN
DRAWN	M.SUTAR	12/05/2022	
CHECK	M.SUTAR	12/05/2022	
APPRD.			
CLIENT - LESTECH			
LOCATION - POSCO MANGAON			
PRODUCT - SLIDING DOOR			
If any queries contact : design@nihva.com	DWG NO:-NIHVA/22-23/MFG/0010		REV- 0
ALL DIMENSION ARE IN mm	SCALE: NTS	SCALE:-- 1:1	SHEET: 01 OF 01

	Date	Revised By

