



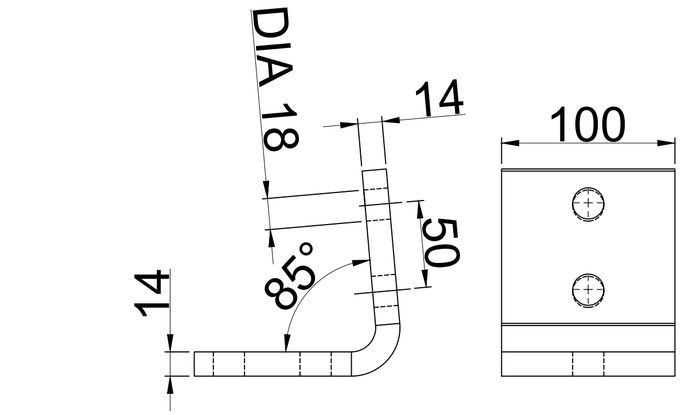


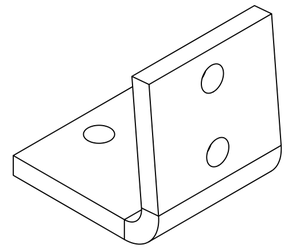

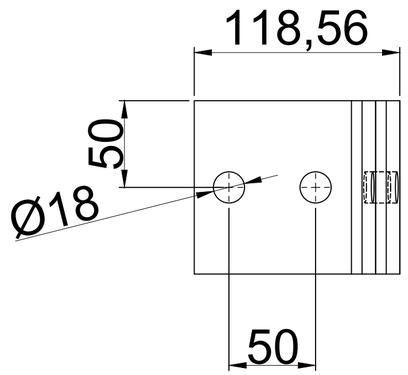


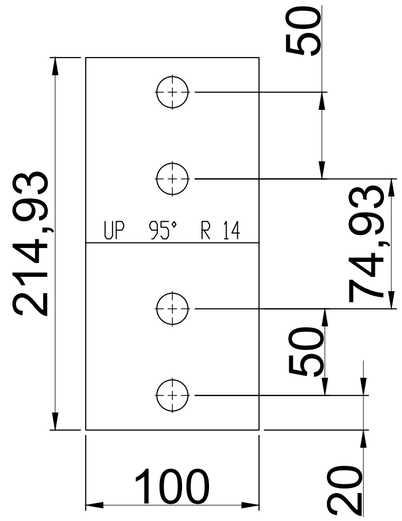

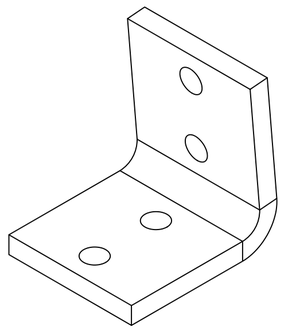

QTY. : 20 NOS.

REV NO.	DESCRIPTION	Date	Revised By

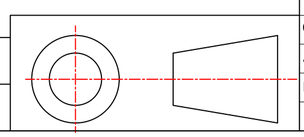

TITLE:- L - BRACKET 85				NIHVA TECHNOLOGIES PVT. LTD.
	NAME	DATE	SIGN	
DRAWN	MAHESH S.	21/10/22		CLIENT - NIHVA TECHNOLOGIES PVT.LTD
CHECK	MAHESH S.	21/10/22		LOCATION -
APPRD.	VIJAY T.	21/10/22		PRODUCT: RETRACTABLE ROOF
If any queries contact : design@nihva.com				DWG NO:-NIHVA/22-23/MFG/0048 / REV- 0
ALL DIMENSION ARE IN mm				SCALE: NTS / SCALE:-- 1:1 / SHEET: 01 OF 01

NIHVA TECHNOLOGIES PVT. LTD. PUNE
Tel : 020 66304033
Email:- info@nihva.com
Website:- www.nihva.com