

PART NO.	PART NAME	DESCRIPTION	QTY
1.	ISA	75 X 75 X 8 X 1950L	2 NOS
2.	ISA	75 X 75 X 8 X 2445L (NOTCH)	2 NOS
3.	R.TUBE	96 X 48 X 4.8 THK X 2445L	2 NOS
4.	R.TUBE	96 X 48 X 4.8 THK X 678L	2 NOS
5.	R.TUBE	96 X 48 X 4.8 THK X 580L	4 NOS
6.	PROFILE	175 X 16 X 200L	4 NOS
7.	FLAT	100 X 10 X 200L	4 NOS
8.	R.TUBE	80 X 40 X 4 THK X 675L (NOTCH)	4 NOS
9.	R.TUBE	80 X 40 X 4 THK X 455L	4 NOS
10.	SOLID	75 X 60 X 100L	4 NOS
11.	FLAT	75 X 16 X 2000L	1 NO
12.	R.TUBE	80 X 40 X 4 THK X 210L	2 NOS
13.	FLAT	40 X 5 X 80L	2 NOS
14.	FLAT	75 X 10 X 150L	2 NOS
15.	FLAT	75 X 10 X 200L	2 NOS

NOTE:~ MTL : MS

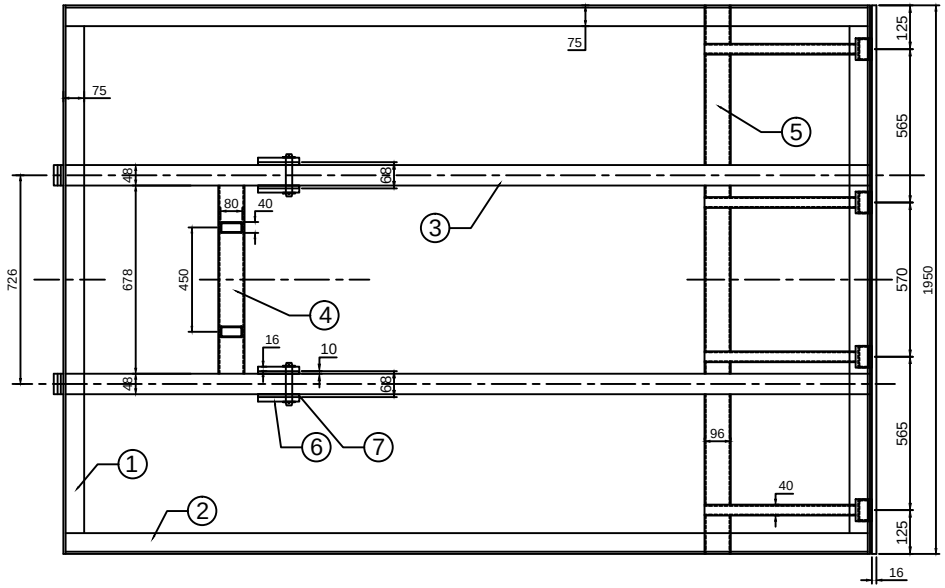

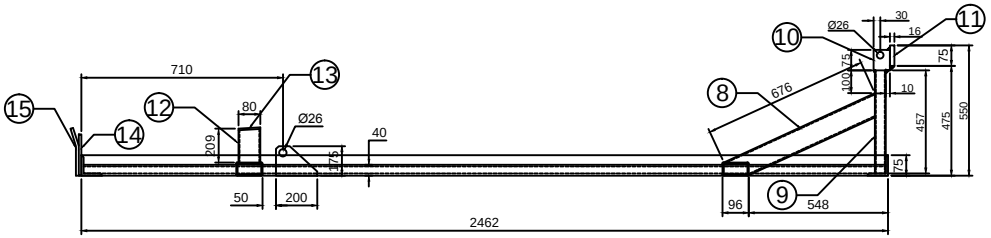

This drawing & design is the property of NIHVA TECHNOLOGIES. Not to be sold or copied to any other concern.

TITLE

BASE FRAME ASSLY

NIHVA TECHNOLOGIES PVT. LTD.
NIHVA TECHNOLOGIES PVT. LTD. PUNE
Tel : 020 66304033
Email:- info@nihva.com
Website:- www.nihva.com

	NAME	SIGN	DATE
DRAWN	PRADEEP		05.09.2018
CHECK	PRADEEP		05.09.2018
APPRD.	PRADEEP		05.09.2018

CLIENT -

PROJECT - NSDL2025

SITE LOCATION -

If any queries contact : design@nihva.com

DWG. NO. : NIHVA/18-19/MFG/NSDL2025/004

ALL DIMENSION ARE IN mm

SCALE: NTS | WT: | REV- 00