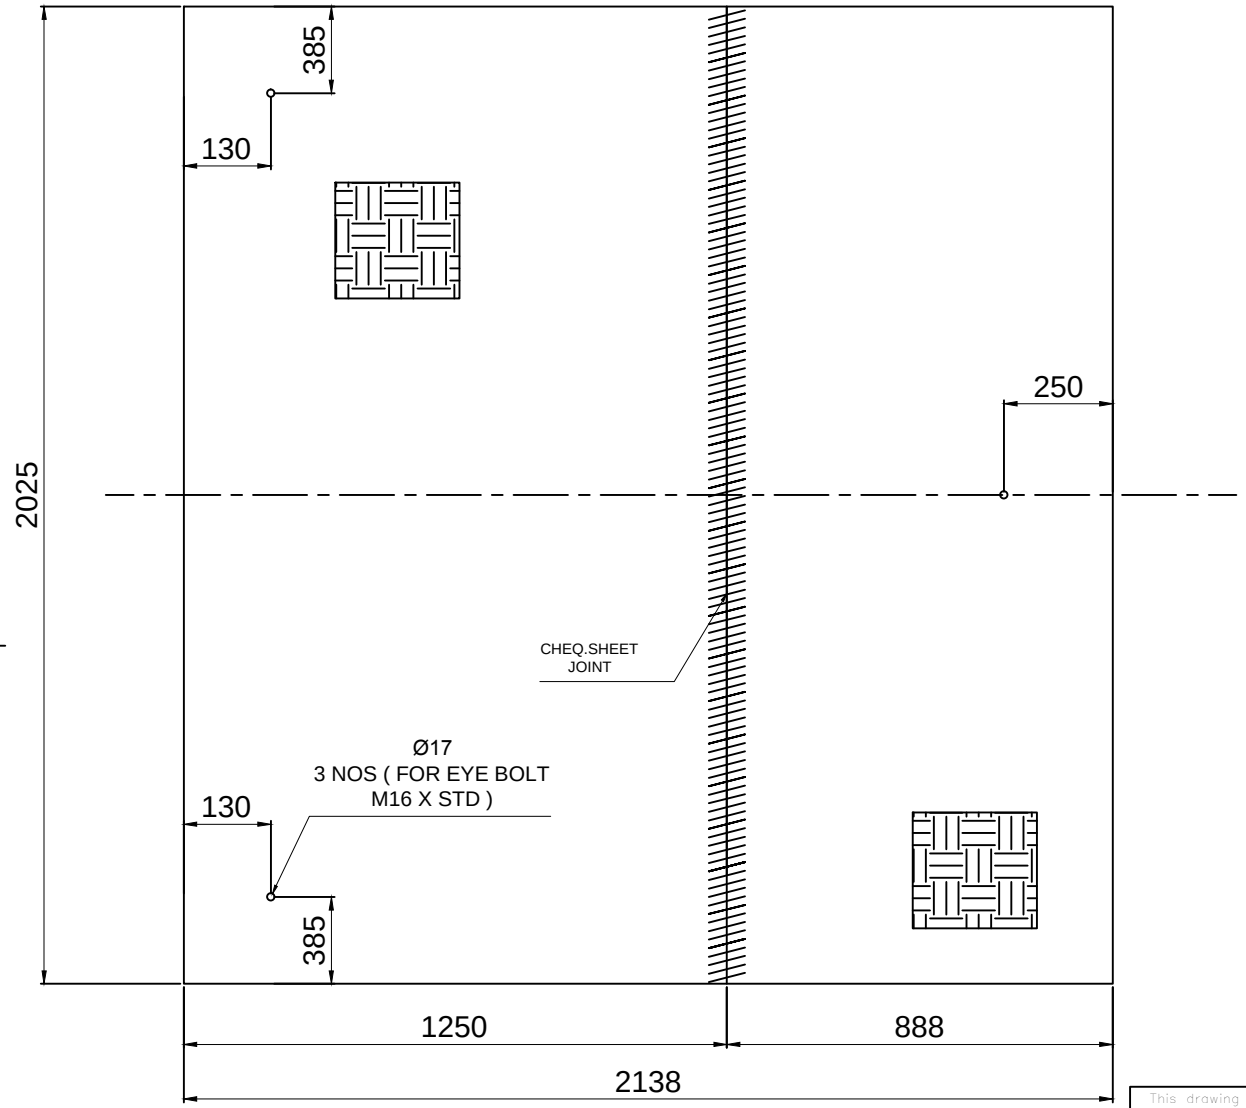


1. CHEQ.SHEET 1250 X 8 THK X 2025L = 1 NO
2. CHEQ.SHEET 888 X 8 THK X 2025L = 1 NO

This drawing & design is the property of NIHVA TECHNOLOGIES. Not to be sold or copied to any other concern.

TITLE				
DECK CHEQ.SHEET				NIHVA TECHNOLOGIES PVT. LTD. PUNE Tel : 020 66304033 Email:- info@nihva.com Website:- www.nihva.com
	NAME	SIGN	DATE	
DRAWN	PRADEEP		05.09.2018	CLIENT -
CHECK	PRADEEP		05.09.2018	PROJECT - DLSD1010
APPRD.	PRADEEP		05.09.2018	SITE LOCATION -
If any queries contact : design@nihva.com				DWG. NO. : NIHVA/18-19/MFG/DLSD1010/003
ALL DIMENSION ARE IN mm				SCALE: NTS / WT: / REV- 00