




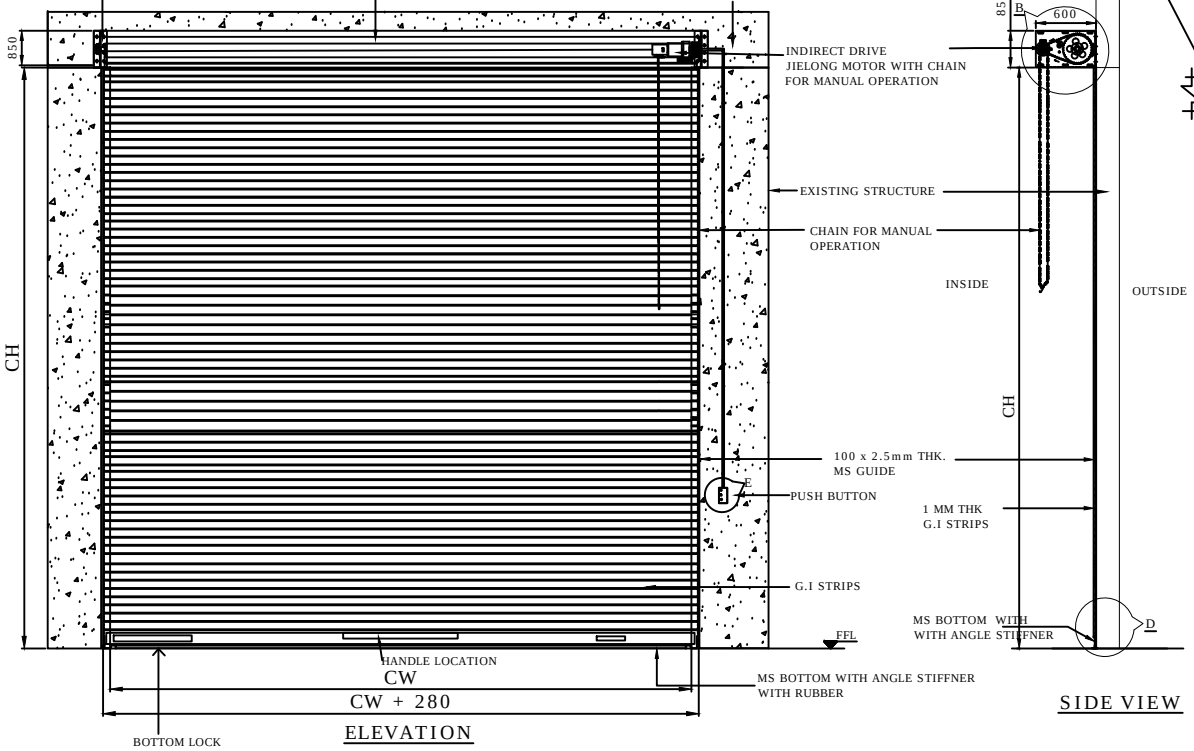


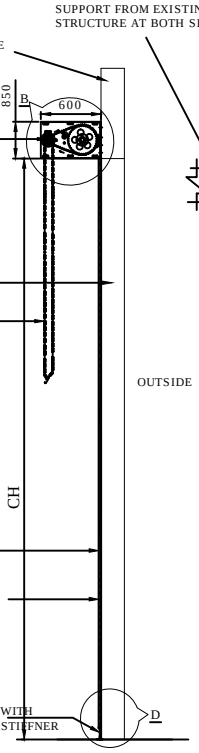


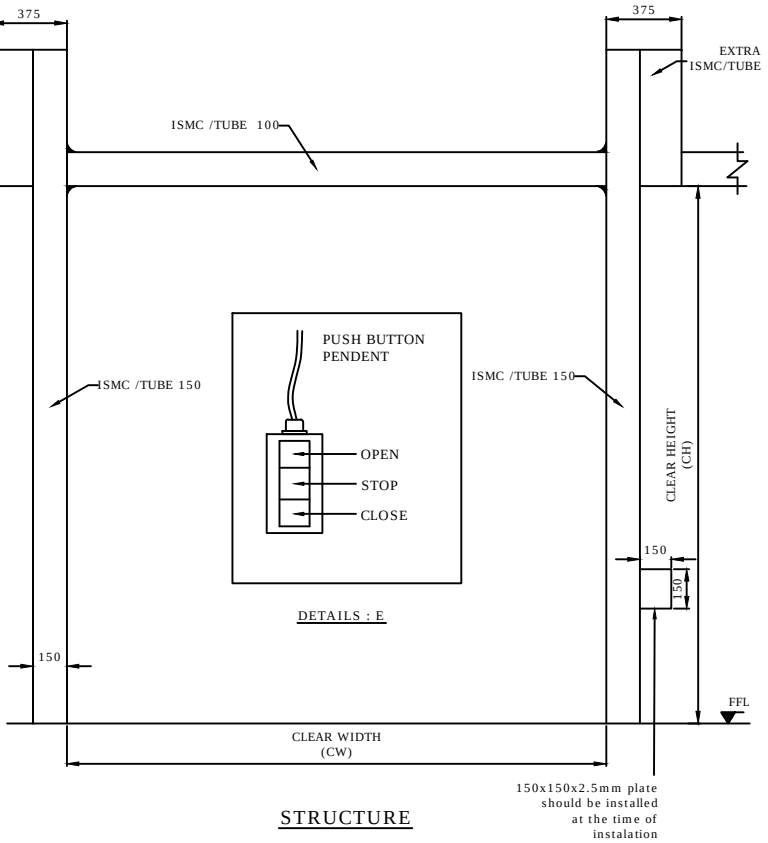


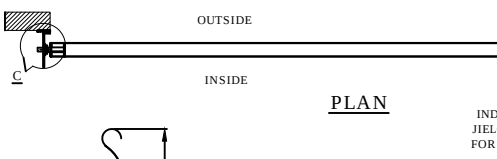

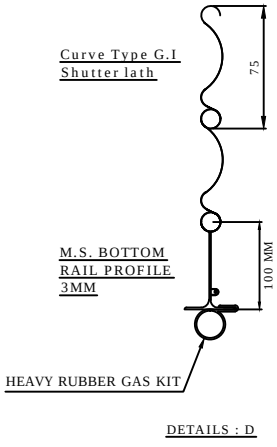

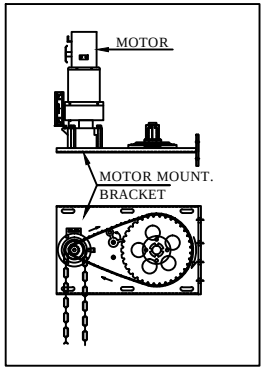

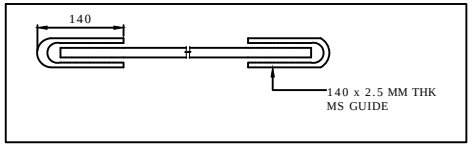

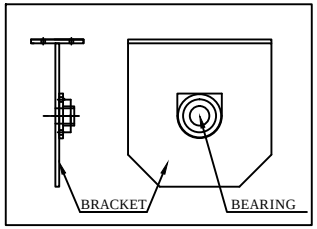

(NOTE: REQUIRED TECHNICAL STRUCTURE & CIVIL WORK FOR SHUTTER IN CLIENT SCOPE)

R01	7.11.2020	GUIDE 140 MM & STRUCTURE CHANGED	S.M.S.	
REV NO	DATE	DESCRIPTION	DRAWN	REMARK

4500	5000	1	RAL 9002 POWDER COATING
CLEAR WIDTH (CW)	CLEAR HEIGHT (CH)	QUANTITY	RAL COLOR

This drawing & design is the property of NIHVA TECHNOLOGIES. Not to be sold or copied to any other concern.

TITLE G.I. SLAT MOTORIZED ROLLING SHUTTER

	NAME	SIGN	DATE
DRAWN	S.M.S.		7.11.2020
CHECK			
APPRD.			

NIHVA TECHNOLOGIES PVT. LTD.
NIHVA TECHNOLOGIES PVT. LTD. PUNE
Tel : 020 66304033
Email:- info@nihva.com
Website:- www.nihva.com

CLIENT - SPACONS EPC PVT LTD
PROJECT - FAURECIA INDIA PVT LTD
SITE LOCATION - PUNE

If any queries contact : projectsupport@nihva.com
DWG. NO. : NIHVA/20-21/0067/R01 REV- R01
ALL DIMENSION ARE IN mm
SCALE: NTS WT: SHEET: